

Bu set, Maltepe / İdealtepe'deki mobilya mağazasının fonksiyonel antrenman stüdyosuna dönüşümü için MİMARİ UYGULAMA PROJESİDİR. Net iç kullanım alanı 103,78 m², 10 mahal. Set; yıkım, uygulama planı, zemin kaplama, tavan planı, iki kesit, dört iç görünüş, mahal listesi, kapı-pencere listesi, duvar tipleri, sekiz imalat detayı ve yangın-tahliye planından oluşur. Mekanik (M-01...M-06) ve elektrik (E-01...E-06) paftaları ayrı dosyalardadır ve bu setle aynı geometrik altlığı kullanır. Bu set müteahhidin imalat yapabilmesi için gereken malzeme, katman ve kot bilgisini taşır; ruhsat başvurusu için proje müellifi mimar tarafından imzalanmış 1/50 takım ayrıca düzenlenecektir.

NET İÇ ALAN

103,78 m²

10 mahal · duvar payı 0,47 m²

ZEMİN KAPLAMA TİPİ

6 tip

Z1–Z6 · bitmiş kot ±0,00 (ıslak –0,02)

DUVAR / TAVAN TİPİ

6 + 4

D1–D6 · T1–T4

KAPI · PENCERE

9 + 2

K01–K09 · P01–P02

GENEL NOTLAR — UYGULAMADA BAĞLAYICIDIR


- 01** Tüm ölçüler metre (m), kaplama katman kalınlıkları milimetre (mm) cinsindendir. Ölçü okunur, çizimden ölçü alınmaz.
- 02** ±0,00 kotu bitmiş zemin kotudur. Mevcut şap üst kotu –0,053 VARSAYILMIŞTIR; söküm sonrası yerinde ölçülüp tüm tesviye şapı kalınlıkları revize edilecektir.
- 03** Taşıyıcı sistemde (kolon, perde, kiriş, döşeme) hiçbir kesme, delme veya yük artışı yapılmayacaktır. Gerekli hâllerde statik proje müellifinden yazılı görüş alınacaktır.
- 04** Mevcut duvar kalınlıkları ve tavan yüksekliği VARSAYIMDIR; rölöve sonrası mahal listesi ve tavan kotları güncellenecektir.
- 05** Alçıpan imalatlarda profil aralığı 400 mm'yi geçmeyecek; 3,0 m üzeri duvarlarda ve kapı kenarlarında kutu profil takviyesi yapılacaktır.
- 06** Islak hacimlerde su yalıtımı EN 14891'e uygun, çimento esaslı 2 bileşenli, 2 kat; tüm köşe ve boru geçişlerinde bant ve manşet kullanılacaktır.
- 07** Islak hacim imalatı bitiminde, seramik öncesi 24 saatlik su tutma (taşkın) testi yapılacak ve tutanağa bağlanacaktır.
- 08** Kauçuk zemin, üst kat konut VARSAYIMI nedeniyle titreşim matı ile yüzer döşeme olarak teşkil edilecektir; mat duvara 50 mm yukarı dönecektir.
- 09** Tüm cam yüzeylerde (kapı, ayna, vitrin) temperli veya lamine güvenlik camı kullanılacaktır (EN 12600).
- 10** Kaçış kapıları kaçış yönünde açılacak, üzerinde kilit veya sürgü bulunmayacak, panik donanımlı olacaktır (EN 1125).
- 11** Asma tavan üstündeki mekanik ve elektrik tesisatı bağımsız askılanacak; ağırlık alçıpan karkasına aktarılmayacaktır.
- 12** Boya, seramik ve kauçuk renk/desen seçimleri numune onayına tabidir; onaysız imalat bedeli yükleniciye aittir.
- 13** Bu set mimari uygulama setidir; ruhsat için proje müellifi mimar tarafından imzalanmış 1/50 onaylı takım ayrıca düzenlenecektir.

PAFTA İNDEKSİ

PAFTA	İÇERİK	ÖLÇEK
A-01	Kapak · genel notlar · pafta indeksi	—
A-02	Mevcut durum ve yıkım / söküm planı	1/75
A-03	Uygulama planı — bölme, kapı, mahal	1/75
A-04	Zemin kaplama planı	1/75
A-05	Tavan planı (RCP) ve tesisat koordinasyonu	1/75
A-06	Kesit A-A	1/50
A-07	Kesit B-B	1/50
A-08	İç görünüşler G-01 ... G-04	1/50
A-09	Mahal listesi — kaplama ve bitiş	—
A-10	Kapı ve pencere listesi · duvar tipleri	—
A-11	İmalat detayları I — zemin ve kot geçişi	1/10
A-12	İmalat detayları II — ıslak hacim, tavan, ayna	1/10
A-13	Yangın ve tahliye planı	1/75
A-14	Duvar tipleri — yatay kesit 1/10	—

MAHAL ÖZETİ

NO	MAHAL	M²	ZEMİN	TAVAN	KOT
101	GİRİŞ · BANKO · SİRKÜLASYON	15,65	Z3	T2	2,75
102	ARENA · SERBEST AĞIRLIK	31,76	Z1	T1	3,20
103	FONKSİYONEL · KARDİYO	22,31	Z2	T1	3,20
104	DİNLENME SALONU	17,33	Z3	T2	2,75
105	ERKEK SOYUNMA	4,48	Z5	T4	2,60
106	ERKEK DUŞ	1,76	Z4	T3	2,40
107	ERKEK WC	1,75	Z4	T3	2,40
108	KADIN SOYUNMA	5,59	Z5	T4	2,60
109	KADIN DUŞ	1,39	Z4	T3	2,40
110	KADIN WC	1,29	Z4	T3	2,40
TOPLAM (NET)		103,31			

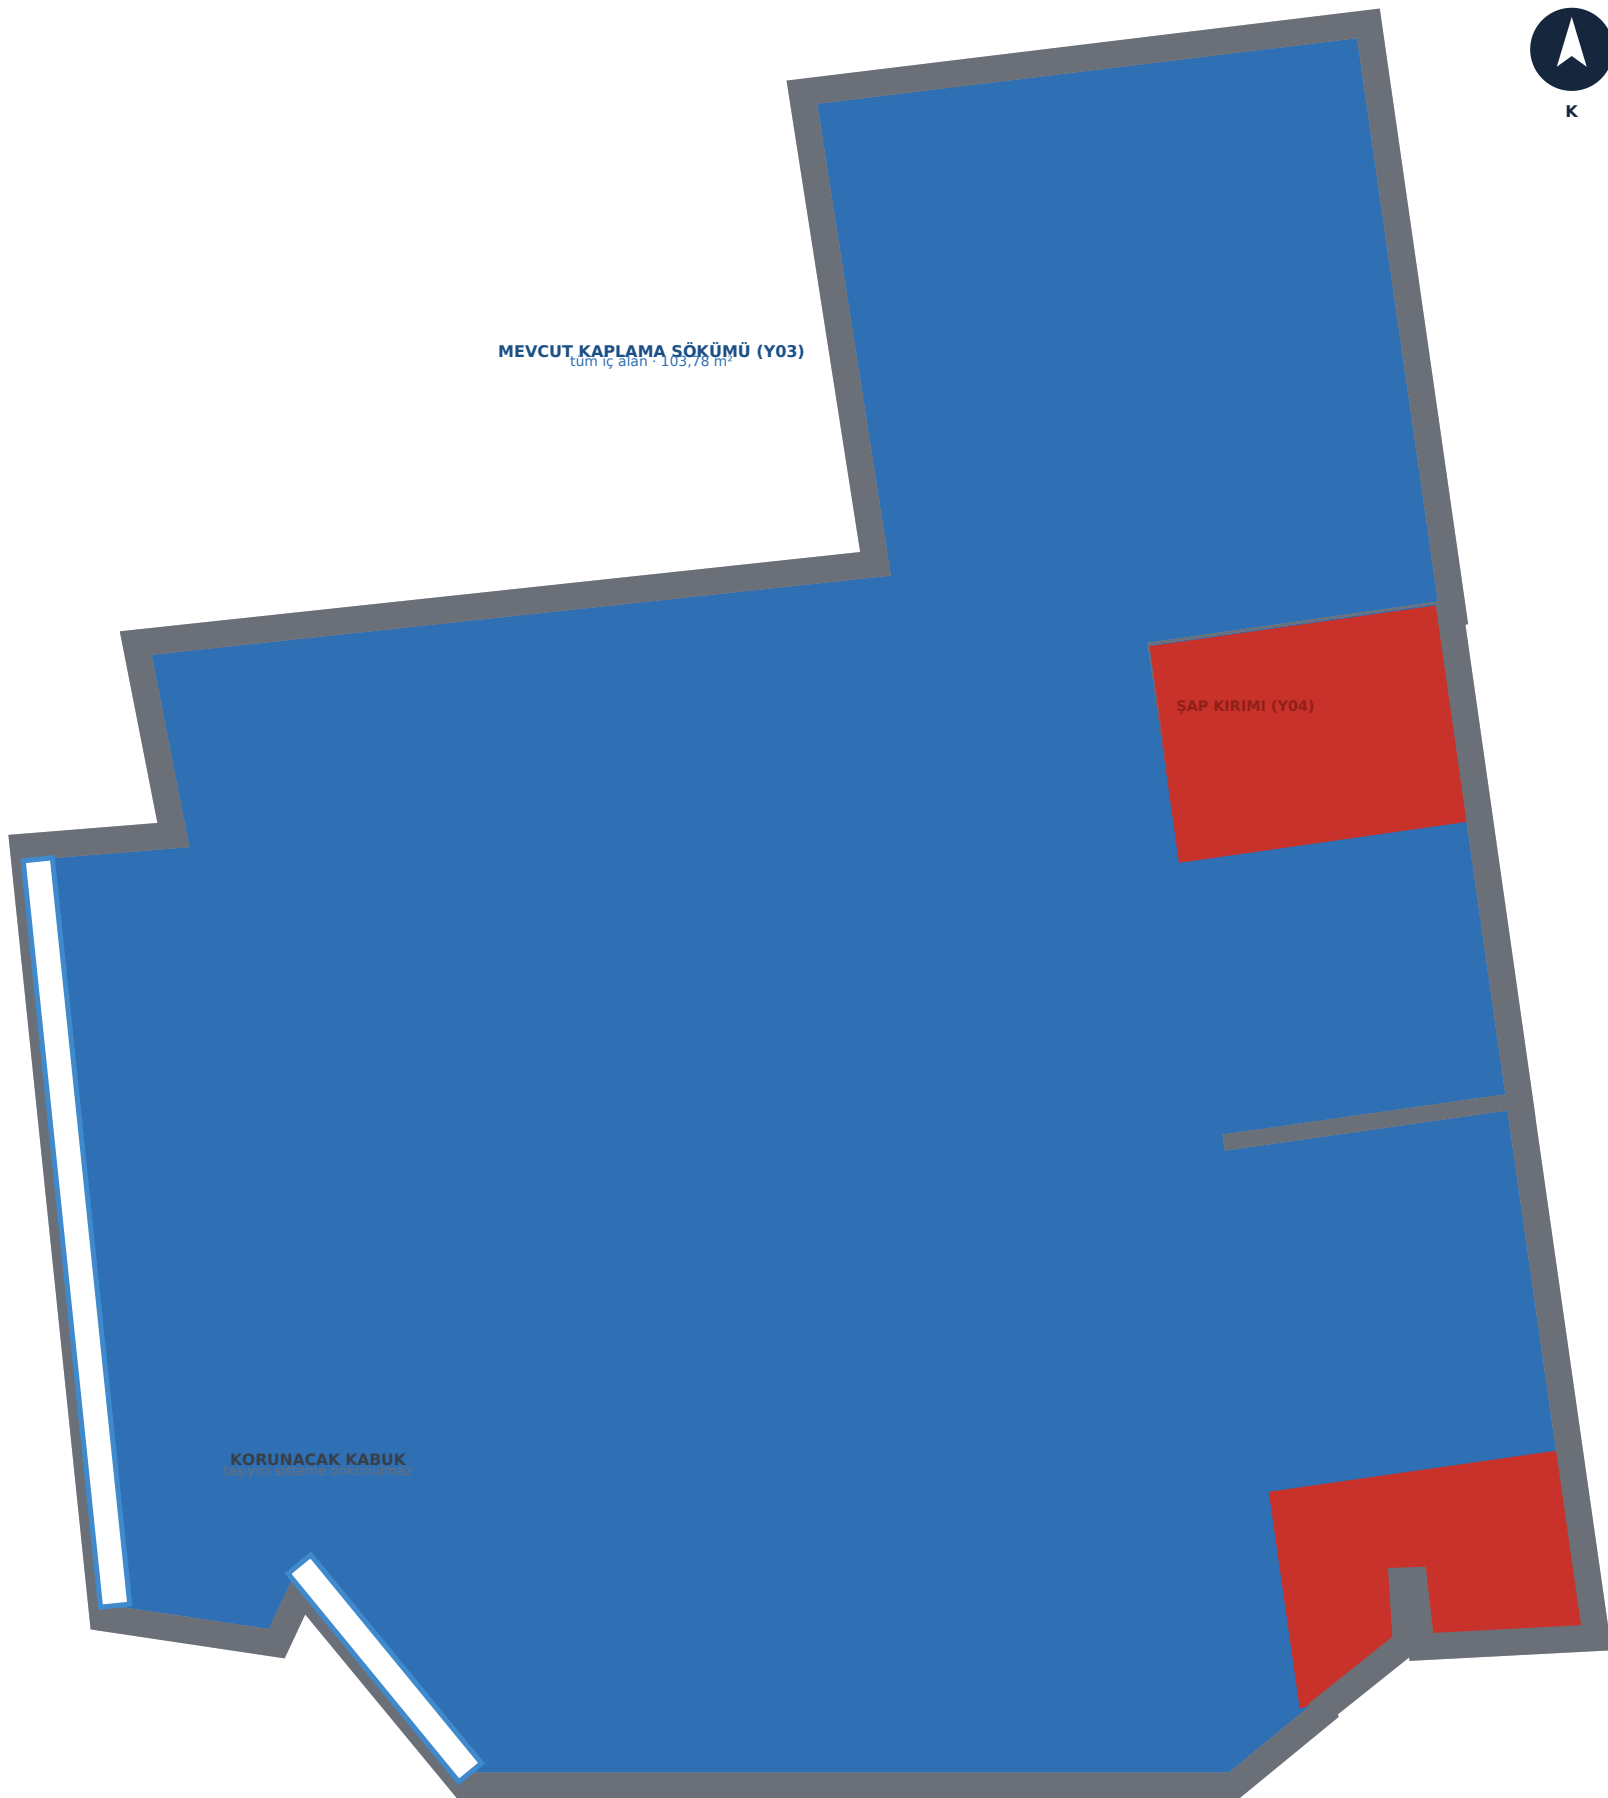

K

Pafta	A-02
Ölçek	1/75 (A3)
Tarih	17 Eylül 2026
Durum	Uygulama — yerinde doğrulanacak

MİMARİ UYGULAMA PROJESİ

Rev F

YIKIM VE SÖKÜM İŞ KALEMLERİ


KOD	TANIM	METRAJ
Y01	Mevcut mağaza rafı, teşhir ünitesi ve mobilyanın sökülüp taşınması	1 komple
Y02	Mevcut asma tavan ve aydınlatma armatürlerinin sökümü	103,78 m²
Y03	Mevcut zemin kaplamasının (laminat / seramik) sökümü, altlık temizliği	103,78 m²
Y04	Islak hacim alanında mevcut şap kırımı (tesisat boşluğu için, ort. 70 mm)	16,73 m²
Y05	Mevcut sıva üstü elektrik tesisatı ve tablosunun sökümü	1 komple
Y06	Mevcut ıslak hacim (varsa) armatür ve duvar seramiği sökümü	16,73 m²
Y07	Yeni kapı boşluklarının açılması, lento teşkili	2 adet
Y08	Moloz çuvallama, yatay-düşey taşıma ve belediye döküm sahasına nakli	14 m³

SÖKÜM ÖNCESİ ZORUNLU ADIMLAR

Mevcutta iç bölme duvarı bulunmadığı, mekânın tek hacim mağaza olduğu VARSAYILMIŞTIR. Söküm öncesi mevcut durum rölövesi alınacak; taşıyıcı sistemde hiçbir elemana dokunulmayacaktır. Kolon, perde ve döşeme kirişlerinde kesme/delme yasaktır.

SIRALAMA

1) Enerji ve su kesilir, mevcut sayaç okuması tutanaklanır. 2) Mevcut durum rölövesi ve fotoğraf kaydı alınır. 3) Devralınacak mobilya ayrılır. 4) Asma tavan ve aydınlatma sökülür. 5) Zemin kaplaması sökülür, şap kotu ölçülür — bu ölçüm tüm tesviye şapı kalınlıklarının girdisidir. 6) Islak hacim şap kırımı ve pis su kotu tespiti yapılır; Seçenek A/B kararı burada verilir. 7) Moloz aynı gün tahliye edilir; kat sahanlığı ve asansör korunur.

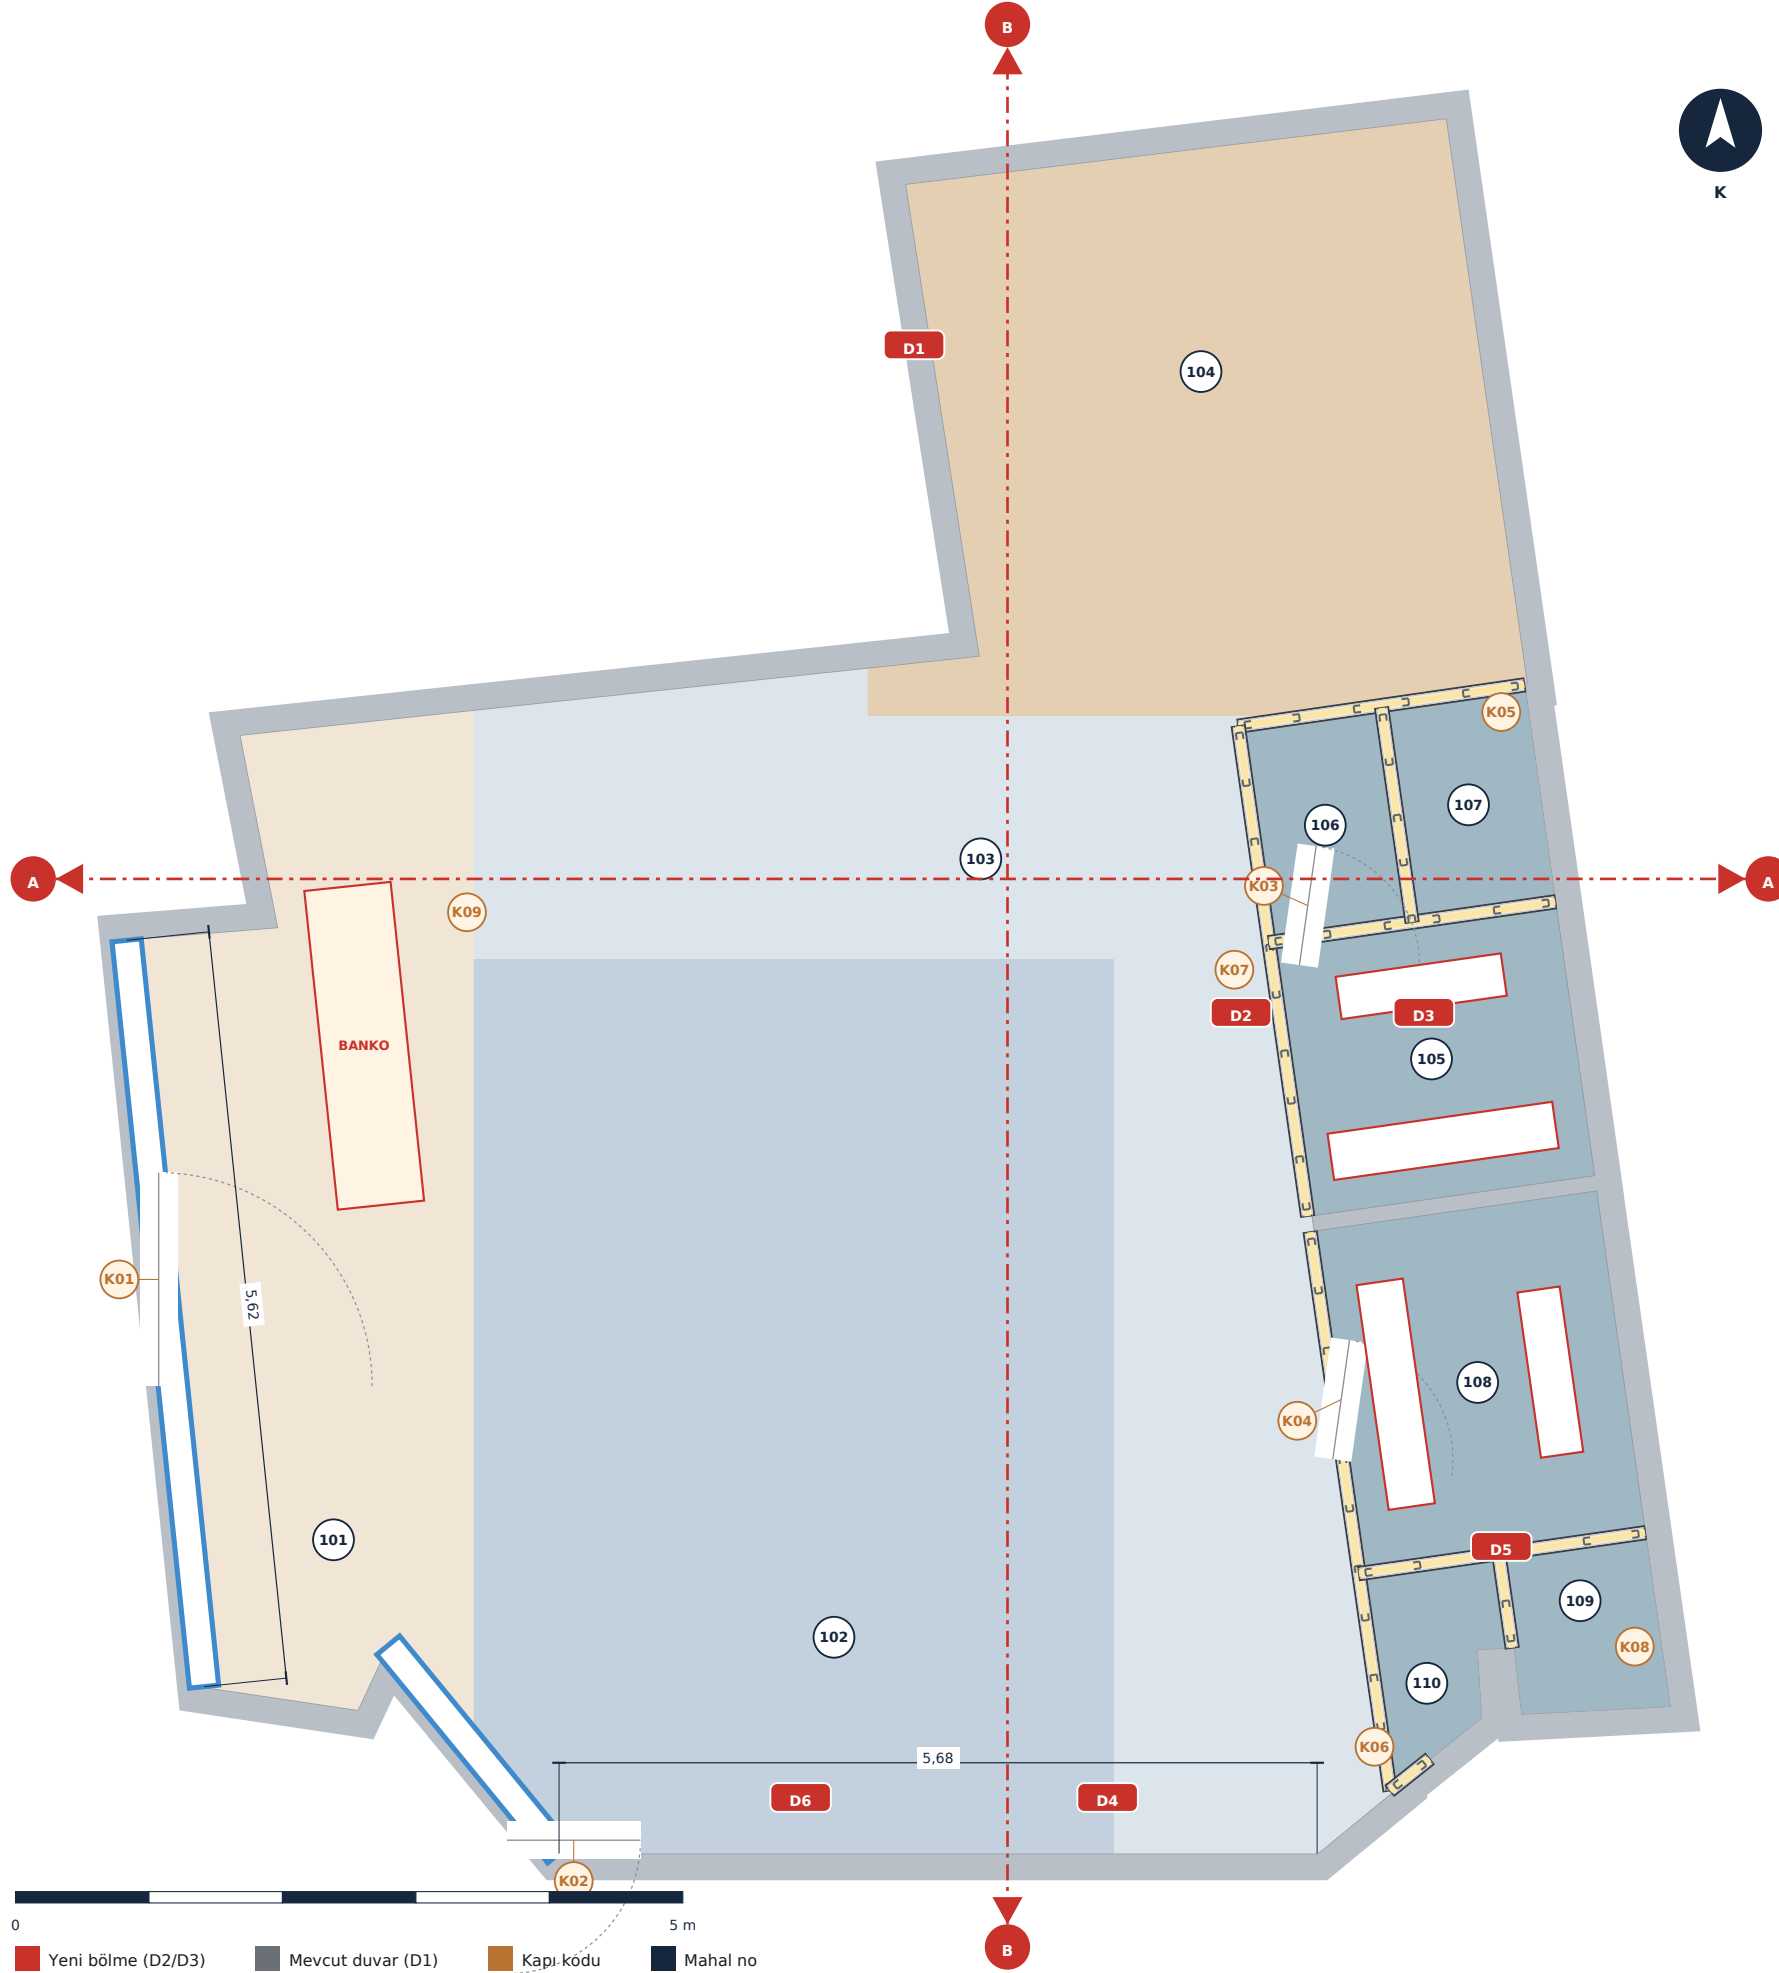

Pafta	A-03
Ölçek	1/75 (A3)
Tarih	17 Eylül 2026
Durum	Uygulama — yerinde doğrulanacak

MİMARİ UYGULAMA PROJESİ

Rev F

KOT ŞEMASI


KOT	TANIM	NOT
±0,00	Bitmiş zemin kotu — tüm kuru hacimler	Referans
-0,02	Duş ve WC bitmiş zemin kotu	Su taşkını kontrolü · eşik profili
-0,053	Mevcut şap üst kotu (VARSAYIM)	Tesviye şapı bu farkı kapatır
+2,40	T3 Alçıpan asma tavan — mahal 106 · 107 · 109 · 110	800 mm tesisat boşluğu · serbestlik 30 mm
+2,60	T4 Alçıpan asma tavan — mahal 105 · 108	600 mm tesisat boşluğu · serbestlik 50 mm
+2,75	T2 Alçıpan asma tavan — mahal 101 · 104	450 mm tesisat boşluğu · serbestlik 30 mm
+3,20	T1 Açık (endüstriyel) tavan — mahal 102 · 103	Yapısal döşeme altı (VARSAYIM)

BÖLME DUVAR METRAJİ

TİP	TANIM	KALINLIK	METRAJ
D2	Alçıpan bölme — kuru hacim	100 mm	≈ 14,6 m ² (VARSAYIM)
D3	Alçıpan bölme — ıslak yüz	100 mm	≈ 21,4 m ² (VARSAYIM)
D4	Akustik giydirme — arena güney çeperi	95 mm	≈ 18,2 m ²
D5	Seramik kaplı duvar — ıslak	216 mm	≈ 46,2 m ²
D6	Ayna duvarı — arena güney çeperi	212 mm	≈ 9,6 m ² (4,80 m × 2,00 m)

BÖLME YÜKSEKLİĞİ

Tüm alçıpan bölmeler asma tavan üstünden geçerek yapısal döşemeye kadar (+3,20) yükseltilecektir. Asma tavan hizasında kesilen bölme, ıslak hacim kokusunu ve soyunma mahremiyetini koruyamaz; akustik performans ($R_w \approx 51$ dB) da yalnızca tam yükseklikte geçerlidir.

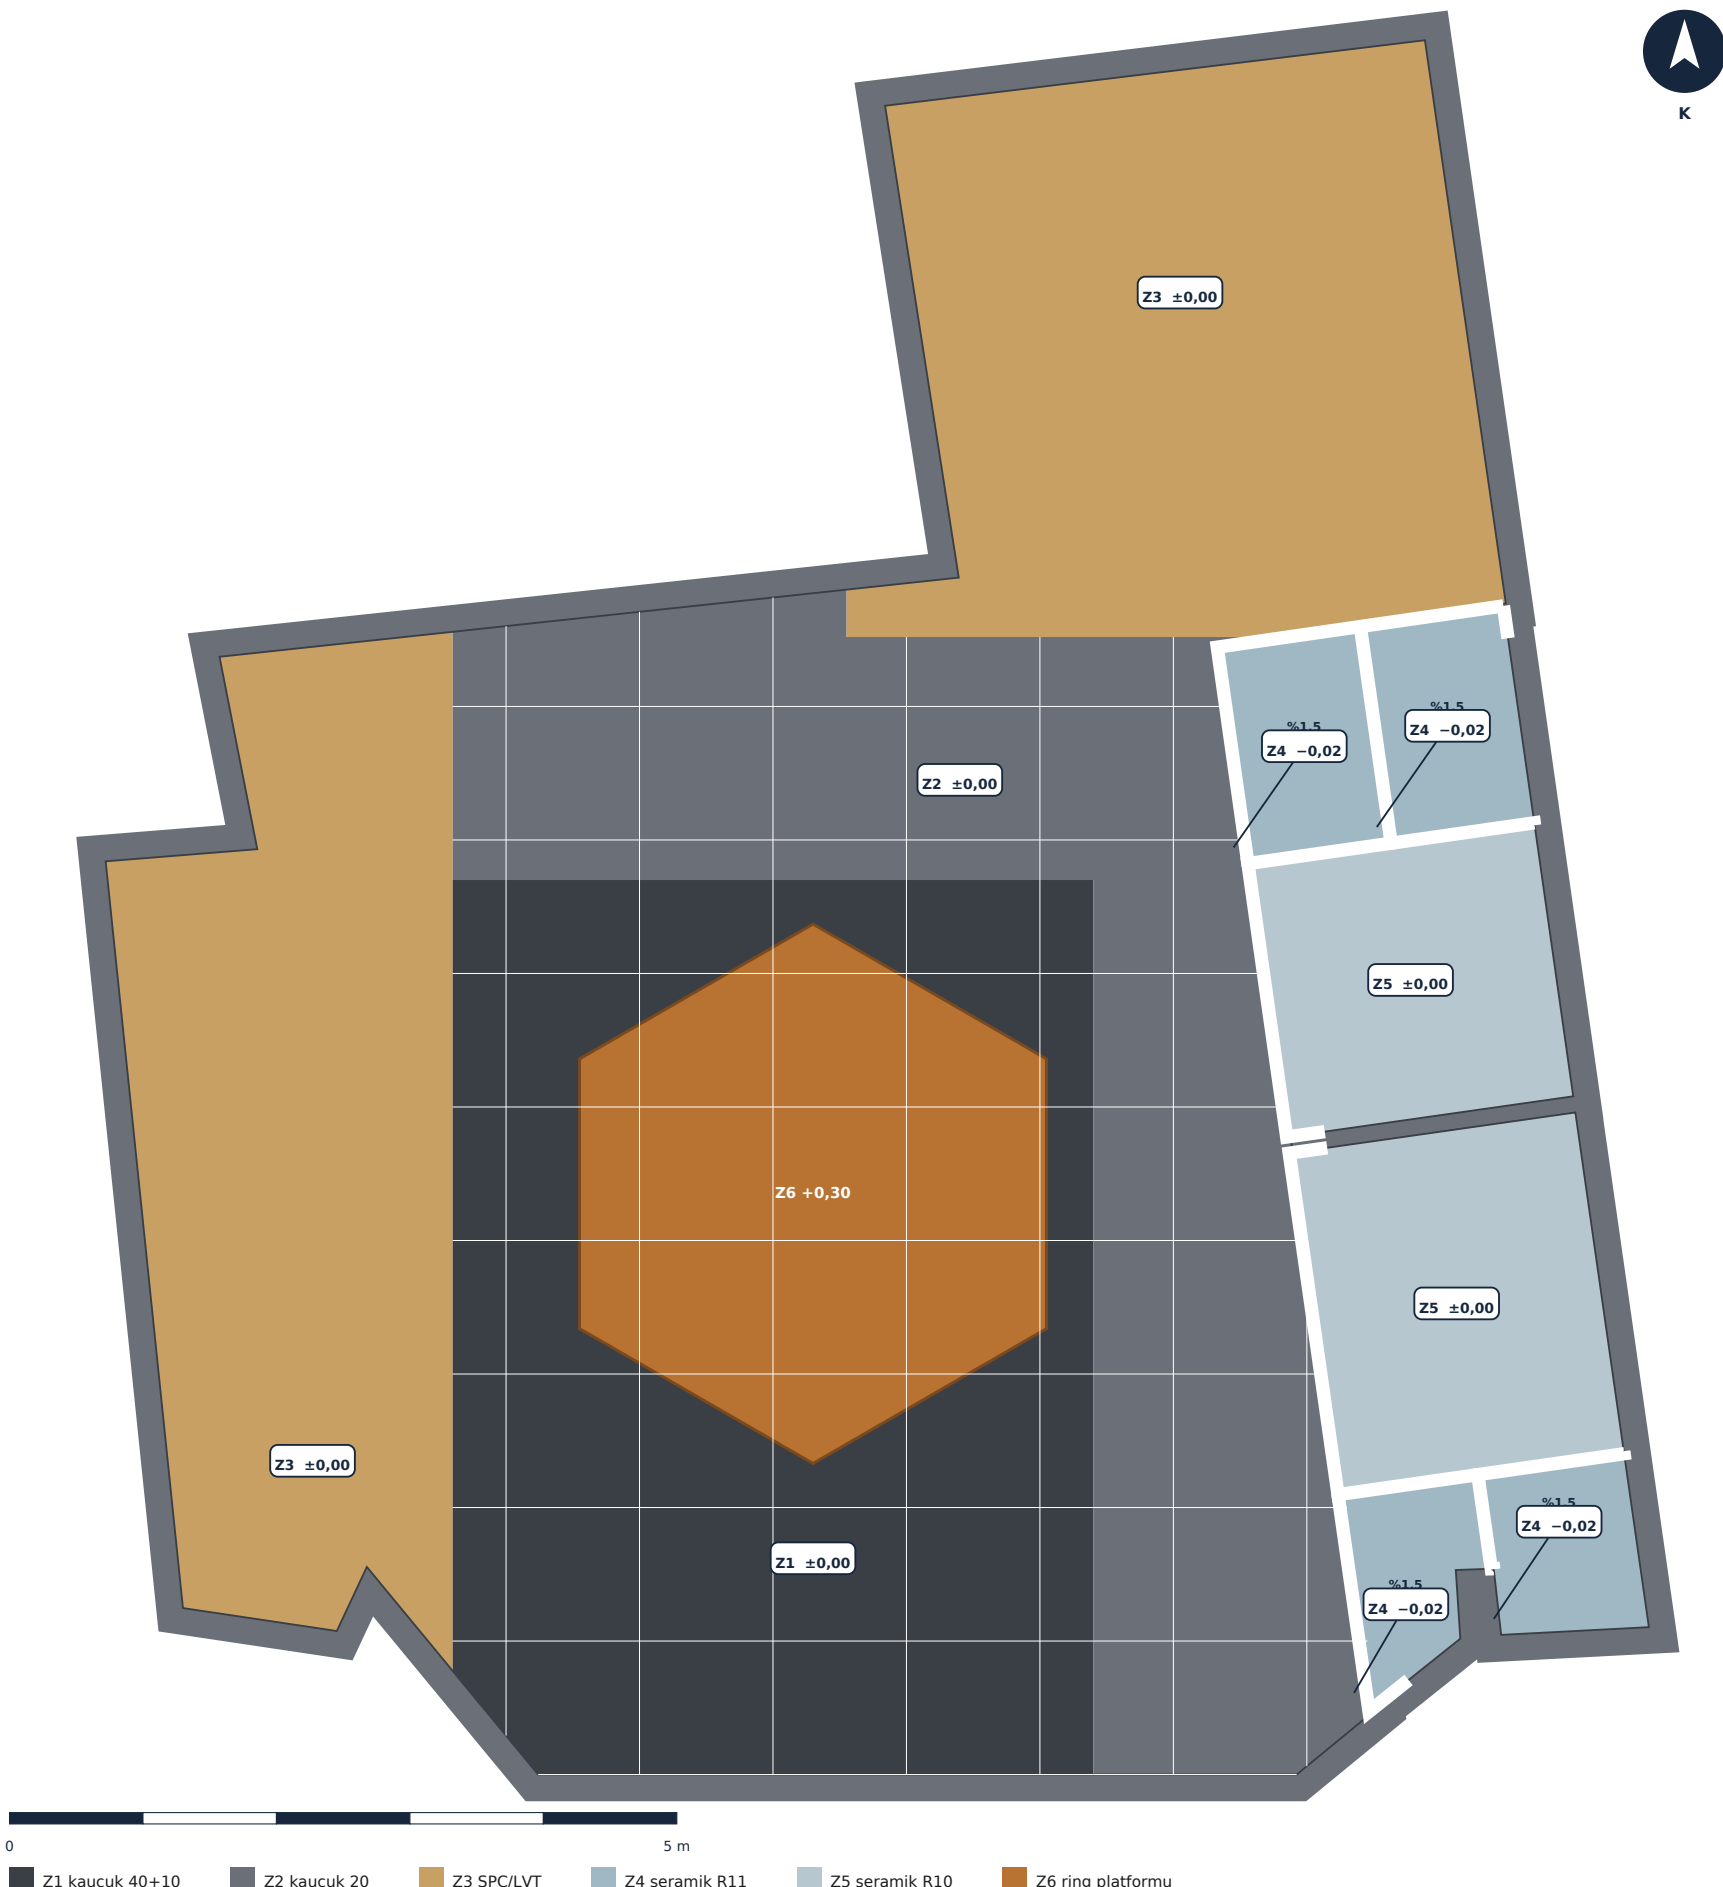

Pafta	A-04
Ölçek	1/75 (A3)
Tarih	17 Eylül 2026
Durum	Uygulama — yerinde doğrulanacak
MİMARİ UYGULAMA PROJESİ	
Rev F	

ZEMİN KAPLAMA TİPLERİ

TİP	MAHAL / KAPLAMA	TOPLAM	BİTMİŞ KOT
Z1	Arena · serbest ağırlık	53 mm	±0,00
Z2	Fonksiyonel · kardiyo	53 mm	±0,00
Z3	Giriş · banko · dinlenme	53 mm	±0,00
Z4	Duş · WC	55 mm	−0,02
Z5	Soyunma	53 mm	±0,00
Z6	Ring platformu (ekipmana bağlı)	300 mm	+0,30

PERFORMANS ŞARTI

- Z1** EN 14041 · yangın Bfl-s1 · EN ISO 10140 $\Delta Lw \geq 18$ dB · serbest ağırlık düşürmeye uygun
- Z2** EN 14041 · Bfl-s1 · kardiyo cihazı nokta yükü ≥ 4 kN/m²
- Z3** EN ISO 10874 aşınma sınıfı 33 / AC5 · EN 14041 Bfl-s1 · kaymazlık DS
- Z4** EN 14891 su yalıtımı · EN 16165 Ek B (R11) · Ek A (B sınıfı ıslak ayak)
- Z5** EN 16165 Ek B (R10) · EN 14411 Bla · rektifiye, 2 mm derz

SÜPÜRGELİK

KOD	TANIM	MAHAL
S1	Kauçuk süpürgelik 100×8 mm — zemin kaplamasıyla aynı malzeme, üst kenarı 45° pahlı	102 · 103
S2	MDF lake süpürgelik 80×16 mm — RAL 9003, akrilik mastik ile duvara yalanır	101 · 104
S3	Süpürgelik yok — duvar seramiği zemine iner; birleşimde içbükey (kaveto) profil	106 · 107 · 109 · 110
S4	Porselen süpürgelik 80 mm — zemin karosundan kesme, rektifiye kenar	105 · 108

KOT SÜREKLİLİĞİ — KONTROL EDİLDİ

Tüm kuru hacimlerde bitmiş zemin kotu ±0,00'dır; tesviye şapı kalınlıkları (Z1: 3 · Z2: 30 · Z3: 42 · Z5: 38 mm) farklı kaplama kalınlıklarını eşitler. Mahaller arasında eşik veya kot farkı oluşmaz. Yalnızca duş ve WC bitmiş kotu −0,02'dir; bu fark kapı altında 20 mm'lik eğimli alüminyum eşik profili ile karşılanır ve su taşkınına mahal içinde tutar.



T1 açık tavan +3,20 T2 alçıpan +2,80 T4 alçıpan +2,60 T3 ıslak alçıpan +2,40 Revizyon kapağı 30×30

Pafta	A-05
Ölçek	1/75 (A3)
Tarih	17 Eylül 2026
Durum	Uygulama — yerinde doğrulanacak
MİMARİ UYGULAMA PROJESİ	
Rev F	

TAVAN TİPLERİ

T1 · Açık (endüstriyel) tavan +3,20

- Mevcut döşeme altı raspa + temizlik
- Tüm MEP tesisatı görünür — düzenli askı ve hizalı güzergâh zorunlu
- 2 kat siyah su bazlı akrilik boya (döşeme altı, kanal ve askılar dâhil)
- Arena üzerinde 12 adet 1200×600×50 mm asma akustik taşıyıcı baffle ($\alpha_w \approx 0,90$)
- Arena · fonksiyonel — serbest yükseklik korunur, ekipman kotu 2,15 m'ye kadar

T2 · Alçıpan asma tavan — kuru hacim +2,75

- Ayarlı askı çubuğu @900 mm, TC47 ana profil @900 / TU27 taşıyıcı @400 mm
- 12,5 mm A tipi alçıpan tek kat
- Derz bandı + 2 kat saten alçı + astar + 2 kat mat boya
- Kenar gölge derzi 10 mm (duvar birleşiminde ayrılma çatlağı önlemi)
- Giriş · banko · dinlenme — üstünde 450 mm tesisat boşluğu (kanal + tava + bakır hat sığsın diye kot 2,80'den 2,75'e indirilmiştir)

T3 · Alçıpan asma tavan — ıslak hacim +2,40

- Galvaniz ayarlı askı @900 mm, TC47 / TU27 karkas
- 12,5 mm H2 (su itici) alçıpan tek kat
- Su bazlı, küf önleyici yarı mat banyo boyası, 2 kat
- 300×300 mm menteşeli revizyon kapağı (her ıslak hacimde 1 adet)
- Duş · WC — üstünde 800 mm tesisat boşluğu (egzoz kanalı geçişi)

T4 · Alçıpan asma tavan — soyunma +2,60


- T2 ile aynı karkas ve kaplama
- Soyunma/duş sınırında kot geçiş bandı (dikme)
- Nem nedeniyle duş kapısı önünde 1,0 m şeridinde H2 alçıpan
- Erkek · kadın soyunma — üstünde 600 mm tesisat boşluğu

TAVAN KOORDİNASYONU — KONTROL EDİLDİ

Armatür, menfez, hoparlör ve dedektör konumları elektrik (E-02, E-04) ve mekanik (M-02) paftalarıyla aynı kaynaktan üretilmiştir; otomatik çıkışma kontrolü (tools/kontrol.py) yapılmıştır. Menfezler lineer armatür sıraları arasına yerleştirilmiş, aynı hizada üst üste gelmesi önlenmiştir. Askı çubukları kanal ve boru güzergâhlarından bağımsız planlanacaktır.


KESİT A-A · ENİNE KESİT — FONKSİYONEL ALAN, ERKEK DUŞ VE WC BLOĞU

1/50 (A3)

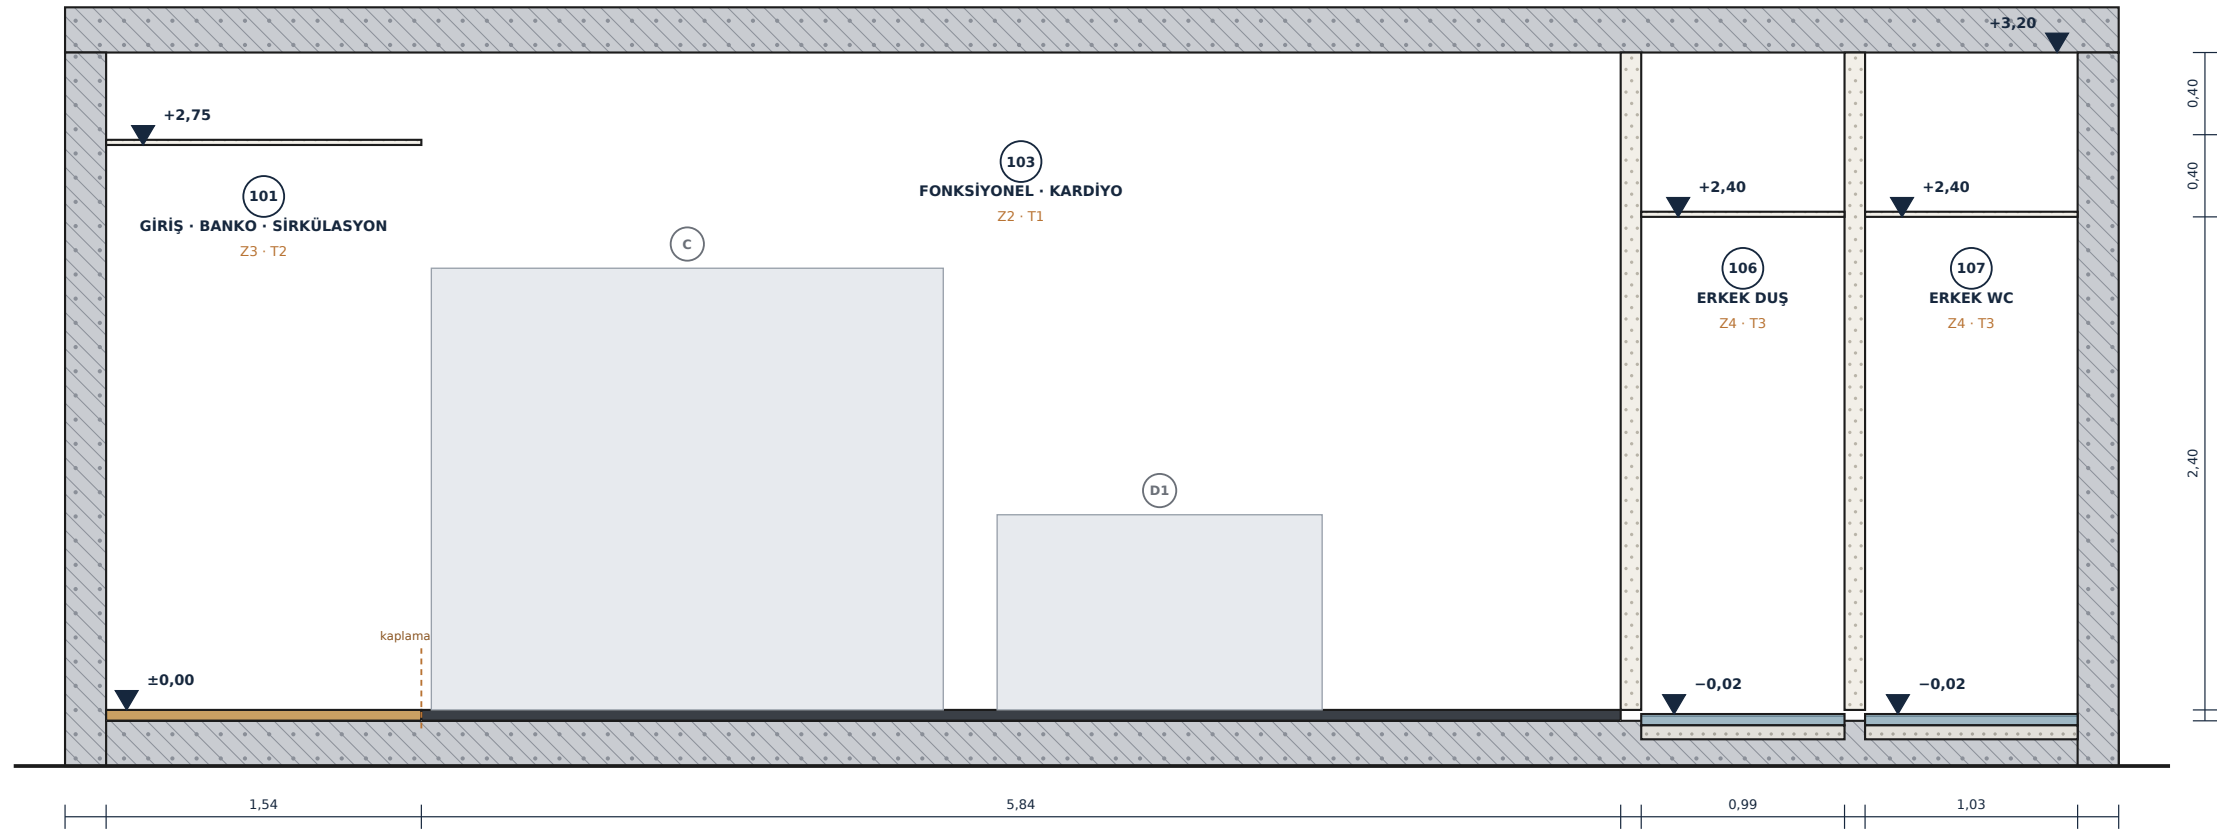

Pafta	A-06
Ölçek	1/50 (A3)
Tarih	17 Eylül 2026
Durum	Uygulama — yerinde doğrulanacak

ANAHTAR PLAN

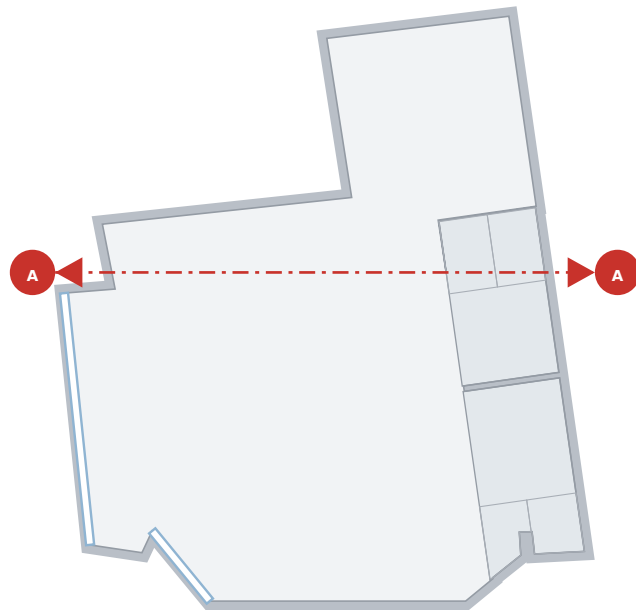


KESİTTE GEÇİLEN MAHALLER

NO	MAHAL	ZEM.	SÜP.	TAV.	T.KOT	Z.KOT
101	GİRİŞ · BANKO · SİRKÜLASYON	Z3	S2	T2	2,75	±0,00
103	FONKSİYONEL · KARDİYO	Z2	S1	T1	3,20	±0,00
106	ERKEK DUŞ	Z4	S3	T3	2,40	-0,02
107	ERKEK WC	Z4	S3	T3	2,40	-0,02

KESİT NOTLARI

Kesilen elemanlar kalın kurtulma ve malzeme taramasıyla, kesit düzleminin arkasında kalan ekipman silüeti ince gri kurtulma gösterilmiştir. Tüm alçıpan bölmeler yapısal düşmeye kadar (+3,20) yükselir, asma tavan hizasında kesilmez. Yapısal düşme kalınlığı ve tavan yüksekliği VARSAYIMDIR – sökülü sonrası yerinde ölçülecek, kesitler ve tavan kotları buna göre revize edilecektir. Zemin katman kalınlıkları bu ölçekte okunmaz; A-11 ve A-12 detaylarına bakınız. Kesit hatı üzerinde kalmayan kapı ve pencereler gösterilmemiştir; doğrama bilgisi için A-10'a bakınız.

1/50 (A3)

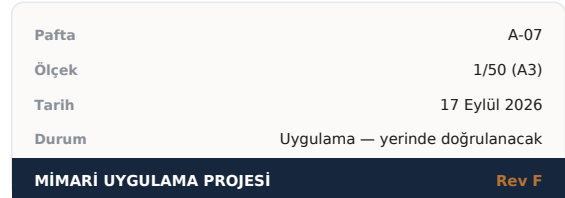


A diagram of a building floor plan with a vertical dashed line labeled 'B' at both ends, indicating a section line. The floor plan is light gray with a thick gray border. The dashed line is red with red triangular arrowheads pointing towards the plan. The label 'B' is in a red circle at each end of the line.

NO	MAHAL	ZEM.	SÜP.	TAV.	T.KOT	Z.KOT
102	ARENA · SERBEST AĞIRLIK	Z1	S1	T1	3,20	±0,00
103	FONKSIYONEL · KARDİYO	Z2	S1	T1	3,20	±0,00
104	DİNLENME SALONU	Z3	S2	T2	2,75	±0,00

Kesilen elemanlar kalın kontrol ve malzeme taramasıyla, kesit düzleminin arkasında kalan ekipman silüeti ince gri kontrolü gösterilmiştir. Tüm alçıpan bölmeler yapısal döşemeye kadar (+3,20) yükselir, asma tavan hizasında kesilmez. Yapısal döşeme kalınlığı ve tavan yüksekliği VARSA YİMDİR — söküm sonrası yerinde ölçülecek, kesitler ve tavan kotları buna göre revize edilecektir. Zemin katman kalınlıkları bu ölçekte okunmaz; A-11 ve A-12 detaylarına bakınız. Kesit hattı üzerinde kalmayan kapı ve pencereler gösterilmemiştir; doğrama bilgisi için A-10'a bakınız.


G-01 · GİRİŞ VE BANKO DUVARI — 101'den batıya bakış

5,60 m açıklık · tavan +2,75

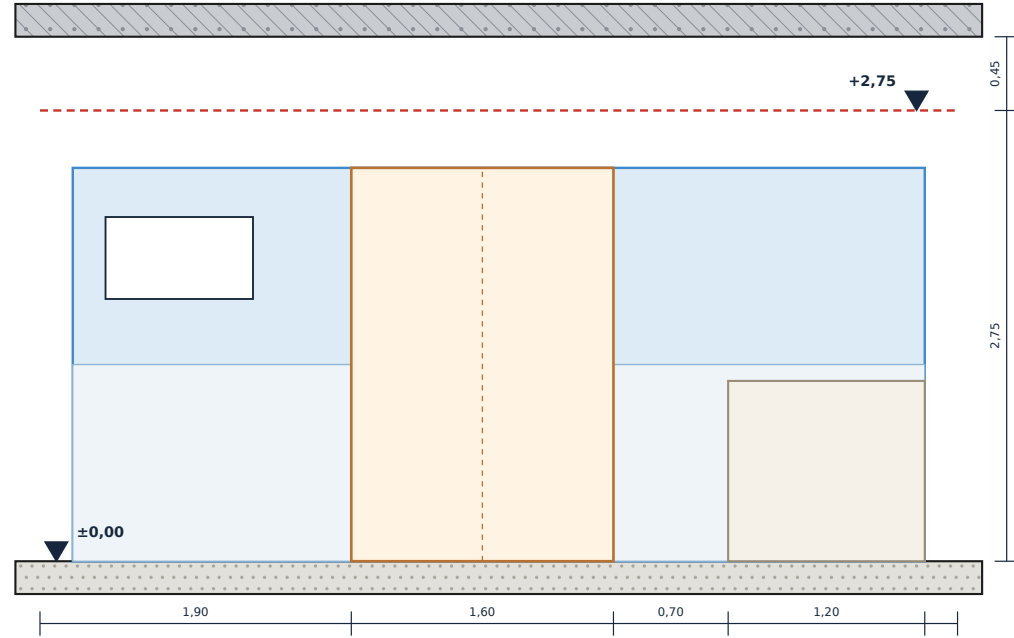


G-02 · ARENA GÜNEY DUVARI — 102'den güneye bakış

5,02 m açıklık · tavan +3,20

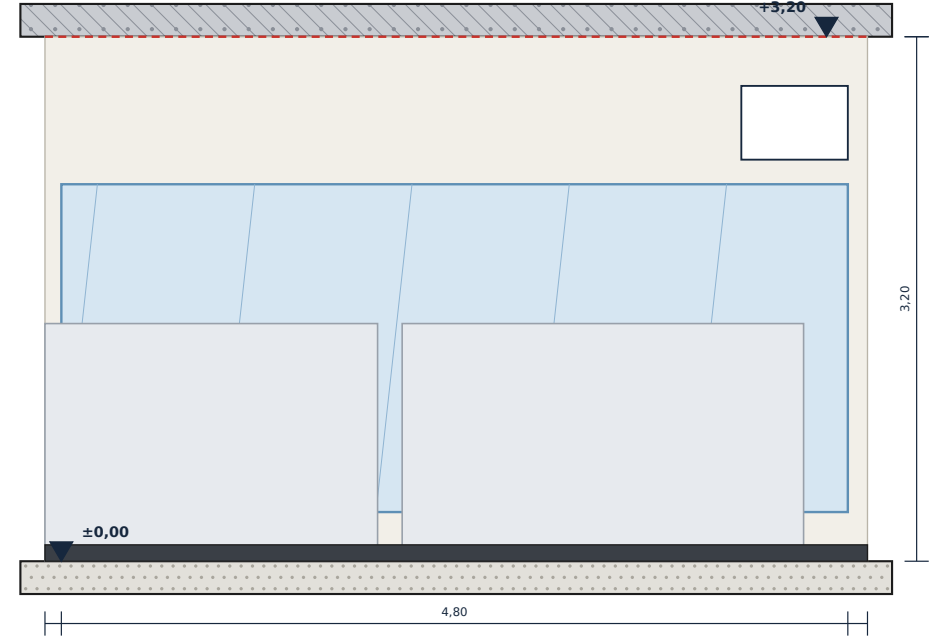


G-03 · SOYUNMA BLOĞU CEPHESİ — salondan doğuya bakış

8,05 m açıklık · tavan +3,20

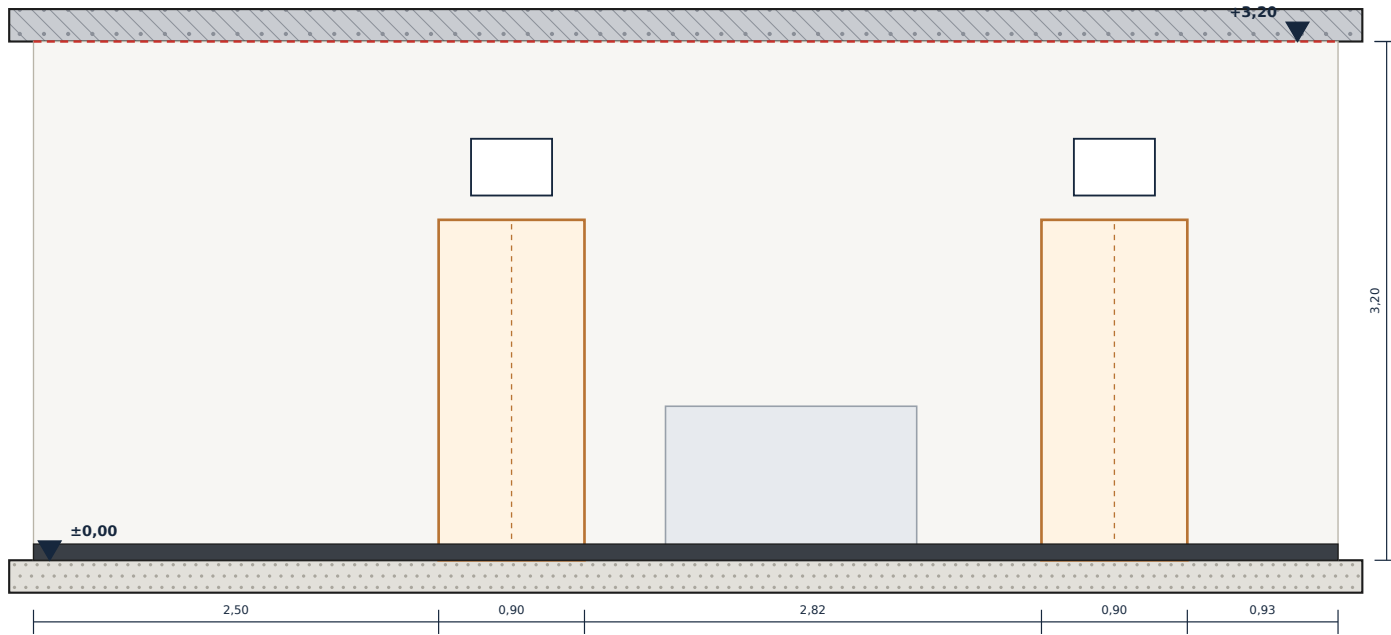

G-04 · ERKEK SOYUNMA İÇ GÖRÜNÜŞ — 105'ten kuzeye bakış

2,60 m açıklık · tavan +2,60

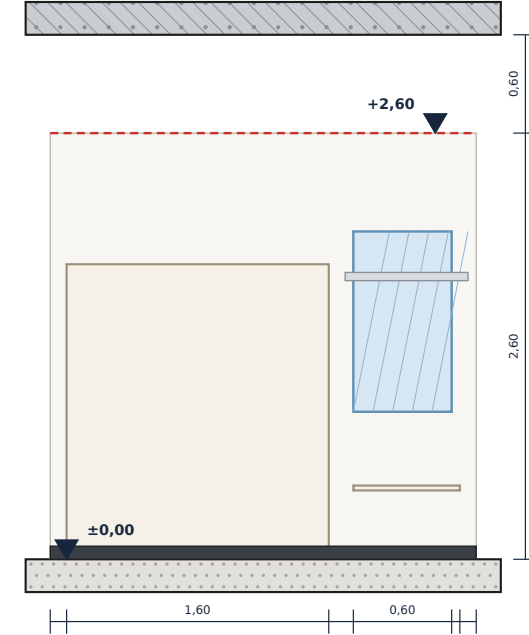

G-01

- Mevcut cephe vitrini P01 — alt 1,20 m buzlu folyo
- Buzlu folyo bandı
- K01 çift kanat cam giriş kapısı — dışa açılır
- Banko — 120×60 cm, lake MDF + kompakt lamine tezgâh
- Tesis tabelası ve çalışma saatleri
- T2 alçıpan asma tavan +2,75

G-02

- D6 ayna duvarı 4,80×2,00 m — 6 mm, arka yüz güvenlik filmli
- F1 — koşu bandı (245×74 cm), duvardan 60 cm serbest
- F2 — koşu bandı (245×74 cm)
- S1 kauçuk süpürgelik 100 mm
- «Ağırılık düşürmek yasaktır» uyarı levhası
- T1 açık tavan +3,20 — siyah boyalı, akustik baffle

G-03

- K04 kadın soyunma kapısı 90×210 — alt menfez 150 cm²
- K03 erkek soyunma kapısı 90×210 — alt menfez 150 cm²
- Piktogram — KADIN
- Piktogram — ERKEK
- D2 — dambıl rafı / sehpa (duvar önü, 155×39 cm)
- S1 kauçuk süpürgelik 100 mm
- T1 açık tavan +3,20 — bölme tavan üstünden döşemeye devam eder

G-04

- 8 gözlü soyunma dolabı 160×45×180 cm — laminat, havalandırma delikli
- Bank 160×35 cm, ahşap latalı, duvara konsol bağlantılı
- Boy aynası 60×110 cm — güvenlik filmli
- Paslanmaz askılık — 5 kancalı
- S4 porselen süpürgelik 80 mm
- T4 alçıpan asma tavan +2,60

NO	MAHAL	M²	ZEMİN	SÜP.	DUVAR	TAVAN	KOT	KAPI	AÇIKLAMA
101	GİRİŞ · BANKO · SİRKÜLASYON	15,65	Z3	S2	D1	T2	2,75	K01 · K09	Cephe vitrini mevcut (P01); alt 1,20 m buzlu folyo. Banko arkası D1 üzeri lake MDF panel.
102	ARENA · SERBEST AĞIRLIK	31,76	Z1	S1	D1 + D4 (güney çeper) + D6 (ayna, 4,80 m)	T1	3,20	—	Ring platformu Z6. Ağırlık düşürme kural olarak yasak — uyarı levhası.
103	FONKSİYONEL · KARDİYO	22,31	Z2	S1	D1 / D2 (soyunma bloğu cephesi)	T1	3,20	—	Koşu bandı arkasında 60 cm serbest güvenlik mesafesi bırakılacak.
104	DİNLENME SALONU	17,33	Z3	S2	D1	T2	2,75	—	Yönetmelik gereği asgari 15 m² dinlenme alanı — sağlanıyor.
105	ERKEK SOYUNMA	4,48	Z5	S4	D2 / D3	T4	2,60	K03	8 kişilik soyunma dolabı + 1,60 m bank + boy aynası. Yönetmelik asgarisi 8 m² blok bazında.
106	ERKEK DUŞ	1,76	Z4	S3	D3 + D5 (tavana kadar)	T3	2,40	K07	1 duş yeri; 100×100 mm paslanmaz süzgeç, %1,5 eğim, termostatik batarya.
107	ERKEK WC	1,75	Z4	S3	D3 + D5 (h=1,60 m)	T3	2,40	K05	1 klozet + 1 lavabo; ekstraktör fan kapı menfezi ile telafi havası.
108	KADIN SOYUNMA	5,59	Z5	S4	D2 / D3	T4	2,60	K04	8 kişilik soyunma dolabı + 1,60 m bank + boy aynası.
109	KADIN DUŞ	1,39	Z4	S3	D3 + D5 (tavana kadar)	T3	2,40	K08	1 duş yeri; 100×100 mm paslanmaz süzgeç, %1,5 eğim, termostatik batarya.
110	KADIN WC	1,29	Z4	S3	D3 + D5 (h=1,60 m)	T3	2,40	K06	1 klozet + 1 lavabo; ekstraktör fan kapı menfezi ile telafi havası.

Net mahal alanları toplamı 103,31 m² · iç bölme duvar payı 0,47 m² · net iç kullanım alanı 103,78 m².

SÜPÜRGELİK TİPLERİ

KOD	TANIM
S1	Kauçuk süpürgelik 100×8 mm — zemin kaplamasıyla aynı malzeme, üst kenarı 45° pahlı
S2	MDF lake süpürgelik 80×16 mm — RAL 9003, akrilik mastik ile duvara yalanır
S3	Süpürgelik yok — duvar seramiği zemine iner; birleşimde içbükey (kaveto) profil
S4	Porselen süpürgelik 80 mm — zemin karosundan kesme, rektifiye kenar

MALZEME ONAY VE NUMUNE ŞARTI

NUMUNE ONAYI

Kauçuk karo, SPC/LVT, porselen seramik, alçıpan boyası ve süpürgelik için imalat öncesi 30×30 cm numune ve teknik föy (CE beyanı, kayma direnci ve yangın sınıfı belgesi) sunulacak; işveren yazılı onayı alınmadan sipariş verilmeyecektir.

YÖNETMELİK BAĞLANTISI

Özel Beden Eğitimi ve Spor Tesisleri Yönetmeliği; soyunma mahalleri için blok başına asgari 8 m², dinlenme alanı için asgari 15 m² aramaktadır. Mahal listesinde 105+106+107 = 7,99 m² ve 108+109+110 = 8,27 m², 104 dinlenme salonu 17,33 m² ile her iki şart sağlanmaktadır. Salon alanına ilişkin GSİM uygulaması için ana dosyanın uygunluk sayfasına bakınız.

İMALAT ŞARTNAMESİ ÖZETİ — TİP KODLARININ KATMAN KARŞILIĞI

TİP	TANIM	KATMAN DİZİLİMİ (ALTtan ÜSTE / İÇTEN DİŞA)	TOPLAM	PERFORMANS · STANDART · MAHAL
Z1	Arena · serbest ağırlık — ağır hizmet kauçuk	Çimento esaslı kendinden yayılan tesviye şapı 3 mm + Kauçuk titreşim yalıtım matı, SBR granül 700 kg/m³ 10 mm + Granül kauçuk karo 1000×1000 mm, EPDM %10 taneli, Shore A 55±5 40 mm	53 mm	EN 14041 · yangın Bfl-s1 · EN ISO 10140 ΔLw ≥ 18 dB · serbest ağırlık düşürmeye uygun
Z2	Fonksiyonel · kardiyo — kauçuk karo	Çimento esaslı tesviye şapı 30 mm + Granül kauçuk karo 1000×1000 mm, Shore A 60 20 mm + Puzzle kilitli kuru derz · çeperde 5 mm genişleme boşluğu 3 mm	53 mm	EN 14041 · Bfl-s1 · kardiyo cihazı nokta yükü ≥ 4 kN/m²
Z3	Giriş · banko · dinlenme — SPC / LVT	Çimento esaslı tesviye şapı 42 mm + IXPE akustik şilte 2 mm + SPC klik LVT, 0,55 mm aşınma tabakası 5 mm + Çeperde 8 mm genişleme boşluğu, süpürgelik altında gizlenir 4 mm	53 mm	EN ISO 10874 aşınma sınıfı 33 / AC5 · EN 14041 Bfl-s1 · kaymazlık DS
Z4	Duş · WC — su yalıtımlı seramik	Atık boru yatağı + tesisat şapı 25 mm + Eğim şapı 15 mm + Çimento esaslı 2 bileşenli su yalıtımı, 2 kat 2 mm + C2TE S1 sınıfı yapıştırıcı 5 mm + Porselen seramik 300×300 mm, R11 / B kaymazlık 8 mm	55 mm	EN 14891 su yalıtımı · EN 16165 Ek B (R11) · Ek A (B sınıfı ıslak ayak)
Z5	Soyunma — porselen seramik	Çimento esaslı tesviye şapı 38 mm + Çimento esaslı su yalıtımı, tek kat 1 mm + C2TE yapıştırıcı 5 mm + Porselen seramik 600×600 mm, R10 9 mm	53 mm	EN 16165 Ek B (R10) · EN 14411 Bla · rektifiye, 2 mm derz
Z6	Ring platformu (ekipmana bağlı — işverence temin)	Bitmiş zemin Z1 üzeri ayarlı çelik ayak + 50×100 ahşap kadron @400 mm 200 mm + Su kontraplağı 2 kat 18 mm, şaşırtmalı vidalı 36 mm + EVA şok emici köpük 40 mm + Kanvas kaplama, kenarda gergi profili 10 mm + Kenarda 100 mm kauçuk kenar bandı + sarı-siyah ikaz şeridi 14 mm	300 mm	Ekipman üreticisi montaj talimatına tabi · platform kenarı zeminden 30 cm
D1	Mevcut taşıyıcı / dolgu duvar — boyalı	Mevcut yığma veya betonarme duvar 200 mm + Çimento esaslı tamir harcı ile yüzey onarımı + Saten alçı perdah, 2 kat 3 mm + Akrilik astar + su bazlı silikonlu mat iç cephe boyası, 2 kat 3 mm	206 mm	Sınıf 1 yıkanabilir boya · mevcut duvar kalınlığı VARSAYIM, yerinde ölçülecek
D2	Alçıpan bölme — kuru hacim	12,5 mm A tipi alçıpan, 2 kat 25 mm + 50×0,6 mm galvaniz C profil @400 mm + U tabanlık 50 mm + Taşyünü dolgu 40 mm / 50 kg/m³ + 12,5 mm A tipi alçıpan, 2 kat 25 mm	100 mm	Rw ≈ 51 dB (EN ISO 717-1) · U tabanlık altında butil ses bandı
D3	Alçıpan bölme — ıslak hacim yüzü	12,5 mm H2 25 mm + 50×0,6 mm galvaniz C profil @400 mm + U tabanlık 50 mm + Taşyünü dolgu 40 mm / 50 kg/m³ + 12,5 mm A tipi alçıpan, 2 kat 25 mm	100 mm	EN 520 tip H2 · ıslak yüzde 2 kat çimento esaslı su yalıtımı + seramik (kalınlık hariç)
D4	Akustik giydirme — arena çeperi	Mevcut duvardan bağımsız 20 mm hava boşluğu 20 mm + 50×0,6 mm C profil karkas 50 mm + Taşyünü dolgu 50 mm / 70 kg/m³ + 12,5 mm yüksek yoğunluklu akustik alçıpan 12,5 mm + 12,5 mm A tipi alçıpan + saten + boya 12,5 mm	95 mm	ΔRw ≈ +10 dB · üst kat konut VARSAYIMI gereği arena çeperinde uygulanır
D5	Seramik kaplı duvar — ıslak hacim	Mevcut duvar veya D3 ıslak yüzü 200 mm + Çimento esaslı 2 bileşenli su yalıtımı, 2 kat; köşe ve zemin birleşiminde 12 cm bant 2 mm + C2TE S1 yapıştırıcı 5 mm + Porselen seramik 300×600 mm, rektifiye 9 mm	216 mm	EN 14891 · duş kabininde tavana kadar, WC'de h=1,60 m, üstü küf önleyici banyo boyası
D6	Ayna duvarı — arena güney çeperi (D1/D4 üzerine giydirme)	D1 veya D4 üzerine 18 mm su kontraplağı taşıyıcı altlık 18 mm + 6 mm güvenlik filmli ayna, yapıştırma + mekanik emniyet profili 6 mm	24 mm	Ayna alt kotu +0,30 · üst kotu +2,30 · kırılmaya karşı arka yüz güvenlik filmi (EN 12600)
T1	Açık (endüstriyel) tavan	Mevcut döşeme altı raspa + temizlik + Tüm MEP tesisatı görünür + 2 kat siyah su bazlı akrilik boya + Arena üzerinde 12 adet 1200×600×50 mm asma akustik taşyünü baffle	+3,20	Arena · fonksiyonel — serbest yükseklik korunur, ekipman kotu 2,15 m'ye kadar
T2	Alçıpan asma tavan — kuru hacim	Ayarlı askı çubuğu @900 mm, TC47 ana profil @900 / TU27 taşıyıcı @400 mm + 12,5 mm A tipi alçıpan tek kat + Derz bandı + 2 kat saten alçı + astar + 2 kat mat boya + Kenar gölge derzi 10 mm	+2,75	Giriş · banko · dinlenme — üstünde 450 mm tesisat boşluğu (kanal + tava + bakır hat sığsın diye kot 2,80'den 2,75'e indirilmiştir)
T3	Alçıpan asma tavan — ıslak hacim	Galvaniz ayarlı askı @900 mm, TC47 / TU27 karkas + 12,5 mm H2 + Su bazlı, küf önleyici yarı mat banyo boyası, 2 kat + 300×300 mm menteşeli revizyon kapağı	+2,40	Duş · WC — üstünde 800 mm tesisat boşluğu (egzoz kanalı geçişi)
T4	Alçıpan asma tavan — soyunma	T2 ile aynı karkas ve kaplama + Soyunma/duş sınırında kot geçiş bandı + Nem nedeniyle duş kapısı önünde 1,0 m şeridinde H2 alçıpan	+2,60	Erkek · kadın soyunma — üstünde 600 mm tesisat boşluğu

KAPI LİSTESİ

KOD	AD.	MAHAL	EN×YÜK (MM)	TİP	KANAT / KASA	DONANIM	ÖZEL ŞART
K01	1	101 Giriş	1600×2400	Çift kanat cam kapı (2×800)	Mevcut alüminyum doğrama + 8 mm temperli cam	Panik kolu (EN 1125), hidrolik kapı kapatıcı, eşiksiz alt profil	Açılış yönü DIŞARI çevrilecek — mevcut doğrama revize
K02	1	101 → GB cephe	1000×2100	Tek kanat acil çıkış	Alüminyum + 8 mm temperli cam	Panik bar (EN 1125), kapı kapatıcı, dışa açılır	Acil çıkış levhası + acil aydınlatma AY3 üstünde
K03	1	105 Erkek soyunma	900×2100	Tek kanat panel kapı	MDF laminat kaplı kanat, WPC kasa ve pervaz	Paslanmaz kol, silindirli kilit, 3 adet menteşe	Alt kısmında 150 cm² net hava geçiş menfezi
K04	1	108 Kadın soyunma	900×2100	Tek kanat panel kapı	MDF laminat kaplı kanat, WPC kasa ve pervaz	Paslanmaz kol, silindirli kilit, 3 adet menteşe	Alt kısmında 150 cm² net hava geçiş menfezi
K05	1	107 Erkek WC	700×2000	Tek kanat WC kapısı	Tam WPC (su geçirmez) kanat ve kasa	Kilit göstergeli WC kolu, paslanmaz menteşe	Alt menfez 150 cm² — egzoz telafi havası
K06	1	110 Kadın WC	700×2000	Tek kanat WC kapısı	Tam WPC (su geçirmez) kanat ve kasa	Kilit göstergeli WC kolu, paslanmaz menteşe	Alt menfez 150 cm² — egzoz telafi havası
K07	1	106 Erkek duş	700×1950	Duş kapağı	6 mm temperli cam, alüminyum profil	Paslanmaz menteşe, manyetik fitil	Alt kenar zeminden 15 mm yukarıda
K08	1	109 Kadın duş	700×1950	Duş kapağı	6 mm temperli cam, alüminyum profil	Paslanmaz menteşe, manyetik fitil	Alt kenar zeminden 15 mm yukarıda
K09	1	101 Depo / teknik dolap	700×2000	Tek kanat dolap kapağı	MDF laminat, banko arkası niş	Bas-aç mandal, kilitli	Havalandırma menfezli — NVR ve router ısısı için

PENCERE / CEPHE DOĞRAMASI

KOD	AD.	MAHAL	DOĞRAMA	CAM / KAPLAMA	NOT
P01	1	101 Giriş — batı cephe vitrini	Mevcut alüminyum doğrama + 8 mm temperli cam	Alt 1,20 m buzlu folyo · üst bant şeffaf · iç yüzde güneş kontrol filmi	Mevcut — ölçü yerinde alınacak (VARSAYIM: 5,62 m açıklık)
P02	1	101 Giriş — GB cephe vitrini	Mevcut alüminyum doğrama + 8 mm temperli cam	Alt 1,20 m buzlu folyo · K02 acil çıkış bu doğrama içinde	Mevcut — ölçü yerinde alınacak (VARSAYIM: 2,02 m açıklık)

DUVAR TİPLERİ — KATMAN DİZİLİMİ

D1 · Mevcut taşıyıcı / dolgu duvar — boyalı206 mm

1. Mevcut yığma veya betonarme duvar — 200 mm

2. Çimento esaslı tamir harcı ile yüzey onarımı

3. Saten alçı perdah, 2 kat — 3 mm

4. Akrilik astar + su bazlı silikonlu mat iç cephe boyası, 2 kat — 3 mm

yatay kesit — katman genişlikleri orantılıdır

Sınıf 1 yıkanabilir boya · mevcut duvar kalınlığı VARSAYIM, yerinde ölçülecek

D2 · Alçıpan bölme — kuru hacim100 mm

1. 12,5 mm A tipi alçıpan, 2 kat (şaşırtmalı derz) — 25 mm

2. 50×0,6 mm galvaniz C profil @400 mm + U tabanlık — 50 mm

3. Taşyünü dolgu 40 mm / 50 kg/m³

4. 12,5 mm A tipi alçıpan, 2 kat — 25 mm

yatay kesit — katman genişlikleri orantılıdır

Rw ≈ 51 dB (EN ISO 717-1) · U tabanlık altında butil ses bandı

D3 · Alçıpan bölme — ıslak hacim yüzü100 mm

1. 12,5 mm H2 (su itici / yeşil) alçıpan, 2 kat — ıslak yüz — 25 mm

2. 50×0,6 mm galvaniz C profil @400 mm + U tabanlık — 50 mm

3. Taşyünü dolgu 40 mm / 50 kg/m³

4. 12,5 mm A tipi alçıpan, 2 kat — kuru yüz — 25 mm

yatay kesit — katman genişlikleri orantılıdır

EN 520 tip H2 · ıslak yüzde 2 kat çimento esaslı su yalıtımı + seramik (kalınlık hariç)

D4 · Akustik giydirme — arena çeperi95 mm

1. Mevcut duvardan bağımsız 20 mm hava boşluğu — 20 mm

2. 50×0,6 mm C profil karkas (duvara bağlantısız, tavan-döşeme arası) — 50 mm

3. Taşyünü dolgu 50 mm / 70 kg/m³

4. 12,5 mm yüksek yoğunluklu akustik alçıpan — 12,5 mm

5. 12,5 mm A tipi alçıpan + saten + boya — 12,5 mm

yatay kesit — katman genişlikleri orantılıdır

ΔRw ≈ +10 dB · üst kat konut VARSAYIMI gereği arena çeperinde uygulanır

D5 · Seramik kaplı duvar — ıslak hacim216 mm

1. Mevcut duvar veya D3 ıslak yüzü — 200 mm

2. Çimento esaslı 2 bileşenli su yalıtımı, 2 kat; köşe ve zemin birleşiminde 12 cm bant — 2 mm

3. C2TE S1 yapıştırıcı — 5 mm

4. Porselen seramik 300×600 mm, rektifiye — 9 mm

yatay kesit — katman genişlikleri orantılıdır

EN 14891 · duş kabininde tavana kadar, WC'de h=1,60 m, üstü küf önleyici banyo boyası

D6 · Ayna duvarı — arena güney çeperi (D1/D4 üzerine giydirme)24 mm

1. D1 veya D4 üzerine 18 mm su kontraplağı taşıyıcı altlık — 18 mm

2. 6 mm güvenlik filmlli ayna, yapıştırma + mekanik emniyet profili — 6 mm

yatay kesit — katman genişlikleri orantılıdır


Ayna alt kotu +0,30 · üst kotu +2,30 · kırılmaya karşı arka yüz güvenlik filmi (EN 12600)

Ön tasarım — yerinde doğrulanmadan ve ruhsat alınmadan uygulama yapılamaz. Tüm ölçüler raster paftadan ölçeklendirilmiştir (±%3).

17 Eylül 2026 · Sayfa 10 / 14

D-01 Z1 ZEMİN KATMAN DETAYI — ARENA · SERBEST AĞIRLIK


Z1

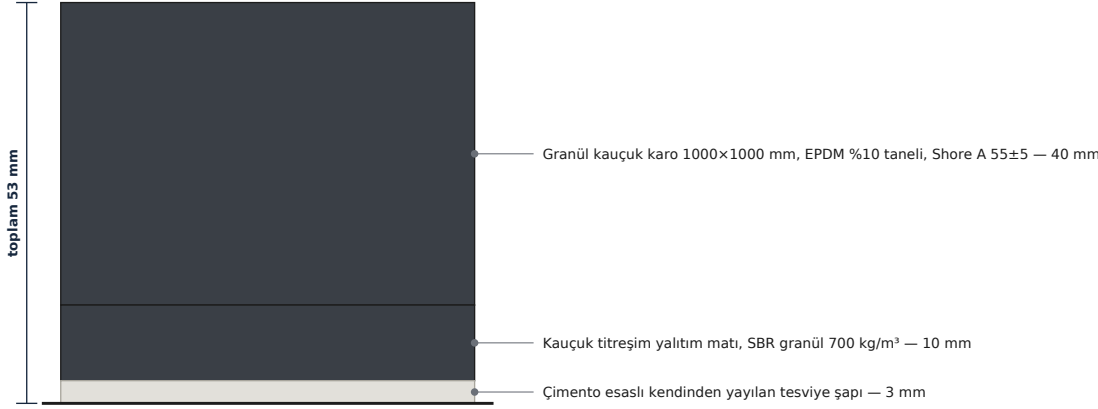

- Kauçuk karo çeperde 5 mm genleşme boşluğu ile biter; boşluk süpürgelik altında kalır.
- Titreşim matı duvara 50 mm yukarı dönerek yüzzer döşeme teşkil eder (yan geçiş sesi kesilir).
- Karo altı kuru uygulamadır — yapıştırıcı kullanılmaz, sökülüp değiştirilebilir.

D-02 Z4 ISLAK HACİM ZEMİN VE DUVAR BİRLEŞİMİ


Z4 · D5

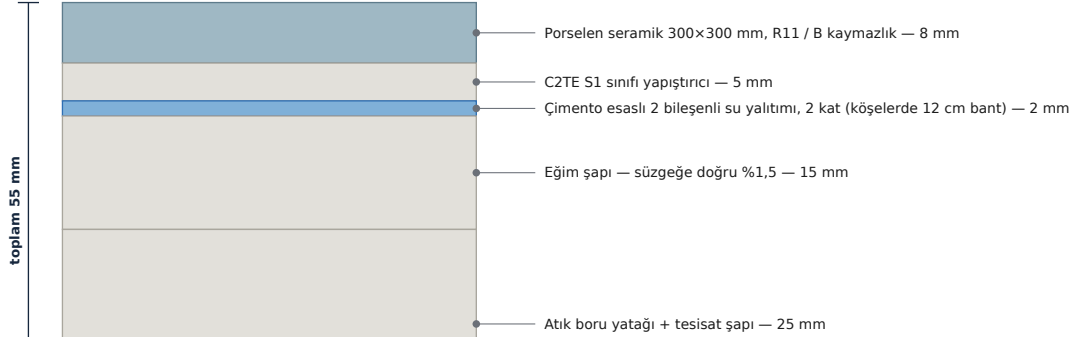

- Su yalıtımı duvarda en az 300 mm, duş kabininde 2000 mm yukarı döner.
- Zemin-duvar köşesinde 120 mm elastik su yalıtım bandı, yalıtımın iki katı arasına gömülür.
- Seramik derzi çimento esaslı (CG2 WA); köşe derzleri silikon (sınıf 25LM, küf önleyici).

D-03 Z3 / Z1 ZEMİN KOT VE MALZEME GEÇİŞ DETAYI

Z1 · Z2 · Z3 · Z5

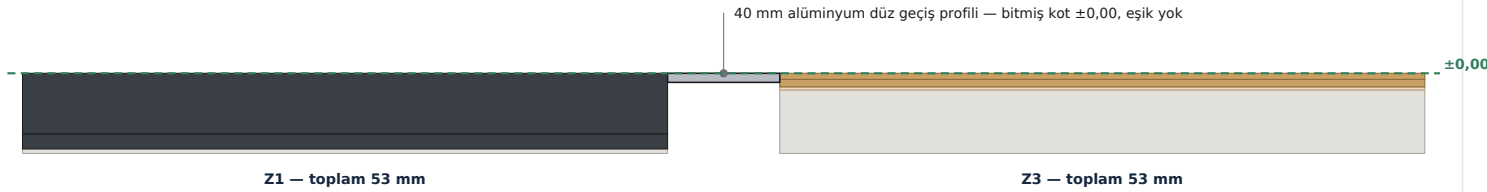

- Bitmiş zemin kotları eşittir (±0,00) — eşik veya rampa oluşmaz, tökezleme riski yoktur.
- Geçişte 40 mm alüminyum düz geçiş profili; kauçuk tarafta 5 mm genleşme boşluğu bırakılır.
- Tesviye şapı kalınlıkları farklıdır (Z1: 3 mm · Z2: 30 mm · Z3: 42 mm · Z5: 38 mm).

D-04 D2 ALÇIPAN BÖLME — YATAY KESİT VE KÖŞE


D2



- C profiller @400 mm; kapı kenarlarında ve 3,0 m'den uzun duvarlarda kutu profil takviye.
- Alçıpan derzleri iki yüzde şaşırtmalı; ikinci kat ilk katla 600 mm kaydırılır.
- Ağır asma yük (ayna, dolap, TV) için karkas içine 18 mm kontraplak takviye gömülür.

D-05 D3 ISLAK BÖLME + DUŞ SÜZGEÇ VE EĞİM DETAYI

D3 · Z4

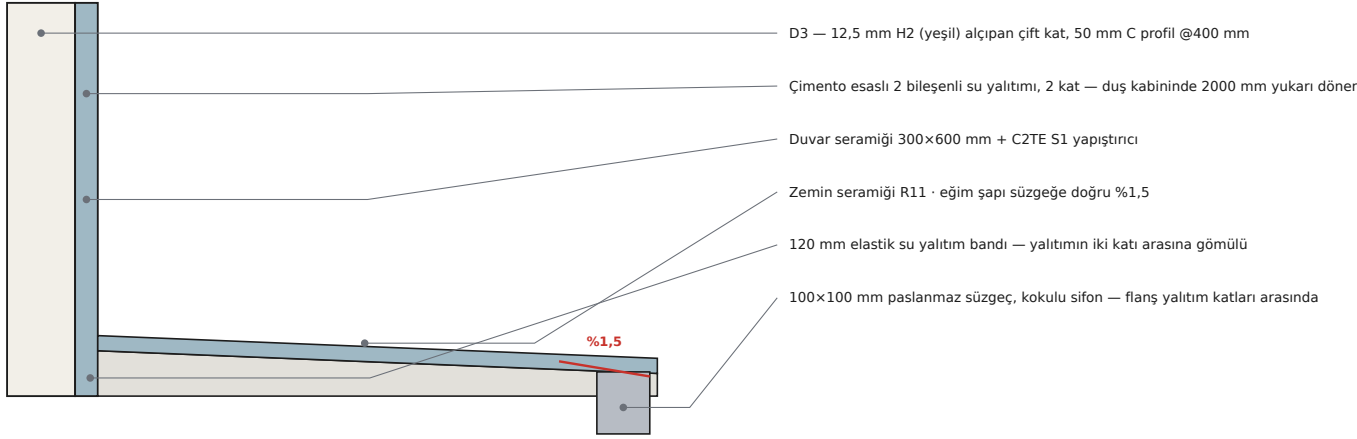


U tabanlılık butil bant üzerine · alçıpan alt kenarı bitmiş zeminden +10 mm

- Duş zemini süzgeçe %1,5 eğimli; süzgeç 100x100 mm paslanmaz, kokulu sifon (50 mm su tutuşlu).
- Süzgeç flanşı su yalıtımının iki katı arasına sıkıştırılır — sızdırmazlık burada sağlanır.
- U tabanlılık profil butil bant üzerine oturur; alçıpan alt kenarı bitmiş zeminden 10 mm yukarıda.

D-06 T2 / T3 ASMA TAVAN KENAR VE REVİZYON KAPAĞI


T2 · T3

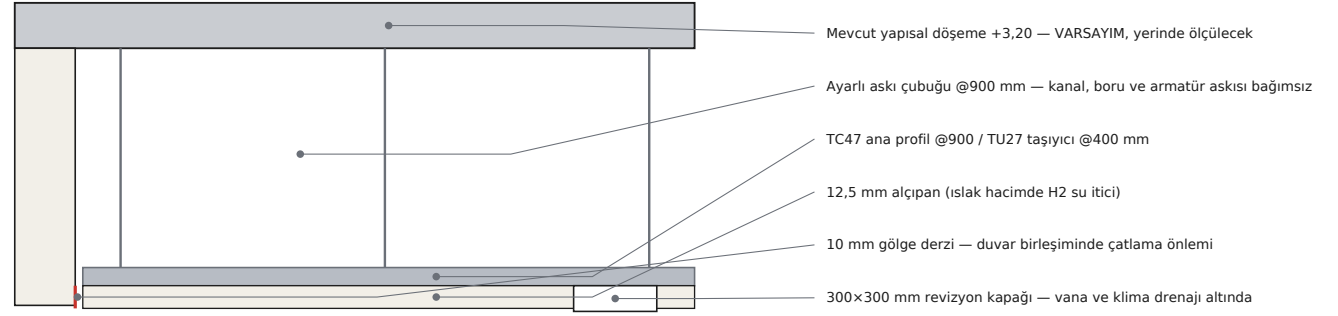

- Duvar birleşiminde 10 mm gölge derzi — farklı oturma nedeniyle çatlamayı önler.
- Askı @900 mm; kanal, boru veya armatür ağırlığı alçıpan karkasına asılmaz, ayrı askılanır.
- Her ıslak hacimde 300x300 mm revizyon kapağı; vana ve klima drenaj bağlantısı altında.

D-07 Z6 RING PLATFORMU KENAR DETAYI

Z6

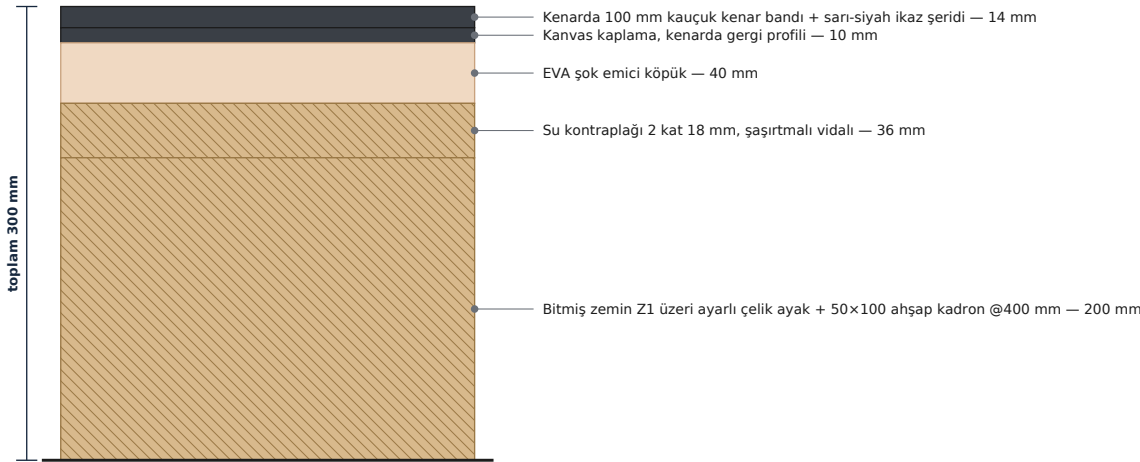


Katman şeması · ölçek 1/5 · bitmiş kot +0,30


- Platform ekipman üreticisinin montaj talimatına tabidir; bu detay çevre bitişini tanımlar.
- Kenarda 100 mm kauçuk kenar bandı + sarı-siyah ikaz şeridi (kot farkı 30 cm).
- Platform altı boşluğu havalandırılmalı bırakılır, temizlik için 2 gözde sökülebilir kapak.

D-08 D6 AYNA MONTAJ DETAYI

D6

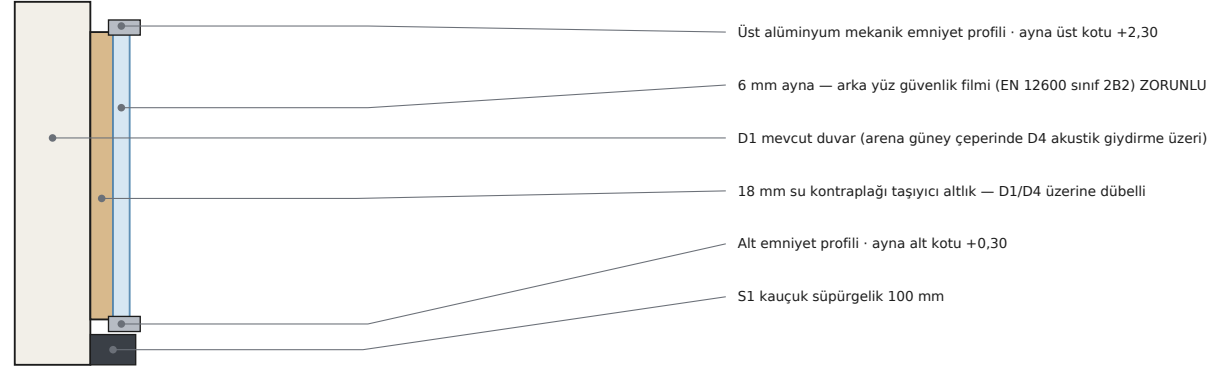

- Ayna alt kotu +0,30 (süpürgelik üstü), üst kotu +2,30.
- Arka yüzde güvenlik filmi (EN 12600 sınıf 2B2) ZORUNLU — serbest ağırlık alanında kırılma riski.
- Yapıştırma + alt ve üstte alüminyum mekanik emniyet profili; ayna arkası nemsiz kalmalı.

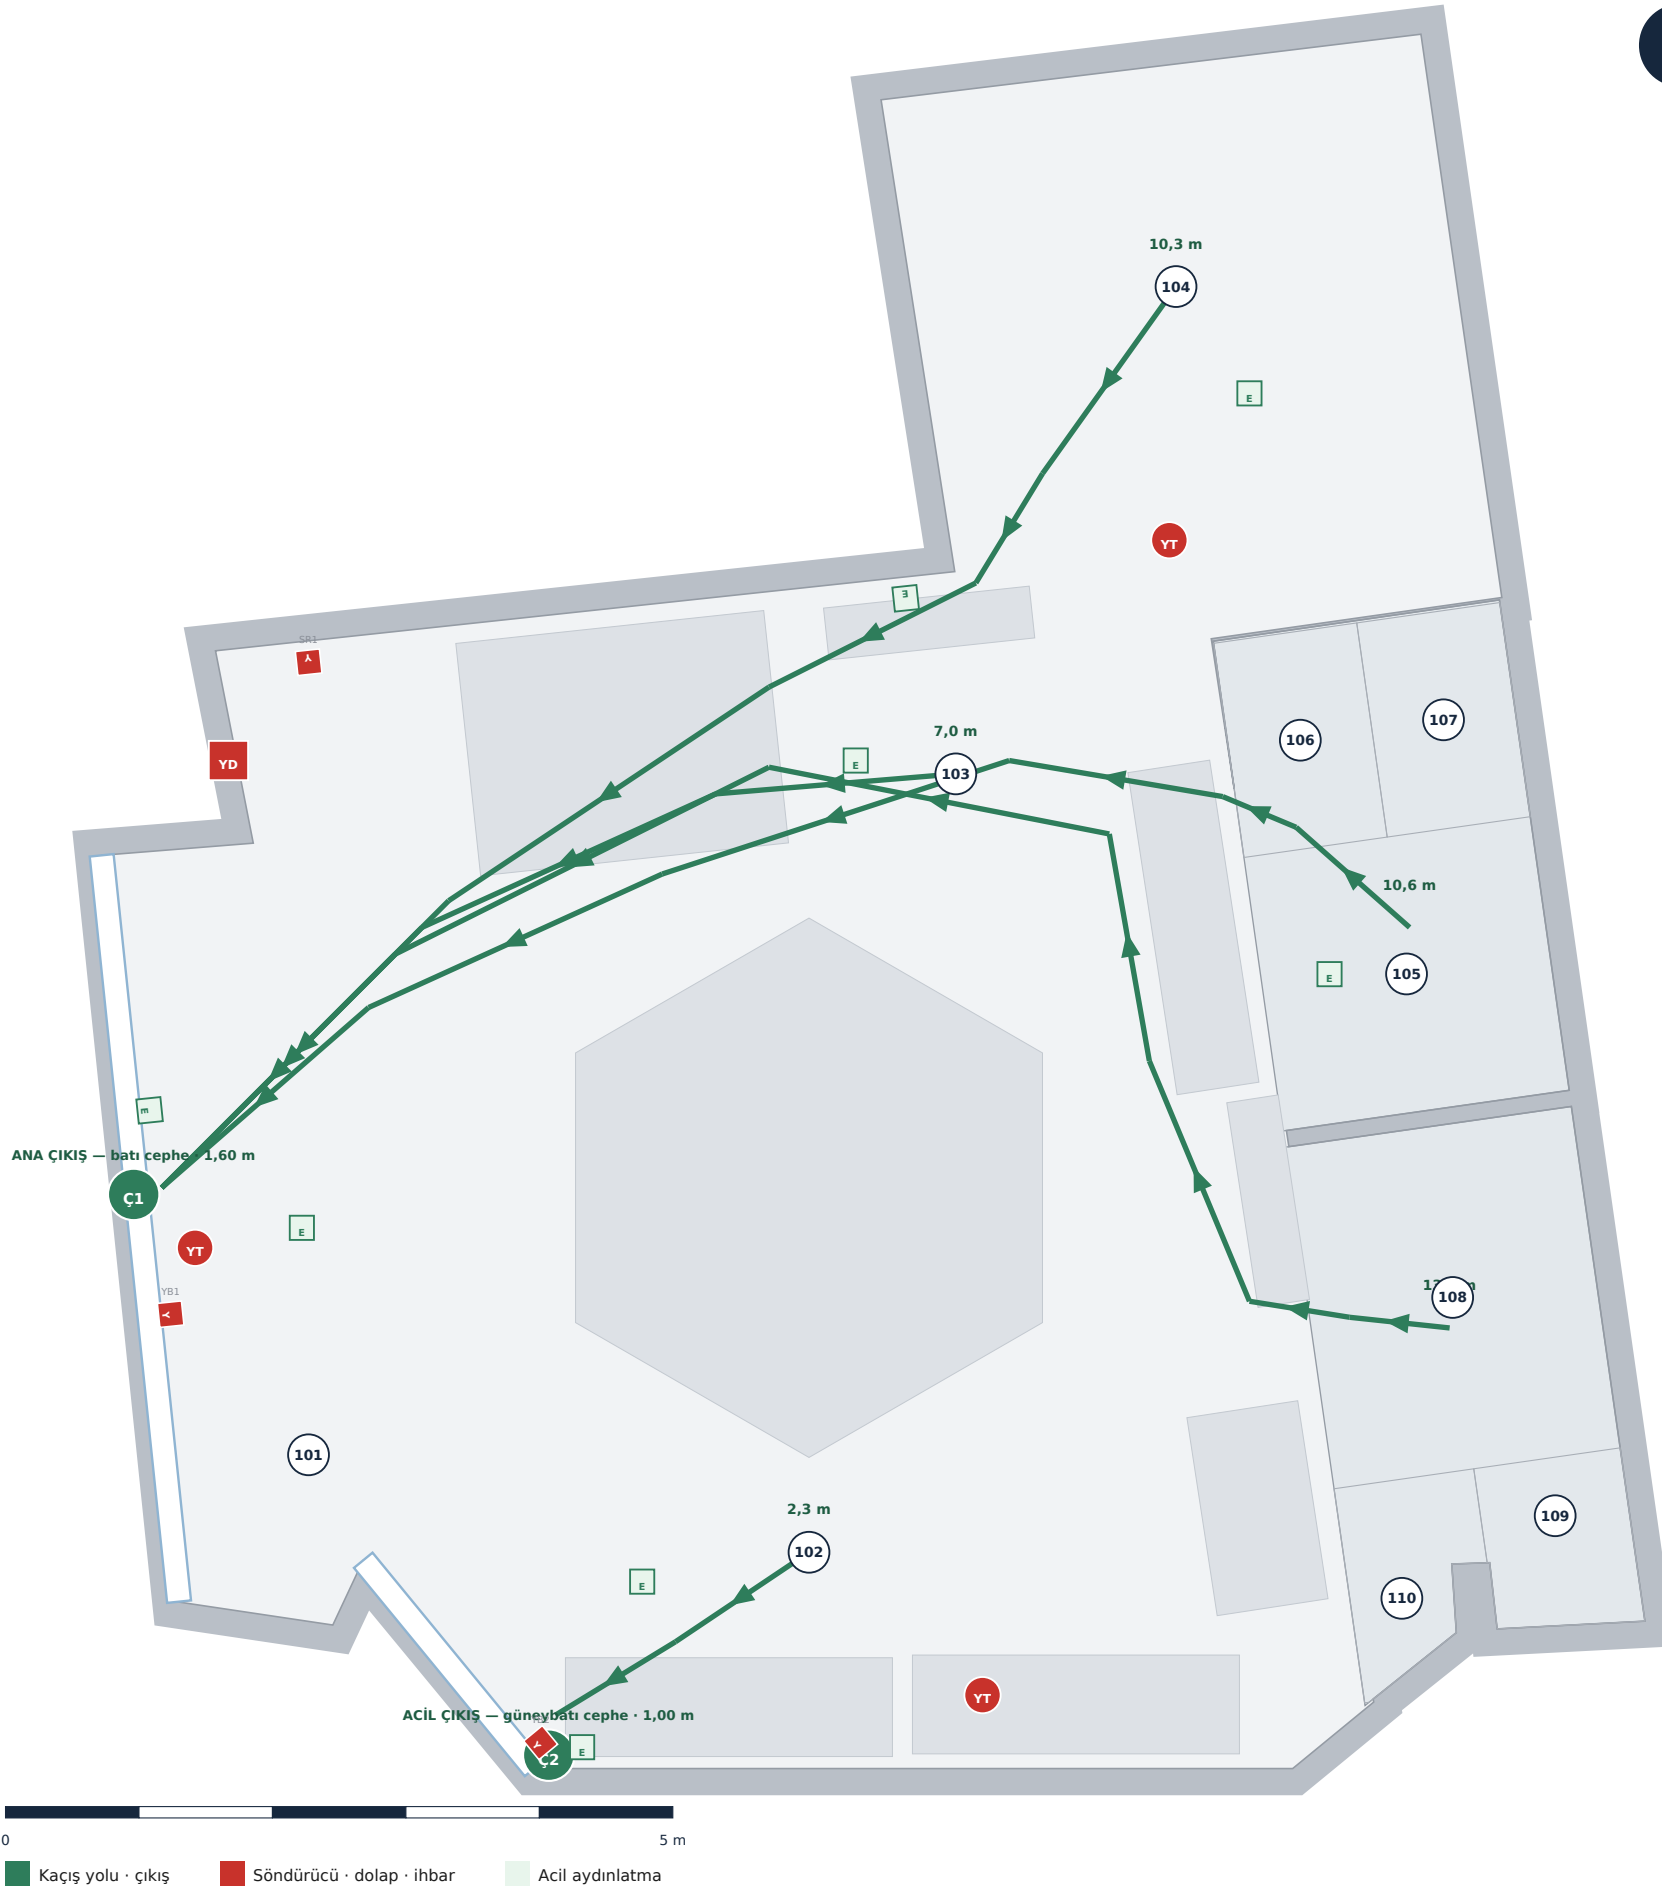

Pafta	A-13
Ölçek	1/75 (A3)
Tarih	17 Eylül 2026
Durum	Uygulama — yerinde doğrulanacak
MİMARİ UYGULAMA PROJESİ	
Rev F	

KAÇIŞ MESAFELERİ

NO	MAHAL	MESAFE	ÇIKIŞ
104	DİNLENME SALONU	10,3 m	Ç1
103	FONKSİYONEL · KARDİYO	7,0 m	Ç1
102	ARENA · SERBEST AĞIRLIK	2,3 m	Ç2
105	ERKEK SOYUNMA	10,6 m	Ç1
108	KADIN SOYUNMA	13,4 m	Ç1
EN UZUN KAÇIŞ		13,4 m	sınır 45 m

YANGIN GÜVENLİK DONANIMI


KOD	TANIM
YD1	Yangın dolabı — 30 m hortum, TS EN 671-2 (opsiyon: GSİM talebine göre)
YT1	6 kg ABC kuru kimyevi tozlu yangın söndürücü — çıkış yanında
YT2	6 kg ABC kuru kimyevi tozlu yangın söndürücü — dinlenme/soyunma yakını
YT3	6 kg ABC kuru kimyevi tozlu yangın söndürücü — acil çıkış yanında
YB1	yangın ihbar butonu — ana çıkış
YB2	yangın ihbar butonu — ikinci çıkış
SR1	siren + flaşör
AY1-3	Çıkış yönlendirme armatürü — kendinden akülü, 60 dk
AA1-5	Acil aydınlatma armatürü — kendinden akülü, 60 dk

TAHLİYE DEĞERLENDİRMESİ

İki bağımsız çıkış (Ç1 ana giriş 1,60 m · Ç2 acil çıkış 1,00 m) mevcuttur; toplam çıkış genişliği 2,60 m, 14 kişilik tasarım kapasitesi için fazlasıyla yeterlidir. En uzun kaçış mesafesi 13,4 m olup Binaların Yangından Korunması Hakkında Yönetmelik'in iki çıkışlı tesisler için öngördüğü sınırın çok altındadır. Kaçış kapıları kaçış yönünde açılacak, panik donanımlı olacak, üzerinde kilit bulunmayacaktır. Kaçış yolu genişliği hiçbir noktada 1,10 m'nin altına düşmeyecek; ekipman ve mobilya bu koridora taşınılmayacaktır.


D2 · Alçıpan bölme — kuru hacim

toplam 100 mm · ölçek 1/5

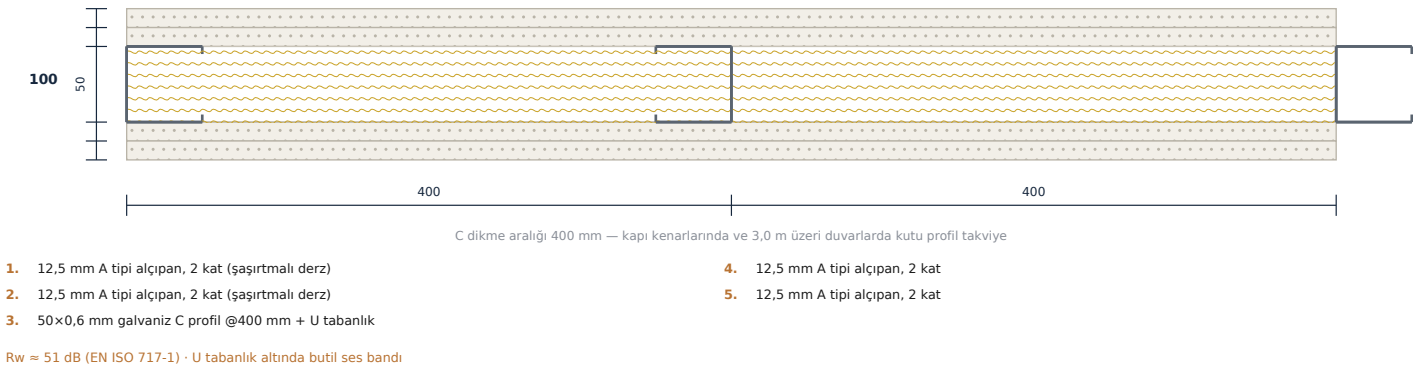


D3 · Alçıpan bölme — ıslak hacim yüzü

toplam 100 mm · ölçek 1/5

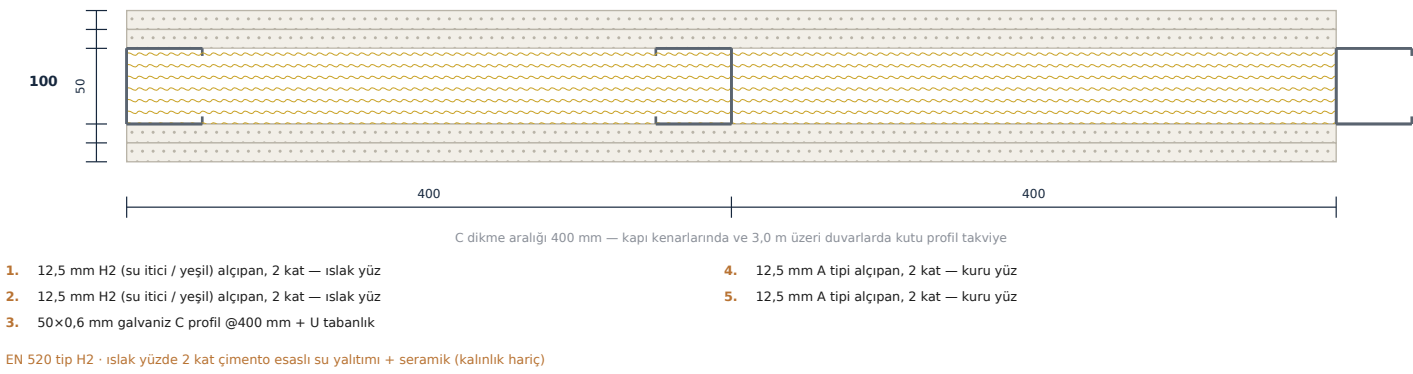


D4 · Akustik giydirme — arena çeperi

toplam 95 mm · ölçek 1/5

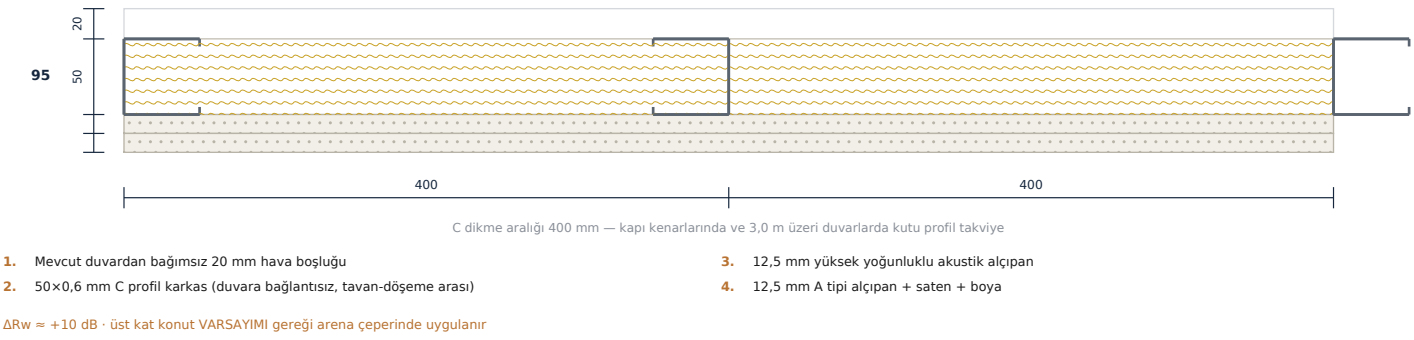

D6 · Ayna duvarı — arena güney çeperi (D1/D4 üzerine giydirme)

toplam 24 mm · ölçek 1/5

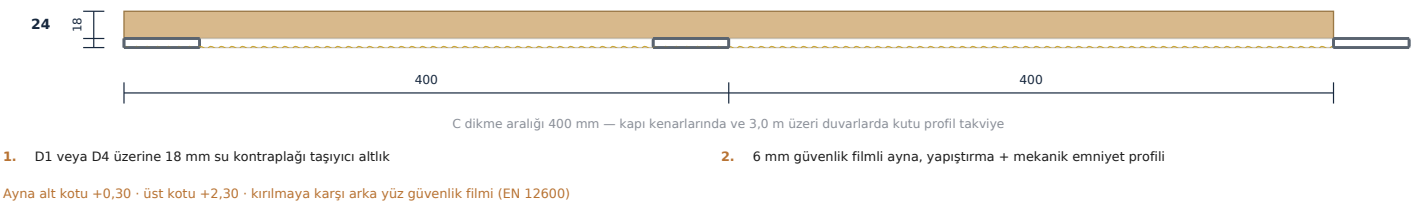

KARKAS METRAJİ — GEOMETRİDEN TÜRETİLMİŞTİR

TİP	EKSEN (M)	UZUNLUK (M)	C50 DİKME	ALAN (M²)
D2	(10,47, 8,75) → (8,33, 8,44)	2,17	6	6,93
D2	(8,33, 8,44) → (8,85, 4,78)	3,71	10	11,86
D2	(8,87, 4,65) → (9,47, 0,47)	4,22	11	13,52
D2	(9,47, 0,47) → (9,76, 0,71)	0,38	2	1,21
D3	(8,56, 6,82) → (10,70, 7,13)	2,17	6	6,94
D3	(9,40, 8,58) → (9,63, 6,98)	1,62	5	5,18
D3	(11,38, 2,40) → (9,23, 2,10)	2,17	6	6,93
D3	(10,38, 1,54) → (10,28, 2,25)	0,71	3	2,28
TOPLAM		17,14	49	54,85

İMALAT KURALLARI

- Taban ve tavan kanalı U50×40×0,6; taban kanalı altına butil ses bandı serilir, dübel aralığı en fazla 600 mm.
- C50×50×0,6 dikmeler @400 mm; dikme boyu, kat yüksekliğinden 10 mm kısa kesilir (yapısal hareket payı). Dikme kanalın içine oturtulur, kanala vidalanmaz.
- Kapı kenarlarında ve 3,00 m'den uzun duvarlarda iki C profil sırt sırta kutu profil olarak birleştirilir; kapı lentosu U profilden teşkil edilir.
- Alçıpan derzleri iki yüzde şaşırtmalı; ikinci kat, ilk kata göre 600 mm kaydırılır. Vida aralığı kenarda 200 mm, ortada 300 mm.
- Ağır asma yük (ayna, dolap, TV) için karkas içine 18 mm su kontrplağı takviye gömülür.
- Taşıyünü dolgu 40 mm / 50 kg/m³, dikmeler arasına sıkıştırılarak yerleştirilir; boşluk bırakılmaz.
- Islak hacim yüzünde 12,5 mm H2 (yeşil) alçıpan kullanılır; alt kenarı bitmiş zeminden 10 mm yukarda bırakılır ve su yalıtımı levha üzerine uygulanır.
- Tüm bölmeler asma tavan üstünden geçerek yapısal döşemeye (+3,20) kadar yükselir.