


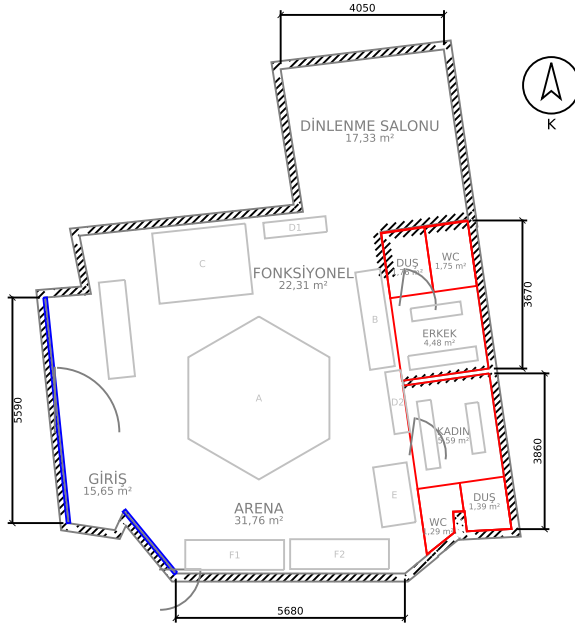

LEJANT

- Mimari — mevcut duvar (korunuyor)
 — Mimari — yeni alçıpan bölme

NOTLAR

Mimari altlık — mevcut duvar korunur.
 Kırmızı: yeni alçıpan bölme.
 Ölçüler raster paftadan (+/-%3).

PROJE

MALTEPE / İDEALTEPE — GYM DÖNÜŞÜMÜ

DISİPLİN
MİMARİ

PAFTA ADI
MİMARİ ALTLIK

PAFTA NO
A-01

TARİH
17 Eylül 2026

BİRİM
milimetre (mm)

Yerinde doğrulanmadan ve ruhsat alınmadan uygulama yapılamaz.

ÖLÇEK
1/75

REVİZYON
Rev F


DURUM
ÖN TASARIM

LEJANT

- Mimari — mevcut duvar (korunuyor)
— Mimari — yeni alçipan bölme

NOTLAR

Mahal no, kapı kodu, duvar tipi ve kesit hattı gösterilmiştir.
Tüm alçipan bölmeler yapısal doseme altına (+3,20) kadar yükselir.

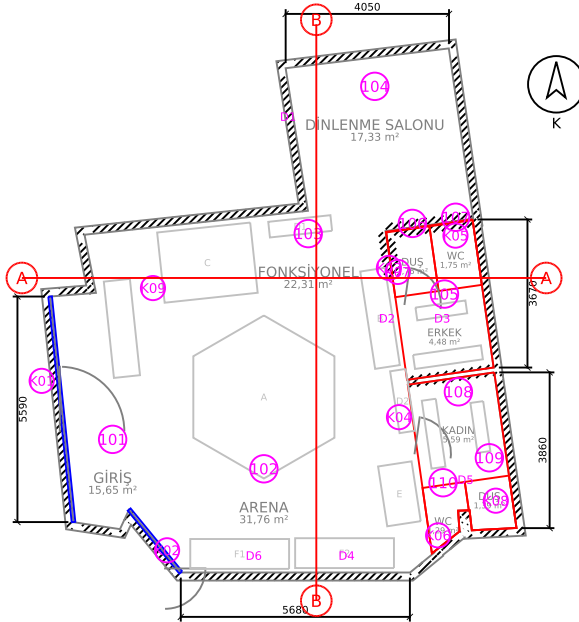

PROJE
MALTEPE / İDEALTEPE — GYM DÖNÜŞÜMÜ

DISİPLİN
MİMARİ

PAFTA ADI
MİMARİ UYGULAMA PLANI

PAFTA NO
A-02

ÖLÇEK
1/75

TARİH
17 Eylül 2026

REVİZYON
Rev F

BİRİM
milimetre (mm)

DURUM
ÖN TASARIM


Yerinde doğrulanmadan ve ruhsat alınmadan uygulama yapılamaz.

— Mimari — mevcut duvar (korunuyor)
— Mimari — yeni alçıpan bölme

Bitmiş zemin kotu tüm kuru hacimde
+/-0,00; duş ve WC -0,02.
Tesviye sapi kalınlıkları farklıdır
(Z1:3 Z2:30 Z3:42 Z5:38 mm).
Kaucuk karo derzi 1000x1000 mm.



PROJE MALTEPE / İDEALTEPE — GYM DÖNÜŞÜMÜ	
DISİPLİN MİMARİ	
PAFTA ADI ZEMİN KAPLAMA PLANI	
PAFTA NO A-03	ÖLÇEK 1 / 75
TARİH 17 Eylül 2026	REVİZYON Rev F
BİRİM milimetre (mm)	DURUM ÖN TASARIM
Yerinde doğrulanmadan ve ruhsat alınmadan uygulama yapılamaz.	

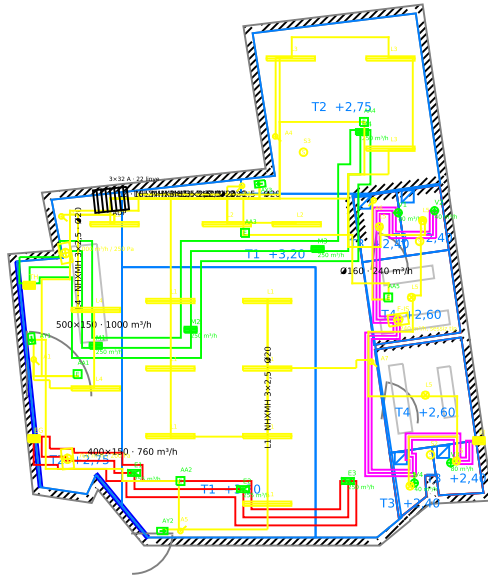

LEJANT

- Mimari — mevcut duvar (korunuyor)
- Mimari — yeni alçıpan bölme
- Mekanik — taze hava kanalı
- Mekanik — egzoz kanalı
- Mekanik — ıslak hacim egzoz kanalı
- Mekanik — menfez ve valf
- Mekanik — menfez bransmanı
- Mekanik — fan ve panjur
- Mekanik — etiket ve not
- Elektrik — lineer LED armatür
- Elektrik — IP44 downlight
- Elektrik — acil aydınlatma / yönlendirme
- Elektrik — anahtar ve sensör
- Elektrik — aydınlatma linyesi (ortogonal)
- Elektrik — anahtar kumanda sortisi
- Elektrik — ana dağıtım panosu
- Elektrik — etiket ve not

NOTLAR

T1 acık tavan +3,20 · T2 +2,75

T4 +2,60 · T3 +2,40.

Tesisat askisi alçıpan karkasına

asılmaz; ayrı askılanır.

Her ıslak hacimde 300x300 revizyon.

PROJE

MALTEPE / İDEALTEPE — GYM DÖNÜŞÜMÜ

DISİPLİN
MİMARİ

PAFTA ADI
TAVAN PLANI (RCP)

PAFTA NO
A-04

TARİH
17 Eylül 2026

BİRİM
milimetre (mm)

ÖLÇEK
1/75

REVİZYON
Rev F

DURUM
ÖN TASARIM


Yerinde doğrulanmadan ve ruhsat alınmadan uygulama yapılamaz.

LEJANT

- Mimari — mevcut duvar (korunuyor)
— Mimari — yeni alçipan bölme

NOTLAR

İki bağımsız çıkış: C1 1,60 m, C2 1,00 m.
En uzun kaçış yolu 13,4 m.
Kaçış kapıları kaçış yönünde açılır,
panik donanımlı, kilitsiz.

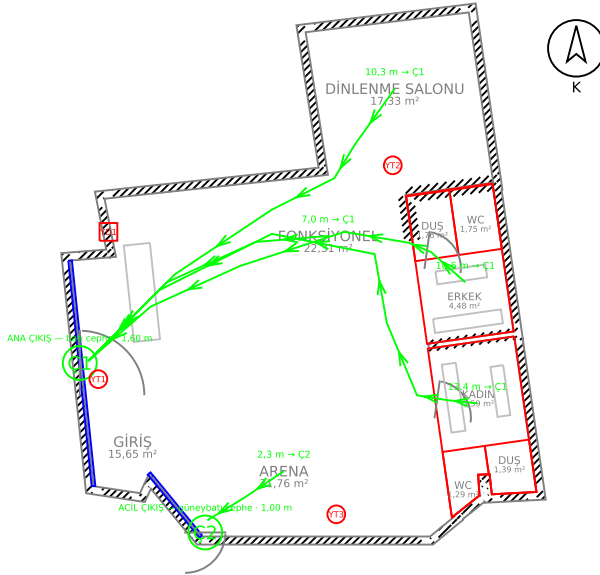

PROJE
MALTEPE / İDEALTEPE — GYM DÖNÜŞÜMÜ

DISİPLİN
MİMARİ

PAFTA ADI
YANGIN VE TAHLİYE PLANI

PAFTA NO
A-05

ÖLÇEK
1 / 75


TARİH
17 Eylül 2026

REVİZYON
Rev F

BİRİM
milimetre (mm)

DURUM
ÖN TASARIM

Yerinde doğrulanmadan ve ruhsat alınmadan uygulama yapılamaz.

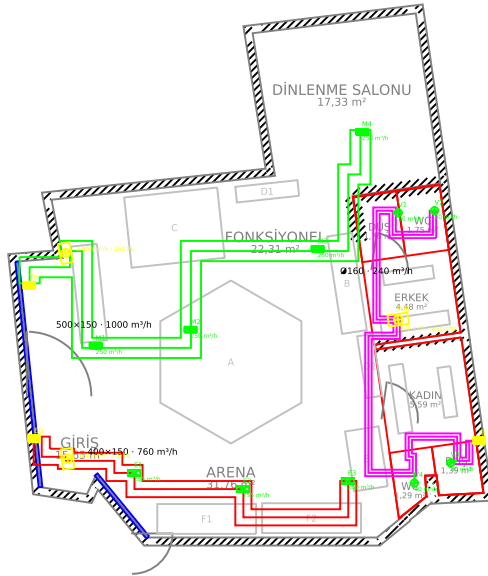

LEJANT

- Mimari — mevcut duvar (korunuyor)
- Mimari — yeni alçıpan bölme
- Mekanik — taze hava kanalı
- Mekanik — egzoz kanalı
- Mekanik — ıslak hacim egzoz kanalı
- Mekanik — menfez ve valf
- Mekanik — menfez bransmanı
- Mekanik — fan ve panjur
- Mekanik — etiket ve not

NOTLAR

Kanallar galvaniz sac, TS EN 1507 sınıf B.
Besleme ve egzoz hattı 19 mm izoleli.
Her bransman baskı debi ayar damperi.
Devreye almada balanslama ve ölçüm raporu.

PROJE

MALTEPE / İDEALTEPE — GYM DÖNÜŞÜMÜ

DISİPLİN

MEKANİK TESİSAT

PAFTA ADI
HAVALANDIRMA PLANI

PAFTA NO
M-01

ÖLÇEK
1/75

TARİH
17 Eylül 2026

REVİZYON
Rev F

BİRİM
milimetre (mm)

DURUM
ÖN TASARIM


Yerinde doğrulanmadan ve ruhsat alınmadan uygulama yapılamaz.

LEJANT

- Mimari — mevcut duvar (korunuyor)
- Mimari — yeni alçıpan bölme
- Mekanik — klima iç ünite
- Mekanik — klima dış ünite platformu
- Mekanik — soğutucu akışkan bakır hattı
- Mekanik — klima drenaj hattı

NOTLAR

İç ünite montaj kotu 2,40 m (alt kot).
Bakır hat izoleli, dış ünite konsolu
titresim takozlu.
Drenaj %1 eğimli.

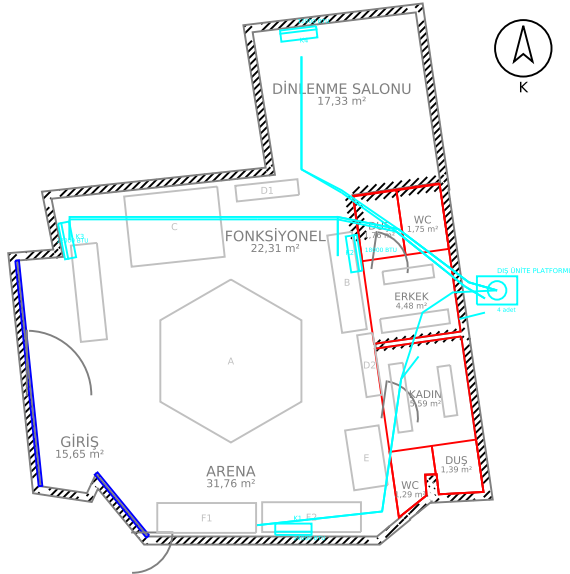

PROJE
MALTEPE / İDEALTEPE — GYM DÖNÜŞÜMÜ

DİSİPLİN
MEKANİK TESİSAT

PAFTA ADI
İKLİMLENDİRME PLANI

PAFTA NO
M-02

ÖLÇEK
1 / 75

TARİH
17 Eylül 2026

REVİZYON
Rev F

BİRİM
milimetre (mm)

DURUM
ÖN TASARIM

Yerinde doğrulanmadan ve ruhsat alınmadan uygulama yapılamaz.

LEJANT


- Mimari — mevcut duvar (korunuyor)
- Mimari — yeni alçıpan bölme
- Mekanik — temiz su PPRC
- Mekanik — sıcak su PPRC izoleli
- Mekanik — pis su PVC
- Mekanik — vitrifiye ve su ısıtıcı

NOTLAR

Pis su %2 eğimli.

Tüm ıslak hacimde sifonlu yer suzgeci.

SOKUM SONRASI İLK İS: mevcut pis su bağlantı kotunun ölçülmesi.

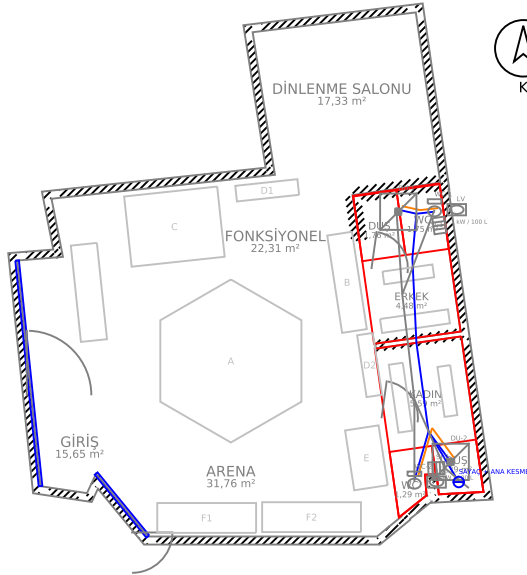

PROJE

MALTEPE / İDEALTEPE — GYM DÖNÜŞÜMÜ

DISİPLİN

MEKANİK TESİSAT

PAFTA ADI
SİHHİ TESİSAT PLANI

PAFTA NO
M-03

TARİH
17 Eylül 2026


BİRİM
milimetre (mm)

Yerinde doğrulanmadan ve ruhsat alınmadan uygulama yapılamaz.

ÖLÇEK
1 / 75

REVİZYON
Rev F

DURUM
ÖN TASARIM

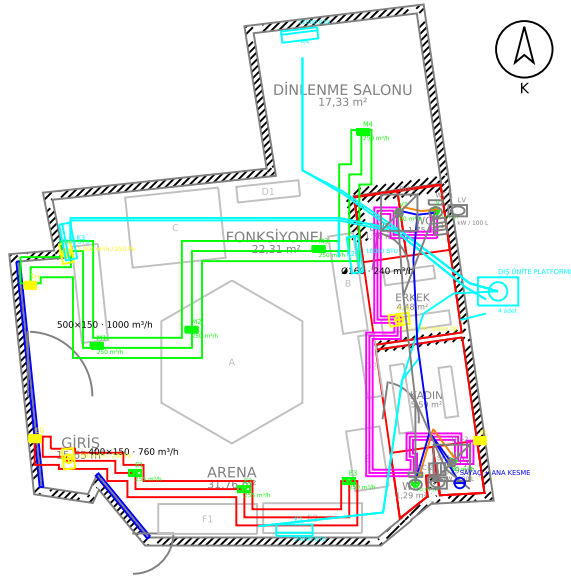

LEJANT

- Mimari — mevcut duvar (korunuyor)
- Mimari — yeni alçıpan bölme
- Mekanik — taze hava kanalı
- Mekanik — egzoz kanalı
- Mekanik — ıslak hacim egzoz kanalı
- Mekanik — menfez ve valf
- Mekanik — menfez bransmanı
- Mekanik — fan ve panjur
- Mekanik — klima iç ünite
- Mekanik — klima dış ünite platformu
- Mekanik — soğutucu akışkan bakır hattı
- Mekanik — klima drenaj hattı
- Mekanik — temiz su PPRC
- Mekanik — sıcak su PPRC izoleli
- Mekanik — pis su PVC
- Mekanik — vitrifiye ve su ısıtıcı
- Mekanik — etiket ve not

NOTLAR

Mekanik disiplin genel yerleşimi.

Ayrıntı için M-01, M-02, M-03 paftaları.

PROJE

MALTEPE / İDEALTEPE — GYM DÖNÜŞÜMÜ

DISİPLİN

MEKANİK TESİSAT

PAFTA ADI

MEKANİK GENEL YERLEŞİM

PAFTA NO
M-04

ÖLÇEK
1 / 75


TARİH
17 Eylül 2026

REVİZYON
Rev F

BİRİM
milimetre (mm)

DURUM
ÖN TASARIM

Yerinde doğrulanmadan ve ruhsat alınmadan uygulama yapılamaz.

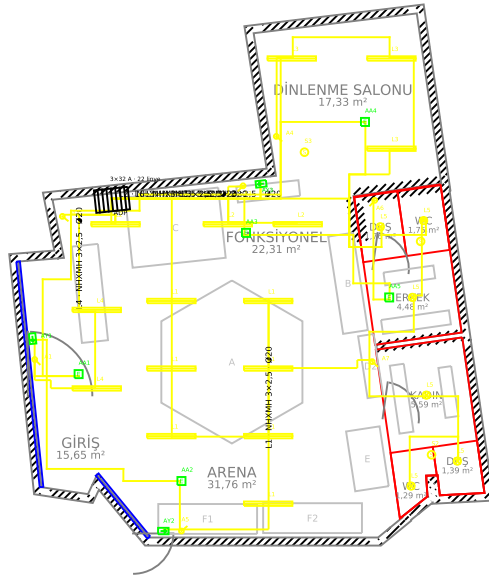

LEJANT

- Mimari — mevcut duvar (korunuyor)
- Mimari — yeni alçıpan bölme
- Elektrik — lineer LED armatür
- Elektrik — IP44 downlight
- Elektrik — acil aydınlatma / yönlendirme
- Elektrik — anahtar ve sensör
- Elektrik — aydınlatma lineesi (ortogonal)
- Elektrik — anahtar kumanda sortisi
- Elektrik — ana dağıtım panosu
- Elektrik — etiket ve not

NOTLAR

Tesisat siva altı spiral boru içinde,
NHXMH halojenizsiz kablo.
Acil aydınlatma 3 saat bataryalı.

PROJE

MALTEPE / İDEALTEPE — GYM DÖNÜŞÜMÜ

DISİPLİN
ELEKTRİK

PAFTA ADI
AYDINLATMA PLANI

PAFTA NO
E-01

TARİH
17 Eylül 2026


BİRİM
milimetre (mm)

Yerinde doğrulanmadan ve ruhsat alınmadan uygulama yapılamaz.

ÖLÇEK
1/75

REVİZYON
Rev F

DURUM
ÖN TASARIM

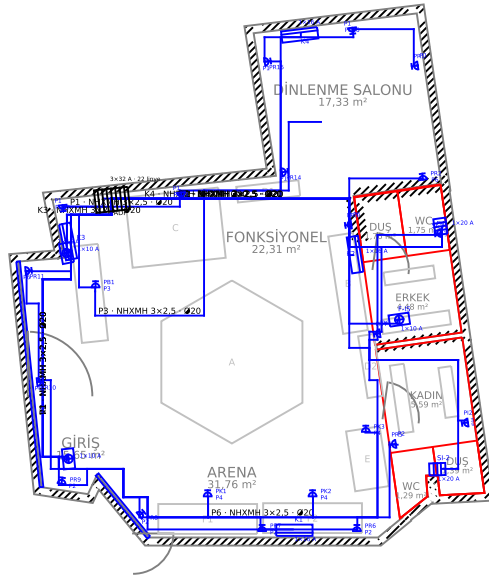

LEJANT

- Mimari — mevcut duvar (korunuyor)
- Mimari — yeni alçıpan bölme
- Elektrik — priz
- Elektrik — klima/sıtıcı/fan beslemesi
- Elektrik — priz ve kuvvet linyesi
- Elektrik — ana dağıtım panosu
- Elektrik — etiket ve not

NOTLAR

Islak hacim linyeleri ayrı 30 mA kaçak akım rolesinden beslenir.
Kardiyo ekipmanı ayrı linyede (P4).

PROJE

MALTEPE / İDEALTEPE — GYM DÖNÜŞÜMÜ

DISİPLİN
ELEKTRİK

PAFTA ADI
PRİZ VE KUVVET PLANI

PAFTA NO
E-02

ÖLÇEK
1 / 75


TARİH
17 Eylül 2026

REVİZYON
Rev F

BİRİM
milimetre (mm)

DURUM
ÖN TASARIM

Yerinde doğrulanmadan ve ruhsat alınmadan uygulama yapılamaz.

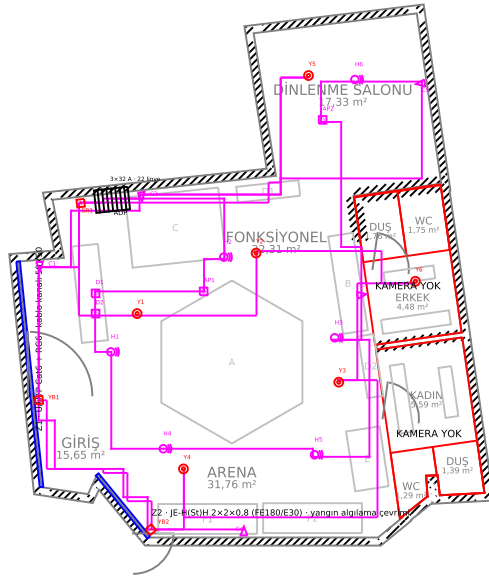

LEJANT

- Mimari — mevcut duvar (korunuyor)
- Mimari — yeni alçıpan bölme
- Elektrik — IP kamera
- Elektrik — tavan hoparlörü
- Elektrik — veri prizi ve rack
- Elektrik — dedektör, buton, siren
- Elektrik — yangın algılama çevrimi
- Elektrik — zayıf akım kablo kanalı
- Elektrik — ana dağıtım panosu
- Elektrik — etiket ve not

NOTLAR

SOYUNMA VE WC İÇİNE KAMERA KONULMAZ.
Yangın algılama panosu kesintisiz beslenir.
Topraklama direnci ≤ 10 ohm.

PROJE

MALTEPE / İDEALTEPE — GYM DÖNÜŞÜMÜ

DİSİPLİN
ELEKTRİK

PAFTA ADI
ZAYIF AKIM PLANI

PAFTA NO
E-03

TARİH
17 Eylül 2026

BİRİM
milimetre (mm)

Yerinde doğrulanmadan ve ruhsat alınmadan uygulama yapılamaz.

ÖLÇEK
1/75

REVİZYON
Rev F

DURUM
ÖN TASARIM



PROJE MALTEPE / İDEALTEPE — GYM DÖNÜŞÜMÜ	
DİSİPLİN ELEKTRİK	
PAFTA ADI ELEKTRİK GENEL YERLEŞİM	
PAFTA NO E-04	ÖLÇEK 1 / 75
TARİH 17 Eylül 2026	REVİZYON Rev F
BİRİM milimetre (mm)	DURUM ÖN TASARIM
Yerinde doğrulanmadan ve ruhsat alınmadan uygulama yapılamaz.	

