

Bu set, Maltepe / İdealtepe'deki mobilya mağazasının fonksiyonel antrenman stüdyosuna dönüşümü için MİMARİ UYGULAMA PROJESİDİR. Net iç kullanım alanı 103,78 m², 10 mahal. Set; yıkım, uygulama planı, zemin kaplama, tavan planı, iki kesit, dört iç görünüş, mahal listesi, kapı-pencere listesi, duvar tipleri, sekiz imalat detayı ve yangın-tahliye planından oluşur. Mekanik (M-01...M-06) ve elektrik (E-01...E-06) paftaları ayrı dosyalardadır ve bu setle aynı geometrik altlığı kullanır. Bu set müteahhidin imalat yapabilmesi için gereken malzeme, katman ve kot bilgisini taşır; ruhsat başvurusu için proje müellifi mimar tarafından imzalanmış 1/50 takım ayrıca düzenlenecektir.

## NET İÇ ALAN

103,78 m²

10 mahal · duvar payı 0,47 m²

## ZEMİN KAPLAMA TİPİ

6 tip

Z1–Z6 · bitmiş kot ±0,00 (ıslak –0,02)

## DUVAR / TAVAN TİPİ

6 + 4

D1–D6 · T1–T4

## KAPI · PENCERE

9 + 2

K01–K09 · P01–P02

## GENEL NOTLAR — UYGULAMADA BAĞLAYICIDIR


- 01** Tüm ölçüler metre (m), kaplama katman kalınlıkları milimetre (mm) cinsindendir. Ölçü okunur, çizimden ölçü alınmaz.
- 02** ±0,00 kotu bitmiş zemin kotudur. Mevcut şap üst kotu –0,053 VARSAYILMIŞTIR; söküm sonrası yerinde ölçülüp tüm tesviye şapı kalınlıkları revize edilecektir.
- 03** Taşıyıcı sistemde (kolon, perde, kiriş, döşeme) hiçbir kesme, delme veya yük artışı yapılmayacaktır. Gerekli hâllerde statik proje müellifinden yazılı görüş alınacaktır.
- 04** Mevcut duvar kalınlıkları ve tavan yüksekliği VARSAYIMDIR; rölöve sonrası mahal listesi ve tavan kotları güncellenecektir.
- 05** Alçıpan imalatlarda profil aralığı 400 mm'yi geçmeyecek; 3,0 m üzeri duvarlarda ve kapı kenarlarında kutu profil takviyesi yapılacaktır.
- 06** Islak hacimlerde su yalıtımı EN 14891'e uygun, çimento esaslı 2 bileşenli, 2 kat; tüm köşe ve boru geçişlerinde bant ve manşet kullanılacaktır.
- 07** Islak hacim imalatı bitiminde, seramik öncesi 24 saatlik su tutma (taşkın) testi yapılacak ve tutanağa bağlanacaktır.
- 08** Kauçuk zemin, üst kat konut VARSAYIMI nedeniyle titreşim matı ile yüzer döşeme olarak teşkil edilecektir; mat duvara 50 mm yukarı dönecektir.
- 09** Tüm cam yüzeylerde (kapı, ayna, vitrin) temperli veya lamine güvenlik camı kullanılacaktır (EN 12600).
- 10** Kaçış kapıları kaçış yönünde açılacak, üzerinde kilit veya sürgü bulunmayacak, panik donanımlı olacaktır (EN 1125).
- 11** Asma tavan üstündeki mekanik ve elektrik tesisatı bağımsız askılanacak; ağırlık alçıpan karkasına aktarılmayacaktır.
- 12** Boya, seramik ve kauçuk renk/desen seçimleri numune onayına tabidir; onaysız imalat bedeli yükleniciye aittir.
- 13** Bu set mimari uygulama setidir; ruhsat için proje müellifi mimar tarafından imzalanmış 1/50 onaylı takım ayrıca düzenlenecektir.

## PAFTA İNDEKSİ

| PAFTA | İÇERİK                                         | ÖLÇEK |
|-------|------------------------------------------------|-------|
| A-01  | Kapak · genel notlar · pafta indeksi           | —     |
| A-02  | Mevcut durum ve yıkım / söküm planı            | 1/75  |
| A-03  | Uygulama planı — bölme, kapı, mahal            | 1/75  |
| A-04  | Zemin kaplama planı                            | 1/75  |
| A-05  | Tavan planı (RCP) ve tesisat koordinasyonu     | 1/75  |
| A-06  | Kesit A-A                                      | 1/50  |
| A-07  | Kesit B-B                                      | 1/50  |
| A-08  | İç görünüşler G-01 ... G-04                    | 1/50  |
| A-09  | Mahal listesi — kaplama ve bitiş               | —     |
| A-10  | Kapı ve pencere listesi · duvar tipleri        | —     |
| A-11  | İmalat detayları I — zemin ve kot geçişi       | 1/10  |
| A-12  | İmalat detayları II — ıslak hacim, tavan, ayna | 1/10  |
| A-13  | Yangın ve tahliye planı                        | 1/75  |

## MAHAL ÖZETİ

| NO  | MAHAL                       | M²     | ZEMİN | TAVAN | KOT  |
|-----|-----------------------------|--------|-------|-------|------|
| 101 | GİRİŞ · BANKO · SİRKÜLASYON | 15,65  | Z3    | T2    | 2,75 |
| 102 | ARENA · SERBEST AĞIRLIK     | 31,76  | Z1    | T1    | 3,20 |
| 103 | FONKSİYONEL · KARDİYO       | 22,31  | Z2    | T1    | 3,20 |
| 104 | DİNLENME SALONU             | 17,33  | Z3    | T2    | 2,75 |
| 105 | ERKEK SOYUNMA               | 4,48   | Z5    | T4    | 2,60 |
| 106 | ERKEK DUŞ                   | 1,76   | Z4    | T3    | 2,40 |
| 107 | ERKEK WC                    | 1,75   | Z4    | T3    | 2,40 |
| 108 | KADIN SOYUNMA               | 5,59   | Z5    | T4    | 2,60 |
| 109 | KADIN DUŞ                   | 1,39   | Z4    | T3    | 2,40 |
| 110 | KADIN WC                    | 1,29   | Z4    | T3    | 2,40 |
|     | TOPLAM (NET)                | 103,31 |       |       |      |

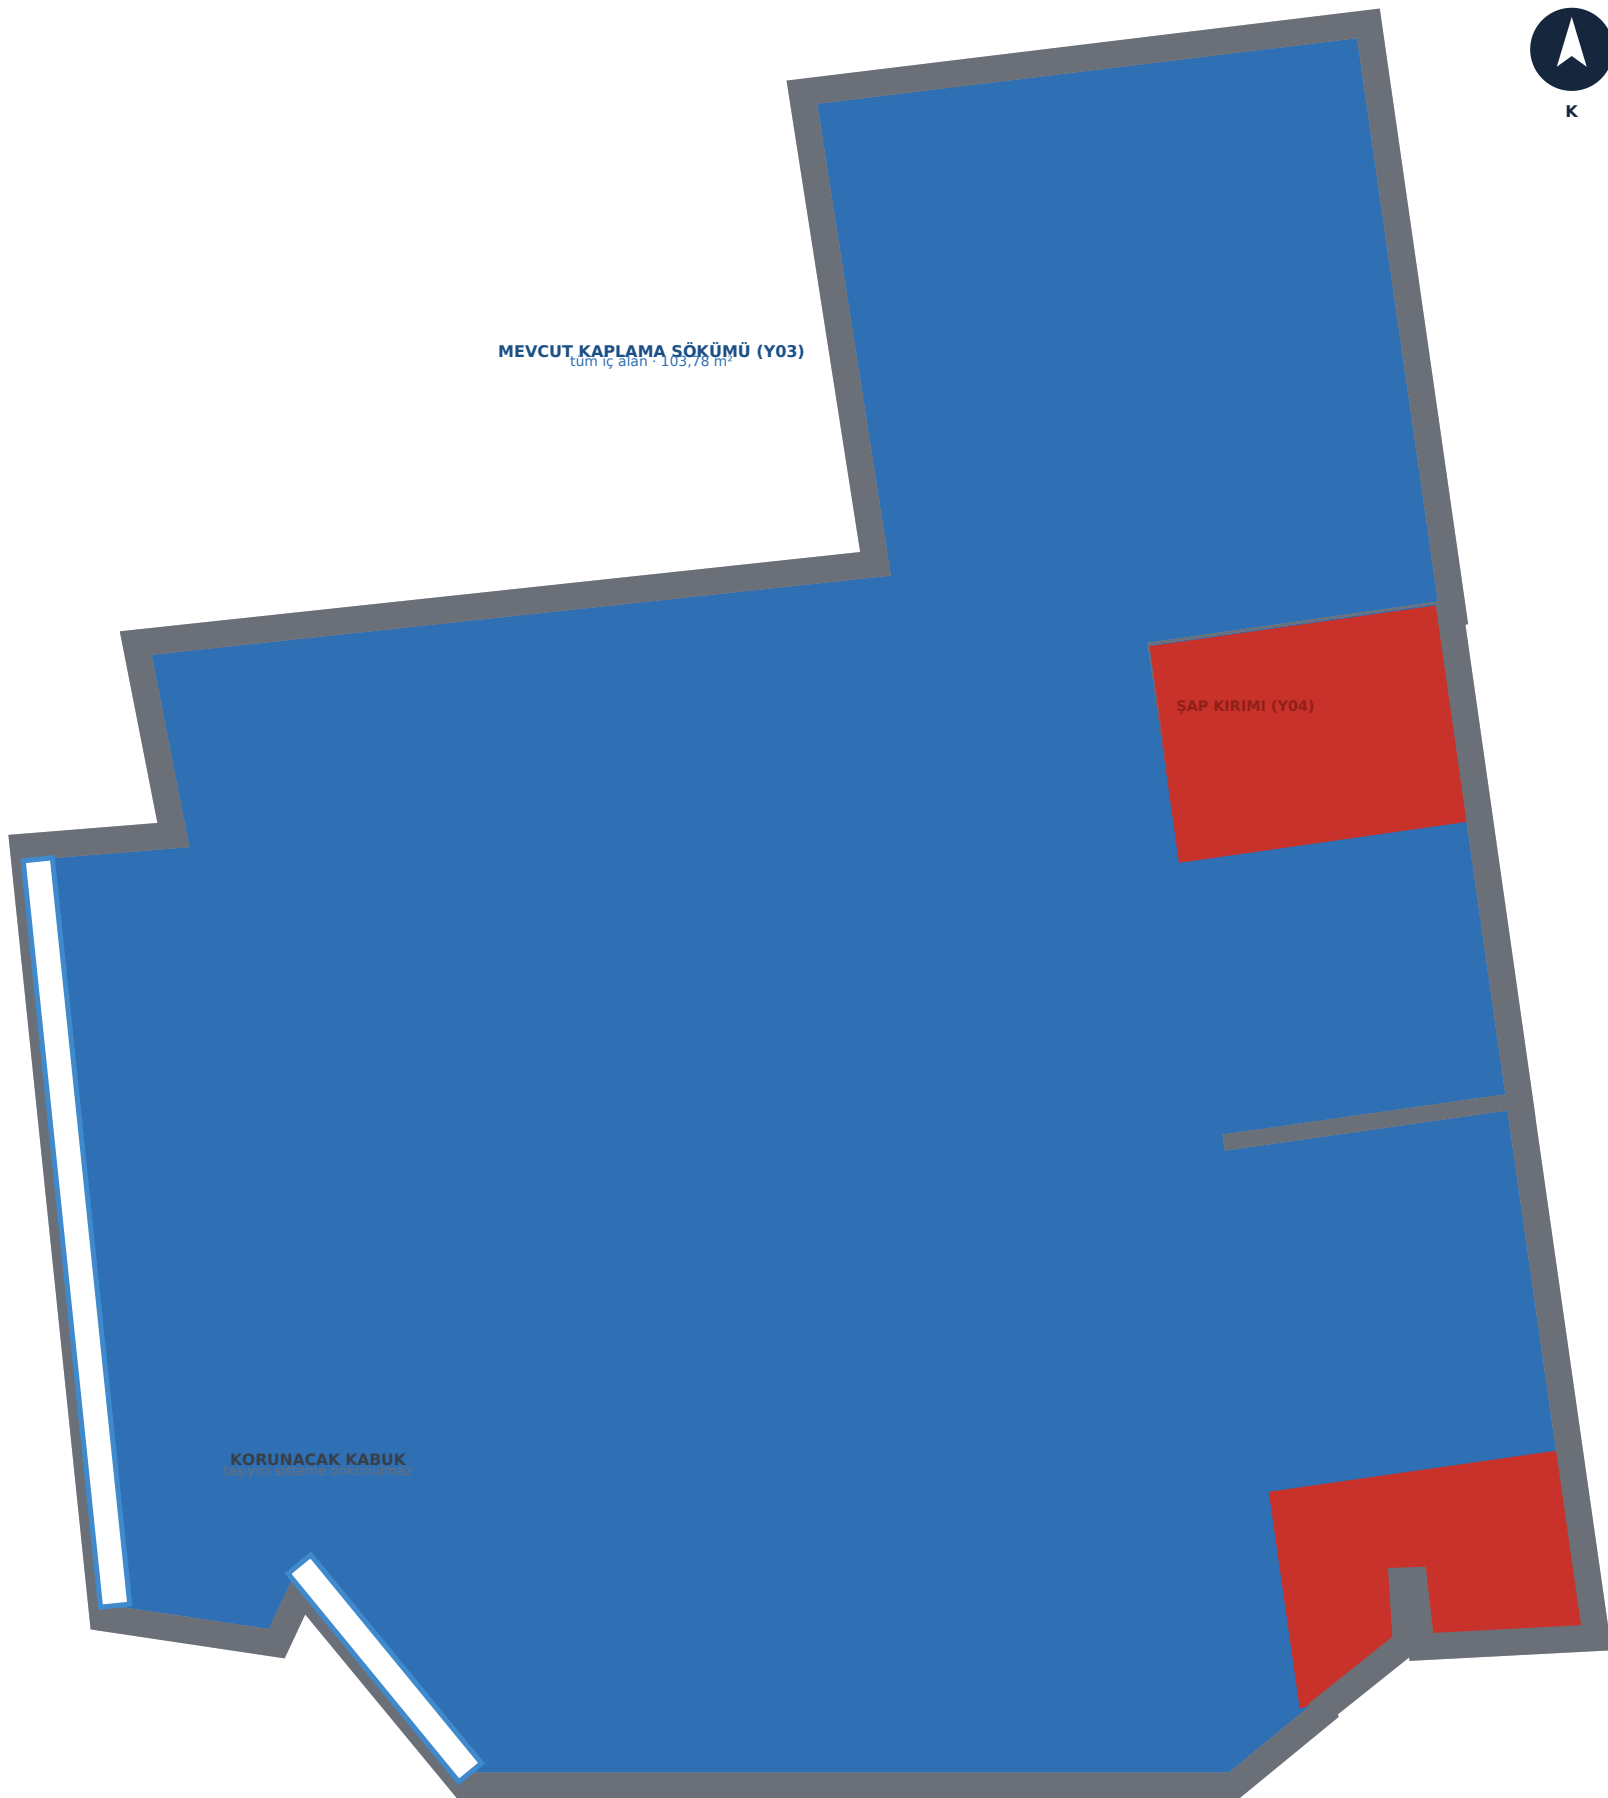

K

|       |                                 |
|-------|---------------------------------|
| Pafta | A-02                            |
| Ölçek | 1/75 (A3)                       |
| Tarih | 17 Eylül 2026                   |
| Durum | Uygulama — yerinde doğrulanacak |

## MİMARİ UYGULAMA PROJESİ

Rev E

## YIKIM VE SÖKÜM İŞ KALEMLERİ


| KOD | TANIM                                                                     | METRAJ    |
|-----|---------------------------------------------------------------------------|-----------|
| Y01 | Mevcut mağaza rafı, teşhir ünitesi ve mobilyanın sökülüp taşınması        | 1 komple  |
| Y02 | Mevcut asma tavan ve aydınlatma armatürlerinin sökümü                     | 103,78 m² |
| Y03 | Mevcut zemin kaplamasının (laminat / seramik) sökümü, altlık temizliği    | 103,78 m² |
| Y04 | Islak hacim alanında mevcut şap kırımı (tesisat boşluğu için, ort. 70 mm) | 16,73 m²  |
| Y05 | Mevcut sıva üstü elektrik tesisatı ve tablosunun sökümü                   | 1 komple  |
| Y06 | Mevcut ıslak hacim (varsa) armatür ve duvar seramiği sökümü               | 16,73 m²  |
| Y07 | Yeni kapı boşluklarının açılması, lento teşkili                           | 2 adet    |
| Y08 | Moloz çuvallama, yatay-düşey taşıma ve belediye döküm sahasına nakli      | 14 m³     |

## SÖKÜM ÖNCESİ ZORUNLU ADIMLAR

Mevcutta iç bölme duvarı bulunmadığı, mekânın tek hacim mağaza olduğu VARSAYILMIŞTIR. Söküm öncesi mevcut durum rölövesi alınacak; taşıyıcı sistemde hiçbir elemana dokunulmayacaktır. Kolon, perde ve döşeme kirişlerinde kesme/delme yasaktır.

## SIRALAMA

1) Enerji ve su kesilir, mevcut sayaç okuması tutanaklanır. 2) Mevcut durum rölövesi ve fotoğraf kaydı alınır. 3) Devralınacak mobilya ayrılır. 4) Asma tavan ve aydınlatma sökülür. 5) Zemin kaplaması sökülür, şap kotu ölçülür — bu ölçüm tüm tesviye şapı kalınlıklarının girdisidir. 6) Islak hacim şap kırımı ve pis su kotu tespiti yapılır; Seçenek A/B kararı burada verilir. 7) Moloz aynı gün tahliye edilir; kat sahanlığı ve asansör korunur.

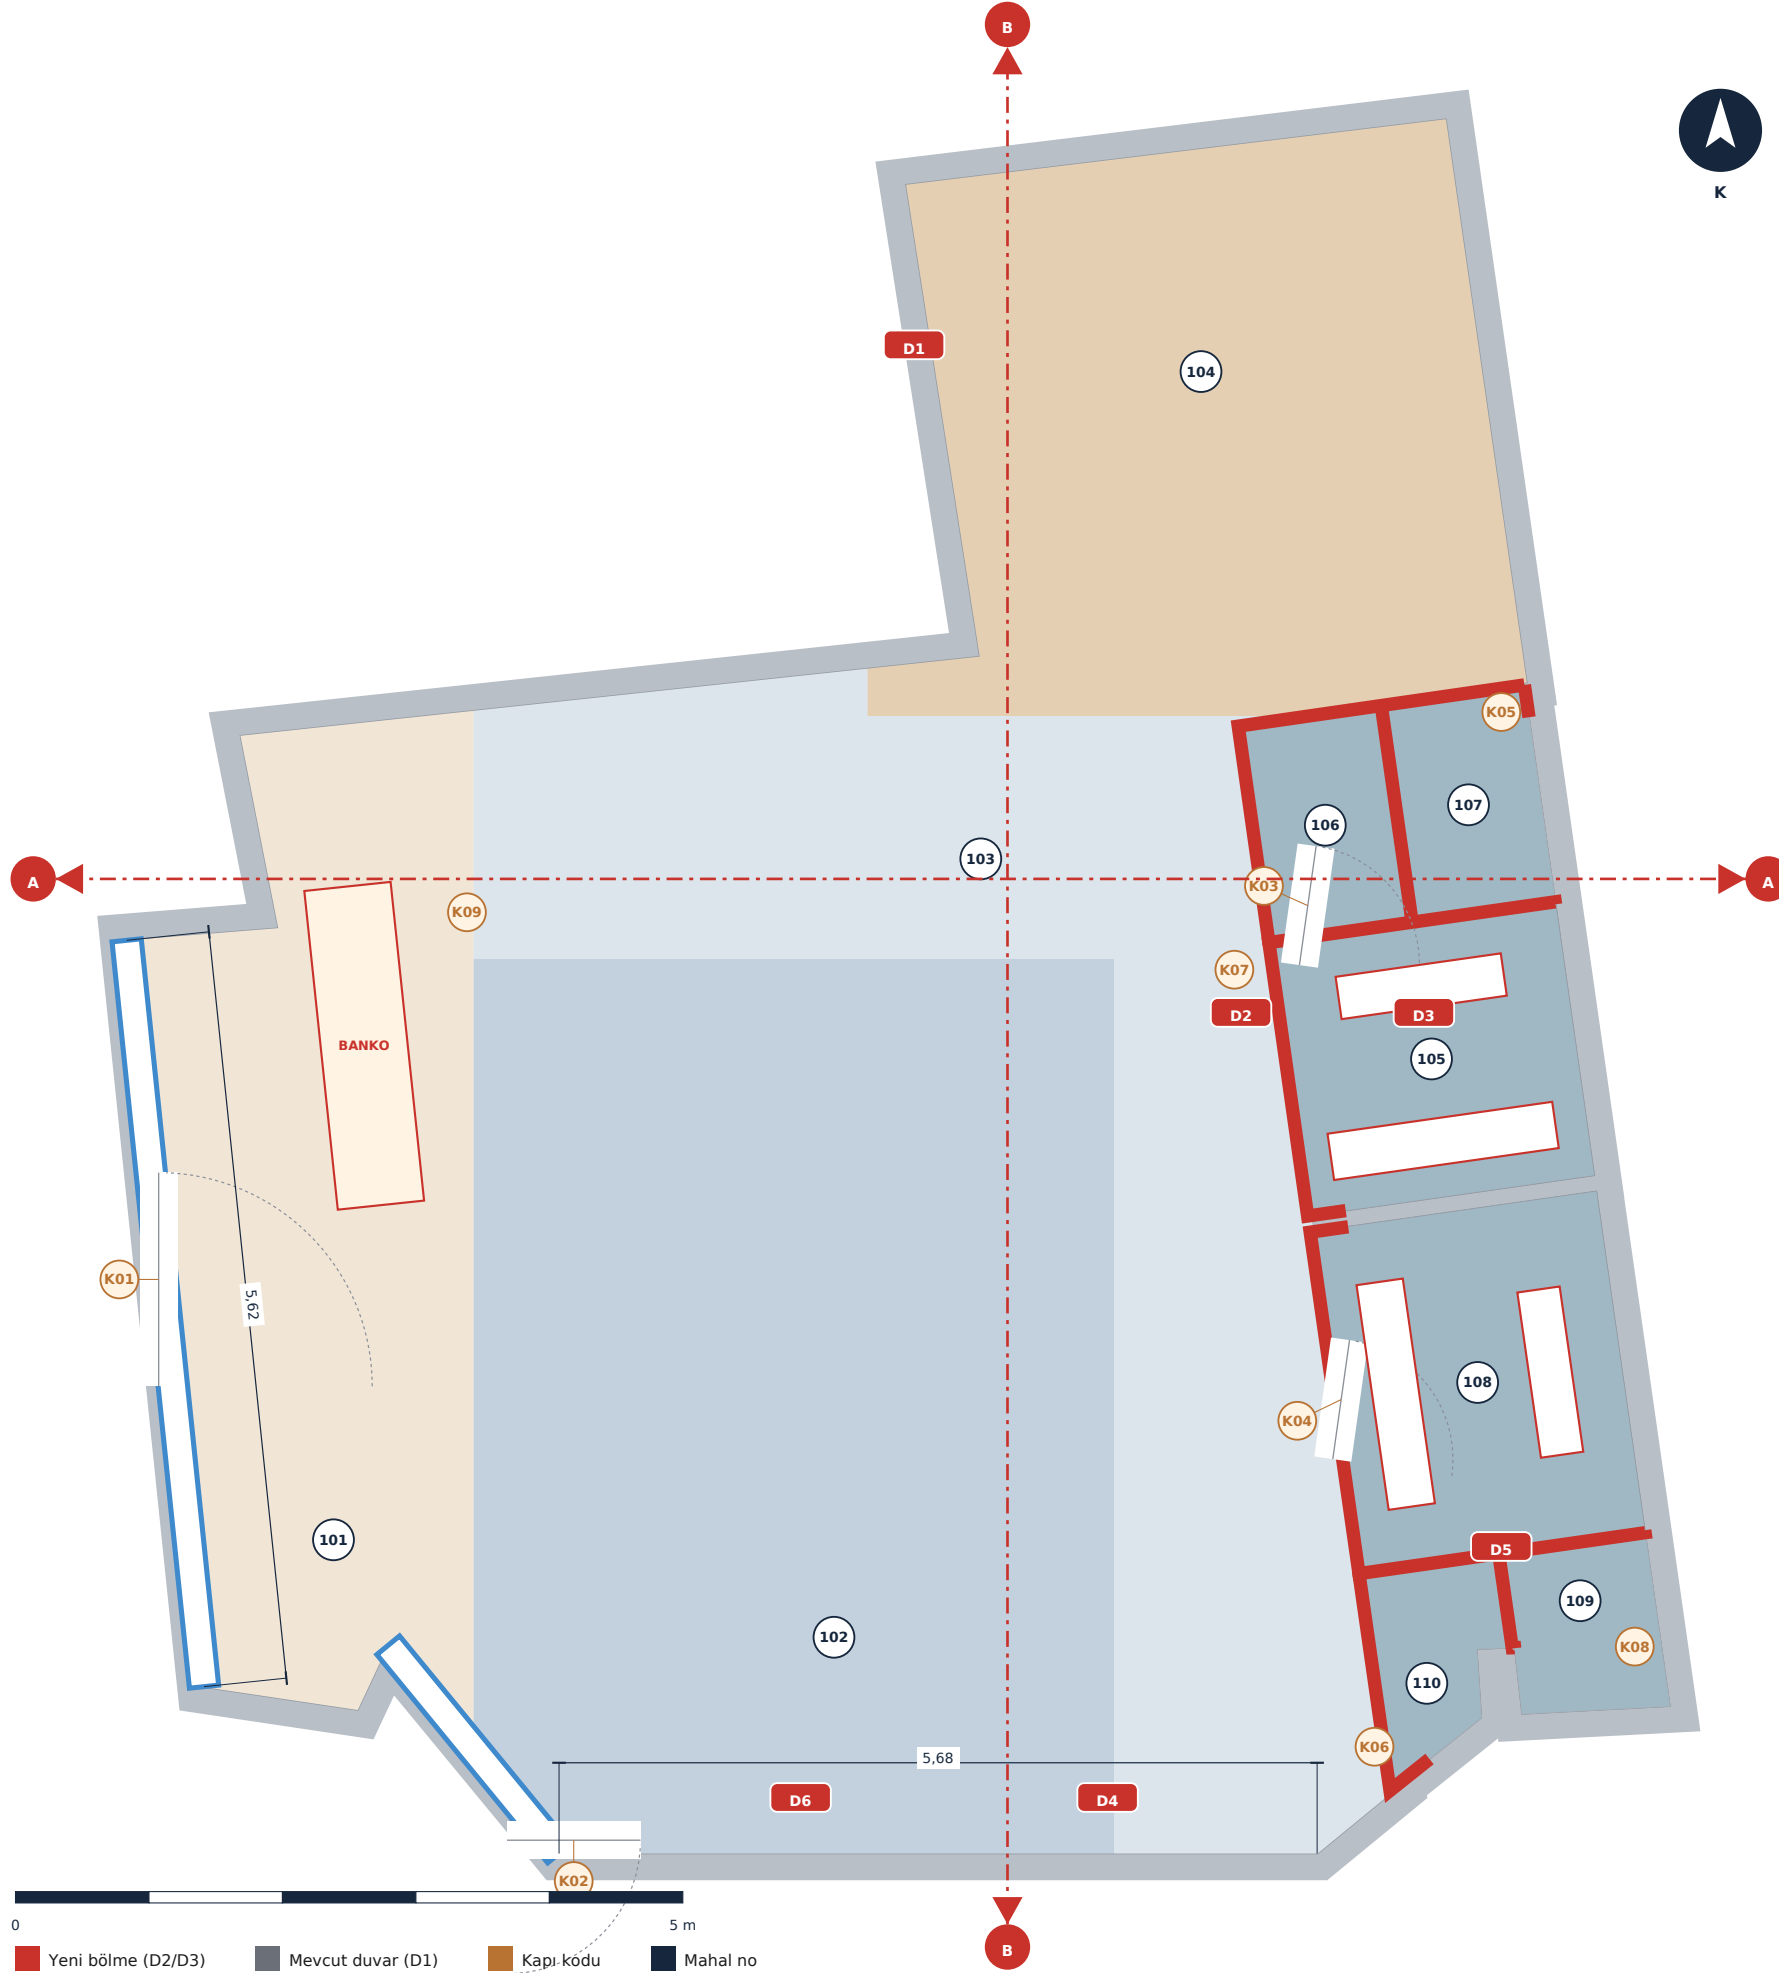

|       |                                 |
|-------|---------------------------------|
| Pafta | A-03                            |
| Ölçek | 1/75 (A3)                       |
| Tarih | 17 Eylül 2026                   |
| Durum | Uygulama — yerinde doğrulanacak |

## MİMARİ UYGULAMA PROJESİ

Rev E

## KOT ŞEMASI


| KOT    | TANIM                                               | NOT                                       |
|--------|-----------------------------------------------------|-------------------------------------------|
| ±0,00  | Bitmiş zemin kotu — tüm kuru hacimler               | Referans                                  |
| -0,02  | Duş ve WC bitmiş zemin kotu                         | Su taşkını kontrolü · eşik profili        |
| -0,053 | Mevcut şap üst kotu (VARSAYIM)                      | Tesviye şapı bu farkı kapatır             |
| +2,40  | T3 Alçıpan asma tavan — mahal 106 · 107 · 109 · 110 | 800 mm tesisat boşluğu · serbestlik 30 mm |
| +2,60  | T4 Alçıpan asma tavan — mahal 105 · 108             | 600 mm tesisat boşluğu · serbestlik 50 mm |
| +2,75  | T2 Alçıpan asma tavan — mahal 101 · 104             | 450 mm tesisat boşluğu · serbestlik 30 mm |
| +3,20  | T1 Açık (endüstriyel) tavan — mahal 102 · 103       | Yapısal döşeme altı (VARSAYIM)            |

## BÖLME DUVAR METRAJİ

| TİP | TANIM                                 | KALINLIK | METRAJ                                 |
|-----|---------------------------------------|----------|----------------------------------------|
| D2  | Alçıpan bölme — kuru hacim            | 100 mm   | ≈ 14,6 m <sup>2</sup> (VARSAYIM)       |
| D3  | Alçıpan bölme — ıslak yüz             | 100 mm   | ≈ 21,4 m <sup>2</sup> (VARSAYIM)       |
| D4  | Akustik giydirme — arena güney çeperi | 95 mm    | ≈ 18,2 m <sup>2</sup>                  |
| D5  | Seramik kaplı duvar — ıslak           | 216 mm   | ≈ 46,2 m <sup>2</sup>                  |
| D6  | Ayna duvarı — arena güney çeperi      | 212 mm   | ≈ 9,6 m <sup>2</sup> (4,80 m × 2,00 m) |

## BÖLME YÜKSEKLİĞİ

Tüm alçıpan bölmeler asma tavan üstünden geçerek yapısal döşemeye kadar (+3,20) yükseltilecektir. Asma tavan hizasında kesilen bölme, ıslak hacim kokusunu ve soyunma mahremiyetini koruyamaz; akustik performans ( $R_w \approx 51$  dB) da yalnızca tam yükseklikte geçerlidir.

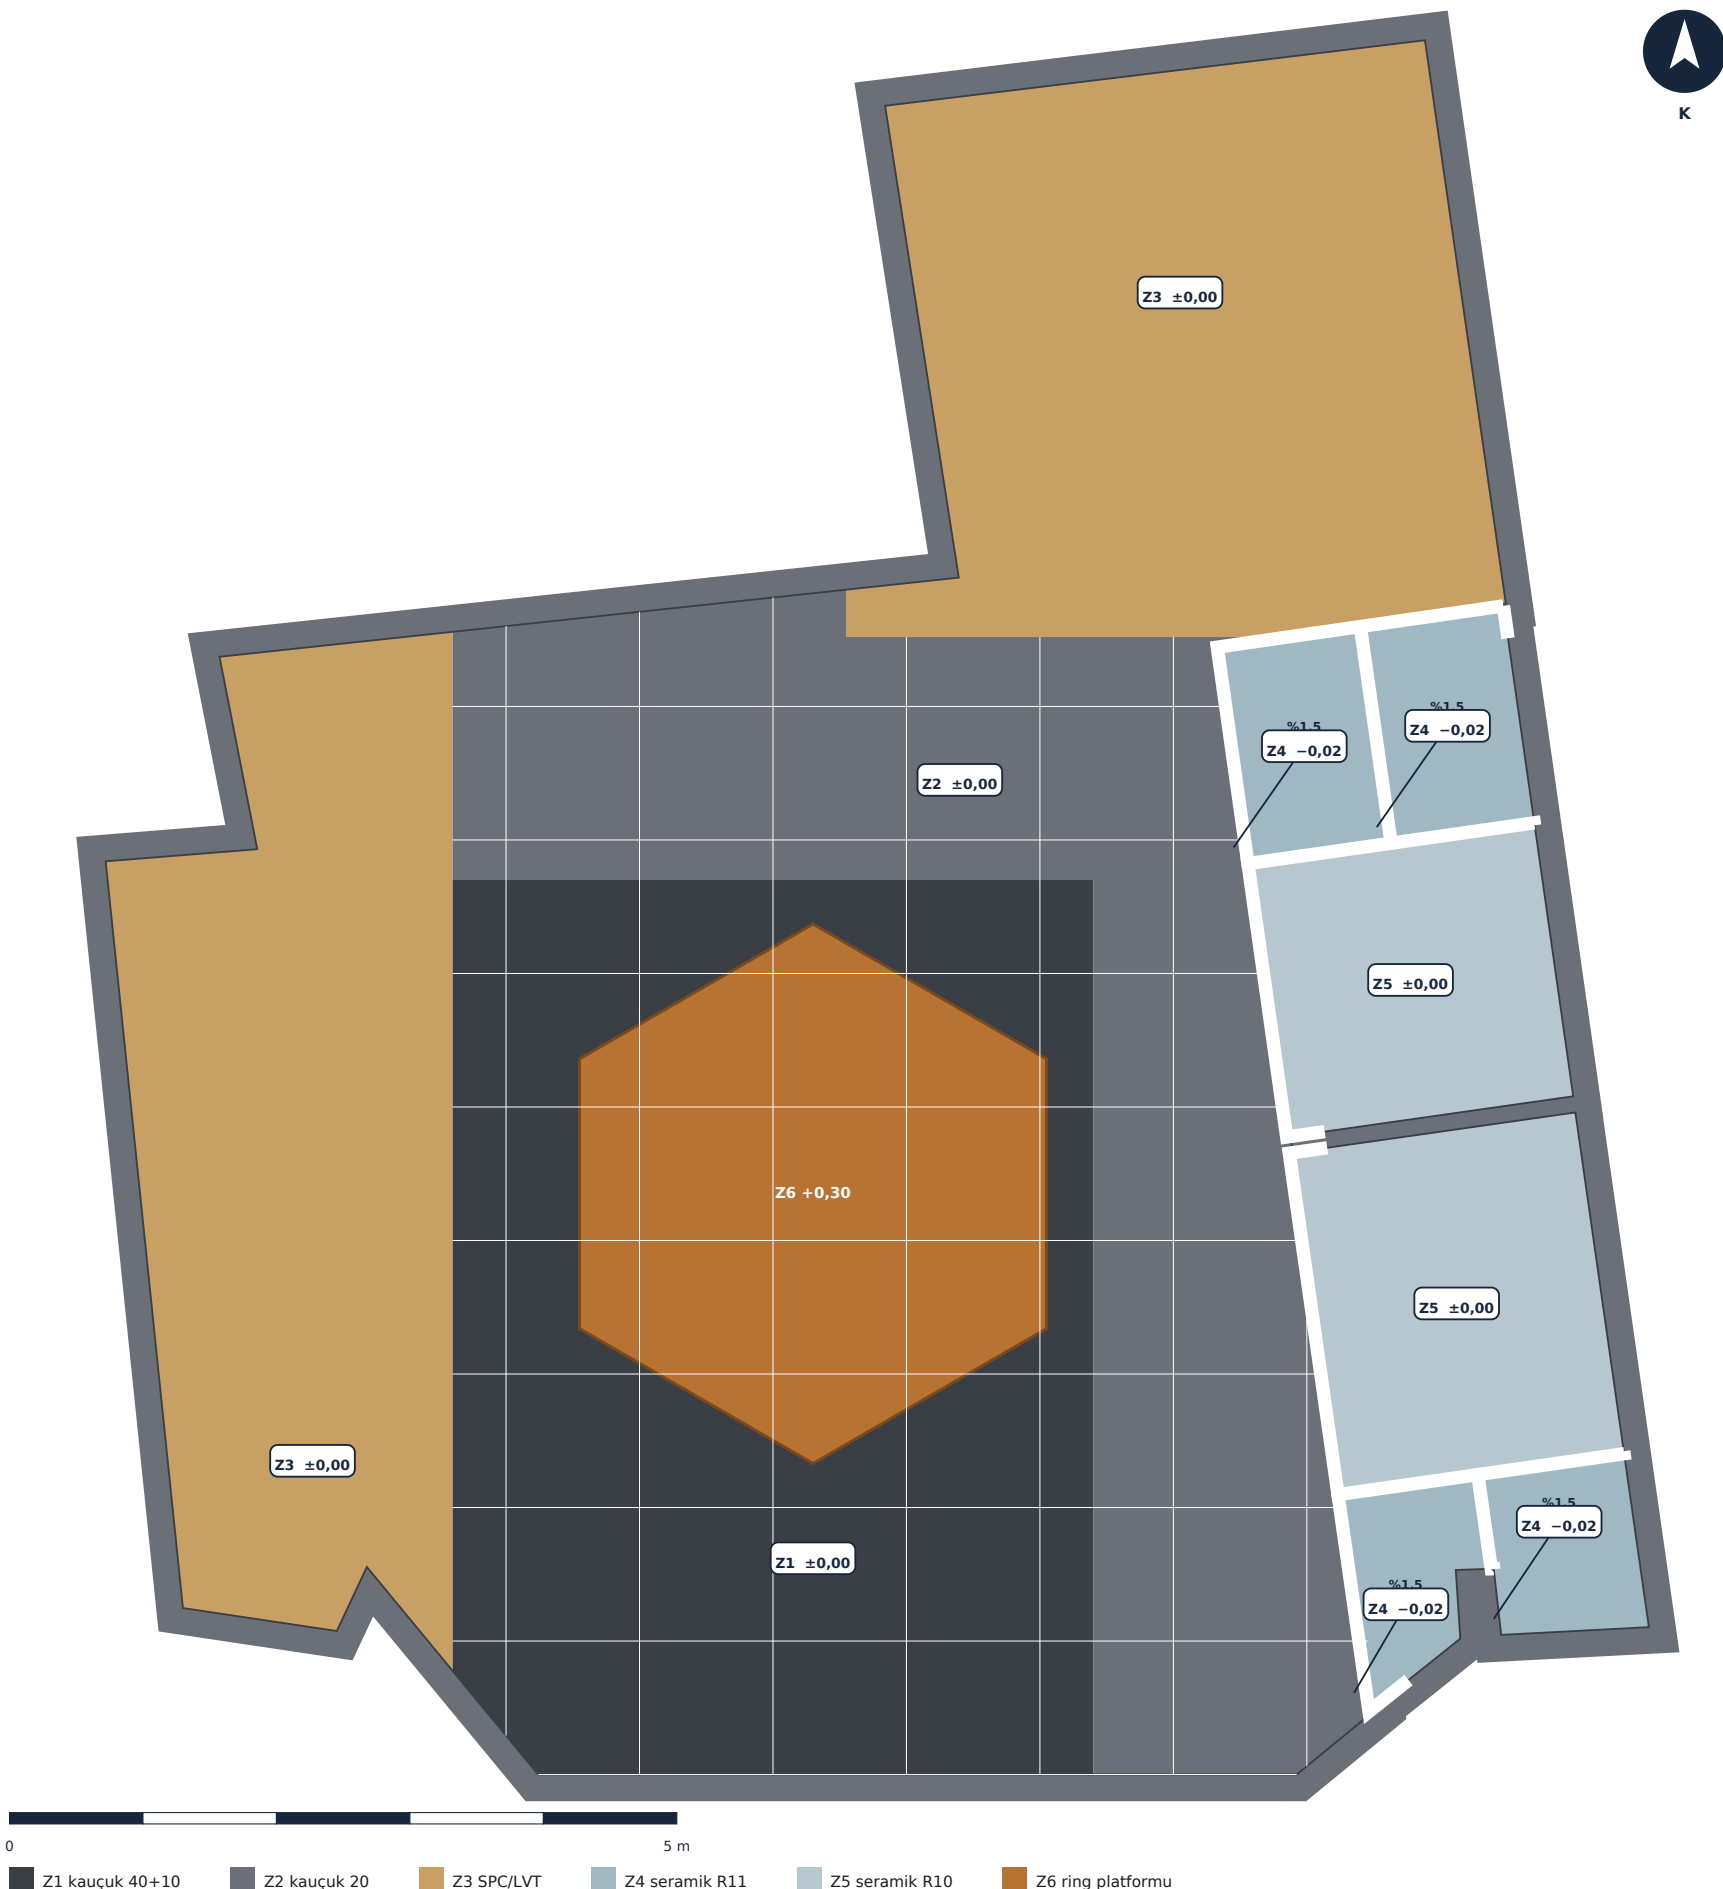

|       |                                 |
|-------|---------------------------------|
| Pafta | A-04                            |
| Ölçek | 1/75 (A3)                       |
| Tarih | 17 Eylül 2026                   |
| Durum | Uygulama — yerinde doğrulanacak |

## MİMARİ UYGULAMA PROJESİ

Rev E

## ZEMİN KAPLAMA TİPLERİ

| TİP | MAHAL / KAPLAMA                 | TOPLAM | BİTMİŞ KOT |
|-----|---------------------------------|--------|------------|
| Z1  | Arena · serbest ağırlık         | 53 mm  | ±0,00      |
| Z2  | Fonksiyonel · kardiyo           | 53 mm  | ±0,00      |
| Z3  | Giriş · banko · dinlenme        | 53 mm  | ±0,00      |
| Z4  | Duş · WC                        | 55 mm  | −0,02      |
| Z5  | Soyunma                         | 53 mm  | ±0,00      |
| Z6  | Ring platformu (ekipmana bağlı) | 300 mm | +0,30      |

## PERFORMANS ŞARTI

- Z1** EN 14041 · yangın Bfl-s1 · EN ISO 10140  $\Delta Lw \geq 18$  dB · serbest ağırlık düşürmeye uygun
- Z2** EN 14041 · Bfl-s1 · kardiyo cihazı nokta yükü  $\geq 4$  kN/m<sup>2</sup>
- Z3** EN ISO 10874 aşınma sınıfı 33 / AC5 · EN 14041 Bfl-s1 · kaymazlık DS
- Z4** EN 14891 su yalıtımı · EN 16165 Ek B (R11) · Ek A (B sınıfı ıslak ayak)
- Z5** EN 16165 Ek B (R10) · EN 14411 Bla · rektifiye, 2 mm derz

## SÜPÜRGELİK

| KOD | TANIM                                                                              | MAHAL                 |
|-----|------------------------------------------------------------------------------------|-----------------------|
| S1  | Kauçuk süpürgelik 100×8 mm — zemin kaplamasıyla aynı malzeme, üst kenarı 45° pahlı | 102 · 103             |
| S2  | MDF lake süpürgelik 80×16 mm — RAL 9003, akrilik mastik ile duvara yalanır         | 101 · 104             |
| S3  | Süpürgelik yok — duvar seramiği zemine iner; birleşimde içbükey (kaveto) profil    | 106 · 107 · 109 · 110 |
| S4  | Porselen süpürgelik 80 mm — zemin karosundan kesme, rektifiye kenar                | 105 · 108             |

## KOT SÜREKLİLİĞİ — KONTROL EDİLDİ

Tüm kuru hacimlerde bitmiş zemin kotu  $\pm 0,00$ 'dir; tesviye şapı kalınlıkları (Z1: 3 · Z2: 30 · Z3: 42 · Z5: 38 mm) farklı kaplama kalınlıklarını eşitler. Mahaller arasında eşik veya kot farkı oluşmaz. Yalnızca duş ve WC bitmiş kotu  $-0,02$ 'dir; bu fark kapı altında 20 mm'lik eğimli alüminyum eşik profili ile karşılanır ve su taşkınına mahal içinde tutar.



|                         |                                 |
|-------------------------|---------------------------------|
| Pafta                   | A-05                            |
| Ölçek                   | 1/75 (A3)                       |
| Tarih                   | 17 Eylül 2026                   |
| Durum                   | Uygulama — yerinde doğrulanacak |
| MİMARİ UYGULAMA PROJESİ |                                 |
| Rev E                   |                                 |

## TAVAN TİPLERİ

## T1 · Açık (endüstriyel) tavan

+3,20

- Mevcut döşeme altı raspa + temizlik
- Tüm MEP tesisatı görünür — düzenli askı ve hizalı güzergâh zorunlu
- 2 kat siyah su bazlı akrilik boya (döşeme altı, kanal ve askılar dâhil)
- Arena üzerinde 12 adet 1200×600×50 mm asma akustik taşıyıcı baffle ( $\alpha_w \approx 0,90$ )
- Arena · fonksiyonel — serbest yükseklik korunur, ekipman kotu 2,15 m'ye kadar

## T2 · Alçıpan asma tavan — kuru hacim

+2,75

- Ayarlı askı çubuğu @900 mm, TC47 ana profil @900 / TU27 taşıyıcı @400 mm
- 12,5 mm A tipi alçıpan tek kat
- Derz bandı + 2 kat saten alçı + astar + 2 kat mat boya
- Kenar gölge derzi 10 mm (duvar birleşiminde ayrılma çatlağı önlemi)
- Giriş · banko · dinlenme — üstünde 450 mm tesisat boşluğu (kanal + tava + bakır hat sığsın diye kot 2,80'den 2,75'e indirilmiştir)

## T3 · Alçıpan asma tavan — ıslak hacim

+2,40

- Galvaniz ayarlı askı @900 mm, TC47 / TU27 karkas
- 12,5 mm H2 (su itici) alçıpan tek kat
- Su bazlı, küf önleyici yarı mat banyo boyası, 2 kat
- 300×300 mm menteşeli revizyon kapağı (her ıslak hacimde 1 adet)
- Duş · WC — üstünde 800 mm tesisat boşluğu (egzoz kanalı geçişi)

## T4 · Alçıpan asma tavan — soyunma

+2,60


- T2 ile aynı karkas ve kaplama
- Soyunma/duş sınırında kot geçiş bandı (dikme)
- Nem nedeniyle duş kapısı önünde 1,0 m şeridinde H2 alçıpan
- Erkek · kadın soyunma — üstünde 600 mm tesisat boşluğu

## TAVAN KOORDİNASYONU — KONTROL EDİLDİ

Armatür, menfez, hoparlör ve dedektör konumları elektrik (E-02, E-04) ve mekanik (M-02) paftalarıyla aynı kaynaktan üretilmiştir; otomatik çıkışma kontrolü (tools/kontrol.py) yapılmıştır. Menfezler lineer armatür sıraları arasına yerleştirilmiş, aynı hizada üst üste gelmesi önlenmiştir. Askı çubukları kanal ve boru güzergâhlarından bağımsız planlanacaktır.

## KESİT A-A · ENİNE KESİT — FONKSİYONEL ALAN, ERKEK DUŞ VE WC BLOĞU


1/50 (A3)

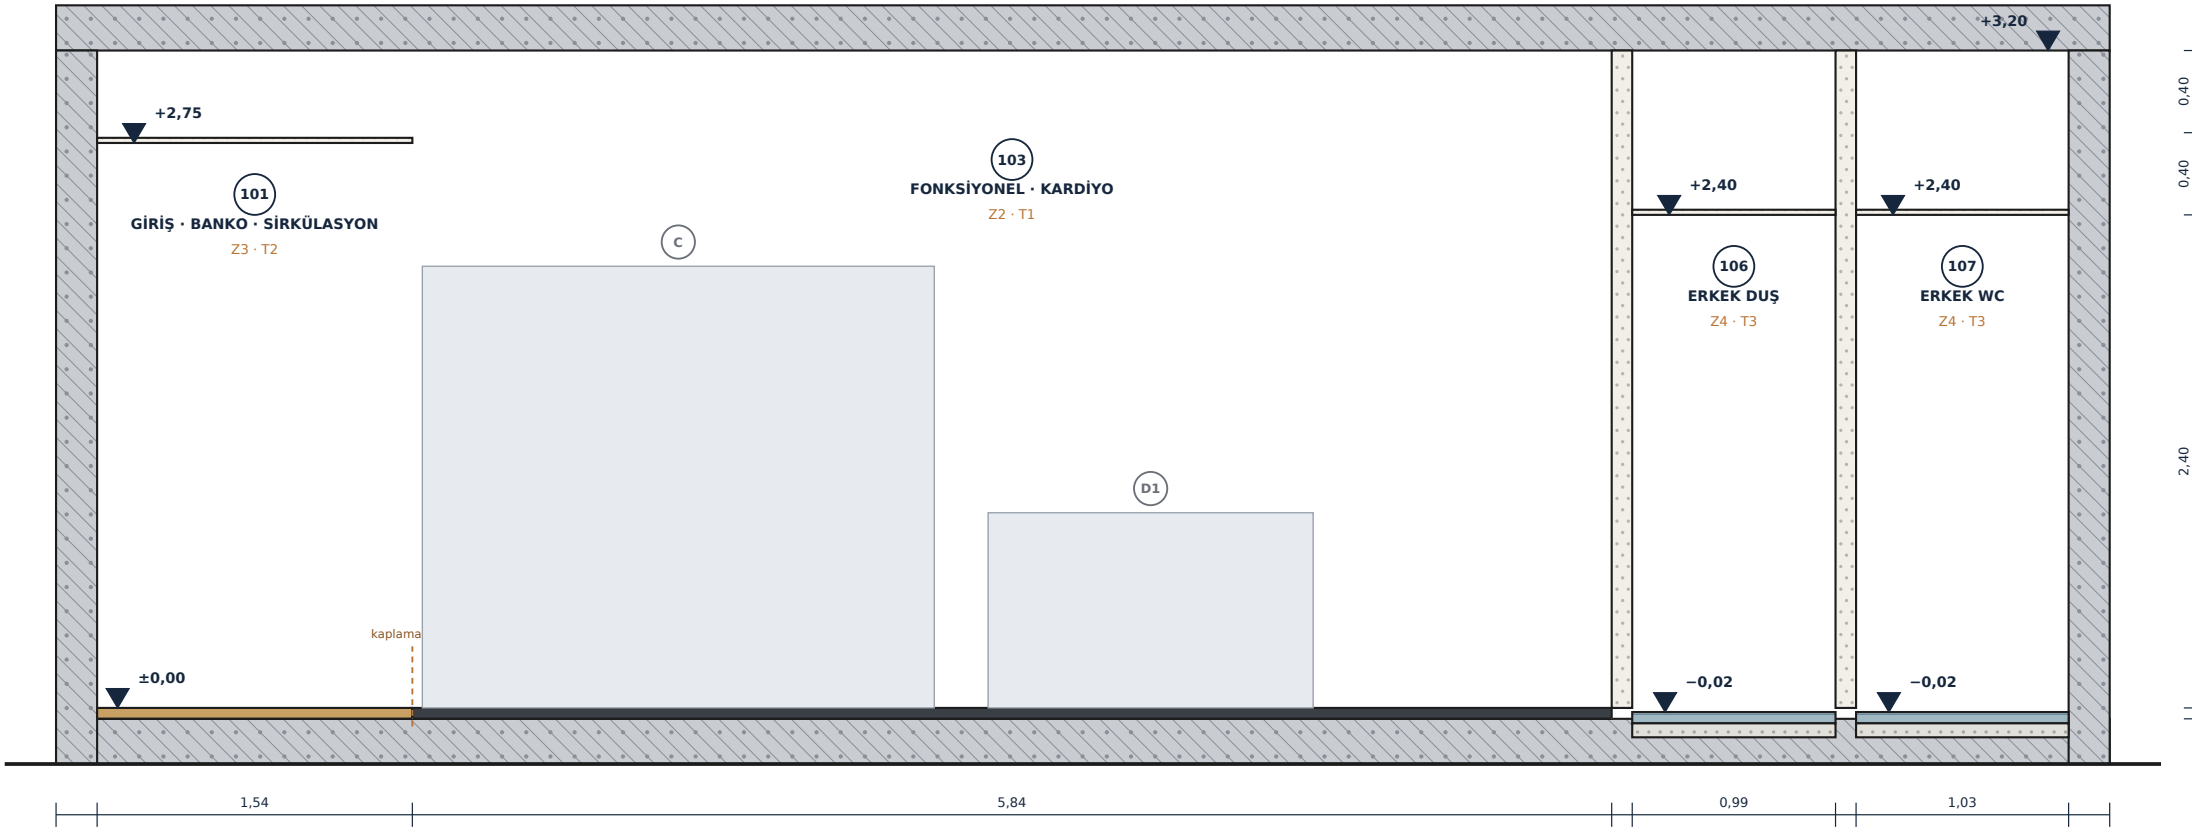

|       |                                 |
|-------|---------------------------------|
| Pafta | A-06                            |
| Ölçek | 1/50 (A3)                       |
| Tarih | 17 Eylül 2026                   |
| Durum | Uygulama — yerinde doğrulanacak |

MİMARİ UYGULAMA PROJESİ Rev E

## ANAHTAR PLAN

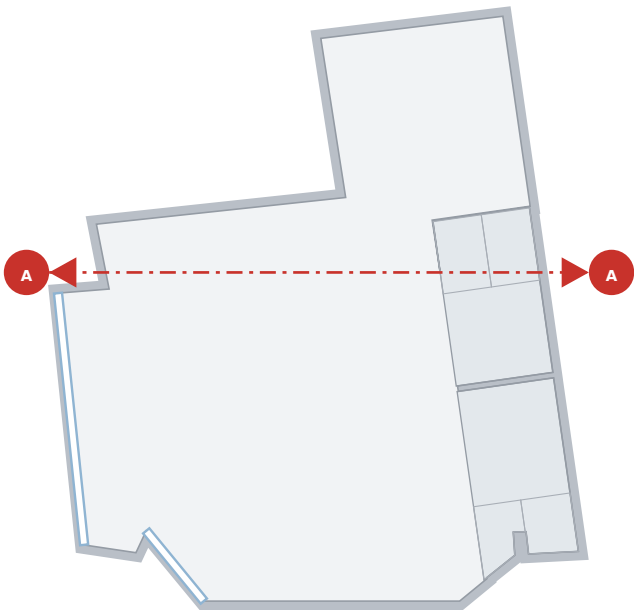

## KESİTTE GEÇİLEN MAHALLER


| NO  | MAHAL                       | ZEM. | SÜP. | TAV. | T.KOT | Z.KOT |
|-----|-----------------------------|------|------|------|-------|-------|
| 101 | GİRİŞ · BANKO · SİRKÜLASYON | Z3   | S2   | T2   | 2,75  | ±0,00 |
| 103 | FONKSİYONEL · KARDİYO       | Z2   | S1   | T1   | 3,20  | ±0,00 |
| 106 | ERKEK DUŞ                   | Z4   | S3   | T3   | 2,40  | −0,02 |
| 107 | ERKEK WC                    | Z4   | S3   | T3   | 2,40  | −0,02 |

## KESİT NOTLARI

Kesilen elemanlar kalın konturla ve malzeme taramasıyla, kesit düzleminin arkasında kalan ekipman silueti ince gri konturla gösterilmiştir. Tüm alçıpan bölmeler yapısal döşemeye kadar (+3,20) yükselir, asma tavan hizasında kesilmez. Yapısal döşeme kalınlığı ve tavan yüksekliği VARSAYIMDIR — söküm sonrası yerinde ölçülecek, kesitler ve tavan kotları buna göre revize edilecektir. Zemin katman kalınlıkları bu ölçekte okunmaz; A-11 ve A-12 detaylarına bakınız. Kesit hattı üzerinde kalmayan kapı ve pencereler gösterilmemiştir; doğrama bilgisi için A-10'a bakınız.


## KESİT B-B · BOYUNA KESİT — ARENA, ALTİGEN RİNG, FONKSİYONEL ALAN VE DİNLENME SALONU

1/50 (A3)

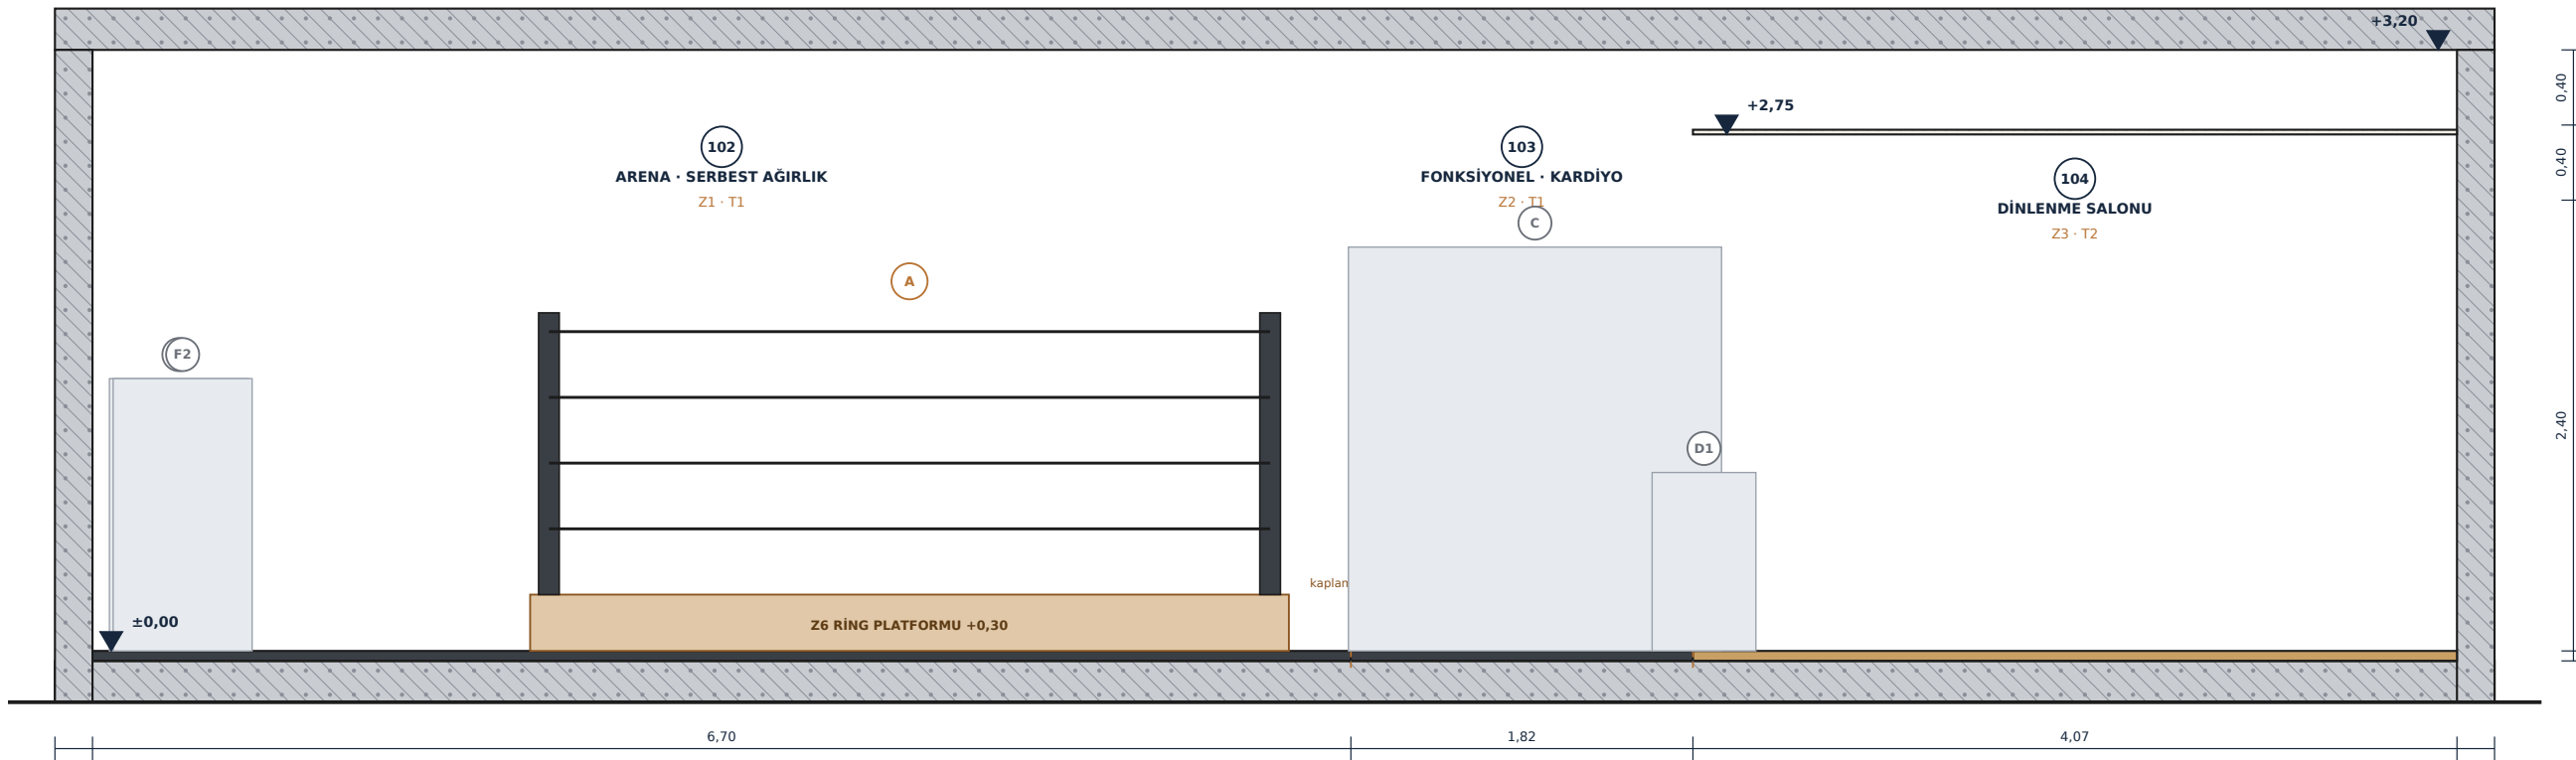

|                         |                                 |
|-------------------------|---------------------------------|
| Pafta                   | A-07                            |
| Ölçek                   | 1/50 (A3)                       |
| Tarih                   | 17 Eylül 2026                   |
| Durum                   | Uygulama — yerinde doğrulanacak |
| MİMARİ UYGULAMA PROJESİ | Rev E                           |

## ANAHTAR PLAN

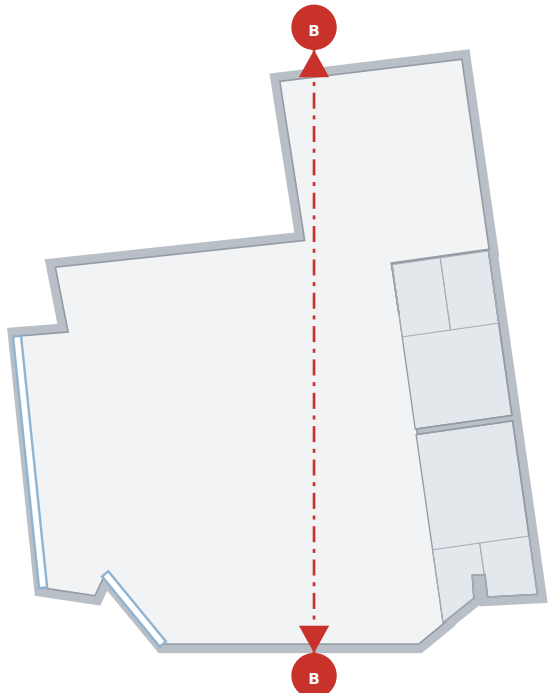

## KESİTTE GEÇİLEN MAHALLER

| NO  | MAHAL                   | ZEM. | SÜP. | TAV. | T.KOT | Z.KOT |
|-----|-------------------------|------|------|------|-------|-------|
| 102 | ARENA · SERBEST AĞIRLIK | Z1   | S1   | T1   | 3,20  | ±0,00 |
| 103 | FONKSİYONEL · KARDİYO   | Z2   | S1   | T1   | 3,20  | ±0,00 |
| 104 | DİNLENME SALONU         | Z3   | S2   | T2   | 2,75  | ±0,00 |

## KESİT NOTLARI

Kesilen elemanlar kalın konturla ve malzeme taramasıyla, kesit düzleminin arkasında kalan ekipman silüeti ince gri konturla gösterilmiştir. Tüm alçıpan bölmeler yapısal döşemeye kadar (+3,20) yükselir, asma tavan hizasında kesilmez. Yapısal döşeme kalınlığı ve tavan yüksekliği VARSAYIMDIR — söküm sonrası yerinde ölçülecek, kesitler ve tavan kotları buna göre revize edilecektir. Zemin katman kalınlıkları bu ölçekte okunmaz; A-11 ve A-12 detaylarına bakınız. Kesit hattı üzerinde kalmayan kapı ve pencereler gösterilmemiştir; doğrama bilgisi için A-10'a bakınız.



| NO  | MAHAL                       | M²    | ZEMİN | SÜP. | DUVAR                                     | TAVAN | KOT  | KAPI      | AÇIKLAMA                                                                                    |
|-----|-----------------------------|-------|-------|------|-------------------------------------------|-------|------|-----------|---------------------------------------------------------------------------------------------|
| 101 | GİRİŞ · BANKO · SİRKÜLASYON | 15,65 | Z3    | S2   | D1                                        | T2    | 2,75 | K01 · K09 | Cephe vitrini mevcut (P01); alt 1,20 m buzlu folyo. Banko arkası D1 üzeri lake MDF panel.   |
| 102 | ARENA · SERBEST AĞIRLIK     | 31,76 | Z1    | S1   | D1 + D4 (güney çeper) + D6 (ayna, 4,80 m) | T1    | 3,20 | —         | Ring platformu Z6. Ağırlık düşürme kural olarak yasak — uyarı levhası.                      |
| 103 | FONKSİYONEL · KARDİYO       | 22,31 | Z2    | S1   | D1 / D2 (soyunma bloğu cephesi)           | T1    | 3,20 | —         | Koşu bandı arkasında 60 cm serbest güvenlik mesafesi bırakılacak.                           |
| 104 | DİNLENME SALONU             | 17,33 | Z3    | S2   | D1                                        | T2    | 2,75 | —         | Yönetmelik gereği asgari 15 m² dinlenme alanı — sağlanıyor.                                 |
| 105 | ERKEK SOYUNMA               | 4,48  | Z5    | S4   | D2 / D3                                   | T4    | 2,60 | K03       | 8 kişilik soyunma dolabı + 1,60 m bank + boy aynası. Yönetmelik asgarisi 8 m² blok bazında. |
| 106 | ERKEK DUŞ                   | 1,76  | Z4    | S3   | D3 + D5 (tavana kadar)                    | T3    | 2,40 | K07       | 1 duş yeri; 100×100 mm paslanmaz süzgeç, %1,5 eğim, termostatik batarya.                    |
| 107 | ERKEK WC                    | 1,75  | Z4    | S3   | D3 + D5 (h=1,60 m)                        | T3    | 2,40 | K05       | 1 klozet + 1 lavabo; ekstraktör fan kapı menfezi ile telafi havası.                         |
| 108 | KADIN SOYUNMA               | 5,59  | Z5    | S4   | D2 / D3                                   | T4    | 2,60 | K04       | 8 kişilik soyunma dolabı + 1,60 m bank + boy aynası.                                        |
| 109 | KADIN DUŞ                   | 1,39  | Z4    | S3   | D3 + D5 (tavana kadar)                    | T3    | 2,40 | K08       | 1 duş yeri; 100×100 mm paslanmaz süzgeç, %1,5 eğim, termostatik batarya.                    |
| 110 | KADIN WC                    | 1,29  | Z4    | S3   | D3 + D5 (h=1,60 m)                        | T3    | 2,40 | K06       | 1 klozet + 1 lavabo; ekstraktör fan kapı menfezi ile telafi havası.                         |

Net mahal alanları toplamı 103,31 m² · iç bölme duvar payı 0,47 m² · net iç kullanım alanı 103,78 m².

SÜPÜRGELİK TİPLERİ

| KOD | TANIM                                                                              |
|-----|------------------------------------------------------------------------------------|
| S1  | Kauçuk süpürgelik 100×8 mm — zemin kaplamasıyla aynı malzeme, üst kenarı 45° pahlı |
| S2  | MDF lake süpürgelik 80×16 mm — RAL 9003, akrilik mastik ile duvara yalanır         |
| S3  | Süpürgelik yok — duvar seramiği zemine iner; birleşimde içbükey (kaveto) profil    |
| S4  | Porselen süpürgelik 80 mm — zemin karosundan kesme, rektifiye kenar                |

MALZEME ONAY VE NUMUNE ŞARTI

NUMUNE ONAYI

Kauçuk karo, SPC/LVT, porselen seramik, alçıpan boyası ve süpürgelik için imalat öncesi 30×30 cm numune ve teknik föy (CE beyanı, kayma direnci ve yangın sınıfı belgesi) sunulacak; işveren yazılı onayı alınmadan sipariş verilmeyecektir.

YÖNETMELİK BAĞLANTISI

Özel Beden Eğitimi ve Spor Tesisleri Yönetmeliği; soyunma mahalleri için blok başına asgari 8 m², dinlenme alanı için asgari 15 m² aramaktadır. Mahal listesinde 105+106+107 = 7,99 m² ve 108+109+110 = 8,27 m², 104 dinlenme salonu 17,33 m² ile her iki şart sağlanmaktadır. Salon alanına ilişkin GSİM uygulaması için ana dosyanın uygunluk sayfasına bakınız.

İMALAT ŞARTNAMESİ ÖZETİ — TİP KODLARININ KATMAN KARŞILIĞI

| TİP | TANIM                                             | KATMAN DİZİLİMİ (ALTtan ÜSTE / İÇten DİŞA)   | TOPLAM | PERFORMANS · STANDART · MAHAL   |
|-----|---------------------------------------------------|---|--------|---|
| Z1  | Arena · serbest ağırlık — ağır hizmet kauçuk      | Çimento esaslı kendinden yayılan tesviye şapı 3 mm + Kauçuk titreşim yalıtım matı, SBR granül 700 kg/m³ 10 mm + Granül kauçuk karo 1000×1000 mm, EPDM %10 taneli, Shore A 55±5 40 mm                                                                                            | 53 mm  | EN 14041 · yangın Bfl-s1 · EN ISO 10140 ΔLw ≥ 18 dB · serbest ağırlık düşürmeye uygun                                              |
| Z2  | Fonksiyonel · kardiyo — kauçuk karo               | Çimento esaslı tesviye şapı 30 mm + Granül kauçuk karo 1000×1000 mm, Shore A 60 20 mm + Puzzle kilitli kuru derz · çeperde 5 mm genişleme boşluğu 3 mm   | 53 mm  | EN 14041 · Bfl-s1 · kardiyo cihazı nokta yükü ≥ 4 kN/m²                                                                            |
| Z3  | Giriş · banko · dinlenme — SPC / LVT              | Çimento esaslı tesviye şapı 42 mm + IXPE akustik şilte 2 mm + SPC klik LVT, 0,55 mm aşınma tabakası 5 mm + Çeperde 8 mm genişleme boşluğu, süpürgelik altında gizlenir 4 mm   | 53 mm  | EN ISO 10874 aşınma sınıfı 33 / AC5 · EN 14041 Bfl-s1 · kaymazlık DS                                                               |
| Z4  | Duş · WC — su yalıtımlı seramik                   | Atık boru yatağı + tesisat şapı 25 mm + Eğim şapı 15 mm + Çimento esaslı 2 bileşenli su yalıtımı, 2 kat 2 mm + C2TE S1 sınıfı yapıştırıcı 5 mm + Porselen seramik 300×300 mm, R11 / B kaymazlık 8 mm                                                                            | 55 mm  | EN 14891 su yalıtımı · EN 16165 Ek B (R11) · Ek A (B sınıfı ıslak ayak)                                                            |
| Z5  | Soyunma — porselen seramik                        | Çimento esaslı tesviye şapı 38 mm + Çimento esaslı su yalıtımı, tek kat 1 mm + C2TE yapıştırıcı 5 mm + Porselen seramik 600×600 mm, R10 9 mm   | 53 mm  | EN 16165 Ek B (R10) · EN 14411 Bla · rektifiye, 2 mm derz                                                                          |
| Z6  | Ring platformu (ekipmana bağlı — işverence temin) | Bitmiş zemin Z1 üzeri ayarlı çelik ayak + 50×100 ahşap kadron @400 mm 200 mm + Su kontraplağı 2 kat 18 mm, şaşırtmalı vidalı 36 mm + EVA şok emici köpük 40 mm + Kanvas kaplama, kenarda gergi profili 10 mm + Kenarda 100 mm kauçuk kenar bandı + sarı-siyah ikaz şeridi 14 mm | 300 mm | Ekipman üreticisi montaj talimatına tabi · platform kenarı zeminden 30 cm                                                          |
| D1  | Mevcut taşıyıcı / dolgu duvar — boyalı            | Mevcut yığma veya betonarme duvar 200 mm + Çimento esaslı tamir harcı ile yüzey onarımı + Saten alçı perdah, 2 kat 3 mm + Akrilik astar + su bazlı silikonlu mat iç cephe boyası, 2 kat 3 mm                                                                                    | 206 mm | Sınıf 1 yıkanabilir boya · mevcut duvar kalınlığı VARSAYIM, yerinde ölçülecek                                                      |
| D2  | Alçıpan bölme — kuru hacim                        | 12,5 mm A tipi alçıpan, 2 kat 25 mm + 50×0,6 mm galvaniz C profil @400 mm + U tabanlık 50 mm + Taşyünü dolgu 40 mm / 50 kg/m³ + 12,5 mm A tipi alçıpan, 2 kat 25 mm   | 100 mm | Rw ≈ 51 dB (EN ISO 717-1) · U tabanlık altında butil ses bandı                                                                     |
| D3  | Alçıpan bölme — ıslak hacim yüzü                  | 12,5 mm H2 25 mm + 50×0,6 mm galvaniz C profil @400 mm + U tabanlık 50 mm + Taşyünü dolgu 40 mm / 50 kg/m³ + 12,5 mm A tipi alçıpan, 2 kat 25 mm   | 100 mm | EN 520 tip H2 · ıslak yüzde 2 kat çimento esaslı su yalıtımı + seramik (kalınlık hariç)                                            |
| D4  | Akustik giydirme — arena çeperi                   | Mevcut duvardan bağımsız 20 mm hava boşluğu 20 mm + 50×0,6 mm C profil karkas 50 mm + Taşyünü dolgu 50 mm / 70 kg/m³ + 12,5 mm yüksek yoğunluklu akustik alçıpan 12,5 mm + 12,5 mm A tipi alçıpan + saten + boya 12,5 mm                                                        | 95 mm  | ΔRw ≈ +10 dB · üst kat konut VARSAYIMI gereği arena çeperinde uygulanır                                                            |
| D5  | Seramik kaplı duvar — ıslak hacim                 | Mevcut duvar veya D3 ıslak yüzü 200 mm + Çimento esaslı 2 bileşenli su yalıtımı, 2 kat; köşe ve zemin birleşiminde 12 cm bant 2 mm + C2TE S1 yapıştırıcı 5 mm + Porselen seramik 300×600 mm, rektifiye 9 mm                                                                     | 216 mm | EN 14891 · duş kabininde tavana kadar, WC'de h=1,60 m, üstü küf önleyici banyo boyası                                              |
| D6  | Ayna duvarı — arena güney çeperi                  | D1 veya D4 üzerine 18 mm su kontraplağı taşıyıcı altlık 18 mm + 6 mm güvenlik filmli ayna, yapıştırma + mekanik emniyet profili 6 mm   | 212 mm | Ayna alt kotu +0,30 · üst kotu +2,30 · kırılmaya karşı arka yüz güvenlik filmi (EN 12600)                                          |
| T1  | Açık (endüstriyel) tavan                          | Mevcut döşeme altı raspa + temizlik + Tüm MEP tesisatı görünür + 2 kat siyah su bazlı akrilik boya + Arena üzerinde 12 adet 1200×600×50 mm asma akustik taşyünü baffle   | +3,20  | Arena · fonksiyonel — serbest yükseklik korunur, ekipman kotu 2,15 m'ye kadar                                                      |
| T2  | Alçıpan asma tavan — kuru hacim                   | Ayarlı askı çubuğu @900 mm, TC47 ana profil @900 / TU27 taşıyıcı @400 mm + 12,5 mm A tipi alçıpan tek kat + Derz bandı + 2 kat saten alçı + astar + 2 kat mat boya + Kenar gölge derzi 10 mm                                                                                    | +2,75  | Giriş · banko · dinlenme — üstünde 450 mm tesisat boşluğu (kanal + tava + bakır hat sığsın diye kot 2,80'den 2,75'e indirilmiştir) |
| T3  | Alçıpan asma tavan — ıslak hacim                  | Galvaniz ayarlı askı @900 mm, TC47 / TU27 karkas + 12,5 mm H2 + Su bazlı, küf önleyici yarı mat banyo boyası, 2 kat + 300×300 mm menteşeli revizyon kapağı   | +2,40  | Duş · WC — üstünde 800 mm tesisat boşluğu (egzoz kanalı geçişi)                                                                    |
| T4  | Alçıpan asma tavan — soyunma                      | T2 ile aynı karkas ve kaplama + Soyunma/duş sınırında kot geçiş bandı + Nem nedeniyle duş kapısı önünde 1,0 m şeridinde H2 alçıpan   | +2,60  | Erkek · kadın soyunma — üstünde 600 mm tesisat boşluğu                                                                             |

KAPI LİSTESİ

| KOD | AD. | MAHAL                   | EN×YÜK (MM) | TİP                         | KANAT / KASA                                 | DONANIM                                                          | ÖZEL ŞART                                             |
|-----|-----|-------------------------|-------------|-----------------------------|----------------------------------------------|------------------------------------------------------------------|-------------------------------------------------------|
| K01 | 1   | 101 Giriş               | 1600×2400   | Çift kanat cam kapı (2×800) | Mevcut alüminyum doğrama + 8 mm temperli cam | Panik kolu (EN 1125), hidrolik kapı kapatıcı, eşiksiz alt profil | Açılış yönü DIŞARI çevrilecek — mevcut doğrama revize |
| K02 | 1   | 101 → GB cephe          | 1000×2100   | Tek kanat acil çıkış        | Alüminyum + 8 mm temperli cam                | Panik bar (EN 1125), kapı kapatıcı, dışa açılır                  | Acil çıkış levhası + acil aydınlatma AY3 üstünde      |
| K03 | 1   | 105 Erkek soyunma       | 900×2100    | Tek kanat panel kapı        | MDF laminat kaplı kanat, WPC kasa ve pervaz  | Paslanmaz kol, silindirli kilit, 3 adet menteşe                  | Alt kısmında 150 cm² net hava geçiş menfezi           |
| K04 | 1   | 108 Kadın soyunma       | 900×2100    | Tek kanat panel kapı        | MDF laminat kaplı kanat, WPC kasa ve pervaz  | Paslanmaz kol, silindirli kilit, 3 adet menteşe                  | Alt kısmında 150 cm² net hava geçiş menfezi           |
| K05 | 1   | 107 Erkek WC            | 700×2000    | Tek kanat WC kapısı         | Tam WPC (su geçirmez) kanat ve kasa          | Kilit göstergeli WC kolu, paslanmaz menteşe                      | Alt menfez 150 cm² — egzoz telafi havası              |
| K06 | 1   | 110 Kadın WC            | 700×2000    | Tek kanat WC kapısı         | Tam WPC (su geçirmez) kanat ve kasa          | Kilit göstergeli WC kolu, paslanmaz menteşe                      | Alt menfez 150 cm² — egzoz telafi havası              |
| K07 | 1   | 106 Erkek duş           | 700×1950    | Duş kapağı                  | 6 mm temperli cam, alüminyum profil          | Paslanmaz menteşe, manyetik fitil                                | Alt kenar zeminden 15 mm yukarıda                     |
| K08 | 1   | 109 Kadın duş           | 700×1950    | Duş kapağı                  | 6 mm temperli cam, alüminyum profil          | Paslanmaz menteşe, manyetik fitil                                | Alt kenar zeminden 15 mm yukarıda                     |
| K09 | 1   | 101 Depo / teknik dolap | 700×2000    | Tek kanat dolap kapağı      | MDF laminat, banko arkası niş                | Bas-aç mandal, kilitli                                           | Havalandırma menfezli — NVR ve router ısısı için      |

PENCERE / CEPHE DOĞRAMASI

| KOD | AD. | MAHAL                          | DOĞRAMA                                      | CAM / KAPLAMA                                                           | NOT                                                       |
|-----|-----|--------------------------------|----------------------------------------------|-------------------------------------------------------------------------|-----------------------------------------------------------|
| P01 | 1   | 101 Giriş — batı cephe vitrini | Mevcut alüminyum doğrama + 8 mm temperli cam | Alt 1,20 m buzlu folyo · üst bant şeffaf · iç yüzde güneş kontrol filmi | Mevcut — ölçü yerinde alınacak (VARSAYIM: 5,62 m açıklık) |
| P02 | 1   | 101 Giriş — GB cephe vitrini   | Mevcut alüminyum doğrama + 8 mm temperli cam | Alt 1,20 m buzlu folyo · K02 acil çıkış bu doğrama içinde               | Mevcut — ölçü yerinde alınacak (VARSAYIM: 2,02 m açıklık) |

DUVAR TİPLERİ — KATMAN DİZİLİMİ

D1 · Mevcut taşıyıcı / dolgu duvar — boyalı206 mm

1. Mevcut yığma veya betonarme duvar — 200 mm

2. Çimento esaslı tamir harcı ile yüzey onarımı

3. Saten alçı perdah, 2 kat — 3 mm

4. Akrilik astar + su bazlı silikonlu mat iç cephe boyası, 2 kat — 3 mm

yatay kesit — katman genişlikleri orantılıdır

Sınıf 1 yıkanabilir boya · mevcut duvar kalınlığı VARSAYIM, yerinde ölçülecek

D2 · Alçıpan bölme — kuru hacim100 mm

1. 12,5 mm A tipi alçıpan, 2 kat (şaşırtmalı derz) — 25 mm

2. 50×0,6 mm galvaniz C profil @400 mm + U tabanlık — 50 mm

3. Taşyünü dolgu 40 mm / 50 kg/m³

4. 12,5 mm A tipi alçıpan, 2 kat — 25 mm

yatay kesit — katman genişlikleri orantılıdır

Rw ≈ 51 dB (EN ISO 717-1) · U tabanlık altında butil ses bandı

D3 · Alçıpan bölme — ıslak hacim yüzü100 mm

1. 12,5 mm H2 (su itici / yeşil) alçıpan, 2 kat — ıslak yüz — 25 mm

2. 50×0,6 mm galvaniz C profil @400 mm + U tabanlık — 50 mm

3. Taşyünü dolgu 40 mm / 50 kg/m³

4. 12,5 mm A tipi alçıpan, 2 kat — kuru yüz — 25 mm

yatay kesit — katman genişlikleri orantılıdır

EN 520 tip H2 · ıslak yüzde 2 kat çimento esaslı su yalıtımı + seramik (kalınlık hariç)

D4 · Akustik giydirme — arena çeperi95 mm

1. Mevcut duvardan bağımsız 20 mm hava boşluğu — 20 mm

2. 50×0,6 mm C profil karkas (duvara bağlantısız, tavan-döşeme arası) — 50 mm

3. Taşyünü dolgu 50 mm / 70 kg/m³

4. 12,5 mm yüksek yoğunluklu akustik alçıpan — 12,5 mm

5. 12,5 mm A tipi alçıpan + saten + boya — 12,5 mm

yatay kesit — katman genişlikleri orantılıdır

ΔRw ≈ +10 dB · üst kat konut VARSAYIMI gereği arena çeperinde uygulanır

D5 · Seramik kaplı duvar — ıslak hacim216 mm

1. Mevcut duvar veya D3 ıslak yüzü — 200 mm

2. Çimento esaslı 2 bileşenli su yalıtımı, 2 kat; köşe ve zemin birleşiminde 12 cm bant — 2 mm

3. C2TE S1 yapıştırıcı — 5 mm

4. Porselen seramik 300×600 mm, rektifiye — 9 mm

yatay kesit — katman genişlikleri orantılıdır

EN 14891 · duş kabininde tavana kadar, WC'de h=1,60 m, üstü küf önleyici banyo boyası

D6 · Ayna duvarı — arena güney çeperi212 mm

1. D1 veya D4 üzerine 18 mm su kontraplağı taşıyıcı altlık — 18 mm

2. 6 mm güvenlik filmlli ayna, yapıştırma + mekanik emniyet profili — 6 mm

yatay kesit — katman genişlikleri orantılıdır


Ayna alt kotu +0,30 · üst kotu +2,30 · kırılmaya karşı arka yüz güvenlik filmi (EN 12600)

Ön tasarım — yerinde doğrulanmadan ve ruhsat alınmadan uygulama yapılamaz. Tüm ölçüler raster paftadan ölçeklendirilmiştir (±%3).

17 Eylül 2026 · Sayfa 10 / 13

## D-01 Z1 ZEMİN KATMAN DETAYI — ARENA · SERBEST AĞIRLIK


Z1

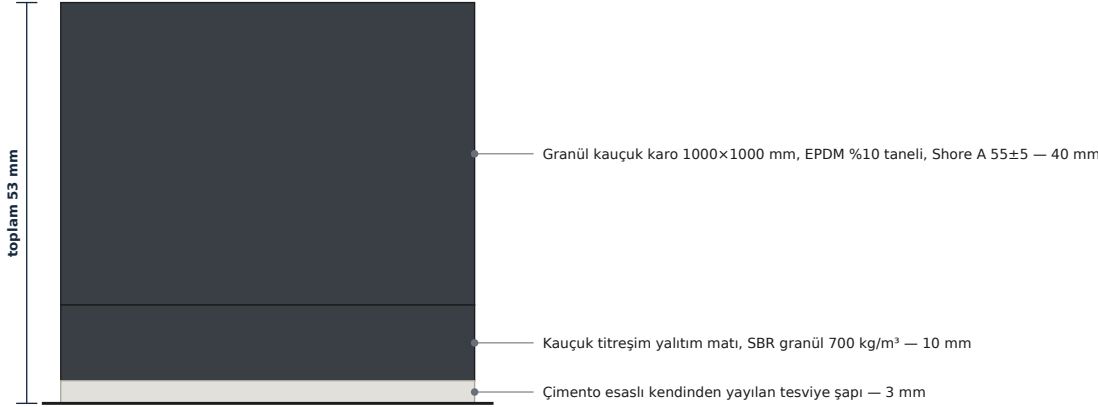

- Kauçuk karo çeperde 5 mm genleşme boşluğu ile biter; boşluk süpürgelik altında kalır.
- Titreşim matı duvara 50 mm yukarı dönerek yüzzer döşeme teşkil eder (yan geçiş sesi kesilir).
- Karo altı kuru uygulamadır — yapıştırıcı kullanılmaz, sökülüp değiştirilebilir.

## D-02 Z4 ISLAK HACİM ZEMİN VE DUVAR BİRLEŞİMİ


Z4 · D5

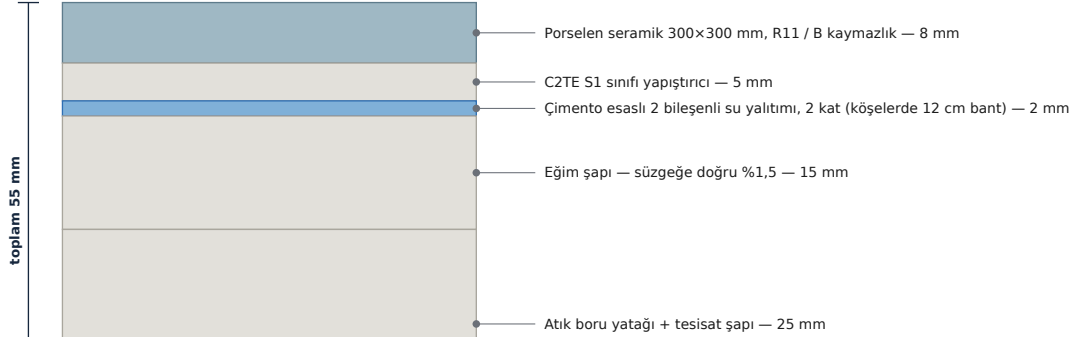

- Su yalıtımı duvarda en az 300 mm, duş kabininde 2000 mm yukarı döner.
- Zemin-duvar köşesinde 120 mm elastik su yalıtım bandı, yalıtımın iki katı arasına gömülür.
- Seramik derzi çimento esaslı (CG2 WA); köşe derzleri silikon (sınıf 25LM, küf önleyici).

## D-03 Z3 / Z1 ZEMİN KOT VE MALZEME GEÇİŞ DETAYI

Z1 · Z2 · Z3 · Z5

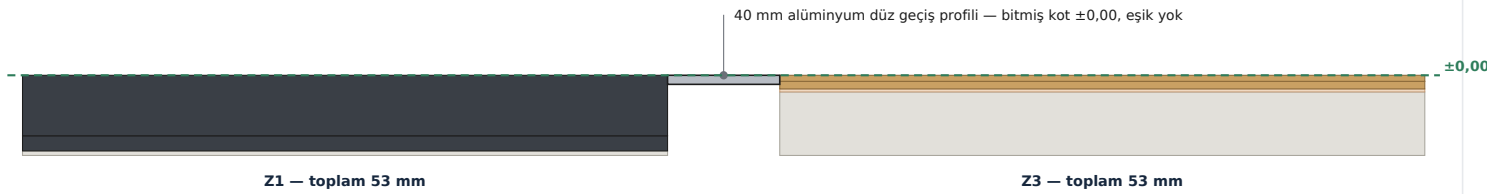

- Bitmiş zemin kotları eşittir (±0,00) — eşik veya rampa oluşmaz, tökezleme riski yoktur.
- Geçişte 40 mm alüminyum düz geçiş profili; kauçuk tarafta 5 mm genleşme boşluğu bırakılır.
- Tesviye şapı kalınlıkları farklıdır (Z1: 3 mm · Z2: 30 mm · Z3: 42 mm · Z5: 38 mm).

## D-04 D2 ALÇIPAN BÖLME — YATAY KESİT VE KÖŞE


D2



- C profiller @400 mm; kapı kenarlarında ve 3,0 m'den uzun duvarlarda kutu profil takviye.
- Alçıpan derzleri iki yüzde şaşırtmalı; ikinci kat ilk katla 600 mm kaydırılır.
- Ağır asma yük (ayna, dolap, TV) için karkas içine 18 mm kontraplak takviye gömülür.

## D-05 D3 ISLAK BÖLME + DUŞ SÜZGEÇ VE EĞİM DETAYI

D3 · Z4

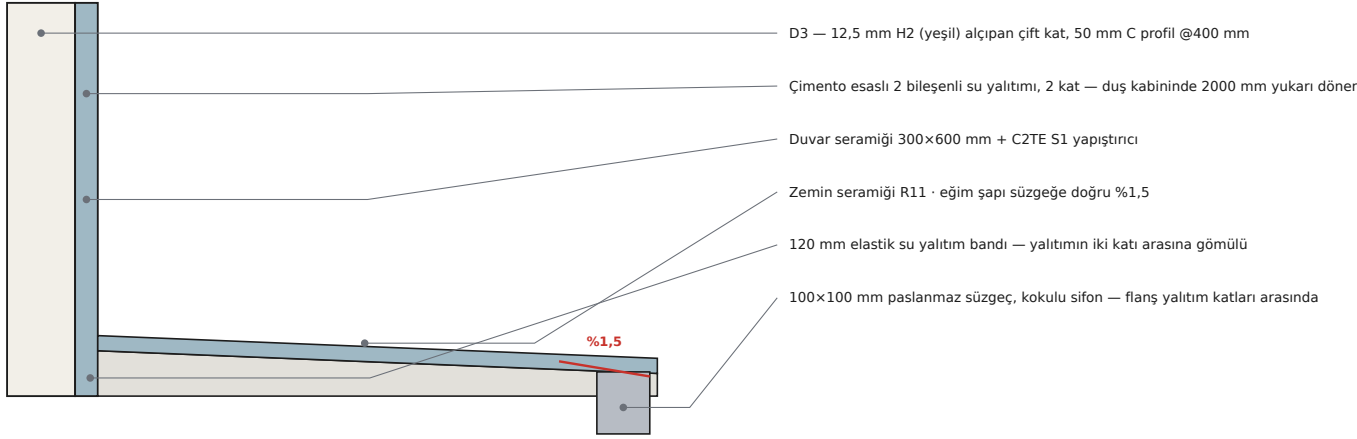


U tabanlılık butil bant üzerine · alçıpan alt kenarı bitmiş zeminden +10 mm

- Duş zemini süzgeçe %1,5 eğimli; süzgeç 100x100 mm paslanmaz, kokulu sifon (50 mm su tutuşlu).
- Süzgeç flanşı su yalıtımının iki katı arasına sıkıştırılır — sızdırmazlık burada sağlanır.
- U tabanlılık profil butil bant üzerine oturur; alçıpan alt kenarı bitmiş zeminden 10 mm yukarıda.

## D-06 T2 / T3 ASMA TAVAN KENAR VE REVİZYON KAPAĞI


T2 · T3

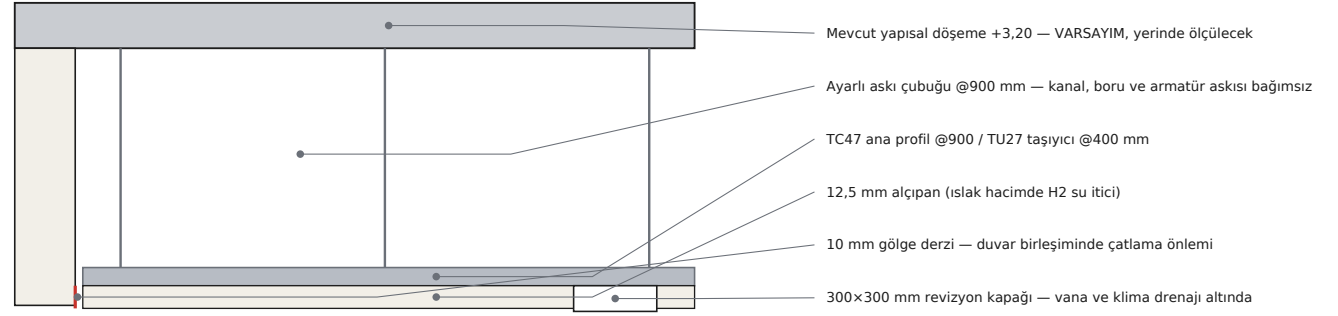

- Duvar birleşiminde 10 mm gölge derzi — farklı oturma nedeniyle çatlamayı önler.
- Askı @900 mm; kanal, boru veya armatür ağırlığı alçıpan karkasına asılmaz, ayrı askılanır.
- Her ıslak hacimde 300x300 mm revizyon kapağı; vana ve klima drenaj bağlantısı altında.

## D-07 Z6 RING PLATFORMU KENAR DETAYI

Z6

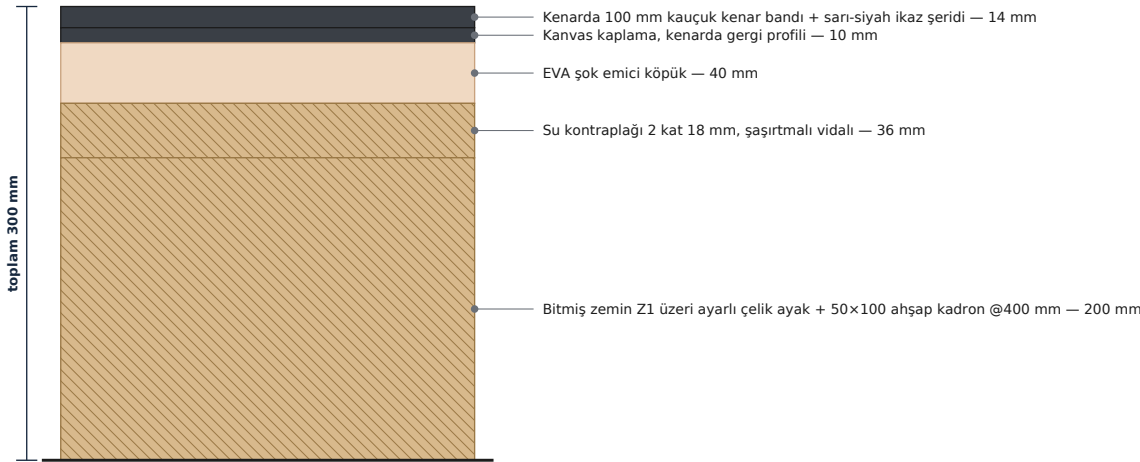


Katman şeması · ölçek 1/5 · bitmiş kot +0,30


- Platform ekipman üreticisinin montaj talimatına tabidir; bu detay çevre bitişini tanımlar.
- Kenarda 100 mm kauçuk kenar bandı + sarı-siyah ikaz şeridi (kot farkı 30 cm).
- Platform altı boşluğu havalandırılmalı bırakılır, temizlik için 2 gözde sökülebilir kapak.

## D-08 D6 AYNA MONTAJ DETAYI

D6

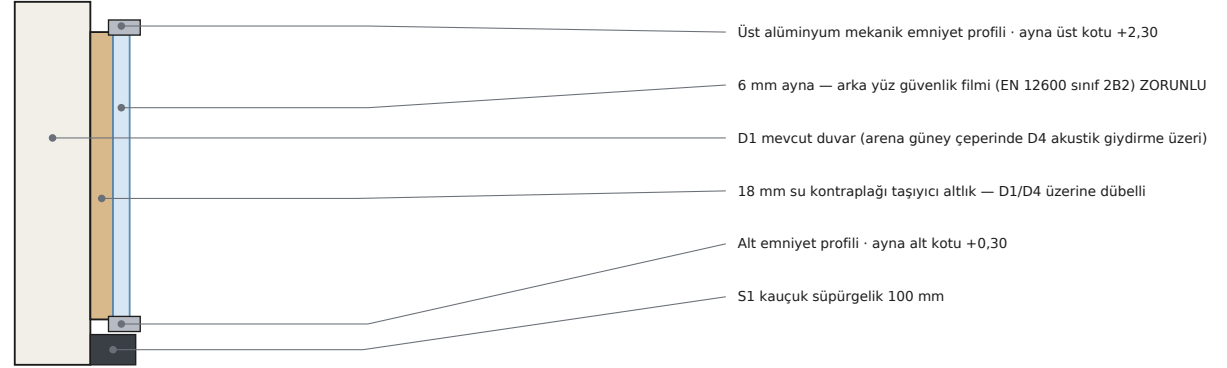

- Ayna alt kotu +0,30 (süpürgelik üstü), üst kotu +2,30.
- Arka yüzde güvenlik filmi (EN 12600 sınıf 2B2) ZORUNLU — serbest ağırlık alanında kırılma riski.
- Yapıştırma + alt ve üstte alüminyum mekanik emniyet profili; ayna arkası nemsiz kalmalı.

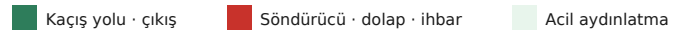

|                         |                                 |
|-------------------------|---------------------------------|
| Pafta                   | A-13                            |
| Ölçek                   | 1/75 (A3)                       |
| Tarih                   | 17 Eylül 2026                   |
| Durum                   | Uygulama — yerinde doğrulanacak |
| MİMARİ UYGULAMA PROJESİ |                                 |
| Rev E                   |                                 |

| NO  | MAHAL                   | MESAFE | ÇIKIŞ      |
|-----|-------------------------|--------|------------|
| 104 | DİNLENME SALONU         | 10,3 m | Ç1         |
| 103 | FONKSİYONEL · KARDİYO   | 7,0 m  | Ç1         |
| 102 | ARENA · SERBEST AĞIRLIK | 2,3 m  | Ç2         |
| 105 | ERKEK SOYUNMA           | 10,6 m | Ç1         |
| 108 | KADIN SOYUNMA           | 13,4 m | Ç1         |
|     | EN UZUN KAÇIŞ           | 13,4 m | sınır 45 m |

| KOD   | TANIM                                                                  |
|-------|------------------------------------------------------------------------|
| YD1   | Yangın dolabı — 30 m hortum, TS EN 671-2 (opsiyon: GSİM talebine göre) |
| YT1   | 6 kg ABC kuru kimyevi tozlu yangın söndürücü — çıkış yanında           |
| YT2   | 6 kg ABC kuru kimyevi tozlu yangın söndürücü — dinlenme/soyunma yakını |
| YT3   | 6 kg ABC kuru kimyevi tozlu yangın söndürücü — acil çıkış yanında      |
| YB1   | yangın ihbar butonu — ana çıkış                                        |
| YB2   | yangın ihbar butonu — ikinci çıkış                                     |
| SR1   | siren + flaşör                                                         |
| AY1-3 | Çıkış yönlendirme armatürü — kendinden akülü, 60 dk                    |
| AA1-5 | Acil aydınlatma armatürü — kendinden akülü, 60 dk                      |

İki bağımsız çıkış (Ç1 ana giriş 1,60 m · Ç2 acil çıkış 1,00 m) mevcuttur; toplam çıkış genişliği 2,60 m, 14 kişilik tasarım kapasitesi için fazlasıyla yeterlidir. En uzun kaçış mesafesi 13,4 m olup Binaların Yangından Korunması Hakkında Yönetmelik'in iki kişilik tesisler için öngördüğü sınırı çok altındadır. Kaçış kapıları kaçış yönünde açılacak, panik donanımlı olacak, üzerinde kilit bulunmayacaktır. Kaçış yolu genişliği hiçbir noktada 1,10 m'nin altına düşmeyecek; ekipman ve mobilya bu koridora taşınmayacaktır.