


LEJANT

- Mimari — mevcut duvar (korunuyor)
— Mimari — yeni alçipan bölme

NOTLAR

Mimari altlık — mevcut duvar korunur.
Kırmızı: yeni alçipan bölme.
Olcüler raster pafıadan (+/-%3).

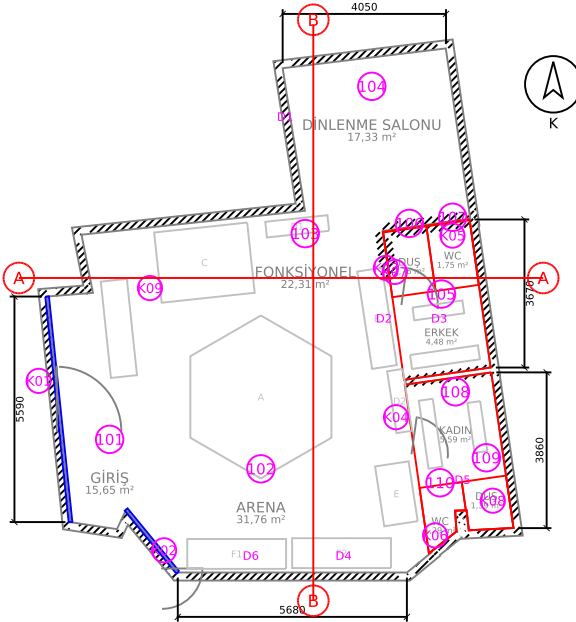

PROJE

MALTEPE / İDEALTEPE — GYM DÖNÜŞÜMÜ

DISİPLİN
MİMARİ

PAFTA ADI
MİMARİ ALTLIK

PAFTA NO
A-01

TARİH
17 Eylül 2026

BİRİM
milimetre (mm)

Yerinde doğrulanmadan ve ruhsat alınmadan uygulama yapılamaz.

ÖLÇEK
1/75

REVİZYON
Rev E


DURUM
ÖN TASARIM

LEJANT

- Mimari — mevcut duvar (korunuyor)
— Mimari — yeni alçipan bölme

NOTLAR

Mahal no, kapı kodu, duvar tipi ve kesit hattı gösterilmiştir.
Tüm alçipan bölmeler yapısal doseme altına (+3,20) kadar yükselir.

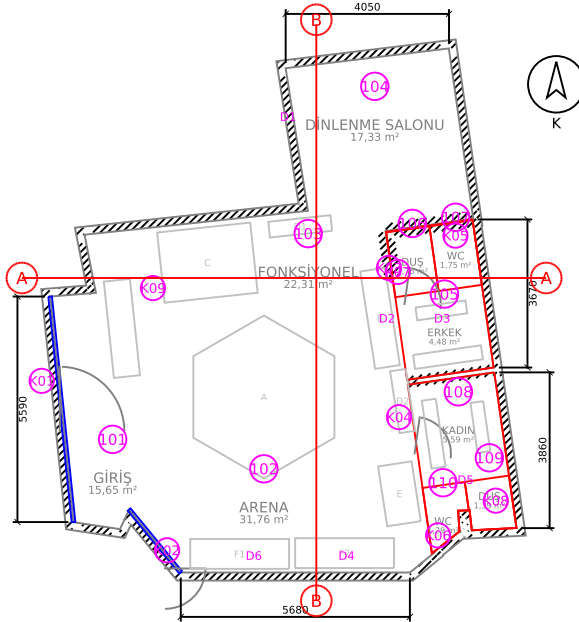

PROJE

MALTEPE / İDEALTEPE — GYM DÖNÜŞÜMÜ

DISİPLİN
MİMARİ

PAFETA ADI
MİMARİ UYGULAMA PLANI

PAFETA NO
A-02

ÖLÇEK
1/75

TARİH
17 Eylül 2026

REVİZYON
Rev E

BİRİM
milimetre (mm)

DURUM
ÖN TASARIM


Yerinde doğrulanmadan ve ruhsat alınmadan uygulama yapılamaz.

LEJANT

- Mimari — mevcut duvar (korunuyor)
— Mimari — yeni alçipan bölme

NOTLAR

Bitmiş zemin kotu tüm kuru hacimde
+/-0,00; dus ve WC -0,02.
Tesiye sapi kalinliklari farklidir
(Z1:3 Z2:30 Z3:42 Z5:38 mm).
Kaucuk karo derzi 1000x1000 mm.

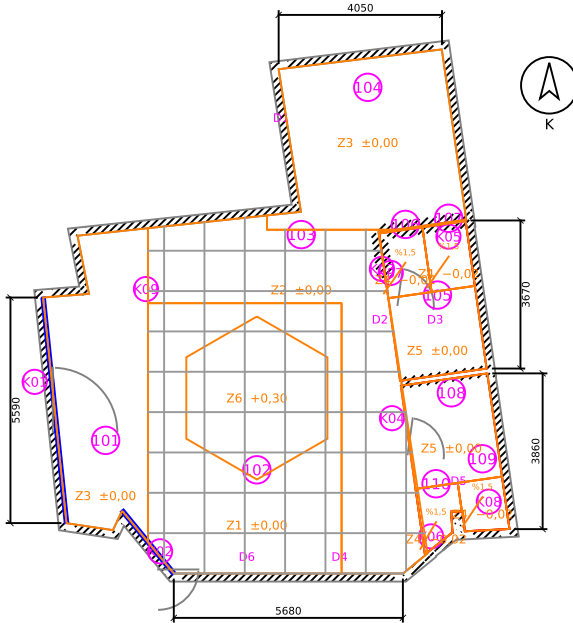

PROJE

MALTEPE / İDEALTEPE — GYM DÖNÜŞÜMÜ

DISİPLİN
MİMARİ

PAFTA ADI
ZEMİN KAPLAMA PLANI

PAFTA NO
A-03

ÖLÇEK
1/75


TARİH
17 Eylül 2026

REVİZYON
Rev E

BİRİM
milimetre (mm)

DURUM
ÖN TASARIM

Yerinde doğrulanmadan ve ruhsat alınmadan uygulama yapılamaz.

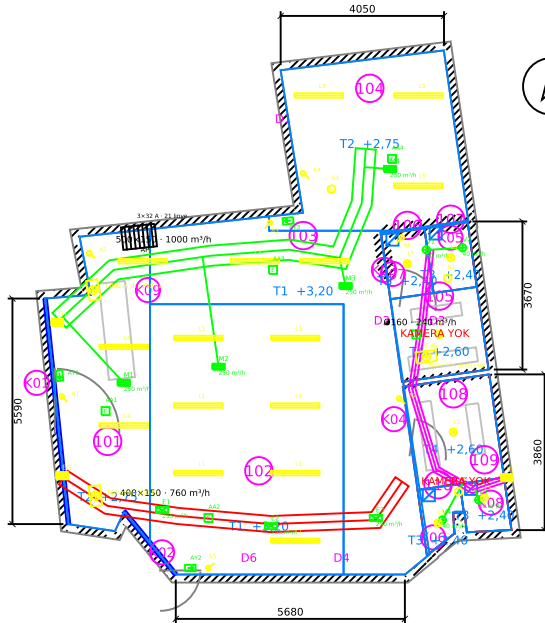

LEJANT

- Mimari — mevcut duvar (korunuyor)
- Mimari — yeni alçıpan bölme
- Mekanik — taze hava kanalı
- Mekanik — egzoz kanalı
- Mekanik — ıslak hacim egzoz kanalı
- Mekanik — menfez ve valf
- Mekanik — menfez bransmanı
- Mekanik — fan ve panjur
- Mekanik — etiket ve not
- Elektrik — lineer LED armatür
- Elektrik — IP44 downlight
- Elektrik — acil aydınlatma / yönlendirme
- Elektrik — anahtar ve sensör
- Elektrik — ana dağıtım panosu
- Elektrik — etiket ve not

NOTLAR

T1 acık tavan +3,20 · T2 +2,75

T4 +2,60 · T3 +2,40.

Tesisat askisi alçıpan karkasına

asılmaz; ayrı askılanır.

Her ıslak hacimde 300x300 revizyon.

PROJE
MALTEPE / İDEALTEPE — GYM DÖNÜŞÜMÜ

DISİPLİN
MİMARİ

PAFTA ADI
TAVAN PLANI (RCP)

PAFTA NO
A-04

TARİH
17 Eylül 2026

BİRİM
milimetre (mm)

ÖLÇEK
1/75

REVİZYON
Rev E

DURUM
ÖN TASARIM


Yerinde doğrulanmadan ve ruhsat alınmadan uygulama yapılamaz.

LEJANT

- Mimari — mevcut duvar (korunuyor)
- Mimari — yeni alçipan bölme
- Elektrik — acil aydınlatma / yönlendirme
- Elektrik — dedektör, buton, siren

NOTLAR

İki bağımsız çıkış: C1 1,60 m, C2 1,00 m.
En uzun kaçış yolu 13,4 m.
Kaçış kapıları kaçış yönünde açılır,
panik donanımlı, kilitsiz.

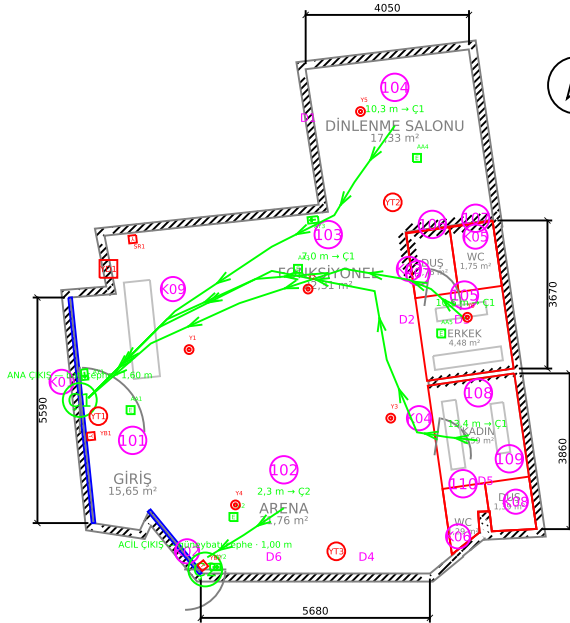

PROJE

MALTEPE / İDEALTEPE — GYM DÖNÜŞÜMÜ

DISİPLİN
MİMARİ

PAFTA ADI
YANGIN VE TAHLİYE PLANI

PAFTA NO
A-05

ÖLÇEK
1/75

TARİH
17 Eylül 2026

REVİZYON
Rev E

BİRİM
milimetre (mm)

DURUM
ÖN TASARIM


Yerinde doğrulanmadan ve ruhsat alınmadan uygulama yapılamaz.

LEJANT

- Mimari — mevcut duvar (korunuyor)
- Mimari — yeni alçıpan bölme
- Mekanik — taze hava kanalı
- Mekanik — egzoz kanalı
- Mekanik — ıslak hacim egzoz kanalı
- Mekanik — menfez ve valf
- Mekanik — menfez bransmanı
- Mekanik — fan ve panjur
- Mekanik — etiket ve not

NOTLAR

Kanallar galvaniz sac, TS EN 1507 sınıf B.
Besleme ve egzoz hattı 19 mm izoleli.
Her bransman baskı debi ayar damperi.
Devreye almada balanslama ve ölçüm raporu.

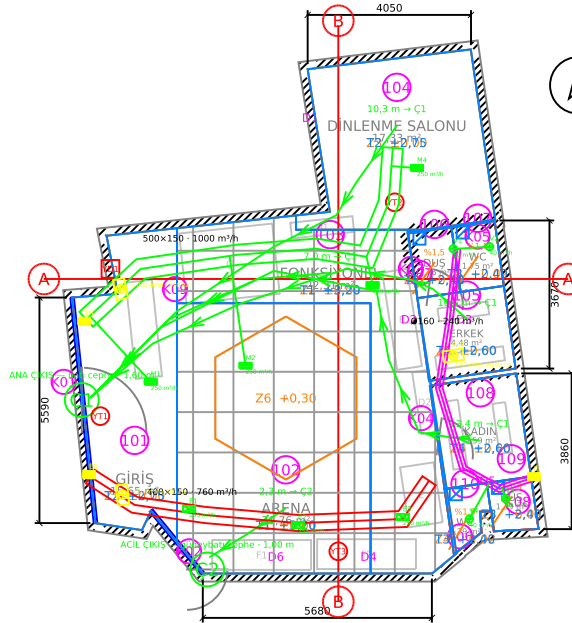

PROJE
MALTEPE / İDEALTEPE — GYM DÖNÜŞÜMÜ

DISİPLİN
MEKANİK TESİSAT

PAFTA ADI
HAVALANDIRMA PLANI

PAFTA NO
M-01

ÖLÇEK
1/75

TARİH
17 Eylül 2026

REVİZYON
Rev E

BİRİM
milimetre (mm)

DURUM
ÖN TASARIM


Yerinde doğrulanmadan ve ruhsat alınmadan uygulama yapılamaz.

LEJANT

- Mimari — mevcut duvar (korunuyor)
- Mimari — yeni açılan bölme
- Mekanik — klima iç ünite
- Mekanik — klima dış ünite platformu
- Mekanik — soğutucu akışkan bakır hattı
- Mekanik — klima drenaj hattı
- Mekanik — etiket ve not

NOTLAR

- İç ünite montaj kotu 2,40 m (alt kot).
- Bakır hat izoleli, dış ünite konsolu titreşim tokozlu.
- Drenaj %1 eğimli.

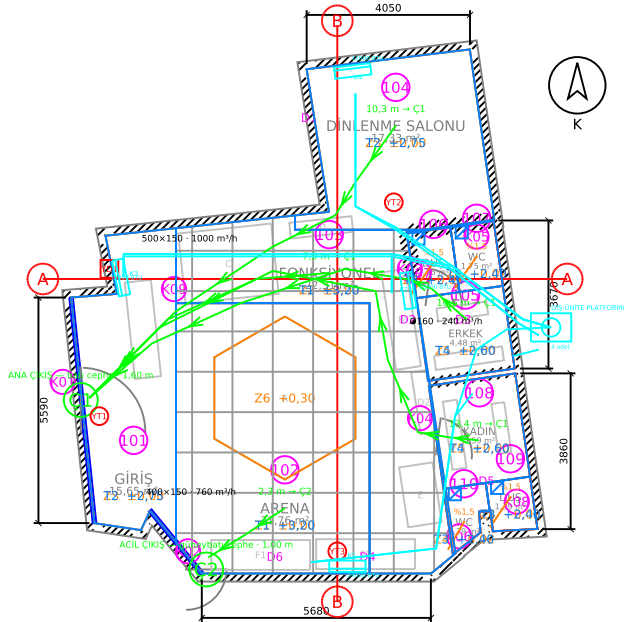


LEJANT

- Mimari — mevcut duvar (korunuyor)
- Mimari — yeni alçıpan bölme
- Mekanik — temiz su PPRC
- Mekanik — sıcak su PPRC izoleli
- Mekanik — pis su PVC
- Mekanik — vitrifiye ve su ısıtıcı
- Mekanik — etiket ve not

NOTLAR

- Pis su %2 eğimli.
- Tum ıslak hacimde sifonlu yer suzgeci.
- SOKUM SONRASI İLK İS: mevcut pis su bağlantı kotunun ölçülmesi.

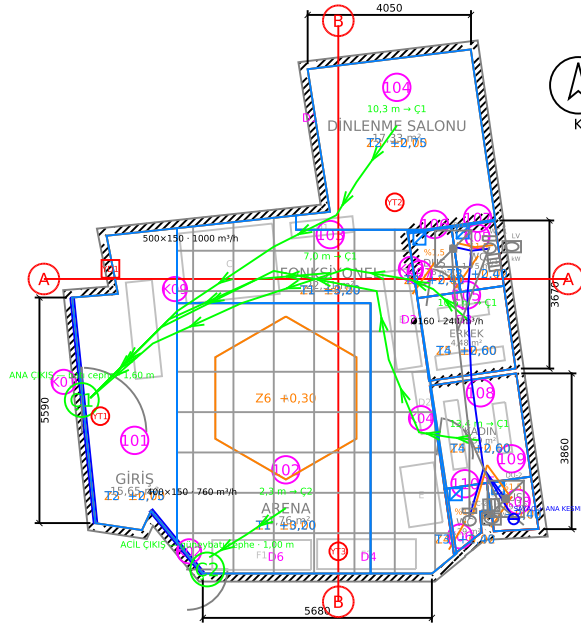

PROJE

MALTEPE / İDEALTEPE — GYM DÖNÜŞÜMÜ

DISİPLİN

MEKANİK TESİSAT

PAFTA ADI
SİHHİ TESİSAT PLANI

PAFTA NO
M-03

ÖLÇEK
1/75

TARİH
17 Eylül 2026

REVİZYON
Rev E

BİRİM
milimetre (mm)

DURUM
ÖN TASARIM

Yerinde doğrulanmadan ve ruhsat alınmadan uygulama yapılamaz.


LEJANT

- Mimari — mevcut duvar (korunuyor)
- Mimari — yeni alçıpan bölme
- Mekanik — taze hava kanalı
- Mekanik — egzoz kanalı
- Mekanik — ıslak hacim egzoz kanalı
- Mekanik — menfez ve valf
- Mekanik — menfez bransmanı
- Mekanik — fan ve panjur
- Mekanik — klima iç ünite
- Mekanik — klima dış ünite platformu
- Mekanik — soğutucu akışkan bakır hattı
- Mekanik — klima drenaj hattı
- Mekanik — temiz su PPRC
- Mekanik — sıcak su PPRC izoleli
- Mekanik — pis su PVC
- Mekanik — vitrifiye ve su ısıtıcı
- Mekanik — etiket ve not

NOTLAR

Mekanik disiplin genel yerleşimi.

Ayrıntı için M-01, M-02, M-03 paftaları.

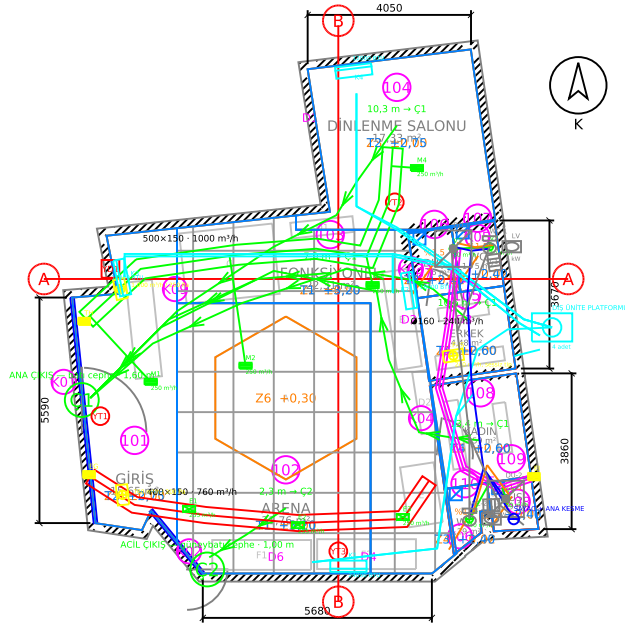

PROJE

MALTEPE / İDEALTEPE — GYM DÖNÜŞÜMÜ

DISİPLİN

MEKANİK TESİSAT

PAFTA ADI

MEKANİK GENEL YERLEŞİM

PAFTA NO
M-04

ÖLÇEK
1/75

TARİH
17 Eylül 2026

REVİZYON
Rev E

BİRİM
milimetre (mm)

DURUM
ÖN TASARIM


Yerinde doğrulanmadan ve ruhsat alınmadan uygulama yapılamaz.

LEJANT

- Mimari — mevcut duvar (korunuyor)
- Mimari — yeni alçıpan bölme
- Elektrik — priz
- Elektrik — klima/sıtıcı/fan beslemesi
- Elektrik — ana dağıtım panosu
- Elektrik — etiket ve not

NOTLAR

Islak hacim linyeleri ayrı 30 mA
kacak akım rolesinden beslenir.
Kardiyo ekipmanı ayrı linyede (P4).

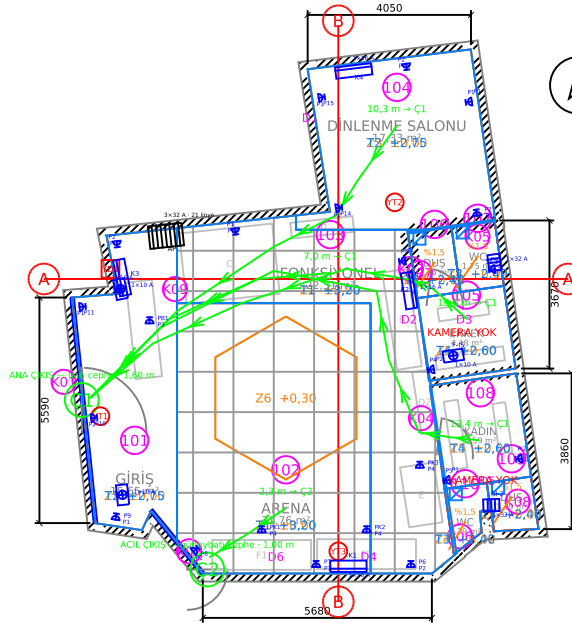

PROJE

MALTEPE / İDEALTEPE — GYM DÖNÜŞÜMÜ

DISİPLİN
ELEKTRİK

PAFTA ADI
PRİZ VE KUVVET PLANI

PAFTA NO
E-02

ÖLÇEK
1/75


TARİH
17 Eylül 2026

REVİZYON
Rev E

BİRİM
milimetre (mm)

DURUM
ÖN TASARIM

Yerinde doğrulanmadan ve ruhsat alınmadan uygulama yapılamaz.

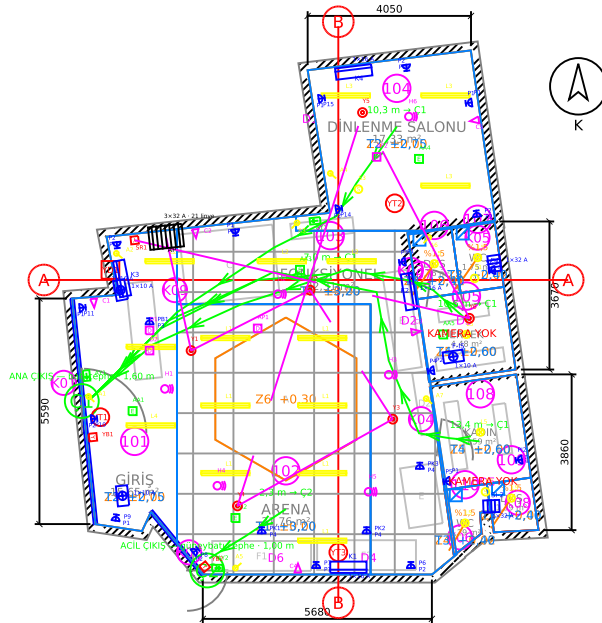

LEJANT

- Mimari — mevcut duvar (korunuyor)
- Mimari — yeni alçıpan bölme
- Elektrik — lineer LED armatür
- Elektrik — IP44 downlight
- Elektrik — acil aydınlatma / yönlendirme
- Elektrik — anahtar ve sensör
- Elektrik — priz
- Elektrik — klima/sıtıcı/fan beslemesi
- Elektrik — IP kamera
- Elektrik — tavan hoparlörü
- Elektrik — veri prizi ve rack
- Elektrik — dedektör, buton, siren
- Elektrik — yangın algılama çevrimi
- Elektrik — ana dağıtım panosu
- Elektrik — etiket ve not

NOTLAR

Elektrik disiplin genel yerleşimi.

Ayrıntı için E-01, E-02, E-03 paftaları.

PROJE

MALTEPE / İDEALTEPE — GYM DÖNÜŞÜMÜ

DISİPLİN
ELEKTRİK

PAFTA ADI
ELEKTRİK GENEL YERLEŞİM

PAFTA NO
E-04

ÖLÇEK
1/75

TARİH
17 Eylül 2026

REVİZYON
Rev E

BİRİM
milimetre (mm)

DURUM
ÖN TASARIM

Yerinde doğrulanmadan ve ruhsat alınmadan uygulama yapılamaz.