


LEJANT

- Mimari — mevcut duvar (korunuyor)
— Mimari — yeni alçıpan bölme
— Mimari — cephe doğraması
— Mimari — kapı ve açılım
— Mimari — spor ekipmanı (işverence temin)
— Mimari — sabit mobilya
— Mimari — mahal adı ve alan

GENEL NOTLAR

1. Mimari altlık — mevcut duvar korunur.
2. Kırmızı: yeni alçıpan bölme.
3. Ölçüler raster paftadan (+/-%3).

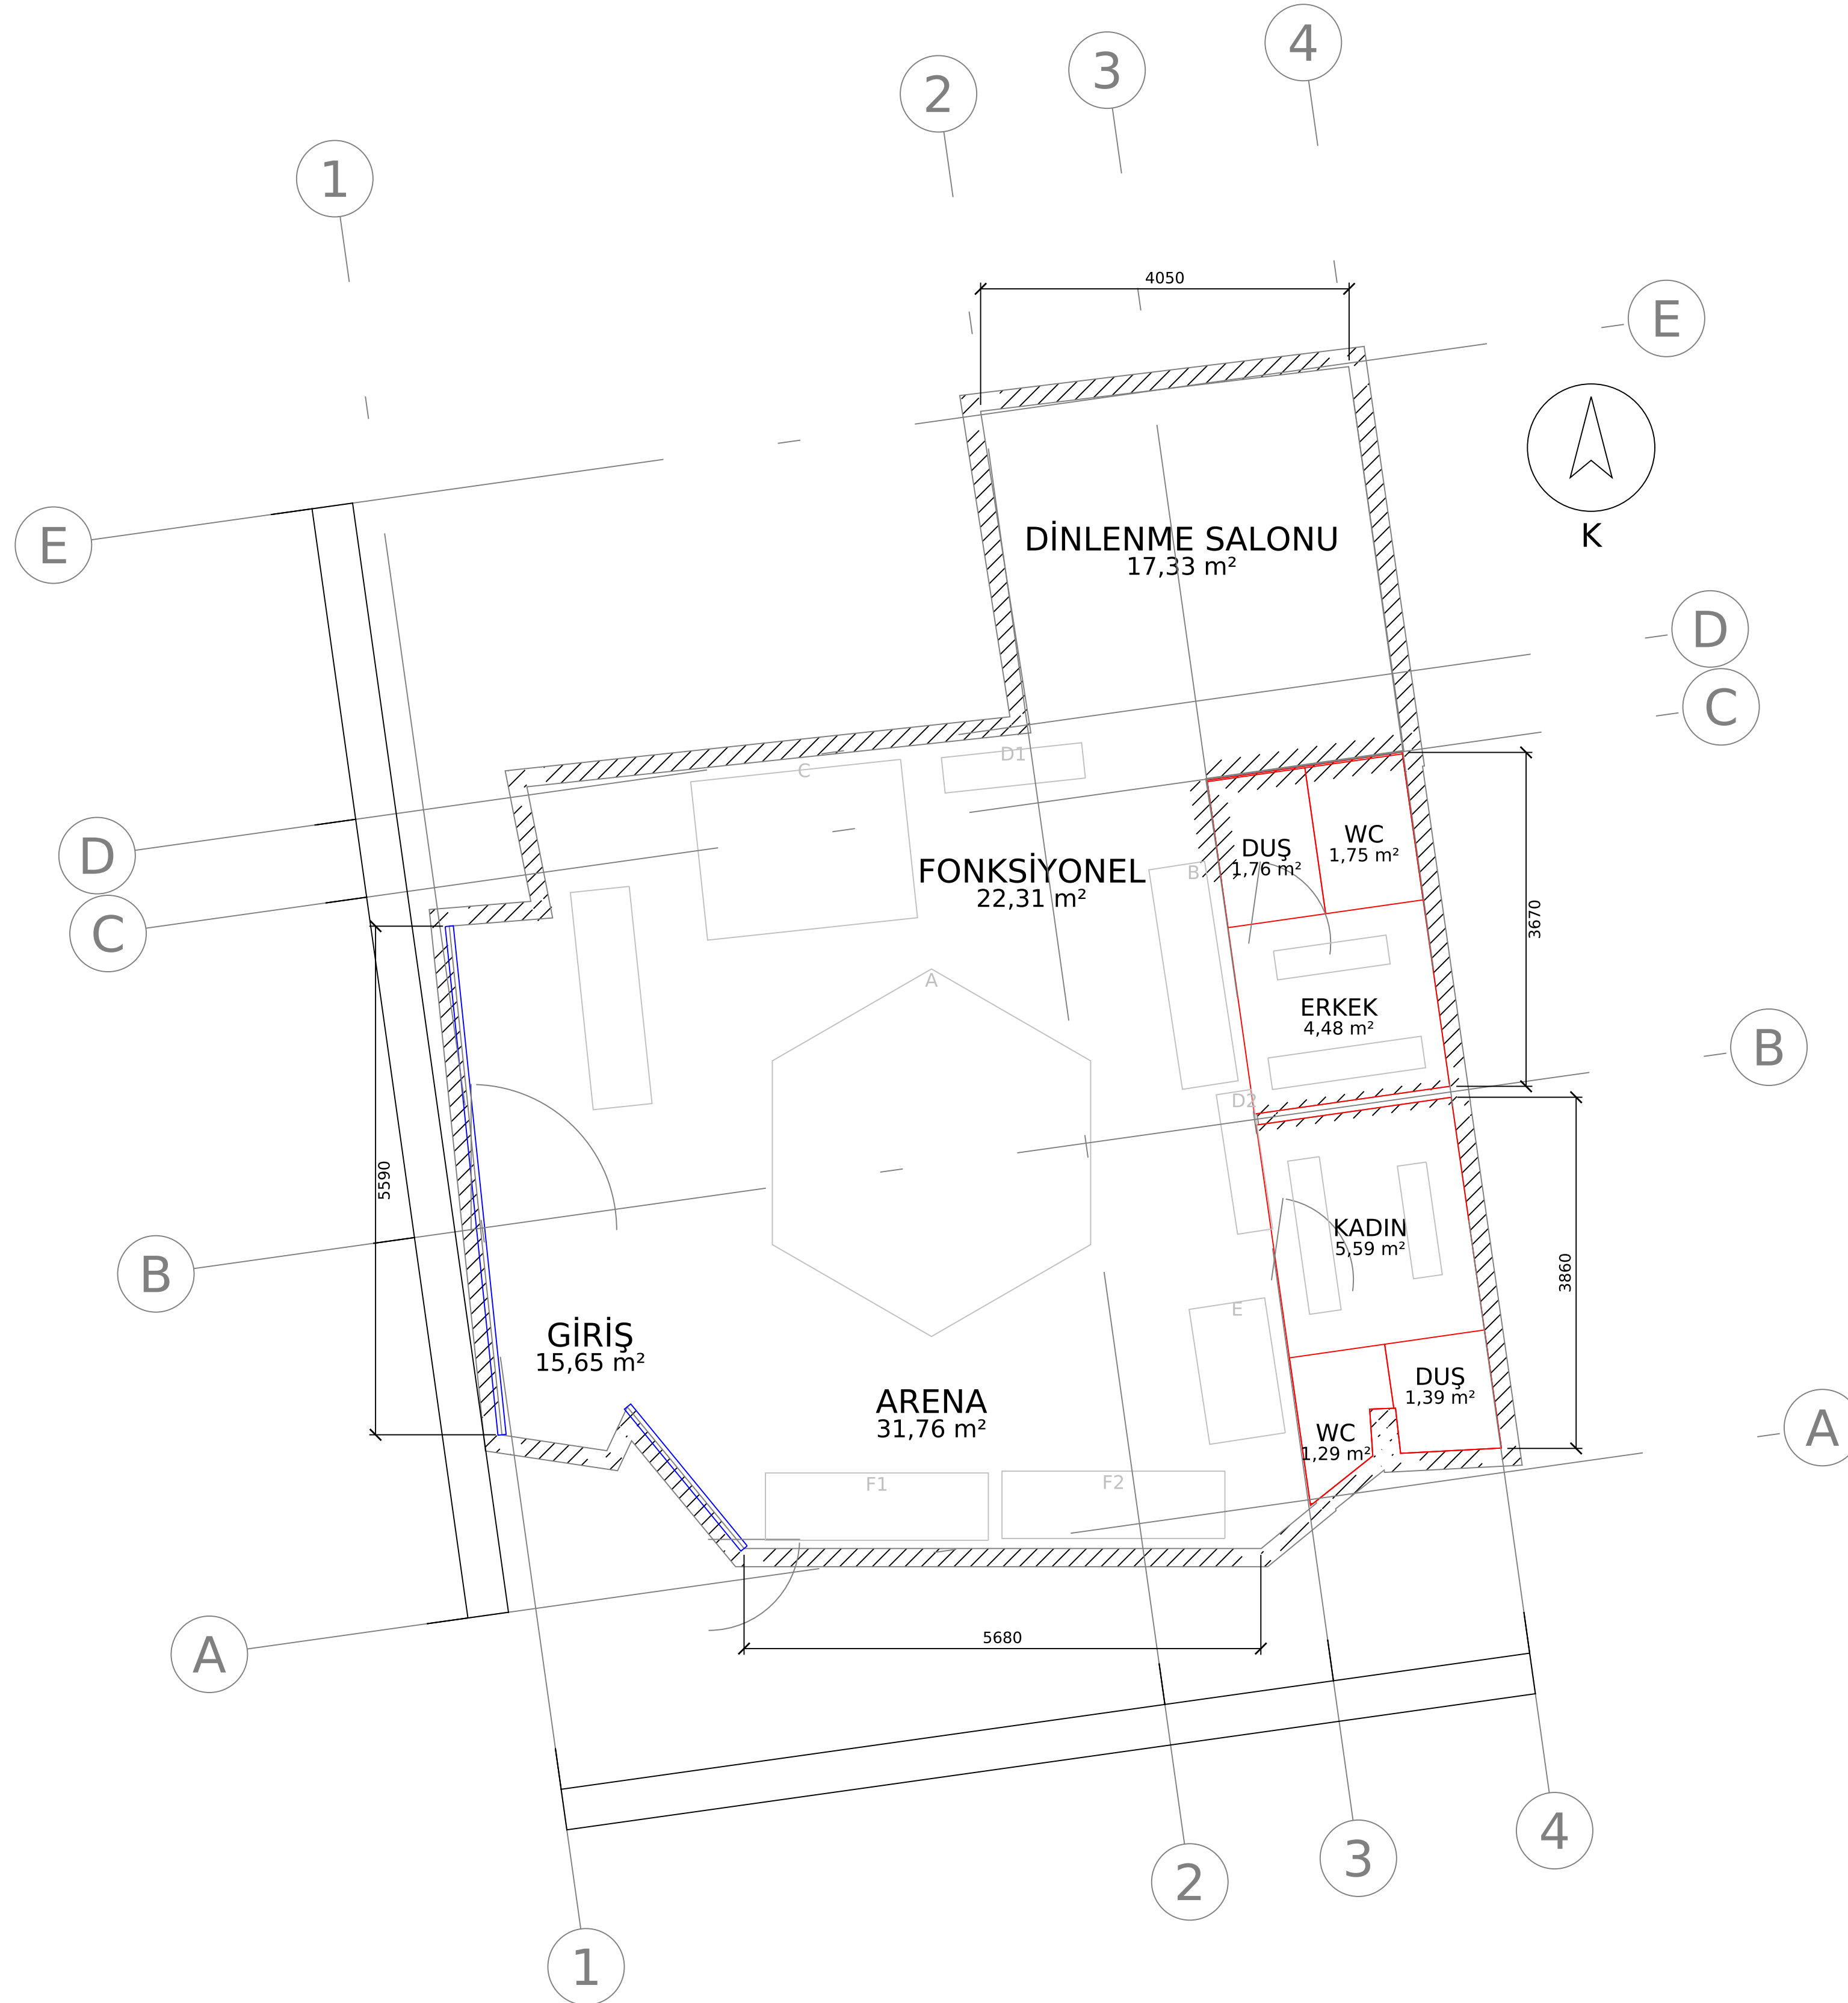

REV	TARİH	AÇIKLAMA	CZ	KT	ON
A	17.09.2026	İlk yayın — ön tasarım	CC	—	—
B	18.09.2026	Aks sistemi, zincir ölçü, ISO 5457/7200 pafta	CC	—	—
C	18.09.2026	A1 pafta, tekil DXF, ADP tek hat şeması CAD'de	CC	—	—

İŞVEREN ÖZEL — MALTEPE / IDEALTEPE					
PROJE MOBİLYA MAĞAZASI → FONKSİYONEL ANTRENMAN STÜDYOSU					
YAPI / MAHAL İdealtepe Mah. · zemin kat dükkân · 103,78 m² iç alan			DİSİPLİN MİMARİ		
PAFTA ADI MİMARİ ALTLIK			Mevcut durum · ölçü ve aks sistemi		
PROJE MÜELLİFİ · ODA SİCİL NO — Oda sicil no: —					
ÇİZEN CC		KONTROL —		ONAY —	
TARİH 17 Eylül 2026		ÖLÇEK 1:50		BİRİM milimetre (mm)	
DURUM ÖN TASARIM		PAFTA NO A-01		REV G	
				SONRAKİ: A-02	

LEJANT

- Mimari — mevcut duvar (korunuyor)
- Mimari — yeni alçıpan bölme
- Mimari — cephe doğraması
- Mimari — kapı ve açılım
- Mimari — spor ekipmanı (işverence temin)
- Mimari — sabit mobilya
- Mimari — mahal adı ve alan
- Mimari — mahal numarası ve kapı kodu balonu
- Mimari — kesit ve görünüş hattı

GENEL NOTLAR

- Mahal no, kapı kodu, duvar tipi ve
- kesit hattı gösterilmiştir.
- Tüm alçıpan bölmeler yapısal döseme
- altına (+3.20) kadar yükselir.


ÖLÇEK 1:50
0 1 2 3 4 5 m

ÖN TASARIM — UYGULAMA İÇİN DEĞİLDİR

100 mm

REV	TARİH	AÇIKLAMA	CZ	KT	ON
A	17.09.2026	İlk yayın — ön tasarım	CC	—	—
B	18.09.2026	Aks sistemi, zincir ölçü, ISO 5457/7200 pafta	CC	—	—
C	18.09.2026	A1 pafta, tekil DXF, ADP tek hat şeması CAD'de	CC	—	—

İŞVEREN ÖZEL — MALTEPE / IDEALTEPE					
PROJE MOBİLYA MAĞAZASI → FONKSİYONEL ANTRENMAN STÜDYOSU					
YAPI / MAHAL İdealtepe Mah. · zemin kat dükkân · 103,78 m² iç alan			DISIPLİN MİMARİ		
PAFTA ADI MİMARİ UYGULAMA PLANI			Bölme duvarlar · kapılar · mahal numaraları		
PROJE MÜELLİFİ · ODA SİCİL NO — Oda sicil no: —					
ÇİZEN CC		KONTROL —	ONAY —		A
TARİH 17 Eylül 2026		ÖLÇEK 1:50	BİRİM milimetre (mm)		
DURUM ÖN TASARIM		PAFTA NO A-02	REV G		SONRAKİ: A-03

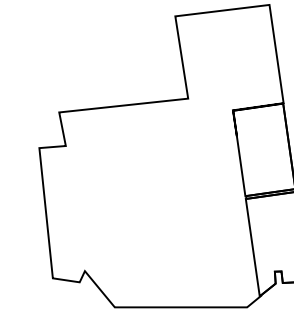

LEJANT

- Mimari — mevcut duvar (korunuyor)
- Mimari — yeni alçıpan bölme
- Mimari — cephe doğraması
- Mimari — kapı ve açılım
- Mimari — mahal numarası ve kapı kodu balonu
- Mimari — zemin kaplama tipi sınırı
- Mimari — zemin kaplama tipi ve kotu
- Mimari — kauçuk karo derz ızgarası

GENEL NOTLAR

- Bitmiş zemin kotu tüm kuru hacimde
- +/-0,00; dus ve WC -0,02.
- Tesviye sapı kalınlıkları farklıdır
- (Z1:3 Z2:30 Z3:42 Z5:38 mm).
- Kaucuk karo derz 1000x1000 mm.


ÖLÇEK 1:50

0 1 2 3 4 5 m


ÖN TASARIM — UYGULAMA İÇİN DEĞİLDİR

REV	TARİH	AÇIKLAMA	CZ	KT	ON
A	17.09.2026	İlk yayın — ön tasarım	CC	—	—
B	18.09.2026	Aks sistemi, zincir ölçü, ISO 5457/7200 pafta	CC	—	—
C	18.09.2026	A1 pafta, tekil DXF, ADP tek hat şeması CAD'de	CC	—	—
İŞVEREN					
ÖZEL — MALTEPE / IDEALTEPE					
PROJE					
MOBİLYA MAĞAZASI → FONKSİYONEL ANTRENMAN STÜDYOSU					
YAPI / MAHAL			DİSİPLİN		
İdealtepe Mah. · zemin kat dükkân · 103,78 m² iç alan			MİMARİ		
PAFTA ADI			Kaplama tipleri · kot · derz yönü		
ZEMİN KAPLAMA PLANI					
PROJE MÜELLİFİ · ODA SİCİL NO					
— Oda sicil no: —					
ÇİZEN		KONTROL		ONAY	
CC		—		—	
TARİH		ÖLÇEK		BİRİM	
17 Eylül 2026		1:50		milimetre (mm)	
DURUM		PAFTA NO		REV	
ÖN TASARIM		A-03		G	
SONRAKİ: A-04					

ÖLÇÜ ALINMAZ — YAZILI ÖLÇÜLER GEÇERLİDİR

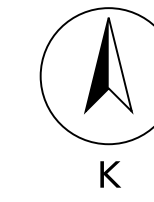

ANAHTAR PLAN

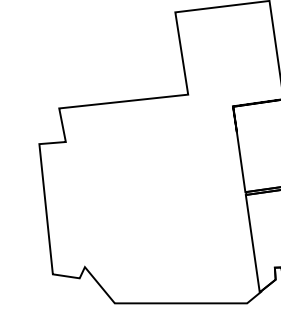

LEJANT

- Mimari — mevcut duvar (korunuyor)
- Mimari — yeni alçıpan bölme
- Mimari — cephe doğraması
- Mimari — kapı ve açılım
- Mimari — sabit mobilya
- Mimari — asma tavan tipi sınırı
- Mimari — asma tavan tipi ve kotu
- Mimari — revizyon kapağı 300x300
- Mekanik — taze hava kanalı
- Mekanik — egzoz kanalı
- Mekanik — ıslak hacim egzoz kanalı
- Mekanik — menfez ve valf
- Mekanik — menfez bransmanı
- Mekanik — fan ve panjur
- Mekanik — etiket ve not
- Elektrik — lineer LED armatür
- Elektrik — IP44 downlight
- Elektrik — acil aydınlatma / yönlendirme
- Elektrik — anahtar ve sensör
- Elektrik — aydınlatma lineyesi (ortogonal)
- Elektrik — anahtar kumanda sortisi
- Elektrik — ana dağıtım panosu
- Elektrik — etiket ve not


GENEL NOTLAR

- T1 açık tavan +3,20 · T2 +2,75
- T4 +2,60 · T3 +2,40.
- Tesisat askisi alçıpan karkasına
- asılmaz; ayrı askılanır.
- Her ıslak hacimde 300x300 revizyon.

ÖLÇEK 1:50
0 1 2 3 4 5 m

ÖN TASARIM — UYGULAMA İÇİN DEĞİLDİR

100 mm

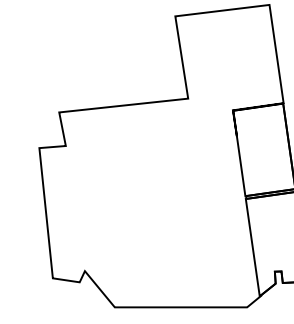


LEJANT

- Mimari — mevcut duvar (korunuyor)
- Mimari — yeni açılan bölme
- Mimari — cephe doğraması
- Mimari — kapı ve açılım
- Mimari — sabit mobilya
- Mimari — mahal adı ve alan
- Mimari — kaçış yolu ve çıkış
- Mimari — söndürücü, dolap, ihbar

GENEL NOTLAR

- İki bağımsız çıkış: Ç1 1,60 m, Ç2 1,00 m.
- En uzun kaçış yolu 13,4 m.
- Kaçış kapıları kaçış yönünde açılır.
- panik donanımlı, kilitsiz.

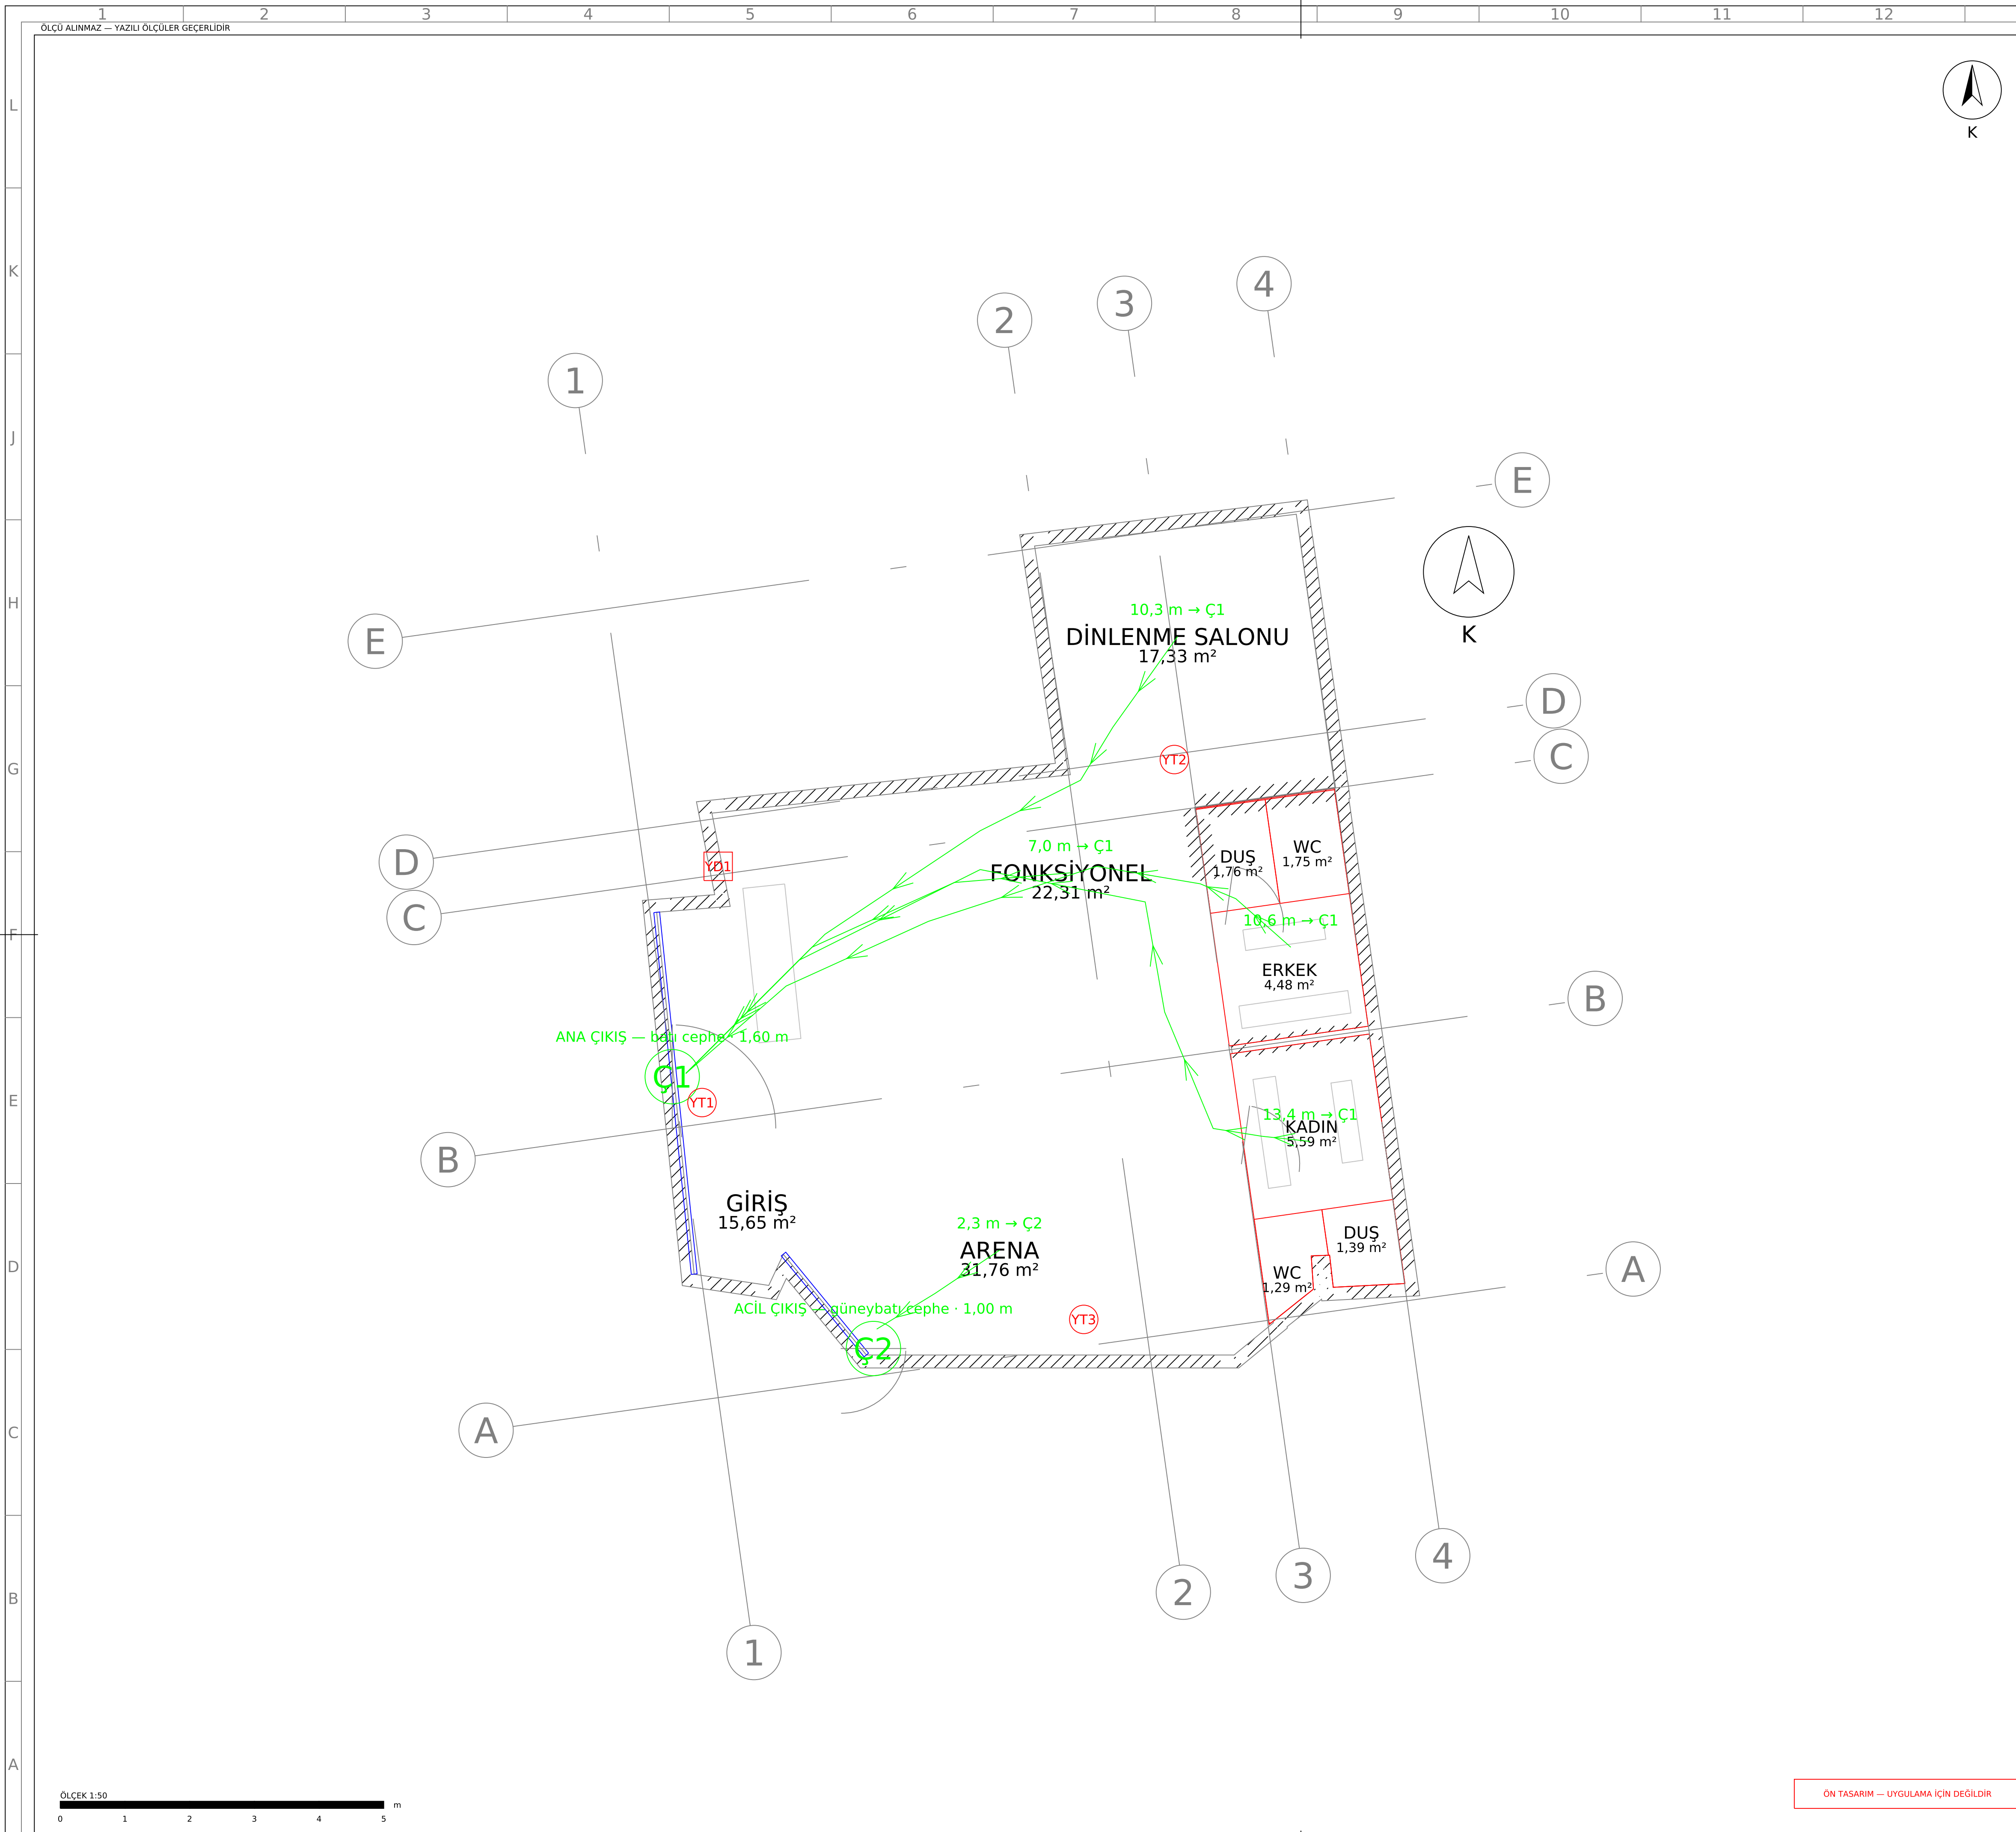

REV	TARİH	AÇIKLAMA	ÇZ	KT	ON
A	17.09.2026	İlk yayın — ön tasarım	CC	—	—
B	18.09.2026	Aks sistemi, zincir ölçü, ISO 5457/7200 pafta	CC	—	—
C	18.09.2026	A1 pafta, tekil DXF, ADP tek hat şeması CAD'de	CC	—	—

İŞVEREN ÖZEL — MALTEPE / IDEALTEPE					
PROJE MOBİLYA MAĞAZASI → FONKSİYONEL ANTRENMAN STÜDYOSU					
YAPI / MAHAL İdealtepe Mah. · zemin kat dükkân · 103,78 m² iç alan			DİSİPLİN MİMARİ		
PAFTA ADI YANGIN VE TAHLİYE PLANI			Kaçış yolları · çıkışlar · söndürücü		
PROJE MÜELLİFİ · ODA SİCİL NO — Oda sicil no: —					
ÇİZEN CC		KONTROL —	ONAY —		A
TARİH 17 Eylül 2026		ÖLÇEK 1:50	BİRİM milimetre (mm)		
DURUM ÖN TASARIM		PAFTA NO A-05	REV G		SONRAKİ: M-01

ÖN TASARIM — UYGULAMA İÇİN DEĞİLDİR

LEJANT

- Mimari — mevcut duvar (korunuyor)
— Mimari — yeni alçıpan bölme
— Mimari — cephe doğraması
— Mimari — kapı ve açılım
— Mimari — spor ekipmanı (isiverence temini)
— Mimari — sabit mobilya
— Mimari — mahal adı ve alan
— Mekanik — taze hava kanalı
— Mekanik — egzoz kanalı
— Mekanik — ıslak hacim egzoz kanalı
— Mekanik — menfez ve valf
— Mekanik — menfez bransmanı
— Mekanik — fan ve panjur
— Mekanik — etiket ve not

GENEL NOTLAR

1. Kanallar galvaniz sac, TS EN 1507 sınıf B.
2. Besleme ve egzoz hattı 19 mm izoleli.
3. Her bransman bası debi ayar damperli.
4. Devreye almada balanslama ve ölçüm raporu.

DİNLENME SALONU
17,33 m²

FONKSİYONEL
22,31 m²

DÜŞ
1,75 m²

ERKEK
4,48 m²

KADIN
5,59 m²

GİRİŞ
15,65 m²

ARENA
31,76 m²

WC
1,29 m²

DÜŞ
1,39 m²

ÖLÇEK 1:50
0 1 2 3 4 5 m

ÖN TASARIM — UYGULAMA İÇİN DEĞİLDİR

REV	TARİH	AÇIKLAMA	CZ	KT	ON
A	17.09.2026	İlk yayın — ön tasarım	CC	—	—
B	18.09.2026	Aks sistemi, zincir ölçü, ISO 5457/7200 pafta	CC	—	—
C	18.09.2026	A1 pafta, tekil DXF, ADP tek hat şeması CAD'de	CC	—	—


İŞVEREN ÖZEL — MALTEPE / IDEALTEPE PROJE MOBİLYA MAĞAZASI → FONKSİYONEL ANTRENMAN STÜDYOSU					
YAPI / MAHAL İdealtepe Mah. · zemin kat dükkân · 103,78 m ² iç alan			DİSİPLİN MEKANİK TESİSAT		
PAFTA ADI HAVALANDIRMA PLANI			Kanal güzergâhı · menfez debileri		
PROJE MÜELLİFİ · ODA SİCİL NO — Oda sicil no: —					
ÇİZEN CC		KONTROL —	ONAY —		A
TARİH 17 Eylül 2026		ÖLÇEK 1:50	BİRİM milimetre (mm)		
DURUM ÖN TASARIM		PAFTA NO M-01	REV G		SONRAKİ: M-02

LEJANT

- Mimari — mevcut duvar (korunuyor)
- Mimari — yeni alçıpan bölme
- Mimari — cephe doğraması
- Mimari — kapı ve açılım
- Mimari — spor ekipmanı (işverence temin)
- Mimari — sabit mobilya
- Mimari — mahal adı ve alan
- Mekanik — klima iç ünite
- Mekanik — klima dış ünite platformu
- Mekanik — soğutucu akışkan bakır hattı
- Mekanik — klima drenaj hattı

GENEL NOTLAR

- İç ünite montaj kotu 2,40 m (altı kot).
- Bakır hat izoleli, dış ünite konsolu
- titresim takozlu.
- Drenaj %1 eğimli.

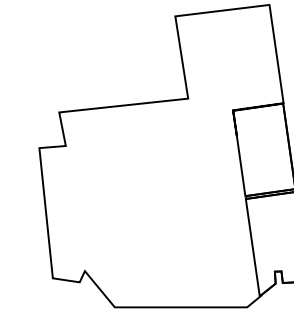

LEJANT

- Mimari — mevcut duvar (korunuyor)
- Mimari — yeni alçıpan bölme
- Mimari — cephe doğraması
- Mimari — kapı ve açılım
- Mimari — spor ekipmanı (işverence temin)
- Mimari — sabit mobilya
- Mimari — mahal adı ve alan
- Mekanik — temiz su PPRC
- Mekanik — sıcak su PPRC İzoleli
- Mekanik — pis su PVC
- Mekanik — vitriflye ve su ısıtıcı

GENEL NOTLAR

- Pis su %2 eğimli.
- Tüm ıslak hacimde sifonlu yer suzgeci.
- SOKUM SONRASI İLK İS: mevcut pis su
- bağlantı kotunun ölçülmesi.

ÖLÇEK 1:50

0 1 2 3 4 5 m

ÖN TASARIM — UYGULAMA İÇİN DEĞİLDİR

REV	TARİH	AÇIKLAMA	CZ	KT	ON
A	17.09.2026	İlk yayın — ön tasarım	CC	—	—
B	18.09.2026	Aks sistemi, zincir ölçü, ISO 5457/7200 pafta	CC	—	—
C	18.09.2026	A1 pafta, tekil DXF, ADP tek hat şeması CAD'de	CC	—	—

İŞVEREN ÖZEL — MALTEPE / IDEALTEPE					
PROJE MOBİLYA MAĞAZASI → FONKSİYONEL ANTRENMAN STÜDYOSU					
YAPI / MAHAL İdealtepe Mah. · zemin kat dükkân · 103,78 m ² iç alan			DİSİPLİN MEKANİK TESİSAT		
PAFTA ADI SİHHİ TESİSAT PLANI			Temiz su · sıcak su · pis su		
PROJE MÜELLİFİ · ODA SİCİL NO — Oda sicil no: —					
ÇİZEN CC		KONTROL —		ONAY —	
TARİH 17 Eylül 2026		ÖLÇEK 1:50		BİRİM milimetre (mm)	
DURUM ÖN TASARIM		PAFTA NO M-03		REV G	
				SONRAKİ: M-04	

LEJANT

- Mimari — mevcut duvar (korunuyor)
- Mimari — yeni alçıpan bölme
- Mimari — cephe doğraması
- Mimari — kapı ve açılım
- Mimari — spor ekipmanı (işverence temini)
- Mimari — sabit mobilya
- Mimari — mahal adı ve alan
- Mekanik — taze hava kanalı
- Mekanik — egzoz kanalı
- Mekanik — ıslak hacim egzoz kanalı
- Mekanik — menfez ve valf
- Mekanik — menfez bransmanı
- Mekanik — fan ve panjur
- Mekanik — klima iç ünite
- Mekanik — klima dış ünite platformu
- Mekanik — soğutucu akışkan bakır hattı
- Mekanik — klima drenaj hattı
- Mekanik — temiz su PPRC
- Mekanik — sıcak su PPRC izoleli
- Mekanik — pis su PVC
- Mekanik — vitrifiye ve su ısıtıcı
- Mekanik — etiket ve not

GENEL NOTLAR

- Mekanik disiplin genel yerleşimi.
- Ayrıntı için M-01, M-02, M-03 paftaları.

REV	TARİH	AÇIKLAMA	CZ	KT	ON
A	17.09.2026	İlk yayın — ön tasarım	CC	—	—
B	18.09.2026	Aks sistemi, zincir ölçü, ISO 5457/7200 pafta	CC	—	—
C	18.09.2026	A1 pafta, tekil DXF, ADP tek hat şeması CAD'de	CC	—	—

İŞVEREN	ÖZEL — MALTEPE / IDEALTEPE
PROJE	MOBİLYA MAĞAZASI → FONKSİYONEL ANTRENMAN STÜDYOSU
YAPI / MAHAL	İdealtepe Mah. · zemin kat dükkân · 103,78 m ² iç alan
PAFTA ADI	MEKANİK GENEL YERLEŞİM
PROJE MÜELLİFİ · ODA SİCİL NO	— Oda sicil no: —
ÇİZEN	CC
TARİH	17 Eylül 2026
DURUM	ÖN TASARIM
KONTROL	—
ÖLÇEK	1:50
PAFTA NO	M-04
ONAY	—
BİRİM	milimetre (mm)
REV	G
SONRAKİ: E-01	

LEJANT

- Mimari — mevcut duvar (korunuyor)
- Mimari — yeni alçıpan bölme
- Mimari — cephe doğraması
- Mimari — kapı ve açılım
- Mimari — spor ekipmanı (işverence temini)
- Mimari — sabit mobilya
- Mimari — mahal adı ve alan
- Elektrik — lineer LED armatür
- Elektrik — IP44 downlight
- Elektrik — acil aydınlatma / yönlendirme
- Elektrik — anahtar ve sensör
- Elektrik — aydınlatma linyesi (ortogonal)
- Elektrik — anahtar kumanda sortisi
- Elektrik — ana dağıtım panosu
- Elektrik — etiket ve not

GENEL NOTLAR

- Tesisat siva altı spiral boru içinde,
- NHXMH halojeniz kablo.
- Acil aydınlatma 3 saat bataryalı.

REV	TARİH	AÇIKLAMA	CZ	KT	ON
A	17.09.2026	İlk yayın — ön tasarım	CC	—	—
B	18.09.2026	Aks sistemi, zincir ölçü, ISO 5457/7200 pafta	CC	—	—
C	18.09.2026	A1 pafta, tekil DXF, ADP tek hat şeması CAD'de	CC	—	—

İŞVEREN ÖZEL — MALTEPE / İDEALTEPE			
PROJE MOBİLYA MAĞAZASI → FONKSİYONEL ANTRENMAN STÜDYOSU			
YAPI / MAHAL İdealtepe Mah. · zemin kat dükkân · 103,78 m ² iç alan		DİSİPLİN ELEKTRİK	
PAFTA ADI AYDINLATMA PLANI		Armatür · anahtar · aydınlatma linyeleri	
PROJE MÜELLİFİ · ODA SİCİL NO — Oda sicil no: —			
ÇİZEN CC	KONTROL —	ONAY —	
TARİH 17 Eylül 2026	ÖLÇEK 1:50	BİRİM milimetre (mm)	
DURUM ÖN TASARIM	PAFTA NO E-01	REV G	SONRAKİ: E-02

ÖLÇEK 1:50
0 1 2 3 4 5 m


ÖN TASARIM — UYGULAMA İÇİN DEĞİLDİR

LEJANT

- Mimari — mevcut duvar (korunuyor)
— Mimari — yeni alçıpan bölme
— Mimari — cephe doğraması
— Mimari — kapı ve açılım
— Mimari — spor ekipmanı (işverence temin)
— Mimari — sabit mobilya
— Mimari — mahal adı ve alan
— Elektrik — priz
— Elektrik — klima/sıtıcı/fan beslemesi
— Elektrik — priz ve kuvvet linyesi
— Elektrik — ana dağıtım panosu
— Elektrik — etiket ve not

GENEL NOTLAR

1. Islak hacim linyeleri ayrı 30 mA
2. kaçak akım rolesinden beslenir.
3. Kardiyo ekipmanı ayrı linyede (P4).

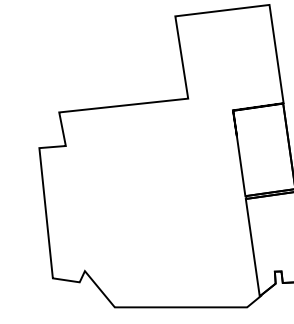

LEJANT

- Mimari — mevcut duvar (korunuyor)
- Mimari — yeni alçıpan bölme
- Mimari — cephe doğraması
- Mimari — kapı ve açılım
- Mimari — spor ekipmanı (işverence temin)
- Mimari — sabit mobilya
- Mimari — mahal adı ve alan
- Elektrik — IP kamera
- Elektrik — tavan hoparlörü
- Elektrik — veri prizi ve rack
- Elektrik — dedektör, buton, siren
- Elektrik — yangın algılama çevrimi
- Elektrik — zayıf akım kablo kanalı
- Elektrik — ana dağıtım panosu
- Elektrik — etiket ve not

GENEL NOTLAR

- SOYUNMA VE WC İÇİNE KAMERA KONULMAZ.
- Yangın algılama panosu kesintisiz beslenir.
- Topraklama direnci ≤ 10 ohm.

ÖLÇEK 1:50

0 1 2 3 4 5 m

ÖN TASARIM — UYGULAMA İÇİN DEĞİLDİR

REV	TARİH	AÇIKLAMA	CZ	KT	ON
A	17.09.2026	İlk yayın — ön tasarım	CC	—	—
B	18.09.2026	Aks sistemi, zincir ölçü, ISO 5457/7200 pafta	CC	—	—
C	18.09.2026	A1 pafta, tekil DXF, ADP tek hat şeması CAD'de	CC	—	—
İŞVEREN					
ÖZEL — MALTEPE / IDEALTEPE					
PROJE					
MOBİLYA MAĞAZASI → FONKSİYONEL ANTRENMAN STÜDYOSU					
YAPI / MAHAL			DİSİPLİN		
İdealtepe Mah. · zemin kat dükkân · 103,78 m² iç alan			ELEKTRİK		
PAFTA ADI			Veri · CCTV · ses · yangın algılama		
ZAYIF AKIM PLANI					
PROJE MÜELLİFİ · ODA SİCİL NO					
— Oda sicil no: —					
ÇİZEN	KONTROL		ONAY		
CC	—		—		
TARİH	ÖLÇEK		BİRİM		
17 Eylül 2026	1:50		milimetre (mm)		
DURUM	PAFTA NO		REV		
ÖN TASARIM	E-03		G		
			SONRAKİ: E-04		

LEJANT

- Mimari — mevcut duvar (korunuyor)
- Mimari — yeni alçıpan bölme
- Mimari — cephe doğraması
- Mimari — kapı ve açılım
- Mimari — spor ekipmanı (işverence temini)
- Mimari — sabit mobilya
- Mimari — mahal adı ve alan
- Elektrik — lineer LED armatür
- Elektrik — IP44 downlight
- Elektrik — acil aydınlatma / yönlendirme
- Elektrik — anahtar ve sensör
- Elektrik — priz
- Elektrik — klima/sıtıcı/fan beslemesi
- Elektrik — IP kamera
- Elektrik — tavan hoparlörü
- Elektrik — veri prizi ve rack
- Elektrik — dedektör, buton, siren
- Elektrik — yangın algılama çevrimi
- Elektrik — aydınlatma lineyesi (ortogonal)
- Elektrik — anahtar kumanda sortisi
- Elektrik — priz ve kuvvet lineyesi
- Elektrik — zayıf akım kablo kanalı
- Elektrik — ana dağıtım panosu
- Elektrik — etiket ve not


GENEL NOTLAR

- Elektrik disiplin genel yerleşimi.
- Ayrıntı için E-01, E-02, E-03 paftaları.

REV	TARİH	AÇIKLAMA	CZ	KT	ON
A	17.09.2026	İlk yayın — ön tasarım	CC	—	—
B	18.09.2026	Aks sistemi, zincir ölçü, ISO 5457/7200 pafta	CC	—	—
C	18.09.2026	A1 pafta, tekil DXF, ADP tek hat şeması CAD'de	CC	—	—

İŞVEREN ÖZEL — MALTEPE / IDEALTEPE					
PROJE MOBİLYA MAĞAZASI → FONKSİYONEL ANTRENMAN STÜDYOSU					
YAPI / MAHAL İdealtepe Mah. · zemin kat dükkân · 103,78 m ² iç alan			DISIPLIN ELEKTRİK		
PAFTA ADI ELEKTRİK GENEL YERLEŞİM			Elektrik disiplin genel yerleşimi		
PROJE MÜELLİFİ · ODA SİCİL NO — Oda sicil no: —					
ÇİZEN CC		KONTROL —	ONAY —		A
TARİH 17 Eylül 2026		ÖLÇEK 1:50	BİRİM milimetre (mm)		
DURUM ÖN TASARIM		PAFTA NO E-04	REV G		SONRAKİ: E-05

ÖN TASARIM — UYGULAMA İÇİN DEĞİLDİR

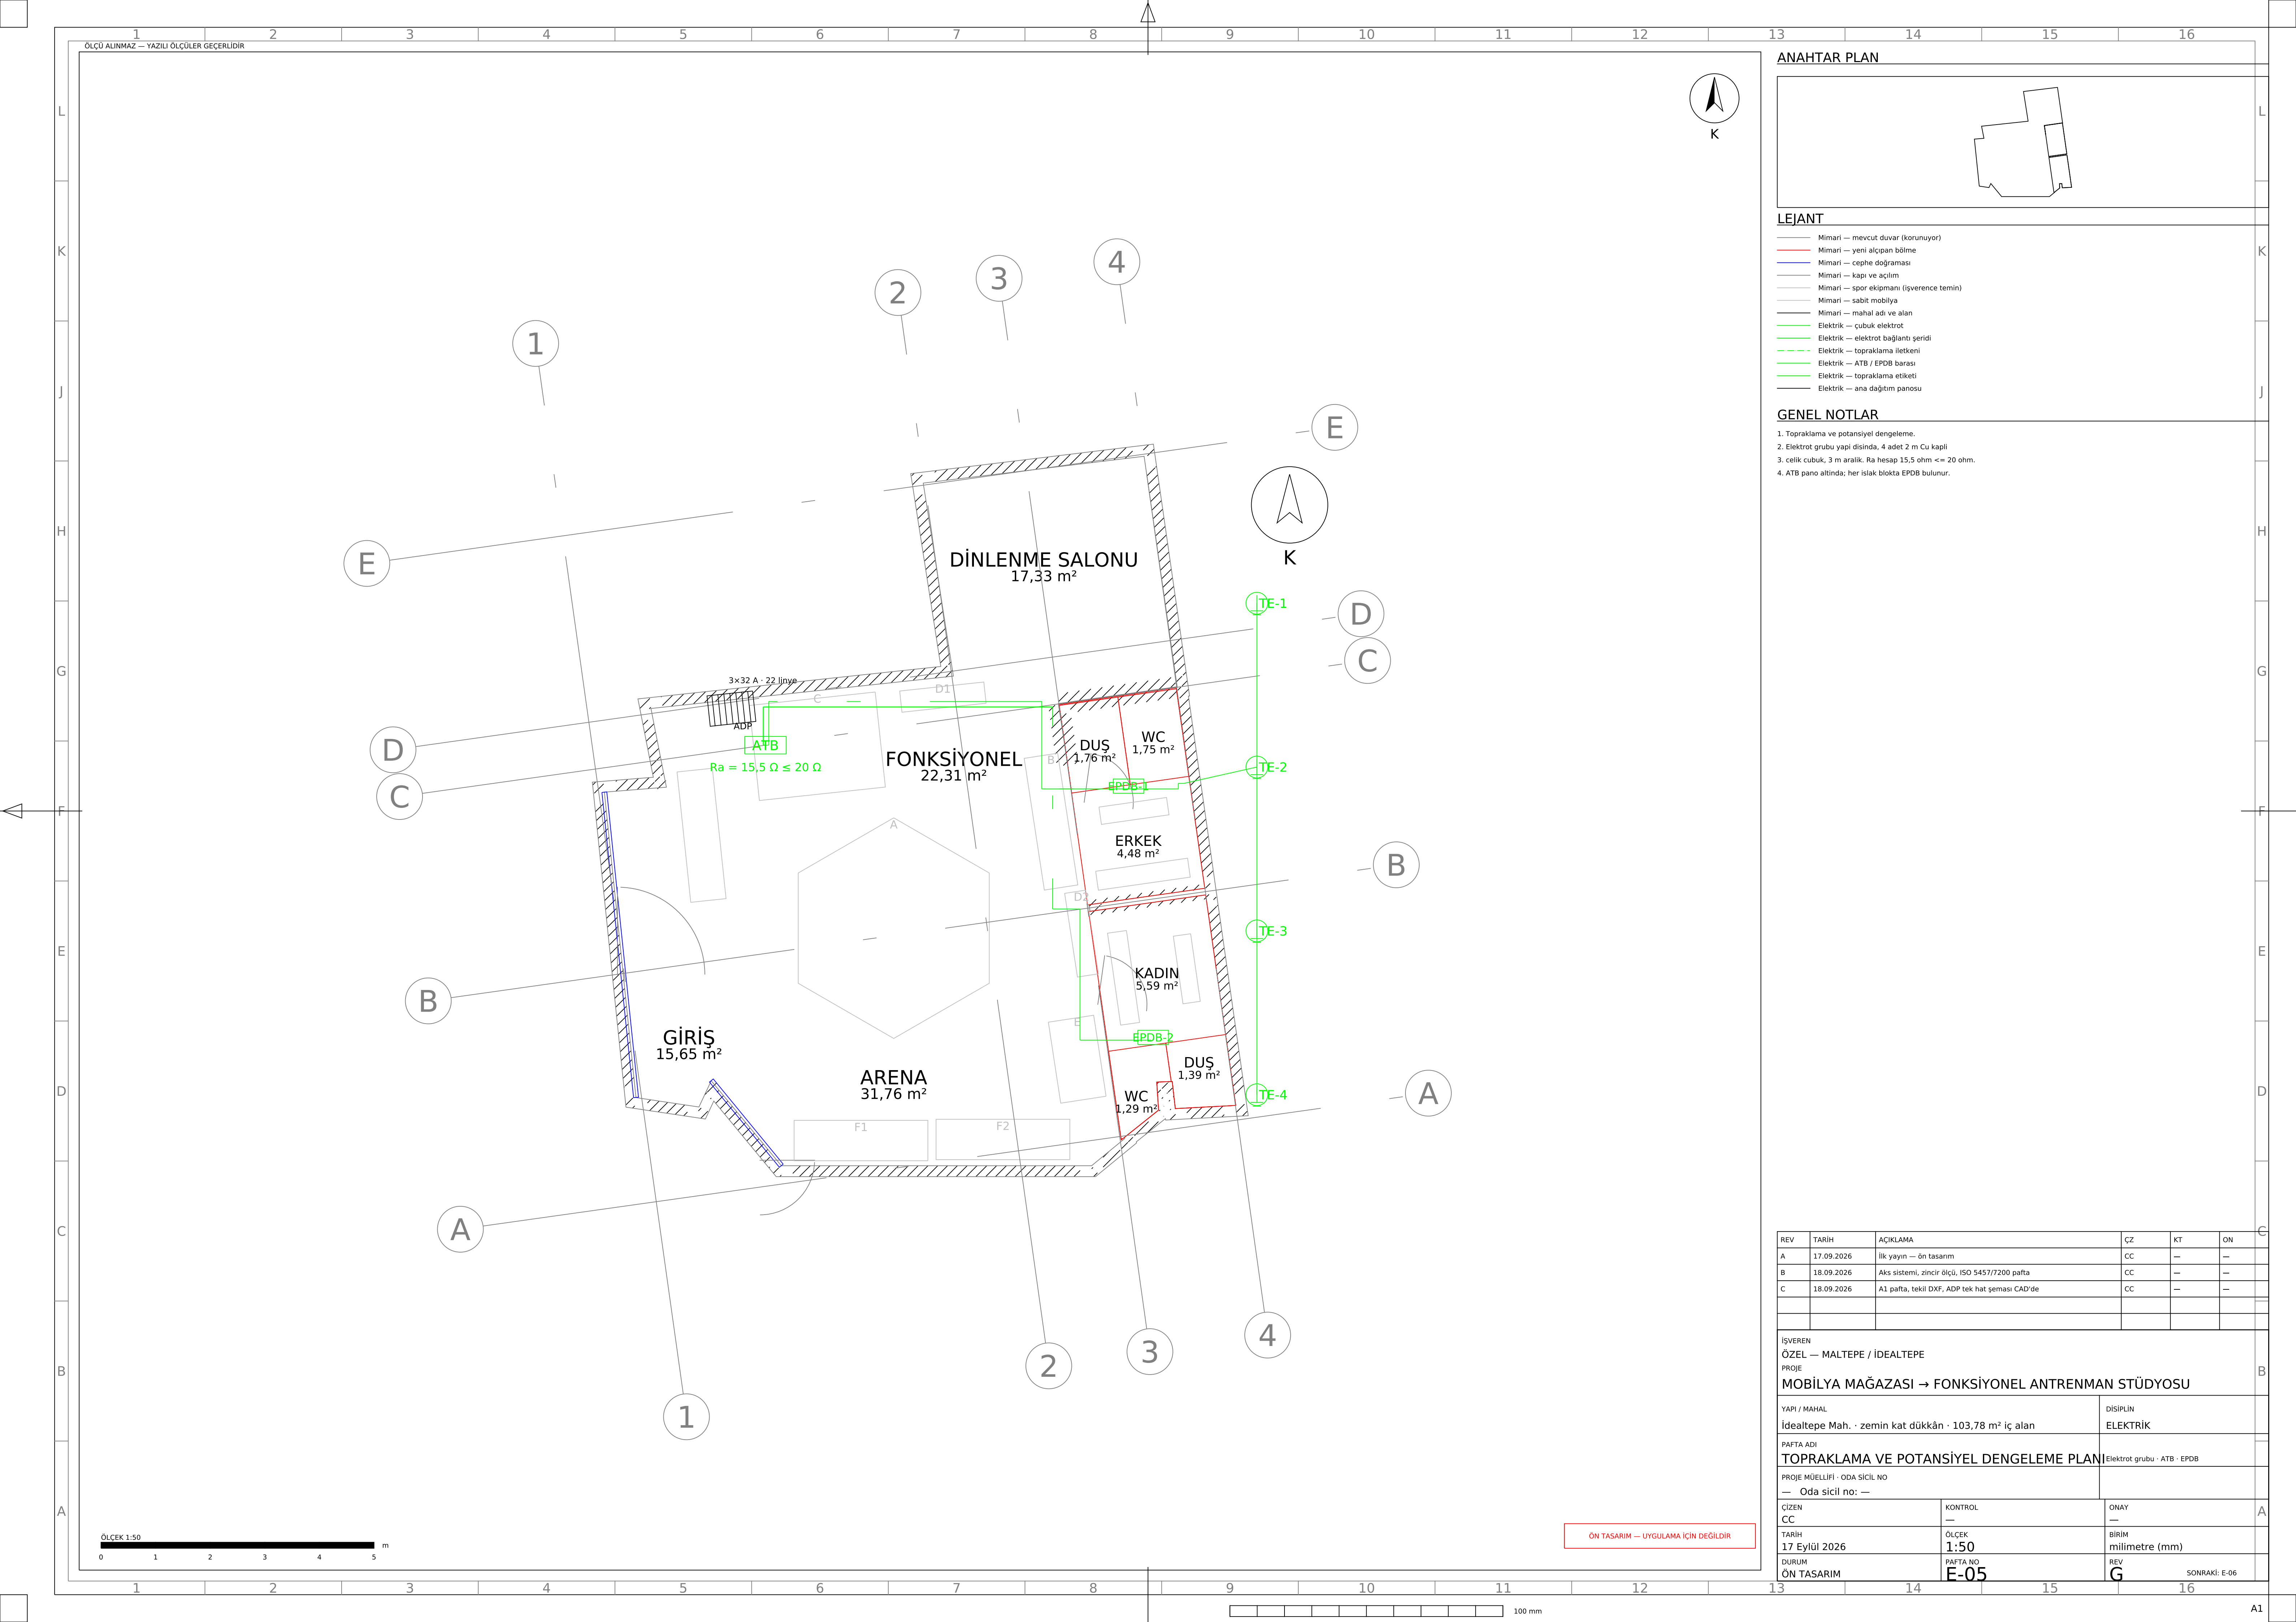

[illegible]

REV	TARİH	AÇIKLAMA	ÇZ	KT	ON
A	17.09.2026	İlk yayın — ön tasarıml	CC	—	—
B	18.09.2026	ACS sistemi, zincir 8/çu, ISO 5457/7200 pafta	CC	—	—
C	18.09.2026	A1 pafta, tekil DXF, ADP tek hat şeması CAD'de	CC	—	—

A1