

0

1

2

3

4

5

6

7

A

ADP — ANA DAĞITIM PANOSU

ÇOK HATLI ŞEMATİK DİYAGRAM SETİ / MULTI-LINE SCHEMATIC SET

Müşteri / Customer

Proje / Project

Pano / Panel

Proje No / Project No

Tarih / Date

Revizyon / Revision

Standartlar / Standards

ÖZEL — MALTEPE / İDEALTEPE

MOBİLYA MAĞAZASI → FONKSİYONEL ANTRENMAN STÜDYOSU

ADP

GYM-25-001-001

17 Eylül 2026

Rev H

IEC 61439-1&2 · IEC 60617 · IEC 81346-2 · TS HD 60364 · Elektrik İç Tesisleri Yönetmeliği

SAYFA İÇERİĞİ / SHEET INDEX

01

Cover Sheet / Kapak

02

Panel Characteristics / Pano Karakteristiği

03

Symbol List / Sembol Listesi

04

Incoming Supply / Ana Besleme

05

Schematic Diagram / Şematik Diyagram

06

Schematic Diagram / Şematik Diyagram

07

Schematic Diagram / Şematik Diyagram

08

Schematic Diagram / Şematik Diyagram

09

Terminal Diagram / Klemens Planı

10

Panel Overview / Pano Önden Görünüş

11

Load Schedule / Yükleme Cetveli

12

Parts List / Malzeme Listesi

Drawn By / Çizen

CC

Customer Name / Müşteri Adı

ÖZEL — MALTEPE / İDEALTEPE

Project Number / Proje Numarası

GYM-25-001-001

Sheet: / Sayfa

1

Checked By / Kontrol Eden

—

Project Description / Proje Açıklaması

MOBİLYA MAĞAZASI → FONKSİYONEL ANTRENMAN STÜDYOSU

Revision / Revizyon

Rev H

Total sheets: / Toplam

12

Approved By / Onaylayan

—

Panel Name / Pano Adı

ADP

Standards / Standartlar

IEC 61439-1&2 · IEC 60617

Sheet size / Kâğıt

A3

Project Date / Proje Tarihi

17 Eylül 2026

Page Description / Sayfa Açıklaması

Cover Sheet / Kapak

B



C


D

E


F

	0	1	2	3	4	5	6	7										
A	PANO KARAKTERİSTİK TABLOSU / PANEL CHARACTERISTICS STANDARTLAR / STANDARDS Tip testli pano / Type tested assembly IEC 61439-1 & IEC 61439-2 Semboller / Symbols IEC 60617 Referans işaretleri / Designations IEC 81346-2 Tesisat / Installation TS HD 60364 · Elektrik İç Tes. Yön. BESLEME / POWER SUPPLY Anma işletme gerilimi / Rated voltage 400/230 V 50 Hz Faz sayısı / Number of phases 3F + N + PE Nötr işletmesi / Neutral operation TN-S Anma akımı / Rated current 32 A Kısa devre dayanımı / Icw 6 kA 1 s Ana besleme kablosu / Main cable NYY 5×10 mm² · 25 m KORUMA / PROTECTION Ana şalter / Main switch 4×32 A Ana kaçak akım / Main RCD 4×40 A / 300 mA S tipi Son devre kaçak akım / Final RCD 30 mA A tipi Aşırı gerilim / SPD Tip 2 · Up 1,4 kV · In 20 kA Kesici eğrisi / MCB curve Aydınlatma B · Priz ve motor C · tümü 6 kA GÖVDE / ENCLOSURE Koruma sınıfı / Degree of protection IP 54 Ayrıştırma / Segregation Form 2b Gövde / Enclosure Sac · RAL 7035 Bara / Busbar Bakır · nötr tam kesit Montaj / Mounting Sabit · kapı arkası kumanda Etiketleme / Labelling PVC · Türkçe · vidalı ÖZET / SUMMARY Linye sayısı / Number of circuits 22 + 4 yedek Bağlı güç / Connected load 20,59 kW Talep gücü / Demand 14,63 kW Faz dengesizliği / Imbalance %1,0 Toplam ΔU / Total voltage drop %2,49 <td></td><td></td><td></td><td></td><td></td><td></td><td></td><td></td><td></td><td></td>																	

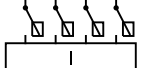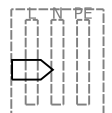
	0	1	2	3	4	5	6	7			
A	SEMBOL LİSTESİ / SYMBOL LIST — IEC 60617										
		-F	Otomatik sigorta, 1 kutup / MCB 1P								
		-F	Otomatik sigorta, 1F+N / MCB 1P+N								
B		-ID	Kaçak akım rölesi 2 kutup / RCD 2P								
		-ID	Kaçak akım rölesi 4 kutup / RCD 4P								
		-F0	Aşırı gerilim koruma Tip 2 / SPD Type 2								
C		-X	Klemens / Terminal								
		PE	Koruma topraklaması / Protective earth								
			Bağlantı noktası / Junction								
D		P	Saha cihazı ve kablo / Field device and cable								
			L1 L2 L3 N Potansiyel rayı / Potential rail								
			Sayfalar arası referans / Cross-page reference								
E											
F											
Drawn By / Çizen		CC	Customer Name / Müşteri Adı			ÖZEL — MALTEPE / İDEALTEPE	Project Number / Proje Numarası		GYM-25-001-001	Sheet: / Sayfa	3
Checked By / Kontrol Eden		—	Project Description / Proje Açıklaması			MOBİLYA MAĞAZASI → FONKSİYONEL ANTRENMAN STÜDYOSU				Next sheet: / Sonraki	4
Approved By / Onaylayan		—	Panel Name / Pano Adı			ADP	Revision / Revizyon		Rev H	Total sheets: / Toplam	12
Project Date / Proje Tarihi		17 Eylül 2026	Page Description / Sayfa Açıklaması			Symbol List / Sembol Listesi	Standards / Standartlar		IEC 61439-1&2 · IEC 60617	Sheet size / Kâğıt	A3

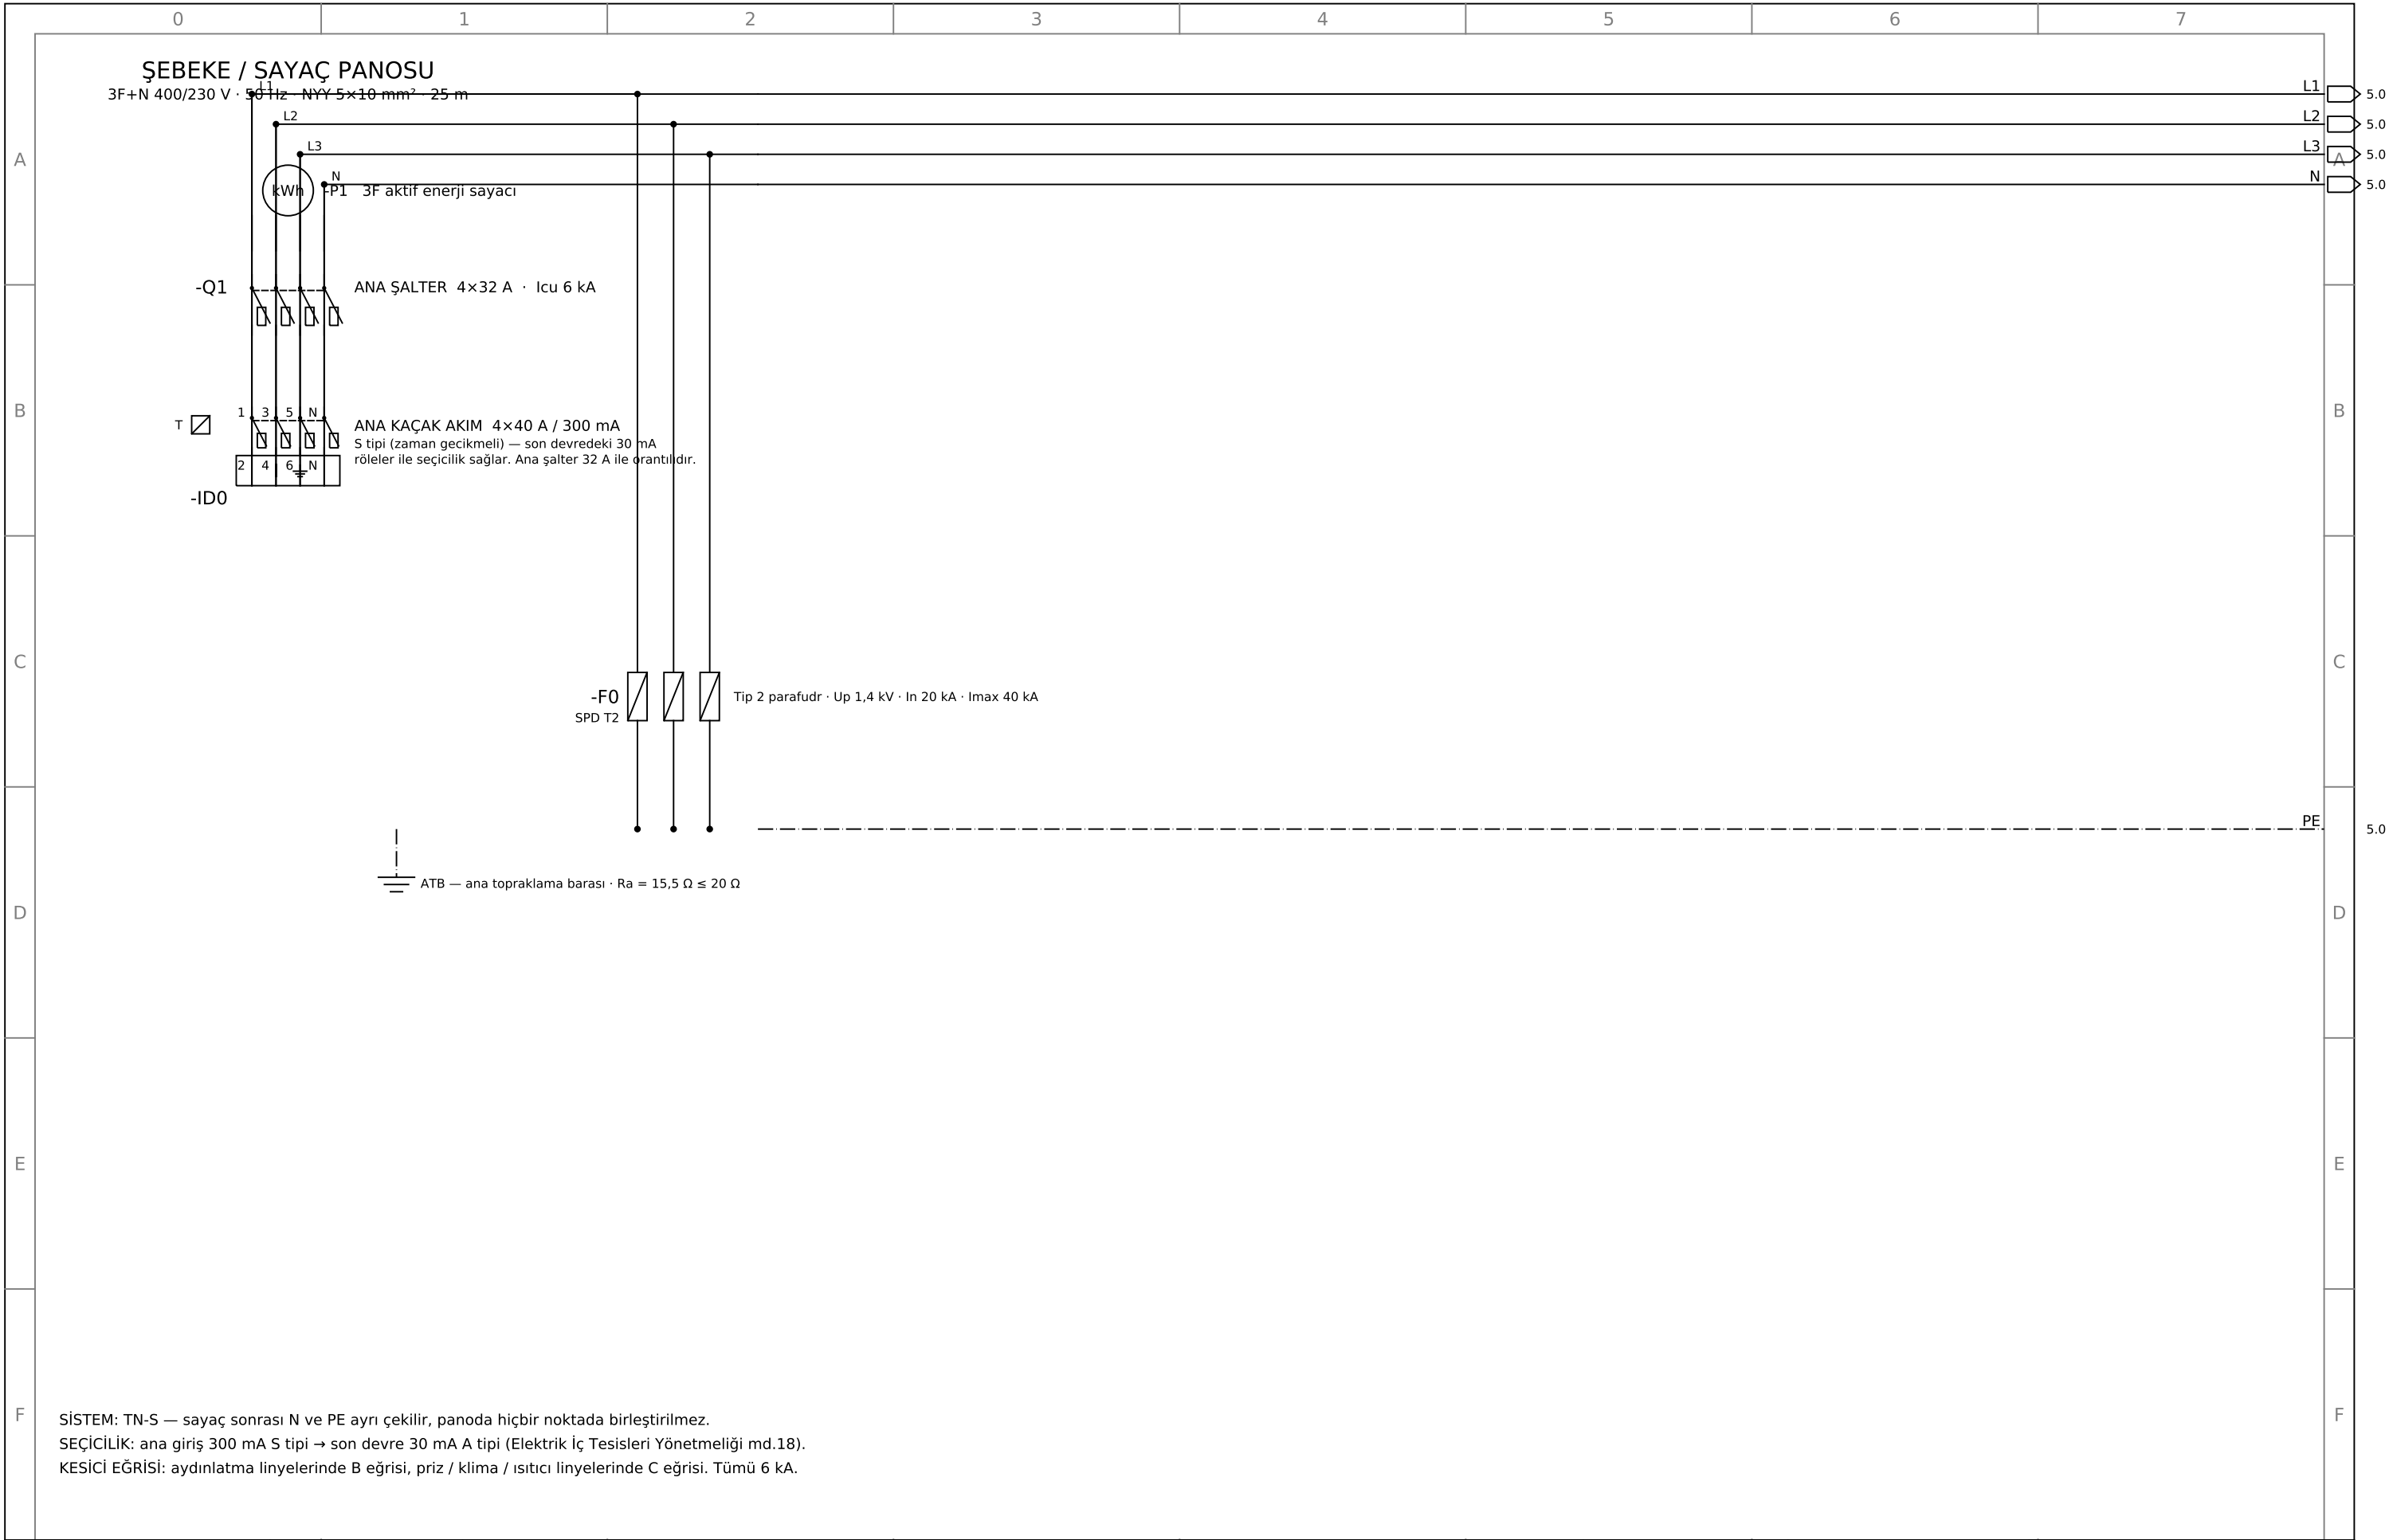


Drawn By / Çizen	CC	Customer Name / Müşteri Adı	ÖZEL — MALTEPE / İDEALTEPE	Project Number / Proje Numarası	GYM-25-001-001	Sheet: / Sayfa	4
Checked By / Kontrol Eden	—	Project Description / Proje Açıklaması	MOBİLYA MAĞAZASI → FONKSİYONEL ANTRENMAN STÜDYOSU			Next sheet: / Sonraki	5
Approved By / Onaylayan	—	Panel Name / Pano Adı	ADP	Revision / Revizyon	Rev H	Total sheets: / Toplam	12
Project Date / Proje Tarihi	17 Eylül 2026	Page Description / Sayfa Açıklaması	Incoming Supply / Ana Besleme	Standards / Standartlar	IEC 61439-1&2 · IEC 60617	Sheet size / Kâğıt	A3

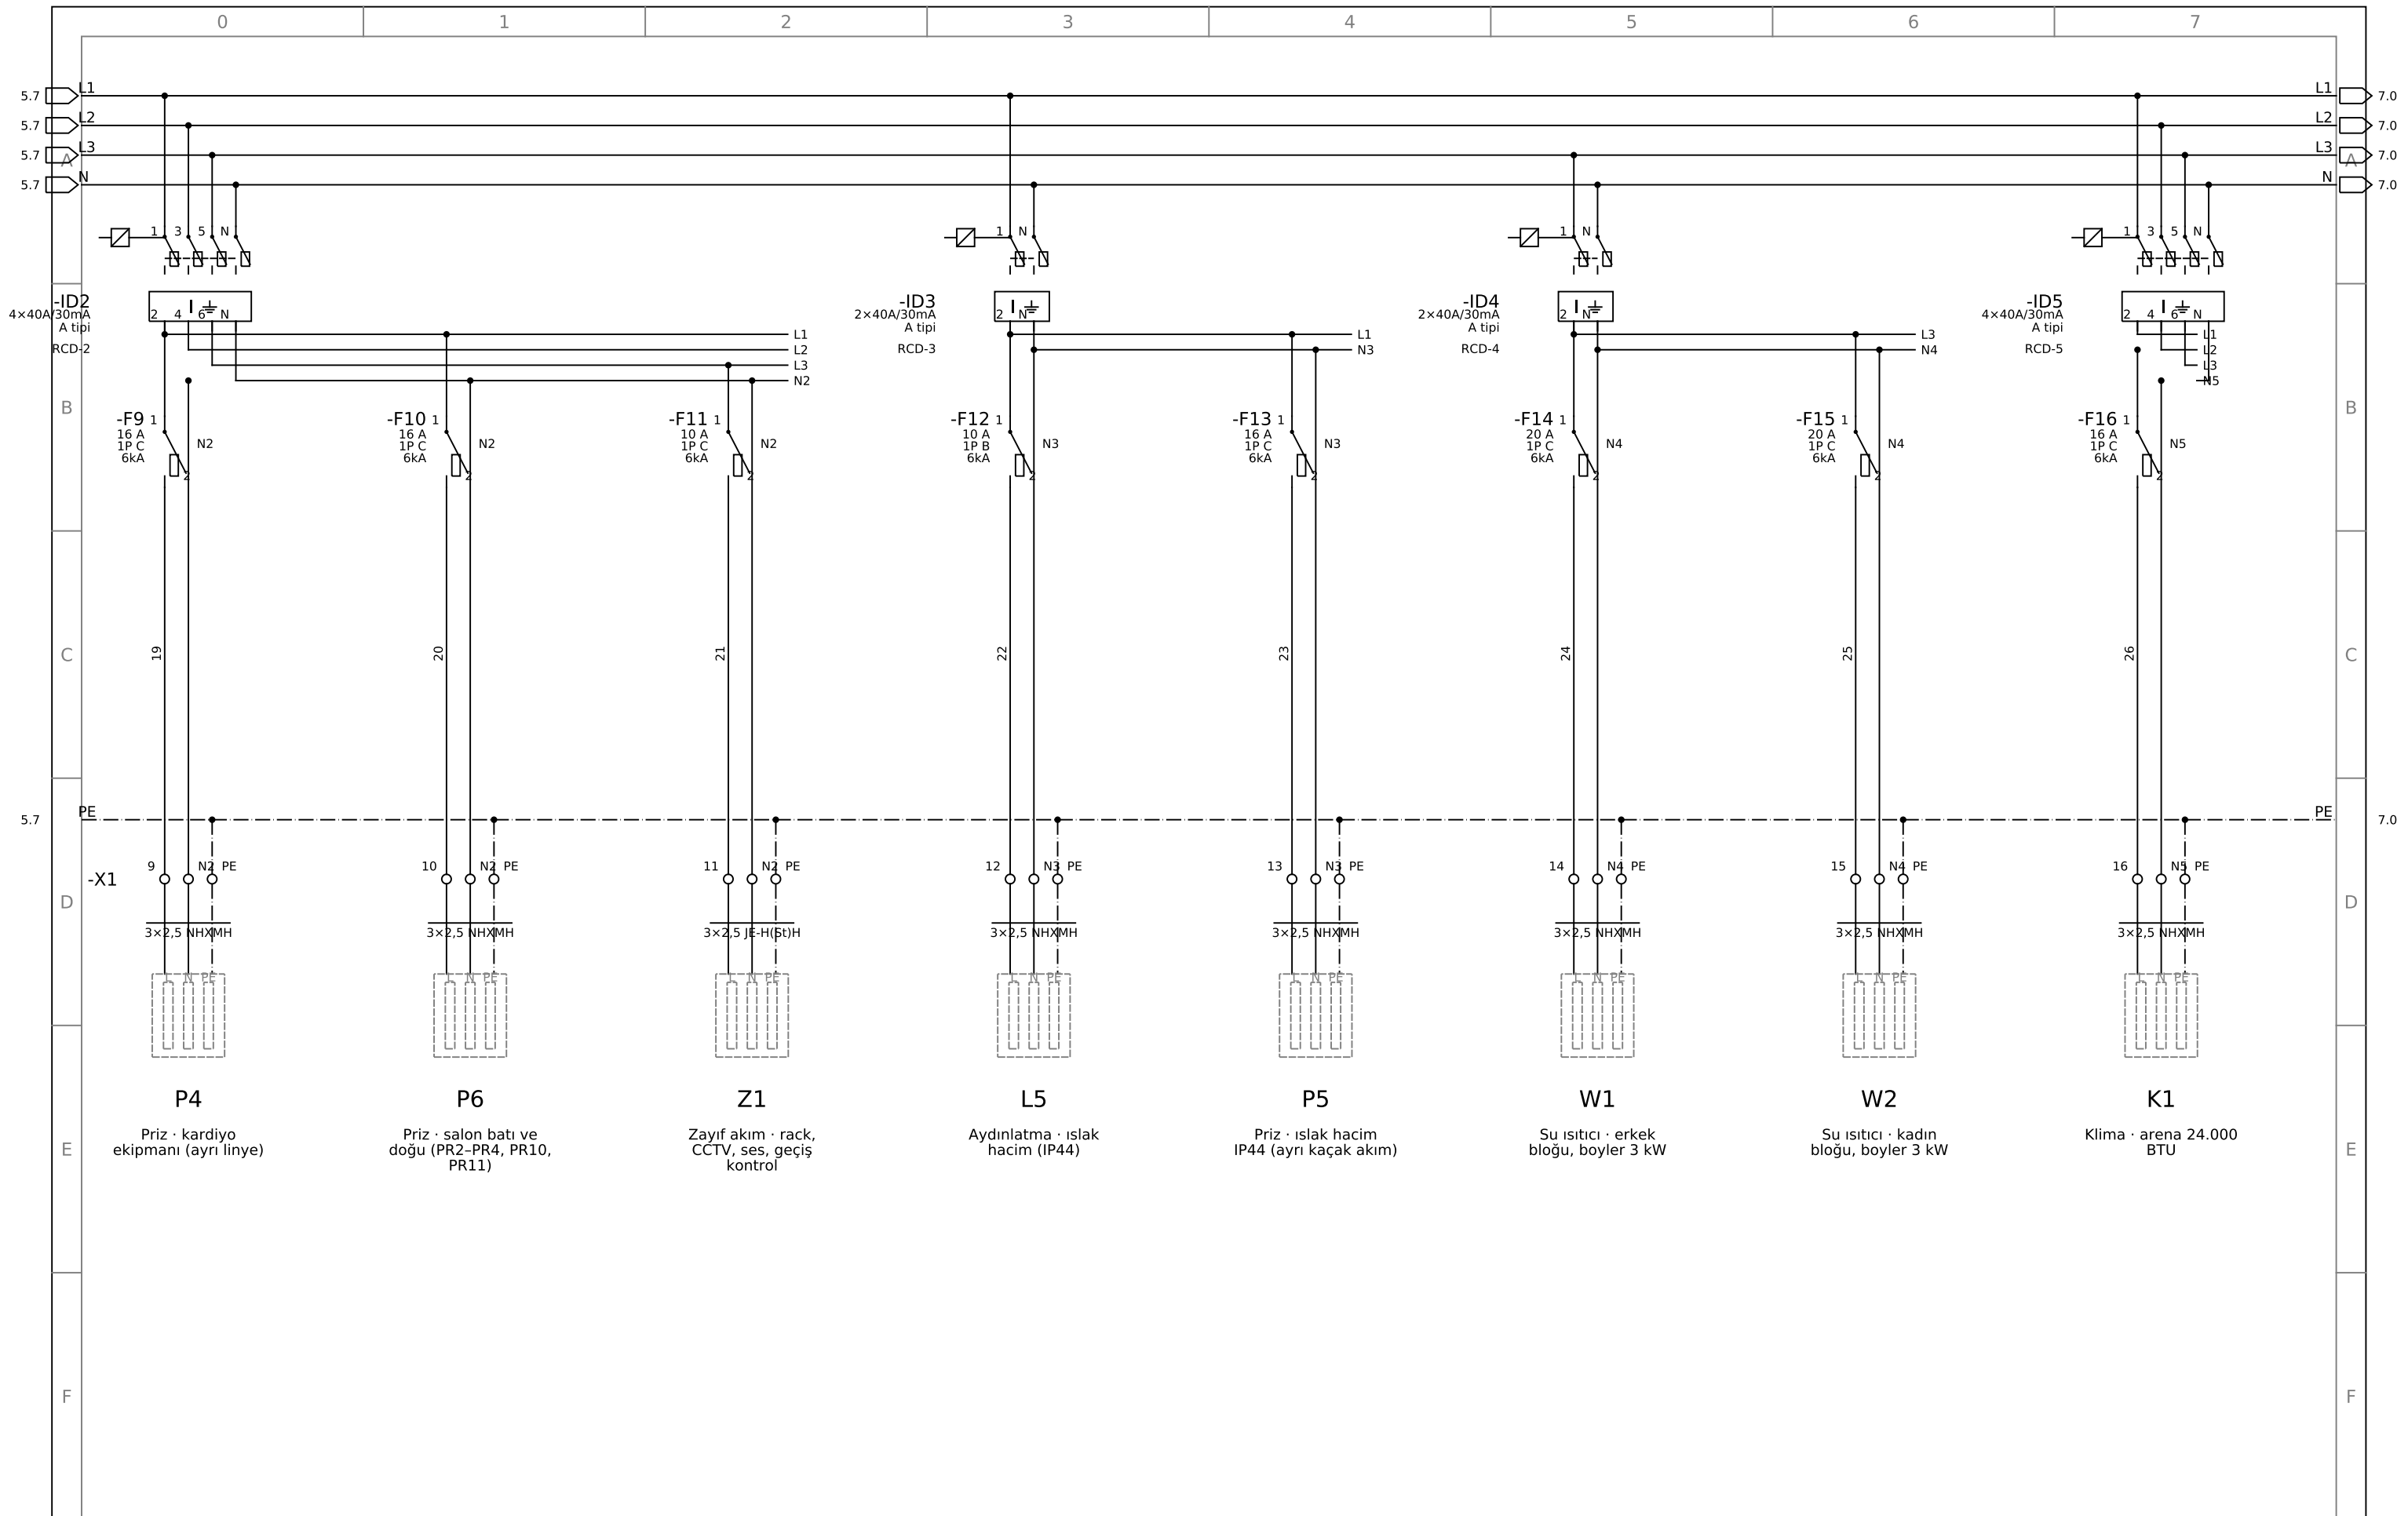

Drawn By / Çizen	CC	Customer Name / Müşteri Adı	ÖZEL — MALTEPE / İDEALTEPE		Project Number / Proje Numarası	GYM-25-001-001	Sheet: / Sayfa	6
Checked By / Kontrol Eden	—	Project Description / Proje Açıklaması	MOBİLYA MAĞAZASI → FONKSİYONEL ANTRENMAN STÜDYOSU				Next sheet: / Sonraki	7
Approved By / Onaylayan	—	Panel Name / Pano Adı	ADP		Revision / Revizyon	Rev H	Total sheets: / Toplam	12
Project Date / Proje Tarihi	17 Eylül 2026	Page Description / Sayfa Açıklaması	Schematic Diagram / Şematik Diyagram		Standards / Standartlar	IEC 61439-1&2 · IEC 60617	Sheet size / Kâğıt	A3

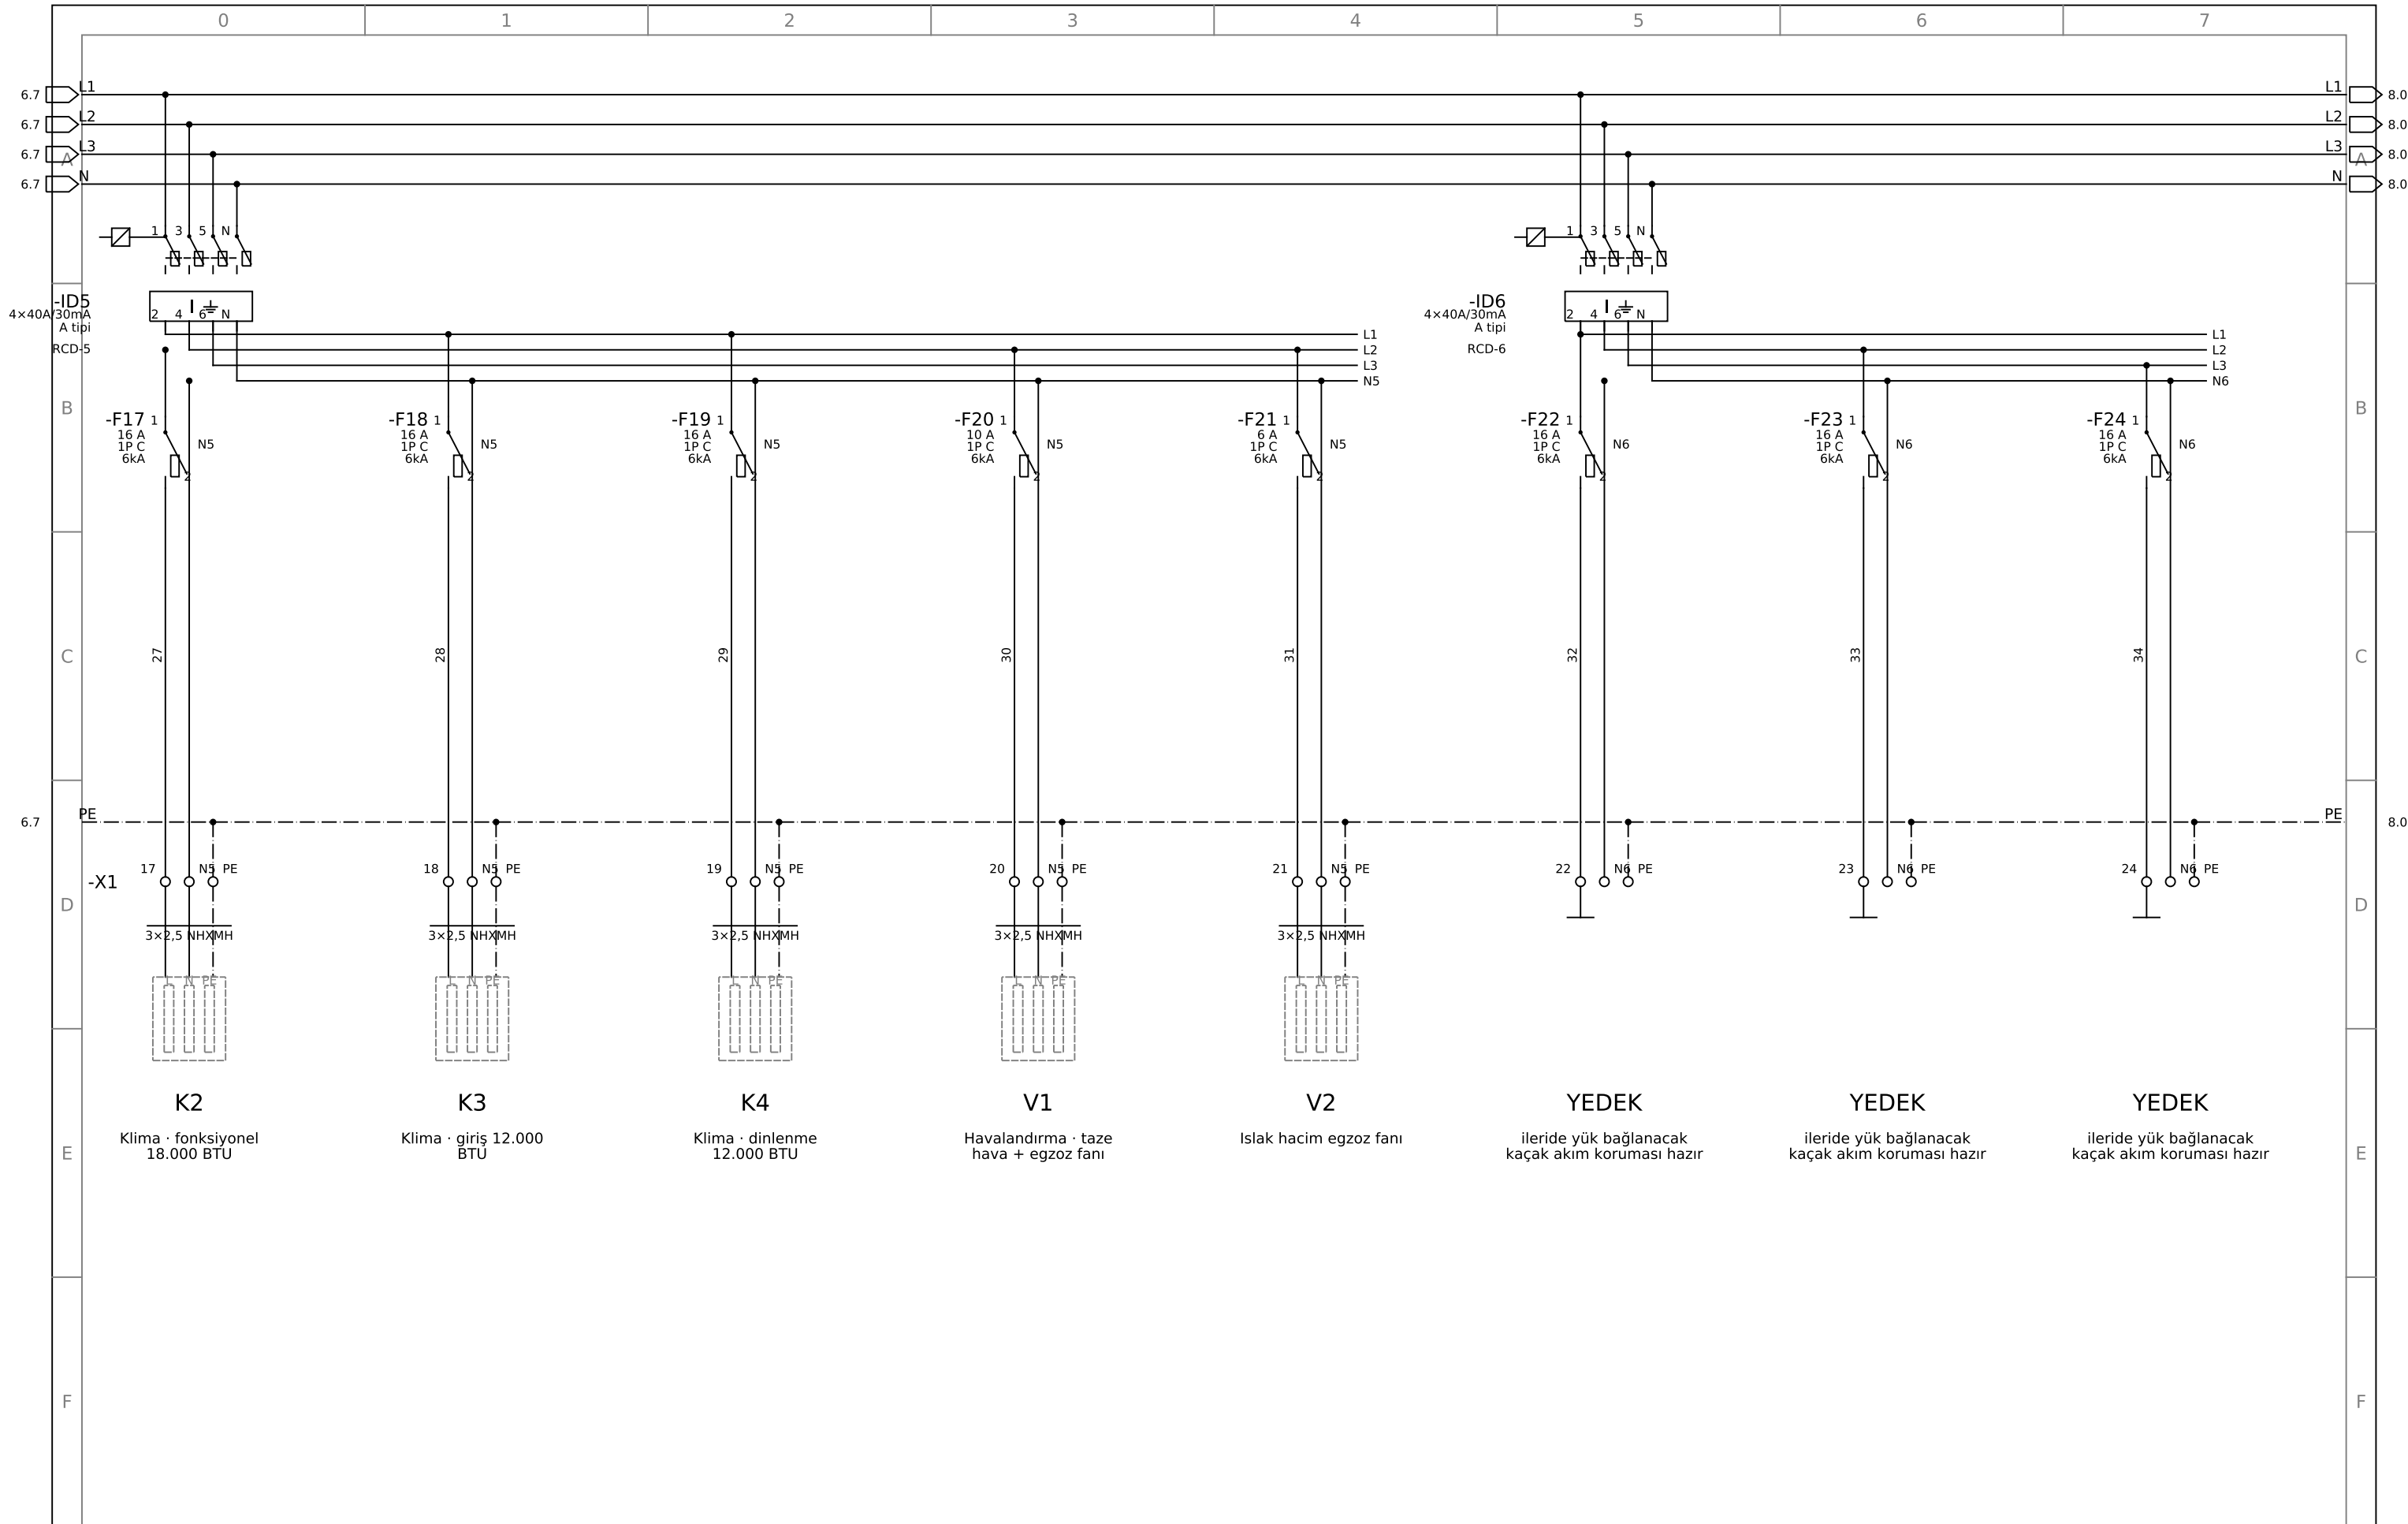

Drawn By / Çizen	CC	Customer Name / Müşteri Adı	ÖZEL — MALTEPE / İDEALTEPE	Project Number / Proje Numarası	GYM-25-001-001	Sheet: / Sayfa	7
Checked By / Kontrol Eden	—	Project Description / Proje Açıklaması	MOBİLYA MAĞAZASI → FONKSİYONEL ANTRENMAN STÜDYOSU			Next sheet: / Sonraki	8
Approved By / Onaylayan	—	Panel Name / Pano Adı	ADP	Revision / Revizyon	Rev H	Total sheets: / Toplam	12
Project Date / Proje Tarihi	17 Eylül 2026	Page Description / Sayfa Açıklaması	Schematic Diagram / Şematik Diyagram	Standards / Standartlar	IEC 61439-1&2 · IEC 60617	Sheet size / Kâğıt	A3

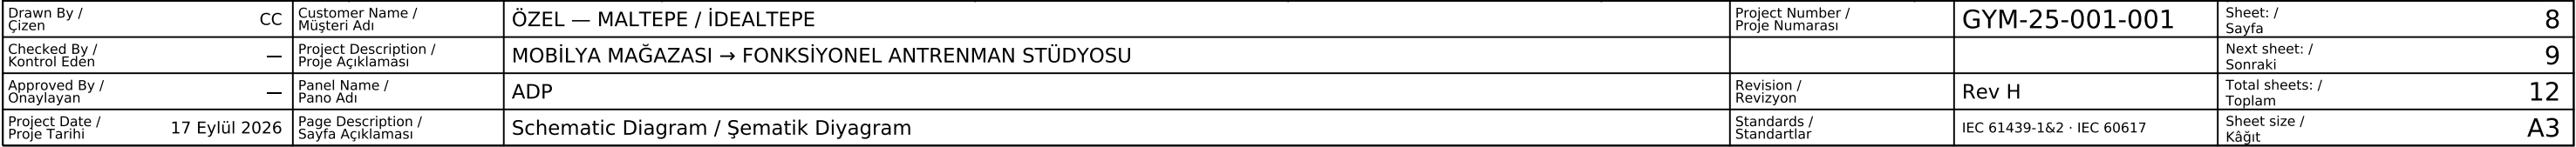

0		1		2		3		4		5		6		7							
KLEMENS PLANI / TERMINAL DIAGRAM — -X1																					
A	KLEMENS	LİNYE	İLETKEN	TEL NO	KABLO	HEDEF / DESTINATION	SAYFA	KAÇAK AKIM													
	1	L1	L	11	NHXMH 3×2,5	Aydınlatma — arena / serbest ağırlık	5	RCD-1													
		L1	N	N1	NHXMH 3×2,5	Aydınlatma — arena / serbest ağırlık	5	RCD-1													
B		L1	PE	PE	NHXMH 3×2,5	Aydınlatma — arena / serbest ağırlık	5	RCD-1													
	2	L2	L	12	NHXMH 3×2,5	Aydınlatma — fonksiyonel / kardiyo	5	RCD-1													
		L2	N	N1	NHXMH 3×2,5	Aydınlatma — fonksiyonel / kardiyo	5	RCD-1													
C		L2	PE	PE	NHXMH 3×2,5	Aydınlatma — fonksiyonel / kardiyo	5	RCD-1													
	3	L3	L	13	NHXMH 3×2,5	Aydınlatma — dinlenme salonu	5	RCD-1													
		L3	N	N1	NHXMH 3×2,5	Aydınlatma — dinlenme salonu	5	RCD-1													
D		L3	PE	PE	NHXMH 3×2,5	Aydınlatma — dinlenme salonu	5	RCD-1													
	4	L4	L	14	NHXMH 3×2,5	Aydınlatma — giriş / banko	5	RCD-1													
		L4	N	N1	NHXMH 3×2,5	Aydınlatma — giriş / banko	5	RCD-1													
E		L4	PE	PE	NHXMH 3×2,5	Aydınlatma — giriş / banko	5	RCD-1													
	5	L6	L	15	NHXMH 3×2,5	Acil aydınlatma ve yönlendirme	5	RCD-1													
		L6	N	N1	NHXMH 3×2,5	Acil aydınlatma ve yönlendirme	5	RCD-1													
F		L6	PE	PE	NHXMH 3×2,5	Acil aydınlatma ve yönlendirme	5	RCD-1													
	6	P1	L	16	NHXMH 3×2,5	Priz — salon kuzey (PR12-PR16, PR1)	5	RCD-2													
		P1	N	N2	NHXMH 3×2,5	Priz — salon kuzey (PR12-PR16, PR1)	5	RCD-2													
A		P1	PE	PE	NHXMH 3×2,5	Priz — salon kuzey (PR12-PR16, PR1)	5	RCD-2													
	7	P2	L	17	NHXMH 3×2,5	Priz — salon güney (PR5-PR9)	5	RCD-2													
		P2	N	N2	NHXMH 3×2,5	Priz — salon güney (PR5-PR9)	5	RCD-2													
B		P2	PE	PE	NHXMH 3×2,5	Priz — salon güney (PR5-PR9)	5	RCD-2													
	8	P3	L	18	NHXMH 3×2,5	Priz — banko, POS, veri	5	RCD-2													
		P3	N	N2	NHXMH 3×2,5	Priz — banko, POS, veri	5	RCD-2													
C		P3	PE	PE	NHXMH 3×2,5	Priz — banko, POS, veri	5	RCD-2													
	9	P4	L	19	NHXMH 3×2,5	Priz — kardiyo ekipmanı (ayrı linye)	6	RCD-2													
		P4	N	N2	NHXMH 3×2,5	Priz — kardiyo ekipmanı (ayrı linye)	6	RCD-2													
D		P4	PE	PE	NHXMH 3×2,5	Priz — kardiyo ekipmanı (ayrı linye)	6	RCD-2													
	10	P6	L	20	NHXMH 3×2,5	Priz — salon batı ve doğu (PR2-PR4, PR10, PR	6	RCD-2													
		P6	N	N2	NHXMH 3×2,5	Priz — salon batı ve doğu (PR2-PR4, PR10, PR	6	RCD-2													
E		P6	PE	PE	NHXMH 3×2,5	Priz — salon batı ve doğu (PR2-PR4, PR10, PR	6	RCD-2													
	11	Z1	L	21	JE-H(St)H 3×2,5	Zayıf akım — rack, CCTV, ses, geçiş kontrol	6	RCD-2													
		Z1	N	N2	JE-H(St)H 3×2,5	Zayıf akım — rack, CCTV, ses, geçiş kontrol	6	RCD-2													
F		Z1	PE	PE	JE-H(St)H 3×2,5	Zayıf akım — rack, CCTV, ses, geçiş kontrol	6	RCD-2													
	12	L5	L	22	NHXMH 3×2,5	Aydınlatma — ıslak hacim (IP44)	6	RCD-3													
		L5	N	N3	NHXMH 3×2,5	Aydınlatma — ıslak hacim (IP44)	6	RCD-3													
A		L5	PE	PE	NHXMH 3×2,5	Aydınlatma — ıslak hacim (IP44)	6	RCD-3													
	13	P5	L	23	NHXMH 3×2,5	Priz — ıslak hacim IP44 (ayrı kaçak akım)	6	RCD-3													
		P5	N	N3	NHXMH 3×2,5	Priz — ıslak hacim IP44 (ayrı kaçak akım)	6	RCD-3													
B		P5	PE	PE	NHXMH 3×2,5	Priz — ıslak hacim IP44 (ayrı kaçak akım)	6	RCD-3													
	14	W1	L	24	NHXMH 3×2,5	Su ısıtıcı — erkek bloğu, boyler 3 kW	6	RCD-4													
		W1	N	N4	NHXMH 3×2,5	Su ısıtıcı — erkek bloğu, boyler 3 kW	6	RCD-4													
C		W1	PE	PE	NHXMH 3×2,5	Su ısıtıcı — erkek bloğu, boyler 3 kW	6	RCD-4													
	15	W2	L	25	NHXMH 3×2,5	Su ısıtıcı — kadın bloğu, boyler 3 kW	6	RCD-4													
		W2	N	N4	NHXMH 3×2,5	Su ısıtıcı — kadın bloğu, boyler 3 kW	6	RCD-4													
D		W2	PE	PE	NHXMH 3×2,5	Su ısıtıcı — kadın bloğu, boyler 3 kW	6	RCD-4													
	16	K1	L	26	NHXMH 3×2,5	Klima — arena 24.000 BTU	6	RCD-5													
		K1	N	N5	NHXMH 3×2,5	Klima — arena 24.000 BTU	6	RCD-5													
E		K1	PE	PE	NHXMH 3×2,5	Klima — arena 24.000 BTU	6	RCD-5													
	17	K2	L	27	NHXMH 3×2,5	Klima — fonksiyonel 18.000 BTU	7	RCD-5													
		K2	N	N5	NHXMH 3×2,5	Klima — fonksiyonel 18.000 BTU	7	RCD-5													
F		K2	PE	PE	NHXMH 3×2,5	Klima — fonksiyonel 18.000 BTU	7	RCD-5													
	18	K3	L	28	NHXMH 3×2,5	Klima — giriş 12.000 BTU	7	RCD-5													
		K3	N	N5	NHXMH 3×2,5	Klima — giriş 12.000 BTU	7	RCD-5													
A		K3	PE	PE	NHXMH 3×2,5	Klima — giriş 12.000 BTU	7	RCD-5													
	19	K4	L	29	NHXMH 3×2,5	Klima — dinlenme 12.000 BTU	7	RCD-5													
		K4	N	N5	NHXMH 3×2,5	Klima — dinlenme 12.000 BTU	7	RCD-5													
B		K4	PE	PE	NHXMH 3×2,5	Klima — dinlenme 12.000 BTU	7	RCD-5													
	20	V1	L	30	NHXMH 3×2,5	Havalandırma — taze hava + egzoz fanı	7	RCD-5													
		V1	N	N5	NHXMH 3×2,5	Havalandırma — taze hava + egzoz fanı	7	RCD-5													
C	Drawn By / Çizen	CC	Customer Name / Müşteri Adı	ÖZEL — MALTEPE / IDEALTEPE	ÖZEL — MALTEPE / IDEALTEPE	ÖZEL — MALTEPE / IDEALTEPE															
	Checked By / Kontrol Eden	V1	Project Description / Proje Açıklaması	PE MOBİLYA MAĞAZASI — FONKSİYONEL ANTRENMAN STÜDYOSU	PE MOBİLYA MAĞAZASI — FONKSİYONEL ANTRENMAN STÜDYOSU	PE MOBİLYA MAĞAZASI — FONKSİYONEL ANTRENMAN STÜDYOSU	7	RCD-5													
	Approved By / Onaylayan	V2	Panel Name / Pano Adı	ADP	ADP	ADP	7	RCD-5													
D	Project Date / Proje Tarihi	17 Eylül 2026	Page Description / Sayfa Açıklaması	PE Terminal Diagram / Klemens Planı	PE Terminal Diagram / Klemens Planı	PE Terminal Diagram / Klemens Planı	7	RCD-5													
		26	Z2	L	36	JE-H(St)H 3×2,5	Yangın algılama paneli (kesintisiz)	8	—												
			Z2	N	N0	JE-H(St)H 3×2,5	Yangın algılama paneli (kesintisiz)	8	—												
E			Z2	PE	PE	JE-H(St)H 3×2,5	Yangın algılama paneli (kesintisiz)	8	—												
F																					
A																					
B																					
C																					
D																					
E																					

	0	1	2	3	4	5	6	7																																			
A	PANO ÖNDEN GÖRÜNÜŞ / PANEL FRONT VIEW — ölçek 1:5								A																																		
B									B																																		
C	ADP · 800×1000×250 mm · IP54 · Form 2b · sac gövde RAL 7035								C																																		
D	R1	<table><tr><td>-Q1</td><td>-ID0</td><td>-F0</td><td colspan="4">BOŞ 12 MOD</td></tr><tr><td>4</td><td>4</td><td>4</td><td colspan="4"></td></tr></table>							-Q1	-ID0	-F0	BOŞ 12 MOD				4	4	4					D																				
-Q1	-ID0	-F0	BOŞ 12 MOD	
4	4	4	
E	R2	<table><tr><td>-ID1</td><td>-F1</td><td>-F2</td><td>-F3</td><td>-F4</td><td>-F5</td><td>-ID2</td><td>BOŞ 1 MOD</td></tr><tr><td>4</td><td>3</td><td>3</td><td>3</td><td>3</td><td>3</td><td>4</td><td></td></tr></table>							-ID1	-F1	-F2	-F3	-F4	-F5	-ID2	BOŞ 1 MOD	4	3	3	3	3	3	4		E																		
-ID1	-F1	-F2	-F3	-F4	-F5	-ID2	BOŞ 1 MOD																																				
4	3	3	3	3	3	4																																					
F	R3	<table><tr><td>-F6</td><td>-F7</td><td>-F8</td><td>-F9</td><td>-F10</td><td>-F11</td><td>-ID3</td><td>-F12</td><td>BOŞ 1 MOD</td></tr><tr><td>3</td><td>3</td><td>3</td><td>3</td><td>3</td><td>3</td><td>2</td><td>3</td><td></td></tr></table>							-F6	-F7	-F8	-F9	-F10	-F11	-ID3	-F12	BOŞ 1 MOD	3	3	3	3	3	3	2	3		F																
-F6	-F7	-F8	-F9	-F10	-F11	-ID3	-F12	BOŞ 1 MOD																																			
3	3	3	3	3	3	2	3																																				
	R4	<table><tr><td>-F13</td><td>-ID4</td><td>-F14</td><td>-F15</td><td>-ID5</td><td>-F16</td><td>-F17</td><td>-F18</td><td>-F19</td><td>-F20</td><td>-F21</td><td>-ID6</td><td>-F22</td><td>-F23</td><td>-F24</td><td>-F25</td><td>-F26</td></tr><tr><td>3</td><td>2</td><td>3</td><td>3</td><td>4</td><td>3</td><td>3</td><td>3</td><td>3</td><td>3</td><td>3</td><td>4</td><td>1</td><td>1</td><td>1</td><td>1</td><td>3</td></tr></table>							-F13	-ID4	-F14	-F15	-ID5	-F16	-F17	-F18	-F19	-F20	-F21	-ID6	-F22	-F23	-F24	-F25	-F26	3	2	3	3	4	3	3	3	3	3	3	4	1	1	1	1	3	
-F13	-ID4	-F14	-F15	-ID5	-F16	-F17	-F18	-F19	-F20	-F21	-ID6	-F22	-F23	-F24	-F25	-F26																											
3	2	3	3	4	3	3	3	3	3	3	4	1	1	1	1	3																											
SIRA		CİHAZ		MODÜL		AÇIKLAMA																																					
R1		-Q1		4		ANA ŞALTER 4×32 A																																					
R1		-ID0		4		ANA KAÇAK AKIM 4×40 A/300 mA																																					
R1		-F0		4		SPD Tip 2																																					
R2		-ID1		4		4×40 A / 30 mA, A tipi																																					
R2		-F1		3		L1 10A B																																					
R2		-F2		3		L2 10A B																																					
R2		-F3		3		L3 10A B																																					
R2		-F4		3		L4 10A B																																					
R2		-F5		3		L6 6A B																																					
R2		-ID2		4		4×40 A / 30 mA, A tipi																																					
R3		-F6		3		P1 16A C																																					
R3		-F7		3		P2 16A C																																					
R3		-F8		3		P3 16A C																																					
R3		-F9		3		P4 16A C																																					
R3		-F10		3		P6 16A C																																					
R3		-F11		3		Z1 10A C																																					
R3		-ID3		2		2×40 A / 30 mA, A tipi																																					
R3		-F12		3		L5 10A B																																					
R4		-F13		3		P5 16A C																																					
R4		-ID4		2		2×40 A / 30 mA, A tipi																																					
R4		-F14		3		W1 20A C																																					
R4		-F15		3		W2 20A C																																					
R4		-ID5		4		4×40 A / 30 mA, A tipi																																					
R4		-F16		3		K1 16A C																																					
R4		-F17		3		K2 16A C																																					
R4		-F18		3		K3 16A C																																					
R4		-F19		3		K4 16A C																																					
R4		-F20		3		V1 10A C																																					
R4		-F21		3		V2 6A C																																					
R4		-ID6		4		4×40 A / 30 mA, A tipi																																					
R4		-F22		1		Y1 16A C																																					
R4		-F23		1		Y2 16A C																																					
R4		-F24		1		Y3 16A C																																					
R4		-F25		1		Y4 16A C																																					
R4		-F26		3		Z2 6A C																																					
Drawn By / Çizen		CC		Customer Name / Müşteri Adı		ÖZEL — MALTEPE / İDEALTEPE				Project Number / Proje Numarası		GYM-25-001-001		Sheet: / Sayfa		10																											
Checked By / Kontrol Eden		—		Project Description / Proje Açıklaması		MOBİLYA MAĞAZASI → FONKSİYONEL ANTRENMAN STÜDYOSU								Next sheet: / Sonraki		11																											
Approved By / Onaylayan		—		Panel Name / Pano Adı		ADP				Revision / Revizyon		Rev H		Total sheets: / Toplam		12																											
Project Date / Proje Tarihi		17 Eylül 2026		Page Description / Sayfa Açıklaması		Panel Overview / Pano Önden Görünüş				Standards / Standartlar		IEC 61439-1&2 · IEC 60617		Sheet size / Kâğıt		A3																											

SIRA	CİHAZ	MODÜL	AÇIKLAMA
R1	-Q1	4	ANA ŞALTER 4×32 A
R1	-ID0	4	ANA KAÇAK AKIM 4×40 A/300 mA
R1	-F0	4	SPD Tip 2
R2	-ID1	4	4×40 A / 30 mA, A tipi
R2	-F1	3	L1 10A B
R2	-F2	3	L2 10A B
R2	-F3	3	L3 10A B
R2	-F4	3	L4 10A B
R2	-F5	3	L6 6A B
R2	-ID2	4	4×40 A / 30 mA, A tipi
R3	-F6	3	P1 16A C
R3	-F7	3	P2 16A C
R3	-F8	3	P3 16A C
R3	-F9	3	P4 16A C
R3	-F10	3	P6 16A C
R3	-F11	3	Z1 10A C
R3	-ID3	2	2×40 A / 30 mA, A tipi
R3	-F12	3	L5 10A B
R4	-F13	3	P5 16A C
R4	-ID4	2	2×40 A / 30 mA, A tipi
R4	-F14	3	W1 20A C
R4	-F15	3	W2 20A C
R4	-ID5	4	4×40 A / 30 mA, A tipi
R4	-F16	3	K1 16A C
R4	-F17	3	K2 16A C
R4	-F18	3	K3 16A C
R4	-F19	3	K4 16A C
R4	-F20	3	V1 10A C
R4	-F21	3	V2 6A C
R4	-ID6	4	4×40 A / 30 mA, A tipi
R4	-F22	1	Y1 16A C
R4	-F23	1	Y2 16A C
R4	-F24	1	Y3 16A C
R4	-F25	1	Y4 16A C
R4	-F26	3	Z2 6A C

ADP YÜKLEME CETVELİ / LOAD SCHEDULE

Grup kaçak akım röleleri ve kapsadıkları linyeler ayrı sütunda gösterilmiştir.

NO	LİNYE	MAHAL / YÜK	FAZ	KESİCİ	KAÇAK AKIM (GRUP)	KABLO	BORU	UZUNLUK	Pb (kW)	cos φ	Ib (A)	ΔU (%)	SONUÇ
1	L1	Aydınlatma — arena / serbest ağırlık	L2	10 A · 1P B · 6 kA	RCD-1 · 4×40 A / 30 mA A tipi	NHXXMH 3×2,5	Ø20	14 m	0,28	0,95	1,3	0,13	UYGUN
2	L2	Aydınlatma — fonksiyonel / kardiyo	L3	10 A · 1P B · 6 kA	↑ aynı grup	NHXXMH 3×2,5	Ø20	11 m	0,12	0,95	0,5	0,05	UYGUN
3	L3	Aydınlatma — dinlenme salonu	L1	10 A · 1P B · 6 kA	↑ aynı grup	NHXXMH 3×2,5	Ø20	14 m	0,12	0,95	0,5	0,06	UYGUN
4	L4	Aydınlatma — giriş / banko	L3	10 A · 1P B · 6 kA	↑ aynı grup	NHXXMH 3×2,5	Ø20	12 m	0,08	0,95	0,4	0,03	UYGUN
5	L6	Acil aydınlatma ve yönlendirme	L2	6 A · 1P B · 6 kA	↑ aynı grup	NHXXMH 3×2,5	Ø20	10 m	0,06	0,95	0,3	0,02	UYGUN
6	P1	Priz — salon kuzey (PR12-PR16, PR1)	L1	16 A · 1P C · 6 kA	RCD-2 · 4×40 A / 30 mA A tipi	NHXXMH 3×2,5	Ø20	8 m	0,90	0,90	4,3	0,24	UYGUN
7	P2	Priz — salon güney (PR5-PR9)	L3	16 A · 1P C · 6 kA	↑ aynı grup	NHXXMH 3×2,5	Ø20	17 m	0,75	0,90	3,6	0,42	UYGUN
8	P3	Priz — banko, POS, veri	L2	16 A · 1P C · 6 kA	↑ aynı grup	NHXXMH 3×2,5	Ø20	9 m	1,00	0,90	4,8	0,30	UYGUN
9	P4	Priz — kardiyo ekipmanı (ayrı linye)	L1	16 A · 1P C · 6 kA	↑ aynı grup	NHXXMH 3×2,5	Ø20	17 m	2,40	0,90	11,6	1,40	UYGUN
10	P6	Priz — salon batı ve doğu (PR2-PR4, PR	L1	16 A · 1P C · 6 kA	↑ aynı grup	NHXXMH 3×2,5	Ø20	10 m	0,75	0,90	3,6	0,27	UYGUN
11	Z1	Zayıf akım — rack, CCTV, ses, geçiş ko	L3	10 A · 1P C · 6 kA	↑ aynı grup	JE-H(St)H 3×2,5	Ø20	9 m	0,60	0,90	2,9	0,18	UYGUN
12	L5	Aydınlatma — ıslak hacim (IP44)	L1	10 A · 1P B · 6 kA	RCD-3 · 2×40 A / 30 mA A tipi	NHXXMH 3×2,5	Ø20	16 m	0,11	0,95	0,5	0,06	UYGUN
13	P5	Priz — ıslak hacim IP44 (ayrı kaçak ak	L3	16 A · 1P C · 6 kA	↑ aynı grup	NHXXMH 3×2,5	Ø20	16 m	0,50	0,90	2,4	0,27	UYGUN
14	W1	Su ısıtıcı — erkek bloğu, boyler 3 kW	L3	20 A · 1P C · 6 kA	RCD-4 · 2×40 A / 30 mA A tipi	NHXXMH 3×2,5	Ø20	16 m	3,00	1,00	13,0	1,66	UYGUN
15	W2	Su ısıtıcı — kadın bloğu, boyler 3 kW	L3	20 A · 1P C · 6 kA	↑ aynı grup	NHXXMH 3×2,5	Ø20	19 m	3,00	1,00	13,0	1,97	UYGUN
16	K1	Klima — arena 24.000 BTU	L2	16 A · 1P C · 6 kA	RCD-5 · 4×40 A / 30 mA A tipi	NHXXMH 3×2,5	Ø20	18 m	2,20	0,85	11,3	1,32	UYGUN
17	K2	Klima — fonksiyonel 18.000 BTU	L2	16 A · 1P C · 6 kA	↑ aynı grup	NHXXMH 3×2,5	Ø20	13 m	1,70	0,85	8,7	0,73	UYGUN
18	K3	Klima — giriş 12.000 BTU	L1	16 A · 1P C · 6 kA	↑ aynı grup	NHXXMH 3×2,5	Ø20	12 m	1,15	0,85	5,9	0,48	UYGUN
19	K4	Klima — dinlenme 12.000 BTU	L1	16 A · 1P C · 6 kA	↑ aynı grup	NHXXMH 3×2,5	Ø20	15 m	1,15	0,85	5,9	0,58	UYGUN
20	V1	Havalandırma — taze hava + egzoz fanı	L2	10 A · 1P C · 6 kA	↑ aynı grup	NHXXMH 3×2,5	Ø20	14 m	0,45	0,85	2,3	0,21	UYGUN
21	V2	Islak hacim egzoz fanı	L2	6 A · 1P C · 6 kA	↑ aynı grup	NHXXMH 3×2,5	Ø20	16 m	0,12	0,85	0,6	0,07	UYGUN
22	Y1	YEDEK — ileride yük bağlanacak	L1	16 A · 1P C · 6 kA	RCD-6 · 4×40 A / 30 mA A tipi	—	—	—	—	—	—	—	YEDEK
23	Y2	YEDEK — ileride yük bağlanacak	L2	16 A · 1P C · 6 kA	↑ aynı grup	—	—	—	—	—	—	—	YEDEK
24	Y3	YEDEK — ileride yük bağlanacak	L3	16 A · 1P C · 6 kA	↑ aynı grup	—	—	—	—	—	—	—	YEDEK
25	Y4	YEDEK — ileride yük bağlanacak	L1	16 A · 1P C · 6 kA	↑ aynı grup	—	—	—	—	—	—	—	YEDEK
26	Z2	Yangın algılama paneli (kesintisiz)	L1	6 A · 1P C · 6 kA	— kaçak akım rölesi yok (kesintisiz)	JE-H(St)H 3×2,5	Ø20	10 m	0,15	0,90	0,7	0,05	UYGUN

ÖZET / SUMMARY

Bağlı güç / Connected	20,59 kW	Talep gücü / Demand	14,63 kW	L1 / L2 / L3 (kW)	4,86 / 4,91 / 4,87	Faz dengesizliği / Imbalance	%1,0
Ana şalter / Main switch	4x32 A	Ana kaçak akım / Main RCD	4x40 A / 300 mA S tipi	Grup kaçak akım sayısı / RCD groups	7 adet	Toplam ΔU / Total	%2,49

Drawn By / Çizen	CC	Customer Name / Müşteri Adı	ÖZEL — MALTEPE / İDEALTEPE	Project Number / Proje Numarası	GYM-25-001-001	Sheet: / Sayfa	11
Checked By / Kontrol Eden	—	Project Description / Proje Açıklaması	MOBİLYA MAĞAZASI → FONKSİYONEL ANTRENMAN STÜDYOSU			Next sheet: / Sonraki	12
Approved By / Onaylayan	—	Panel Name / Pano Adı	ADP	Revision / Revizyon	Rev H	Total sheets: / Toplam	12
Project Date / Proje Tarihi	17 Eylül 2026	Page Description / Sayfa Açıklaması	Load Schedule / Yükleme Cetveli	Standards / Standartlar	IEC 61439-1&2 · IEC 60617	Sheet size / Kâğıt	A3

0

1

2

3

4

5

6

7

A

B

C

D

E

F

MALZEME LİSTESİ / PARTS LIST

S.NO	MALZEME / MATERIAL	BİRİM	MİKTAR
1	Otomatik sigorta 2×16 A C eğrisi · 6 kA	adet	10
2	Otomatik sigorta 2×10 A B eğrisi · 6 kA	adet	5
3	Otomatik sigorta 1×16 A C eğrisi · 6 kA	adet	4
4	Kaçak akım rölesi 4×40 A / 30 mA, A tipi	adet	4
5	Otomatik sigorta 2×10 A C eğrisi · 6 kA	adet	2
6	Otomatik sigorta 2×20 A C eğrisi · 6 kA	adet	2
7	Otomatik sigorta 2×6 A C eğrisi · 6 kA	adet	2
8	Kaçak akım rölesi 2×40 A / 30 mA, A tipi	adet	2
9	Otomatik sigorta 2×6 A B eğrisi · 6 kA	adet	1
10	Ana şalter 4×32 A yük ayırıcı	adet	1
11	Ana kaçak akım rölesi 4×40 A / 300 mA S tipi	adet	1
12	Parafudr Tip 2 · Up 1,4 kV · In 20 kA (3F+N)	adet	1
13	Pano gövdesi 800×1000×250 mm IP54 Form 2b	adet	1
14	Bakır bara seti 3F+N+PE	adet	1
15	Klemens sırası -X1 (vidalı, 4 mm²)	adet	66
16	Etiket seti (PVC, Türkçe, vidalı)	adet	1

Drawn By / Çizen	CC	Customer Name / Müşteri Adı	ÖZEL — MALTEPE / İDEALTEPE	Project Number / Proje Numarası	GYM-25-001-001	Sheet: / Sayfa	12
Checked By / Kontrol Eden	—	Project Description / Proje Açıklaması	MOBİLYA MAĞAZASI → FONKSİYONEL ANTRENMAN STÜDYOSU			Next sheet: / Sonraki	—
Approved By / Onaylayan	—	Panel Name / Pano Adı	ADP	Revision / Revizyon	Rev H	Total sheets: / Toplam	12
Project Date / Proje Tarihi	17 Eylül 2026	Page Description / Sayfa Açıklaması	Parts List / Malzeme Listesi	Standards / Standartlar	IEC 61439-1&2 · IEC 60617	Sheet size / Kâğıt	A3