


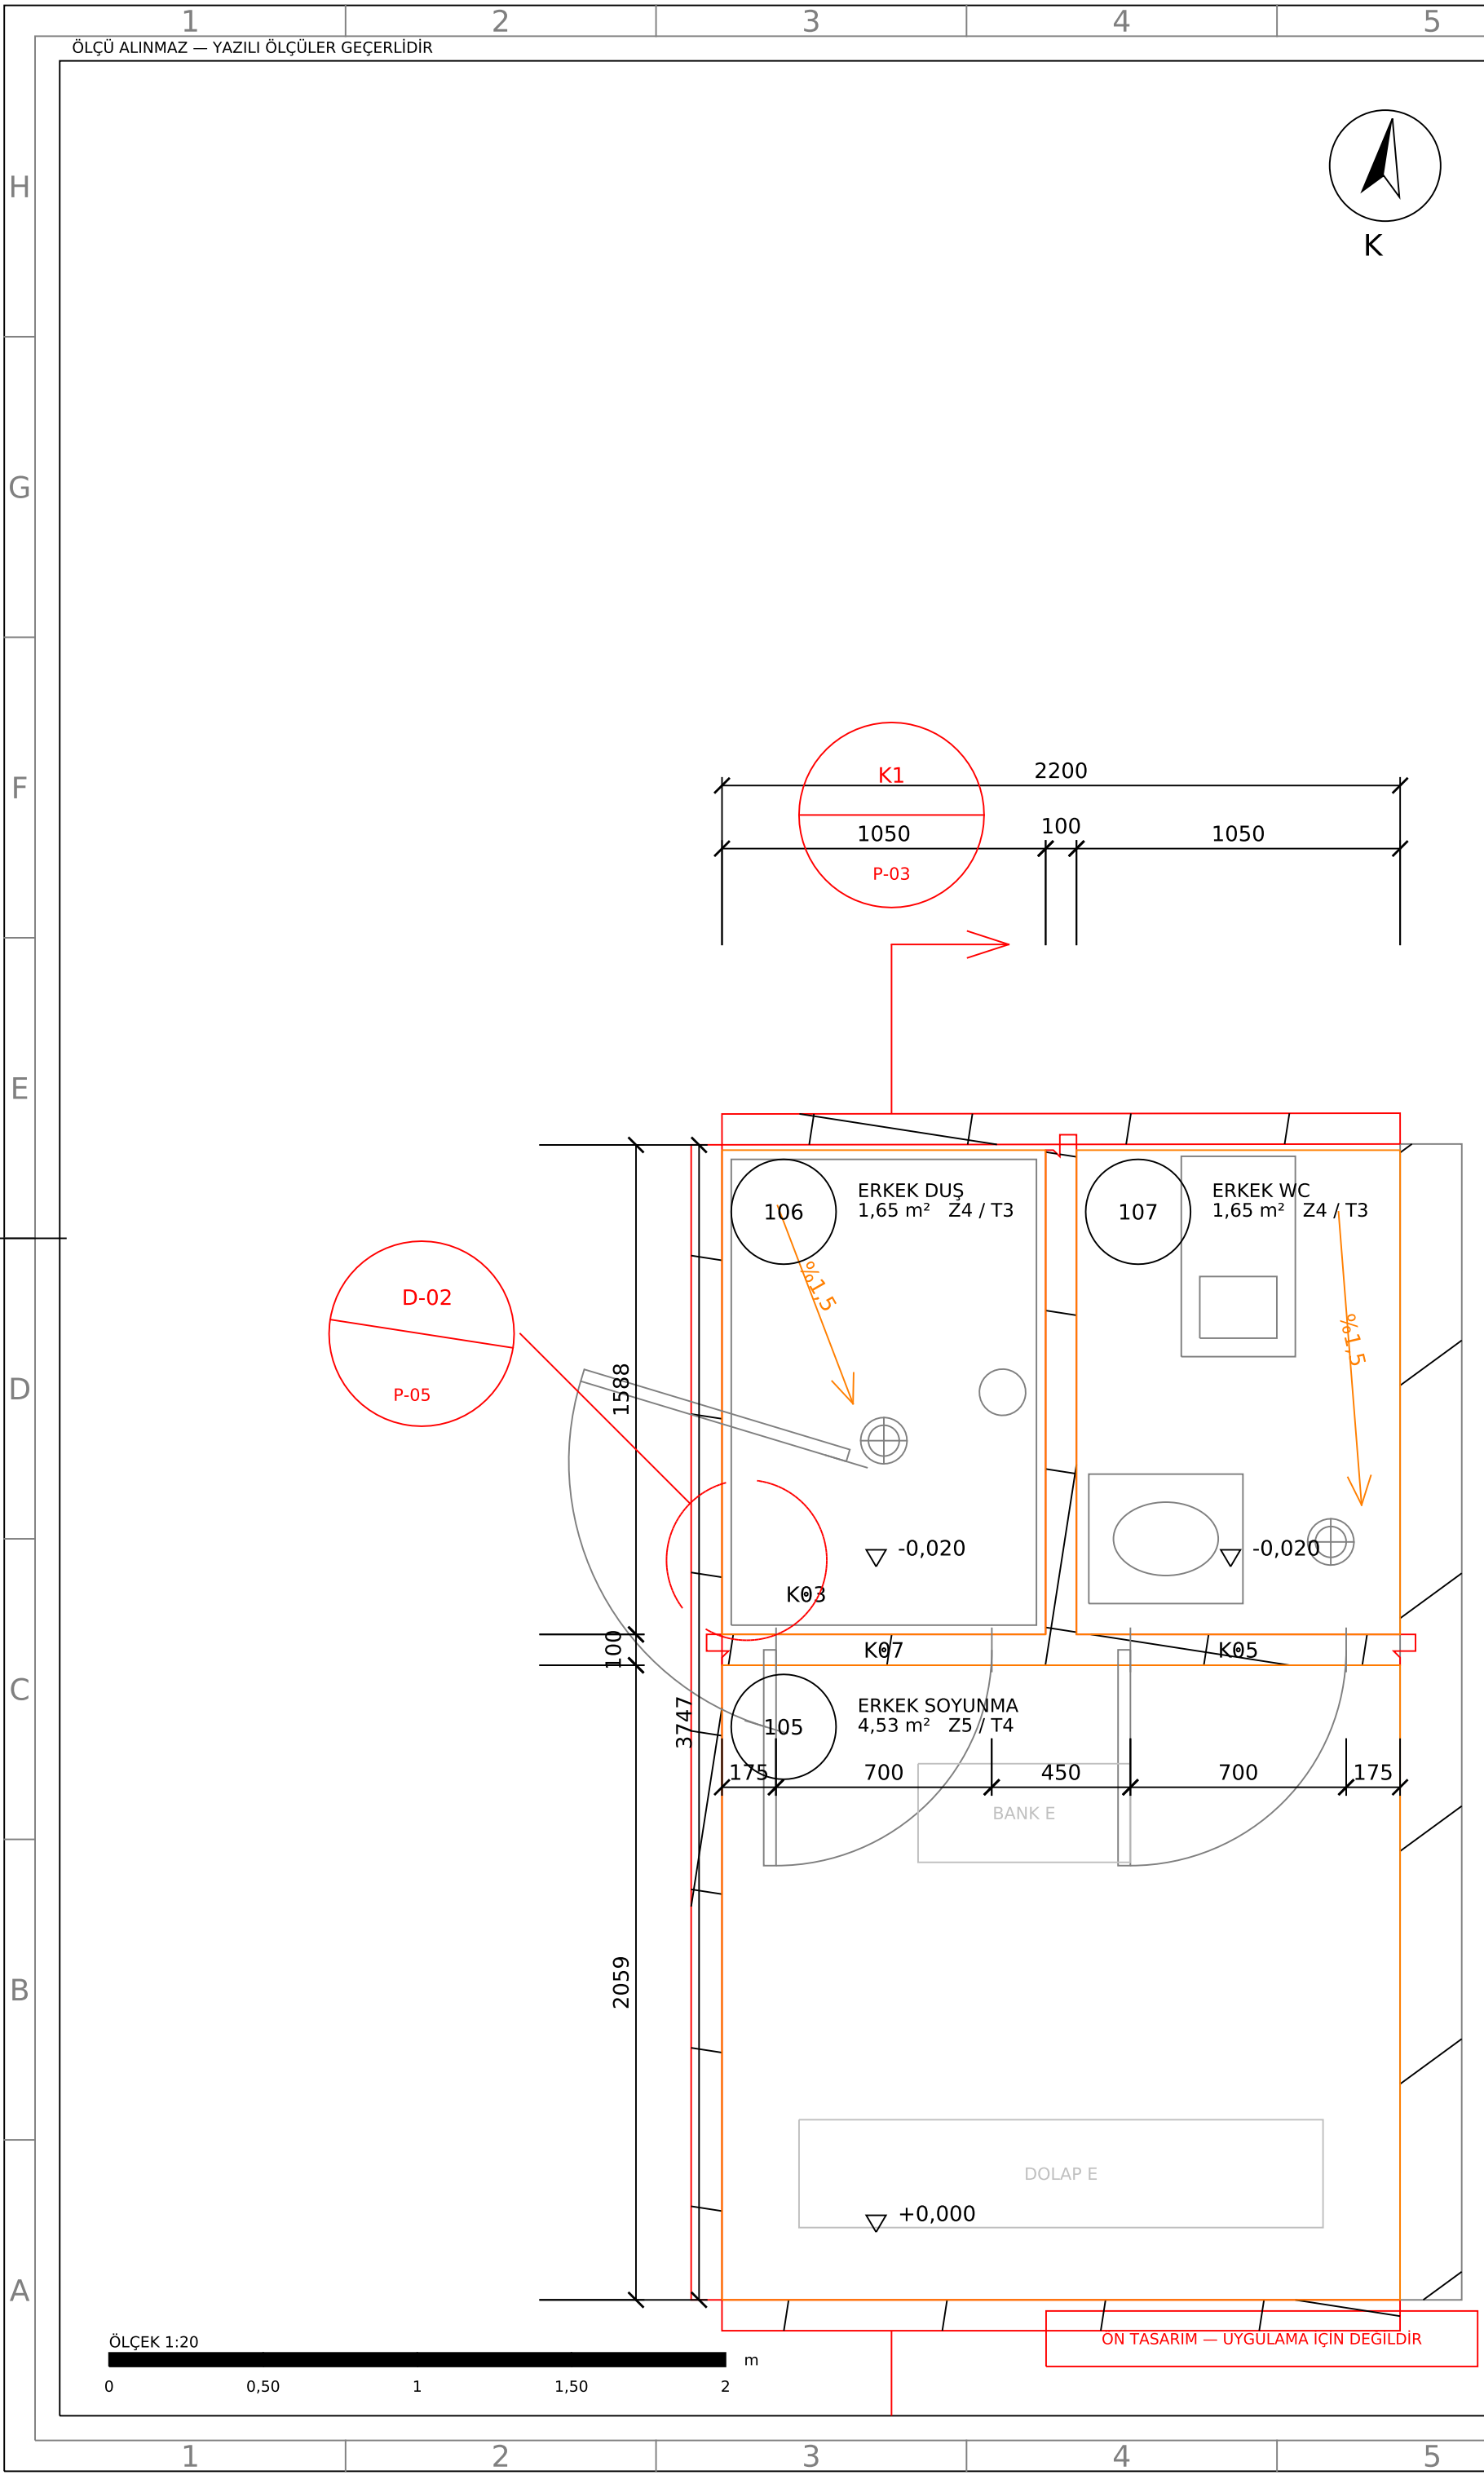

MAHZEME VE EKİPMAN LİSTESİ

MAHAL LİSTESİ

NO	MAHAL	m ²	ZEMİN	DUVAR	TAVAN
105	ERKEK SOYUNMA	4,53	Z5	D2 / D3	T4
106	ERKEK DUŞ	1,65	Z4	D3 + D5 (tavana kadar)	T3
107	ERKEK WC	1,65	Z4	D3 + D5 (h=1,60 m)	T3

KAPI LİSTESİ (bu bölge)

KOD	MAHAL	mm	TİP
K03	105 Erkek soyunma	900×2100	Tek kanat panel kapı
K05	107 Erkek WC	700×2000	Tek kanat WC kapısı
K07	106 Erkek duş	700×1950	Duş kapağı

VİTRİFİYE VE ARMATÜR

KOD	TANIM	mm
WC-1	Asma klozet + gömme rezervuar	370×650
LV-1	Lavabo + batarya	500×420
DU-1	Duş bataryası + tepe duşu	—
SZ-1	Sifonlu yer süzgeci Ø100, paslanmaz	150×150


LEJANT

- Mimari — mevcut duvar (korunuyor)
- Mimari — yeni alçıpan bölme
- Mimari — kapı ve açılım
- Mimari — sabit mobilya
- Mimari — mahal adı ve alan
- Mimari — mahal numarası ve kapı kodu balonu
- Mimari — kesit ve görünüş hattı
- Mimari — zemin kaplama tipi sınırı
- Mimari — zemin kaplama tipi ve kotu
- Kesit — malzeme taraması
- Kot işareti ve değeri
- Detay çağrı balonu ve kopuş çizgisi
- Mekanik — pis su PVC
- Mekanik — vitrifiye ve su ısıtıcı
- Genel — zincir ölçü
- Genel — kesit ve detay işareti

GENEL NOTLAR

- Geometri ölçülmüş röleveden alınmıştır (ESAT-FINAL.dwg, TRIMODE).
- Mahal alanları BİTİMİŞ YÜZ net alanıdır; iç bölme payı düşülmüştür.
- Ölçüler bloğun kendi doğrultusundadır (dünya eksenine izdüşüm değil).
- Duş ve WC zemininde süzgeçe doğru %1,5 eğim verilecektir.
- Kapı kodları kapı cetveliyle (K03-K05-K07) aynı kaynaktan üretilir.

REV	TARİH	AÇIKLAMA	ÇZ	KT	ON
A	13.09.2026	İlk yayın — ön tasarım			
B	17.09.2026	Mühendis geri bildirimi işlendi			
C	18.09.2026	Geometri ölçülmüş röleveye taşındı (ESAT-FINAL.dwg)			
D	18.09.2026	Pilot bölge: ölçülü plan · tavan · kesit · görünüş · detay			
İŞVEREN ÖZEL — MALTEPE / İDEALTEPE PROJE					
YAPI / MAHAL Mevcut mağaza → fonksiyonel antrenman stüdyosu (fit-out)			DİSİPLİN MİMARİ		
PAFTA ADI ÖLÇÜLÜ PLAN — ERKEK ISLAK BLOK			PİLOT BÖLGE — ERKEK ISLAK BLOK (105-106-107)		
PROJE MÜELLİFİ · ODA SİCİL NO — (proje müellifi imzası için ayrılmıştır) —					
ÇİZEN CC		KONTROL —		ONAY —	
TARİH 17 Eylül 2026		ÖLÇEK 1:20		BİRİM milimetre (mm)	
DURUM ÖN TASARIM		PAFTA NO P-01		REV D SONRAKİ: P-02	

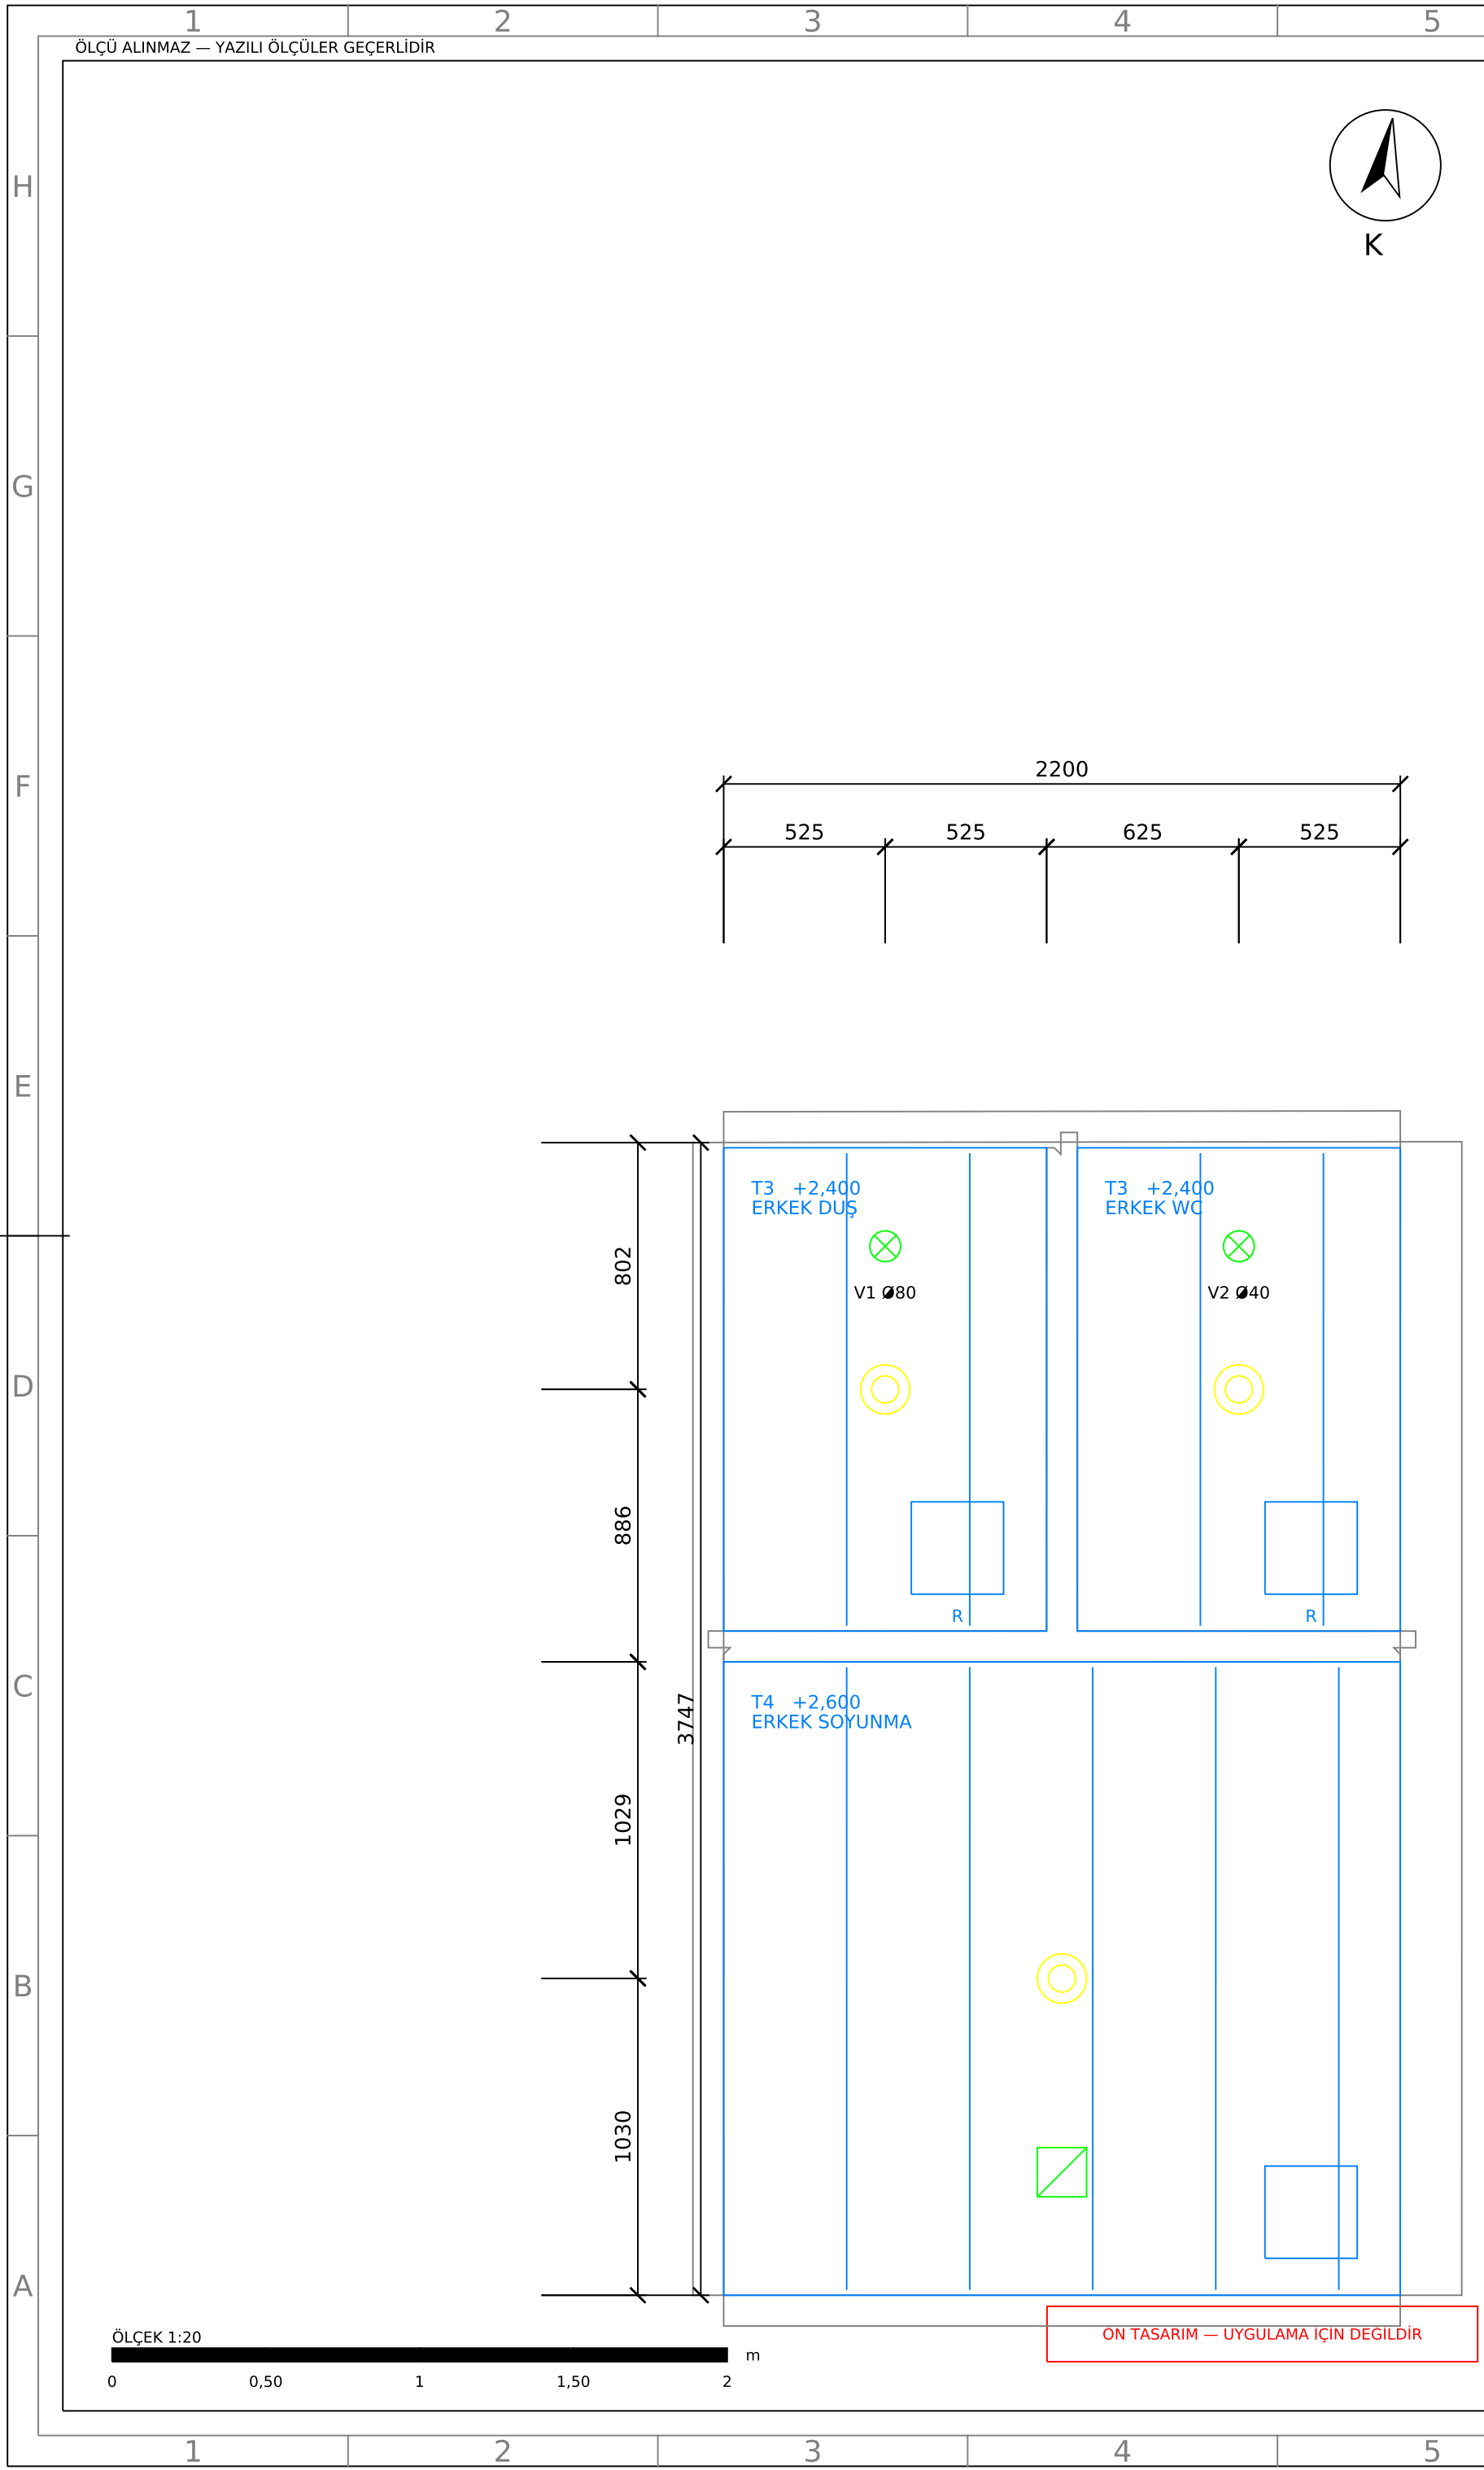

MALZEME VE EKİPMAN LİSTESİ

ASMA TAVAN

NO	MAHAL	TİP	KOT m	BOŞLUK mm
105	ERKEK SOYUNMA	T4	2,60	600
106	ERKEK DUŞ	T3	2,40	800
107	ERKEK WC	T3	2,40	800

TAVAN KATMANLARI

TİP	KATMAN VE İMALAT
T4	T2 ile aynı karkas ve kaplama
	Soyunma/duş sınırında kot geçiş bandı (dikme)
	Nem nedeniyle duş kapısı önünde 1,0 m şeridinde H2 alçıpan
T3	Galvaniz ayarlı askı @900 mm, TC47 / TU27 karkas
	12,5 mm H2 (su itici) alçıpan tek kat
	Su bazlı, küf önleyici yarı mat banyo boyası, 2 kat
	300×300 mm menteşeli revizyon kapağı (her ıslak hacimde 1 adet)

TAVAN CİHAZLARI

KOD	CİHAZ	ADET/DEBİ
L-1	IP44 downlight 18 W / 1800 lm	1 / mahal
V1	Egzoz valfi Ø80 — duş	80 m³/h
V2	Egzoz valfi Ø40 — WC	40 m³/h
R	Revizyon kapağı 300×300 menteşeli	1 / mahal
S1	Hareket sensörü — ıslak blok	1


LEJANT

- Mimari — asma tavan tipi sınırı
- Mimari — asma tavan tipi ve kotu
- Mimari — revizyon kapağı 300×300
- Kesit — arkada kalan / ikincil eleman
- Mekanik — menfez ve valf
- Mekanik — etiket ve not
- Elektrik — IP44 downlight
- Elektrik — acil aydınlatma / yönlendirme
- Genel — zincir ölçü

GENEL NOTLAR

- Tavan kotları bitmiş zemin kotundan ölçülür.
- Duş ve WC üzerinde T3 (H2 su itici alçıpan), soyunmada T4 kullanılır.
- Her ıslak hacimde 300×300 mm menteşeli revizyon kapağı bulunur.
- Armatür ve valf konumları koordinasyon kesiti P-03 ile çıkışma kontrolünden geçmiştir.

REV	TARİH	AÇIKLAMA	ÇZ	KT	ON
A	13.09.2026	İlk yayın — ön tasarım			
B	17.09.2026	Mühendis geri bildirimi işlendi			
C	18.09.2026	Geometri ölçülmüş röleveye taşındı (ESAT-FINAL.dwg)			
D	18.09.2026	Pilot bölge: ölçülü plan · tavan · kesit · görünüş · detay			
İŞVEREN ÖZEL — MALTEPE / İDEALTEPE PROJE					
YAPI / MAHAL Mevcut mağaza → fonksiyonel antrenman stüdyosu (fit-out)			DİSİPLİN MİMARİ		
PAFTA ADI TAVAN PLANI (RCP) — ERKEK ISLAK BLOK			PILOT BÖLGE — ERKEK ISLAK BLOK (105-106-107)		
PROJE MÜELLİFİ · ODA SİCİL NO — (proje müellifi imzası için ayrılmıştır) —					
ÇİZEN CC	KONTROL —		ONAY —		
TARİH 17 Eylül 2026	ÖLÇEK 1:20		BİRİM milimetre (mm)		
DURUM ÖN TASARIM	PAFTA NO P-02		REV D SONRAKİ: P-03		

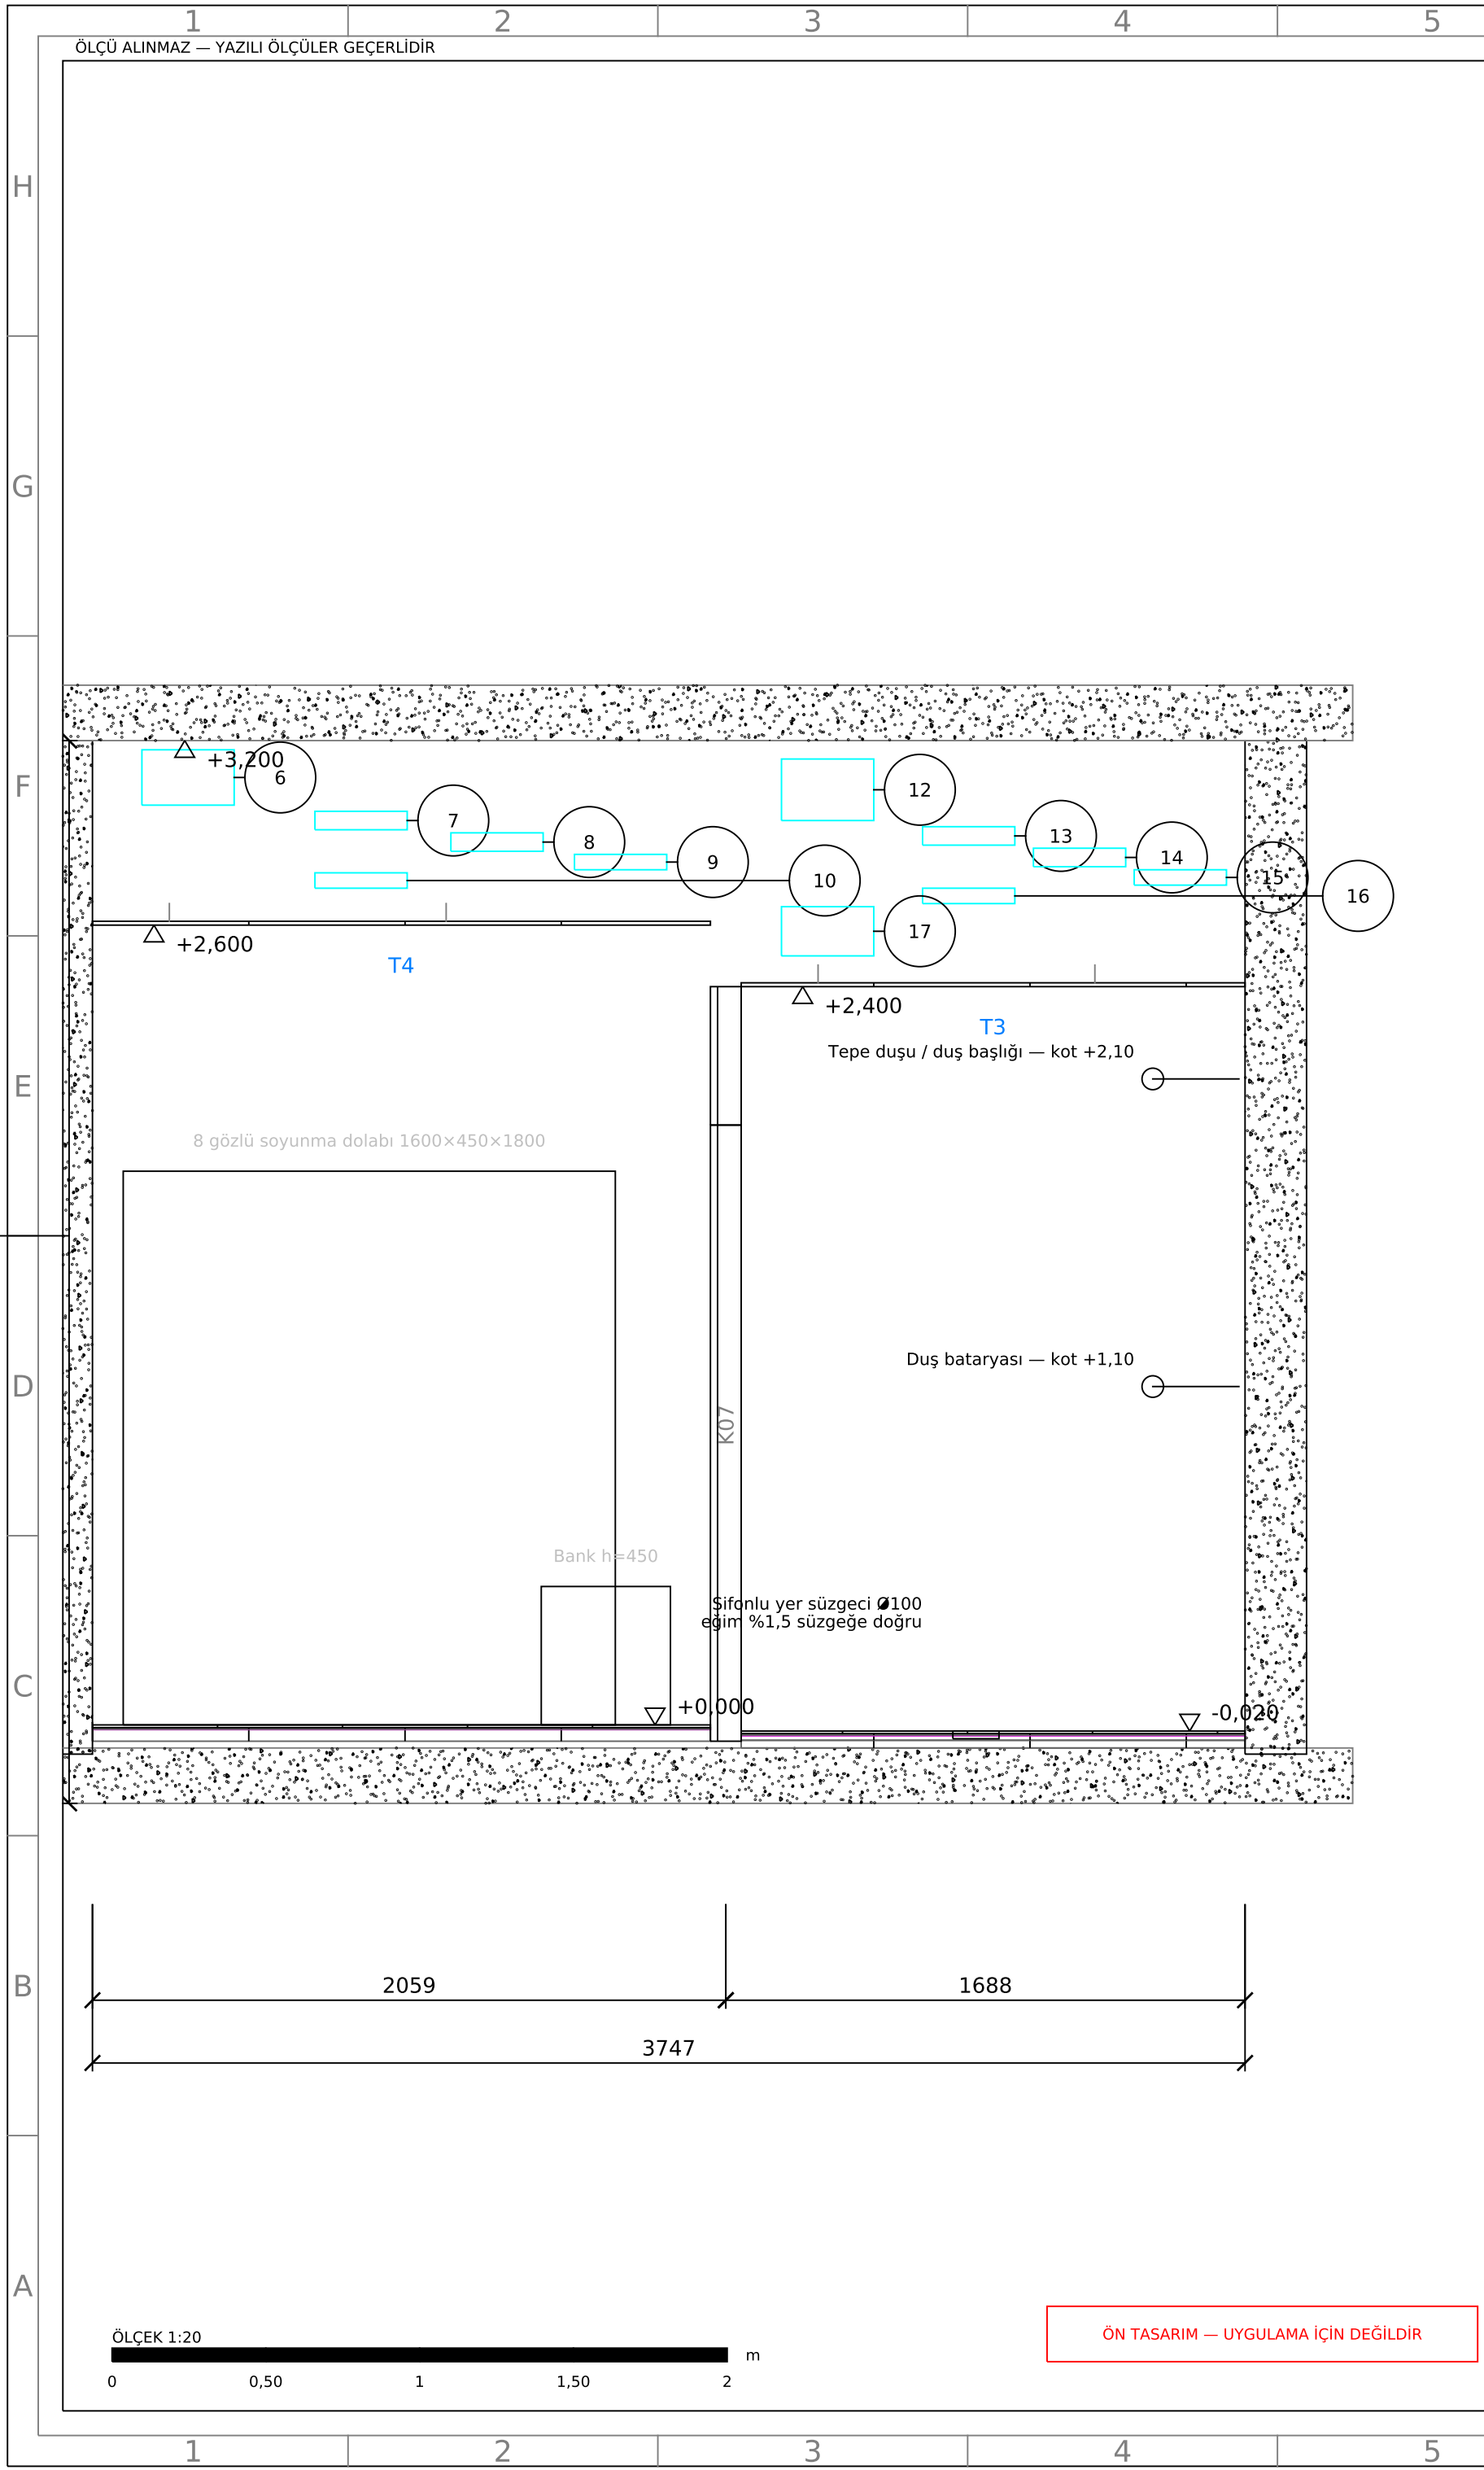

MALZEME VE EKİPMAN LİSTESİ

ZEMİN KATMANLARI

TİP	ZEMİN KATMANI (alttan üste)	mm
Z5	Mevcut betonarme döşeme / şap	mevcut
	Çimento esaslı tesviye şapı (kot eşitleme)	38
	Çimento esaslı su yalıtımı, tek kat (sıçrama koruması)	1
	C2TE yapıştırıcı	5
	Porselen seramik 600×600 mm, R10	9
Z4	Mevcut şap kırımı sonrası betonarme döşeme (tesisat boş)	mevcut
	Atık boru yatağı + tesisat şapı	25
	Eğim şapı — süzgeçe doğru %1,5	15
	Çimento esaslı 2 bileşenli su yalıtımı, 2 kat (köşelerde)	2
	C2TE S1 sınıfı yapıştırıcı	5
	Porselen seramik 300×300 mm, R11 / B kaymazlık	8

TAVAN İÇİ KOORDİNASYON (Nº kesitteki balon)

Nº	TAVAN	TAVAN İÇİ TESİSAT	ALT m	ÜST m
6	T4	Ana hava kanalı 400×200 mm + 25 mm izolasyon	2,990	3,170
7	T4	Soğutucu akışkan bakır hattı + klima drenajı (%1)	2,910	2,970
8	T4	Kablo tavası 200×60 mm — kuvvet ve aydınlatma	2,840	2,900
9	T4	Zayıf akım kanalı 100×50 mm — tavadan ≥ 200 mm	2,780	2,830
10	T4	Temiz su PPRC Ø25 (yalıtlımlı) — pis su ZEMİNDE	2,720	2,770
11	T4	Asma tavan askı + TC47 / TU27 taşıyıcı bölgesi	2,612	2,670
12	T3	Ana hava kanalı 400×200 mm + 25 mm izolasyon	2,940	3,140
13	T3	Soğutucu akışkan bakır hattı + klima drenajı (%1)	2,860	2,920
14	T3	Kablo tavası 200×60 mm — kuvvet ve aydınlatma	2,790	2,850
15	T3	Zayıf akım kanalı 100×50 mm — tavadan ≥ 200 mm	2,730	2,780
16	T3	Temiz su PPRC Ø25 (yalıtlımlı) — pis su ZEMİNDE	2,670	2,720
17	T3	Islak hacim egzoz kanalı Ø160 mm + izolasyon	2,500	2,660
18	T3	Asma tavan askı + TC47 / TU27 taşıyıcı bölgesi	2,413	2,470


LEJANT

- Mimari — kapı ve açılım
- Mimari — sabit mobilya
- Mimari — asma tavan tipi ve kotu
- Kesit — kesilen eleman çeperi
- Kesit — kesit düzlemi arkasında görünen
- Kesit — arkada kalan / ikincil eleman
- Kesit — malzeme taraması
- Kesit — mevcut betonarme döşeme ve duvar
- Detay — katman ayırım çizgisi
- Detay — su yalıtımı ve bandı
- Kot işareti ve değeri
- Kesit — tavan içi tesisat gövdesi
- Mekanik — etiket ve not
- Genel — zincir ölçü

GENEL NOTLAR

- Kesit düzlemi K1-K1; bakış yönü plan üzerinde gösterilmiştir.
- Tavan içi tesisat kotları tek kaynaktan (TAVAN_KATMAN) türetilir.
- Kesilen eleman 0,70 mm · görünen 0,35 mm · arkada kalan 0,18 mm (ISO 128-2).
- Mevcut döşeme kotu ve kalınlığı VARSAYIMDIR — söküm sonrası ölçülecektir.

REV	TARİH	AÇIKLAMA	ÇZ	KT	ON
A	13.09.2026	İlk yayın — ön tasarım			
B	17.09.2026	Mühendis geri bildirimi işlendi			
C	18.09.2026	Geometri ölçülmüş röleveye taşındı (ESAT-FINAL.dwg)			
D	18.09.2026	Pilot bölge: ölçülü plan · tavan · kesit · görünüş · detay			
İŞVEREN ÖZEL — MALTEPE / İDEALTEPE PROJE					
YAPI / MAHAL Mevcut mağaza → fonksiyonel antrenman stüdyosu (fit-out)			DISİPLİN KOORDİNASYON		
PAFTA ADI KOORDİNASYON KESİTİ K1-K1			PILOT BÖLGE — ERKEK ISLAK BLOK (105-106-107)		
PROJE MÜELLİFİ · ODA SİCİL NO — (proje müellifi imzası için ayrılmıştır) —					
ÇİZEN CC	KONTROL —		ONAY —		
TARİH 17 Eylül 2026	ÖLÇEK 1:20		BİRİM milimetre (mm)		
DURUM ÖN TASARIM	PAFTA NO P-03		REV D SONRAKİ: P-04		

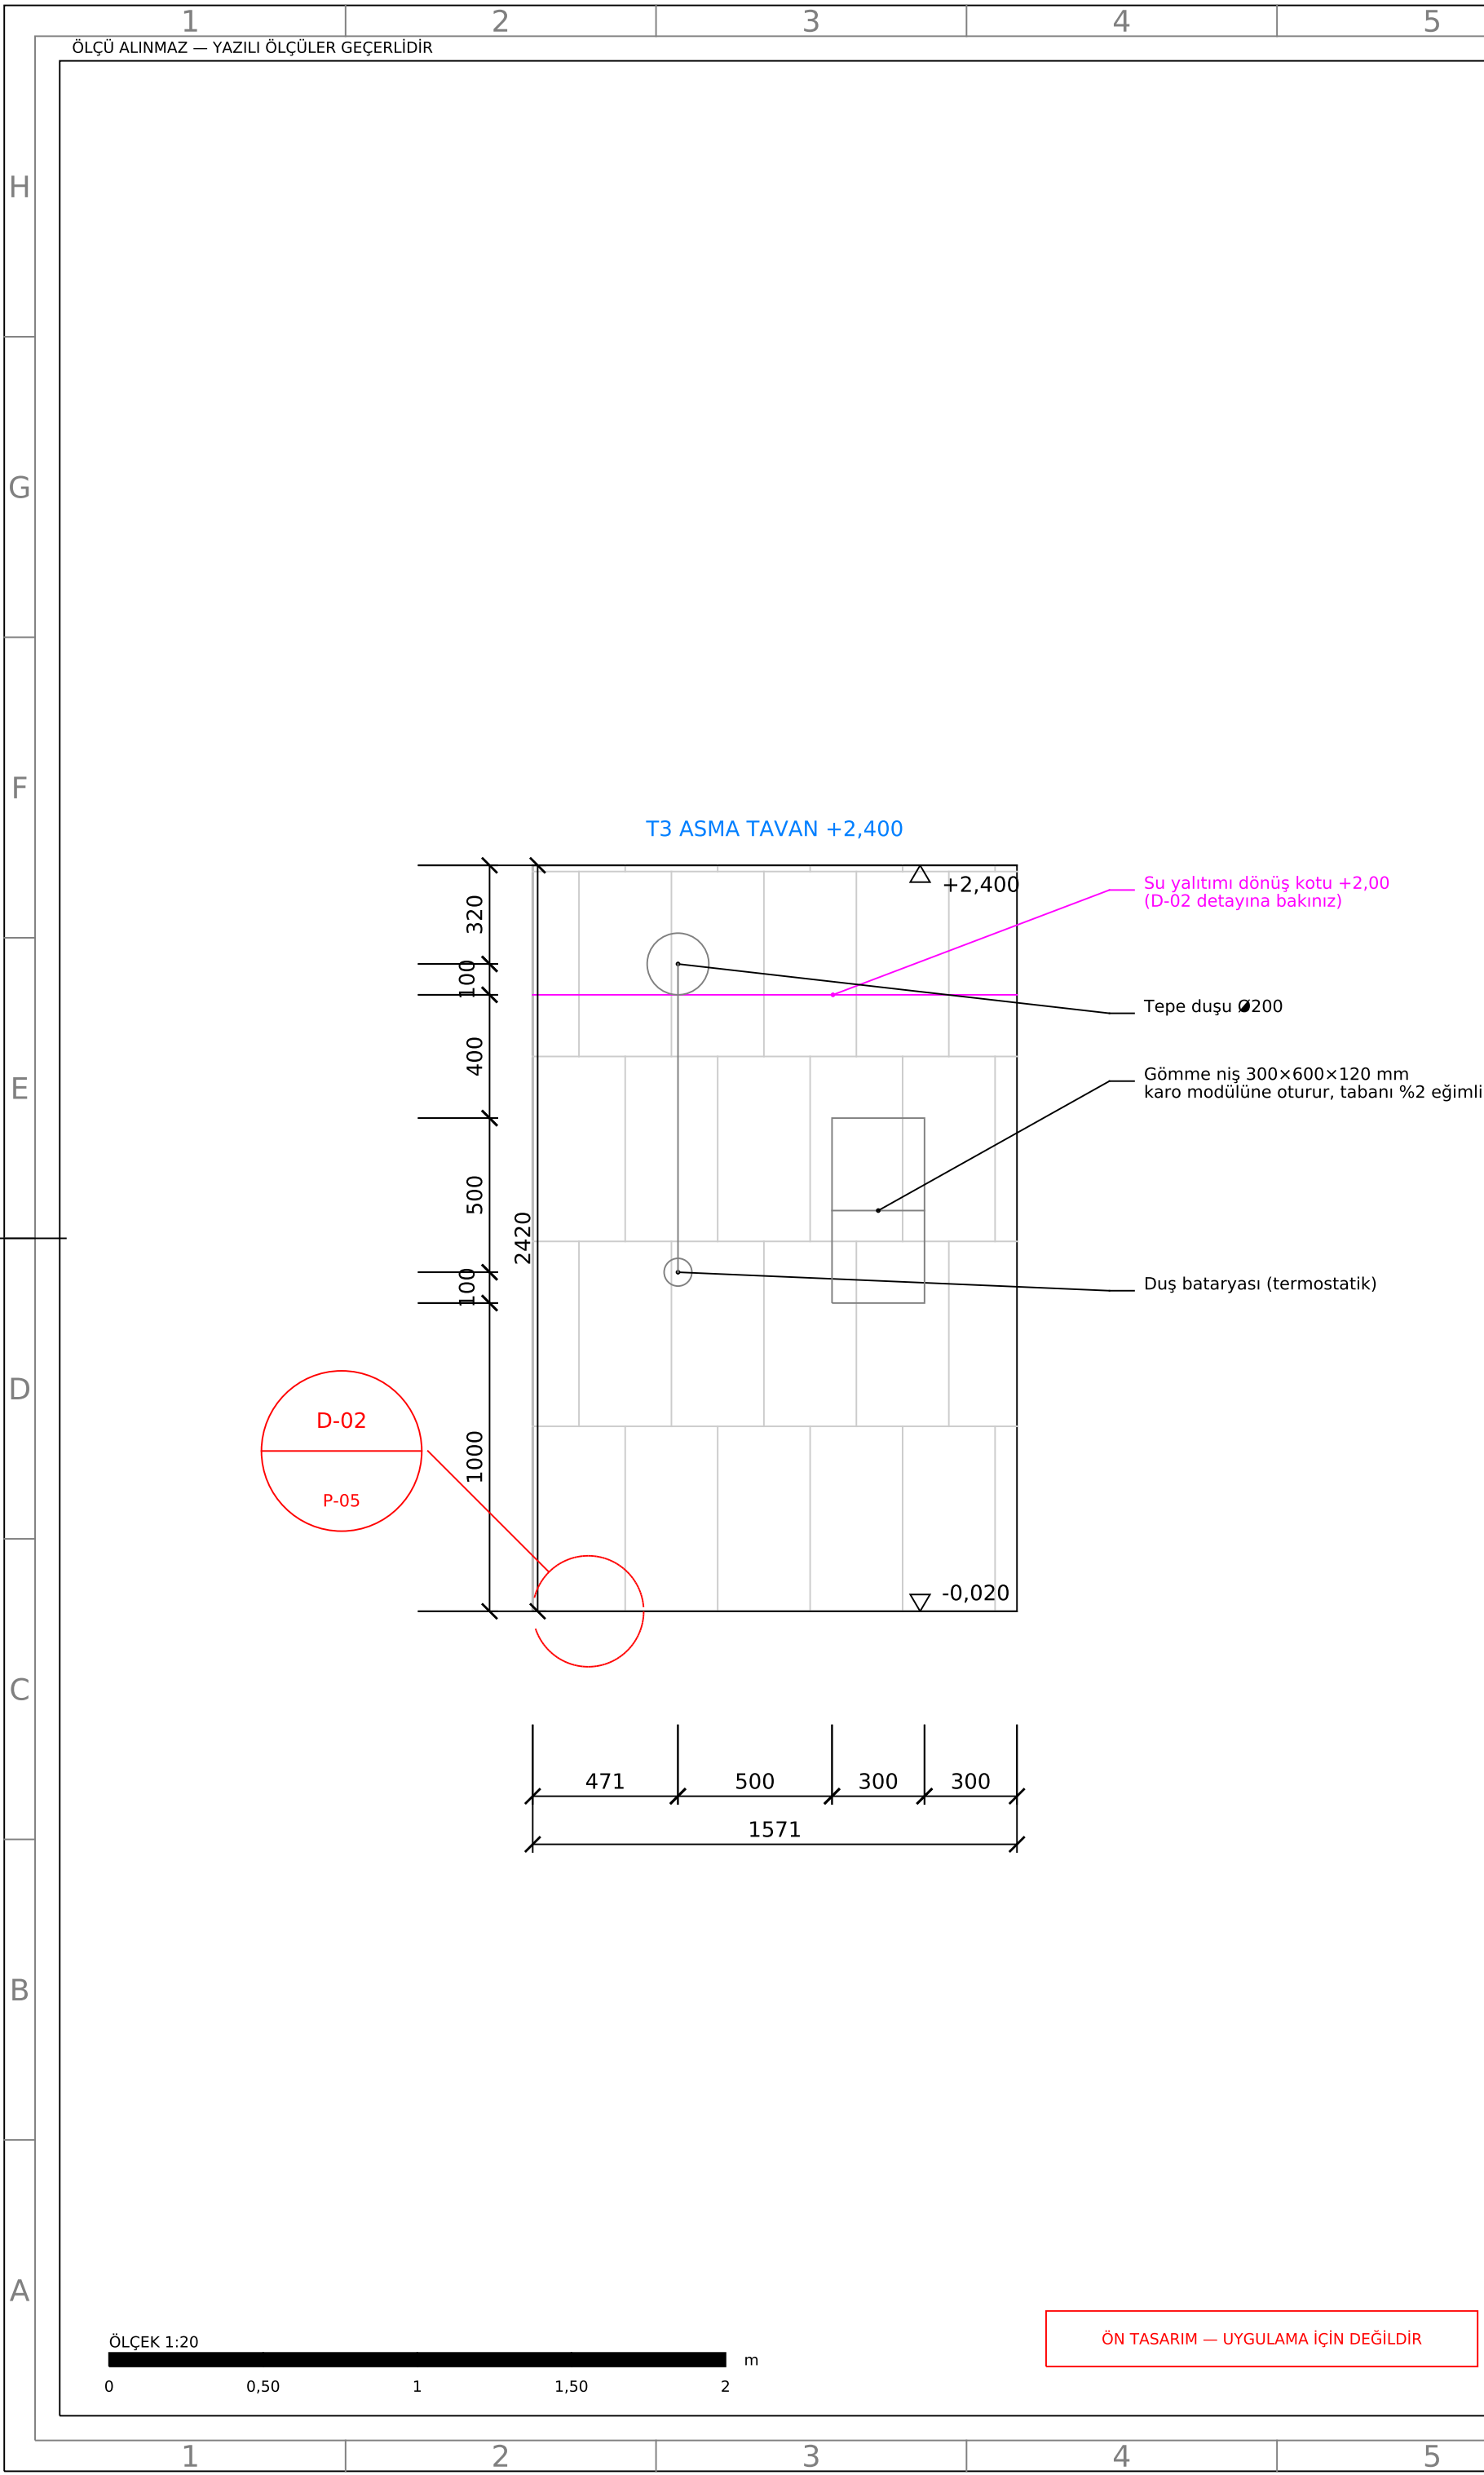

MALZEME VE EKİPMAN LİSTESİ

DUVAR YAPISI

D5 DUVAR KATMANI (içten dışa)	mm
Mevcut duvar veya D3 ıslak yüzü	200
Çimento esaslı 2 bileşenli su yalıtımı, 2 kat; köşe ve zemin birleşiminde 12 cm bandı	2
C2TE S1 yapıştırıcı	5
Porselen seramik 300×600 mm, rektifiye	9

KAPLAMA VE BİRLEŞİM

KALEM	TANIM
Karo	Porselen 300×600 mm rektifiye, düşey şaşırtmalı
Derz	CG2 WA çimento esaslı, 2 mm — köşelerde 25LM silikon
Yapıştırıcı	C2TE S1, çift taraflı sıvama (tam yapışma)
Yalıtım	EN 14891 çimento esaslı 2 bileşenli, 2 kat, +2,00 m
Süpürgelik	S3 — süpürgelik yok; karo zemine iner, kaveto profil

ARMATÜR VE DONATI KOTLARI

ELEMAN	TANIM	KOT m
Duş bataryası	termostatik, krom	+1,10
Tepe duşu	Ø200 paslanmaz	+2,10
Gömme niş	300×600×120 mm	+1,00
Duş kapağı K07	6 mm temperli cam 700×1950	+0,015


LEJANT

—	Mimari — mahal adı ve alan
—	Mimari — asma tavan tipi ve kotu
—	Detay — su yalıtımı ve bandı
—	Kot işareti ve değeri
—	İç görünüş — eleman dış sınırı
—	İç görünüş — iç bölüntü ve donatı
—	İç görünüş — seramik derz ızgarası
—	Detay çağrı balonu ve kopuş çizgisi
—	Mekanik — etiket ve not
—	Genel — zincir ölçü

GENEL NOTLAR

- Seramik 300×600 mm rektifiye, düşey derz şaşırtmalı (yarım kaydırma).
- Su yalıtımı duş kabiniinde +2,00 m'ye kadar döner (D-02 detayına bakınız).
- Batarya ve duş başlığı kotları bitmiş zeminden ölçülür.
- Derz ızgarası gerçek karo boyutundan üretilmiştir; dekoratif değildir.

REV	TARİH	AÇIKLAMA	ÇZ	KT	ON
A	13.09.2026	İlk yayın — ön tasarım			
B	17.09.2026	Mühendis geri bildirimi işlendi			
C	18.09.2026	Geometri ölçülmüş röleveye taşındı (ESAT-FINAL.dwg)			
D	18.09.2026	Pilot bölge: ölçülü plan · tavan · kesit · görünüş · detay			
İŞVEREN ÖZEL — MALTEPE / İDEALTEPE PROJE					
YAPI / MAHAL Mevcut mağaza → fonksiyonel antrenman stüdyosu (fit-out)			DISİPLİN İÇ MİMARİ		
PAFTA ADI İÇ GÖRÜNÜŞ G-05 — 106 DUŞ, BATI DUVARI			PILOT BÖLGE — ERKEK ISLAK BLOK (105-106-107)		
PROJE MÜELLİFİ · ODA SİCİL NO — (proje müellifi imzası için ayrılmıştır) —					
ÇİZEN CC	KONTROL —		ONAY —		
TARİH 17 Eylül 2026	ÖLÇEK 1:20		BİRİM milimetre (mm)		
DURUM ÖN TASARIM	PAFTA NO P-04		REV D SONRAKİ: P-05		

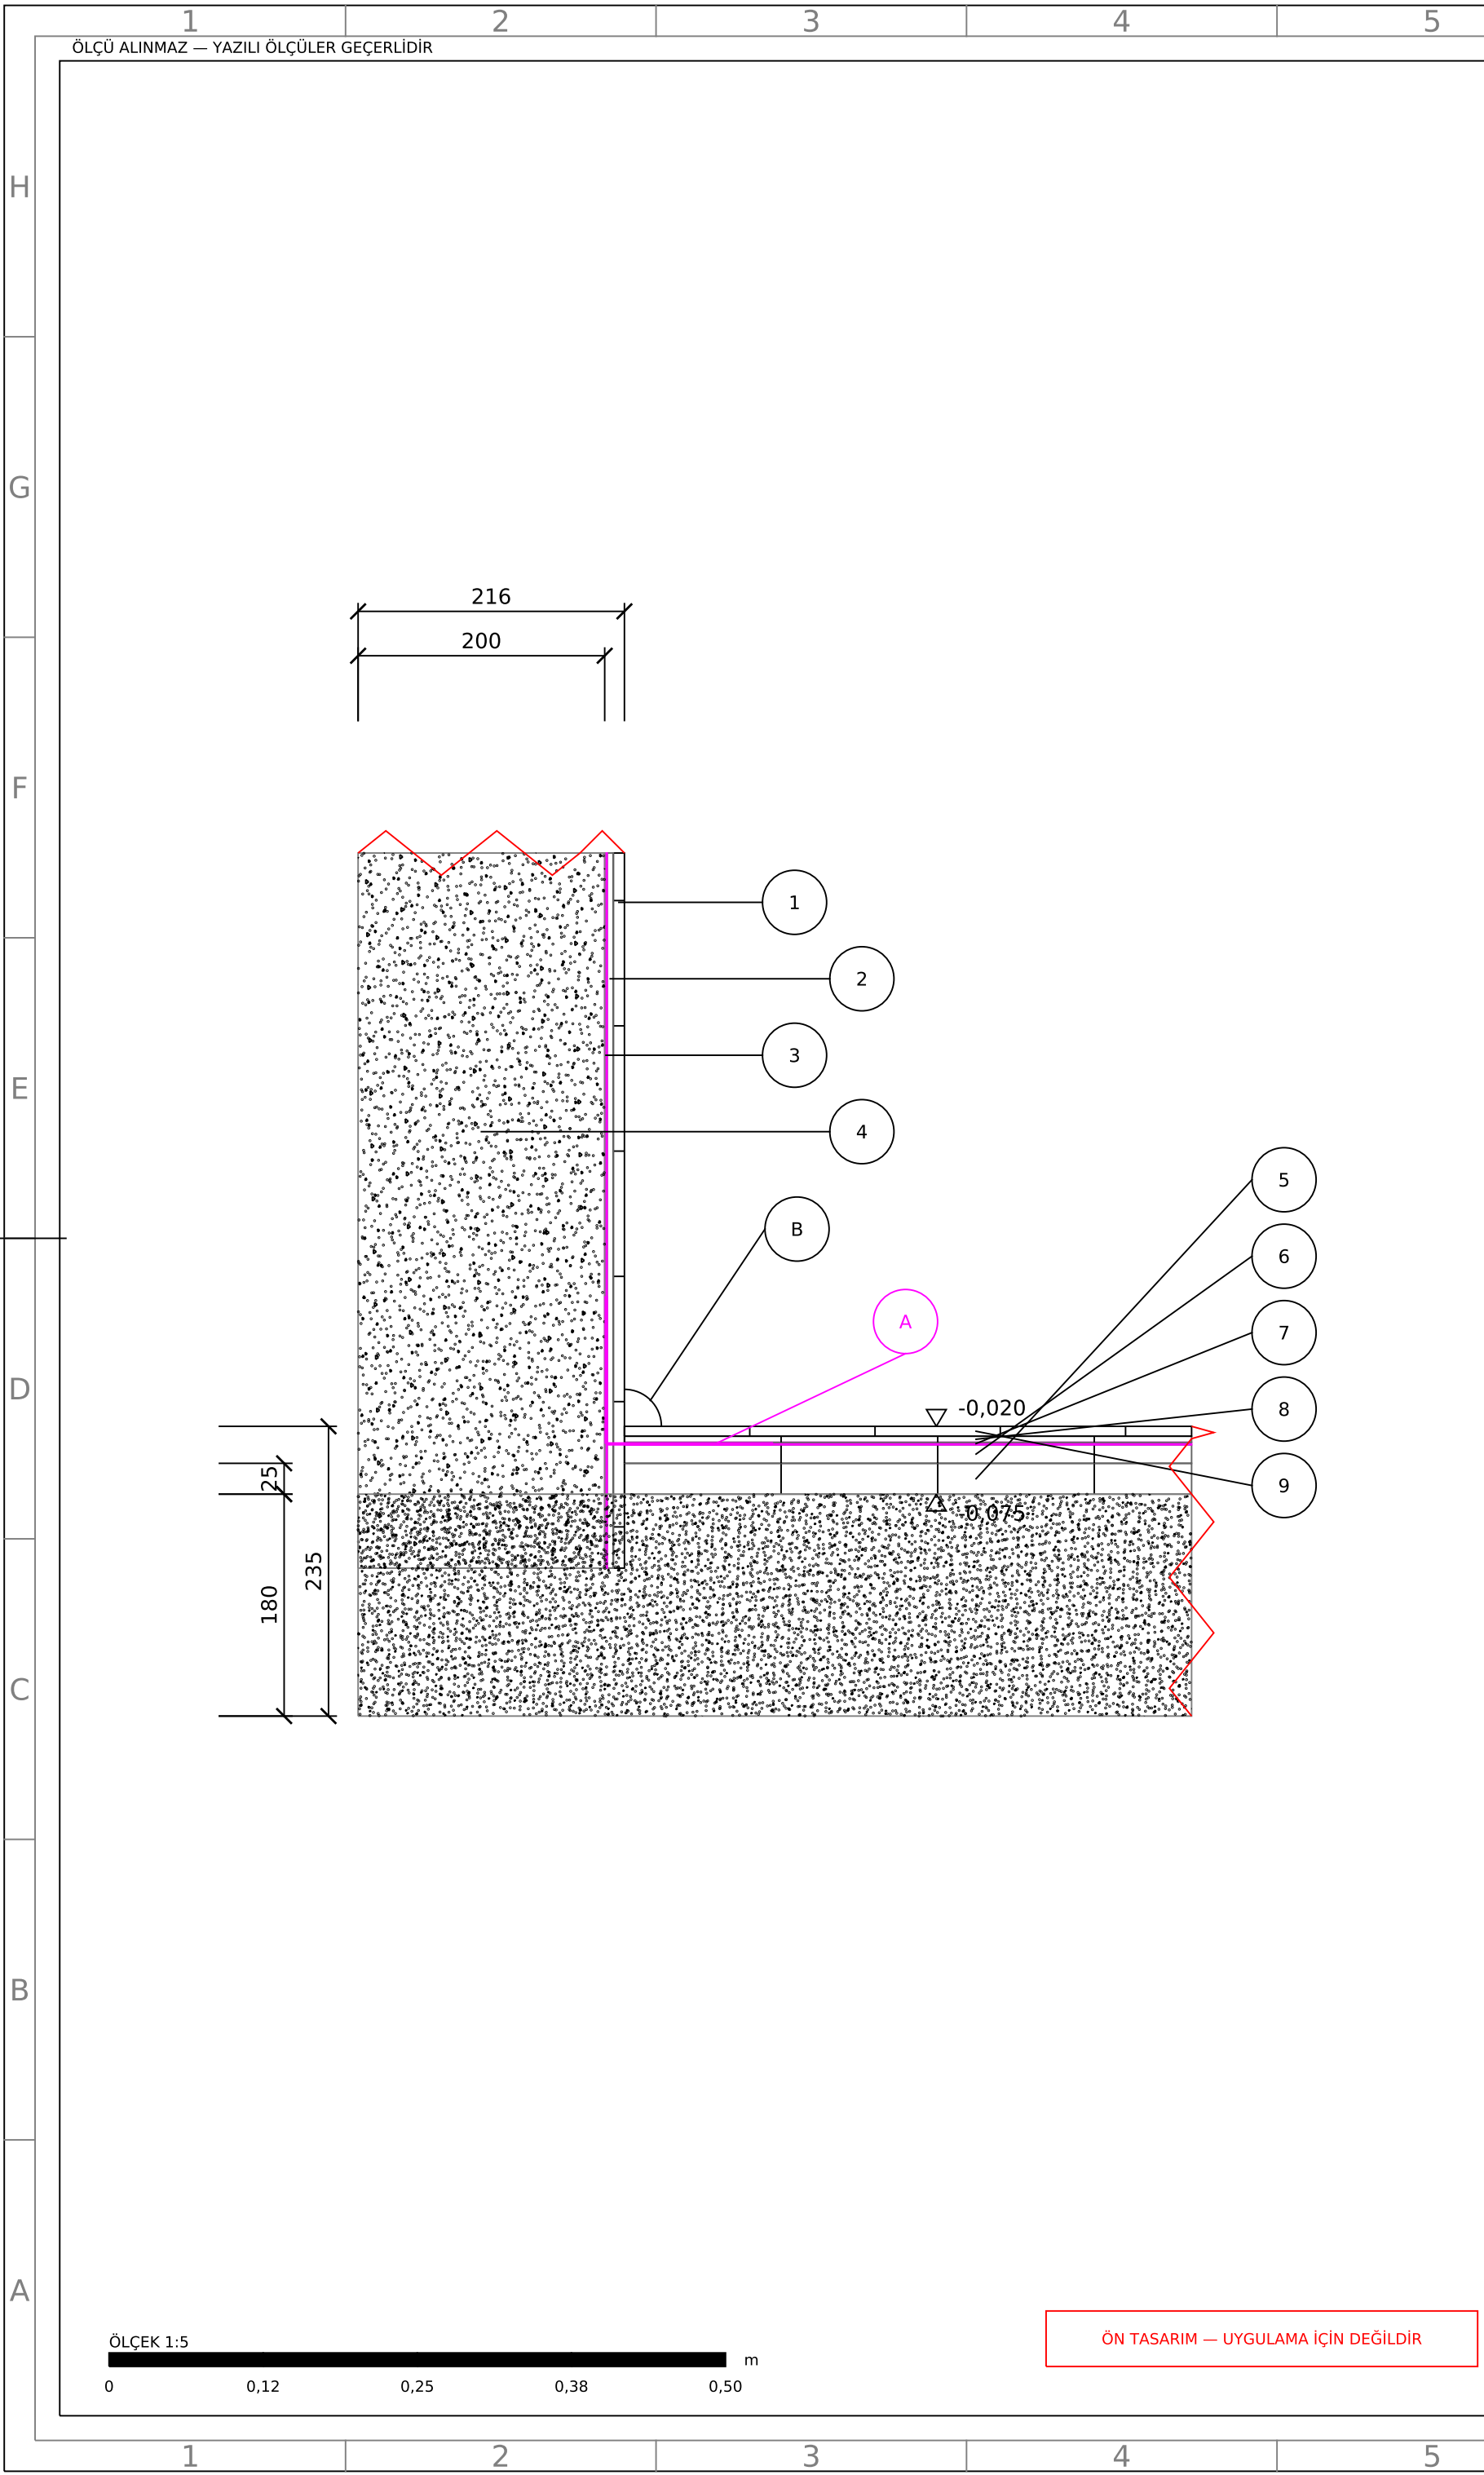

MALZEME VE EKİPMAN LİSTESİ

DETAY KATMAN LİSTESİ

Nº	GRUP	KATMAN	mm
1	D5 duvar	Porselen seramik 300×600 mm, rektifiye	9
2	D5 duvar	C2TE S1 yapıştırıcı	5
3	D5 duvar	Çimento esaslı 2 bileşenli su yalıtımı, 2 kat; köşe	2
4	D5 duvar	Mevcut duvar veya D3 ıslak yüzü	200
5	Z4 zemin	Atık boru yatağı + tesisat şapı	25
6	Z4 zemin	Eğim şapı — süzgeçe doğru %1,5	15
7	Z4 zemin	Çimento esaslı 2 bileşenli su yalıtımı, 2 kat (köşel	2
8	Z4 zemin	C2TE S1 sınıfı yapıştırıcı	5
9	Z4 zemin	Porselen seramik 300×300 mm, R11 / B kaymazlık	8

BİRLEŞİM NOTLARI

Nº	BİRLEŞİM ELEMANI
A	Elastik su yalıtım bandı 120 mm — yalıtımın iki katı arasına gömülür
B	S3 — süpürgelik yok; duvar karosu zemine iner, birleşimde içbükey (kaveto) porselen profil

DETAY NOTLARI

D-02 — UYGULAMA KURALI
Su yalıtımı duvarda en az 300 mm, duş kabinde 2000 mm yukarı döner.
Zemin-duvar köşesinde 120 mm elastik su yalıtım bandı, yalıtımın iki katı arasına gömülür.
Seramik derzi çimento esaslı (CG2 WA); köşe derzleri silikon (sınıf 25LM, küf önleyici).

UYGULANAN STANDARTLAR (aday — proje bazında doğrulanacak)

KAYNAK	KONU
EN 14891	Çimento esaslı su yalıtımı — sıvı uygulanan
EN 16165 Ek B	R11 kaymazlık — duş ve WC zemini
EN 12004 / C2TE S1	Seramik yapıştırıcısı, deforme olabilir
EN 13888 / CG2 WA	Derz dolgusu — su emmesi azaltılmış
ISO 11600 / 25LM	Köşe silikonu — küf önleyici

LEJANT

—	Mimari — mahal adı ve alan
—	Kesit — kesilen eleman çeperi
—	Kesit — malzeme taraması
—	Kesit — mevcut betonarme döşeme ve duvar
—	Detay — katman ayırım çizgisi
—	Detay — su yalıtımı ve bandı
—	Kot işareti ve değeri
—	Detay çağrı balonu ve kopuş çizgisi
—	Genel — zincir ölçü

GENEL NOTLAR

- Katman kalınlıkları Z4 zemin ve D5 duvar tip tablosundan gelir.
- Su yalıtımı zemin-duvar köşesinde 120 mm elastik bantla sürekliliği sağlar.
- Detay 1:5 ölçeğindedir; ölçü alınmaz, yazılı ölçüler geçerlidir.

REV	TARİH	AÇIKLAMA	ÇZ	KT	ON
A	13.09.2026	İlk yayın — ön tasarım			
B	17.09.2026	Mühendis geri bildirimi işlendi			
C	18.09.2026	Geometri ölçülmüş röleveye taşındı (ESAT-FINAL.dwg)			
D	18.09.2026	Pilot bölge: ölçülü plan · tavan · kesit · görünüş · detay			
İŞVEREN ÖZEL — MALTEPE / İDEALTEPE PROJE					
YAPI / MAHAL Mevcut mağaza → fonksiyonel antrenman stüdyosu (fit-out)			DISİPLİN DETAY		
PAFTA ADI BİRLEŞİM DETAYI D-02 — Z4 ZEMİN / D5 DUVAR SU YALITIMI			SU YALITIMI DUYULAN İSLAK BLOK (105-106-107)		
PROJE MÜELLİFİ · ODA SİCİL NO — (proje müellifi imzası için ayrılmıştır) —					
ÇİZEN CC	KONTROL —		ONAY —		
TARİH 17 Eylül 2026	ÖLÇEK 1:5		BİRİM milimetre (mm)		
DURUM ÖN TASARIM	PAFTA NO P-05		REV D		