


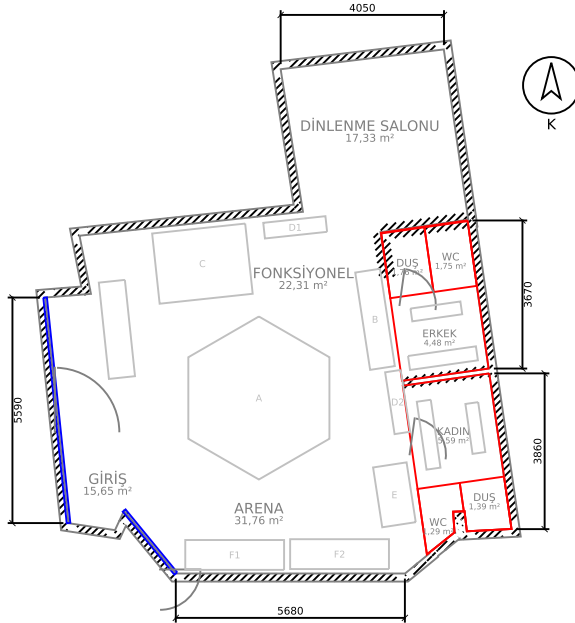

LEJANT

- Mimari — mevcut duvar (korunuyor)
 — Mimari — yeni alçıpan bölme

NOTLAR

Mimari altlık — mevcut duvar korunur.
 Kırmızı: yeni alçıpan bölme.
 Ölçüler raster paktan (+/-%3).

PROJE
 MALTEPE / İDEALTEPE — GYM DÖNÜŞÜMÜ

DISİPLİN
 MİMARİ

PAFTA ADI
 MİMARİ ALTLIK

PAFTA NO
 A-01

TARİH
 13 Eylül 2026


BİRİM
 milimetre (mm)

ÖLÇEK
 1 / 75

REVİZYON
 Rev C

DURUM
 ÖN TASARIM

Yerinde doğrulanmadan ve ruhsat alınmadan uygulama yapılamaz.

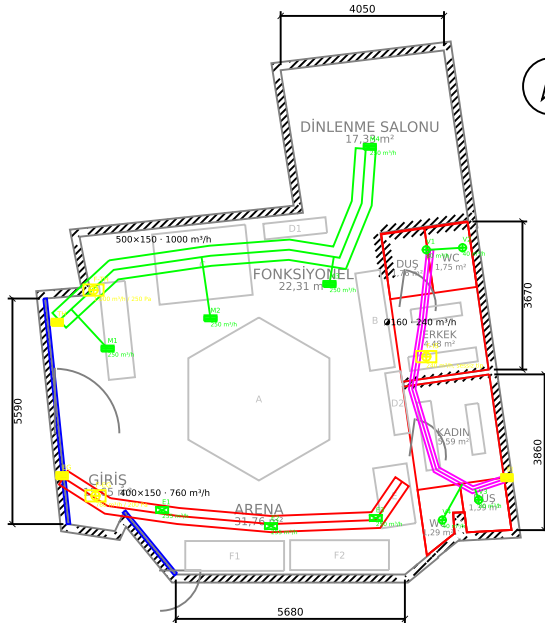

LEJANT

- Mimari — mevcut duvar (korunuyor)
- Mimari — yeni alçıpan bölme
- Mekanik — taze hava kanalı
- Mekanik — egzoz kanalı
- Mekanik — ıslak hacim egzoz kanalı
- Mekanik — menfez ve valf
- Mekanik — menfez bransmanı
- Mekanik — fan ve panjür
- Mekanik — etiket ve not

NOTLAR

Kanallar galvaniz sac, TS EN 1507 sınıf B.
Besleme ve egzoz hattı 19 mm izoleli.
Her bransman baskı debi ayar damperi.
Devreye almada balanslama ve ölçüm raporu.

PROJE

MALTEPE / İDEALTEPE — GYM DÖNÜŞÜMÜ

DISİPLİN

MEKANİK TESİSAT

PAFTA ADI
HAVALANDIRMA PLANI

PAFTA NO
M-01

ÖLÇEK
1/75

TARİH
13 Eylül 2026

REVİZYON
Rev C

BİRİM
milimetre (mm)

DURUM
ÖN TASARIM


Yerinde doğrulanmadan ve ruhsat alınmadan uygulama yapılamaz.

LEJANT

- Mimari — mevcut duvar (korunuyor)
- Mimari — yeni alçıpan bölme
- Mekanik — klima iç ünite
- Mekanik — klima dış ünite platformu
- Mekanik — soğutucu akışkan bakır hattı
- Mekanik — klima drenaj hattı
- Mekanik — etiket ve not

NOTLAR

İç ünite montaj kotu 2,40 m (alt kot).
Bakır hat izoleli, dış ünite konsolu
titresim takozlu.
Drenaj %1 eğimli.

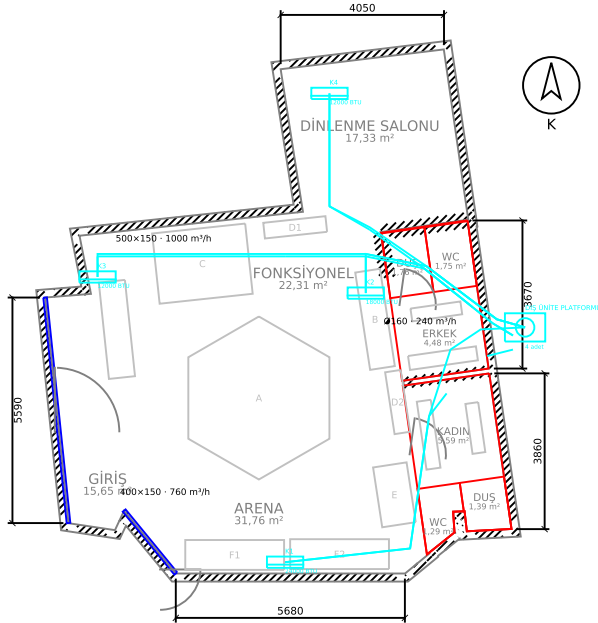

PROJE

MALTEPE / İDEALTEPE — GYM DÖNÜŞÜMÜ

DISİPLİN

MEKANİK TESİSAT

PAFETA ADI
İKLİMLENDİRME PLANI

PAFETA NO
M-02

ÖLÇEK
1/75


TARİH
13 Eylül 2026

REVİZYON
Rev C

BİRİM
milimetre (mm)

DURUM
ÖN TASARIM

Yerinde doğrulanmadan ve ruhsat alınmadan uygulama yapılamaz.

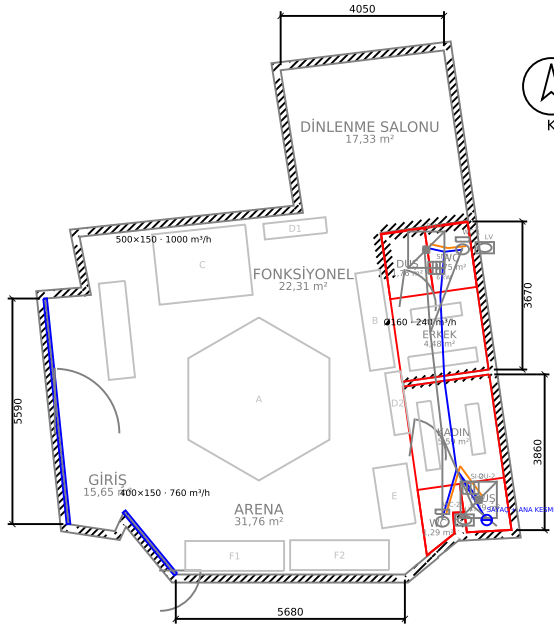

LEJANT

- Mimari — mevcut duvar (korunuyor)
- Mimari — yeni alçıpan bölme
- Mekanik — temiz su PPRC
- Mekanik — sıcak su PPRC izoleli
- Mekanik — pis su PVC
- Mekanik — vitrifiye ve su ısıtıcı
- Mekanik — etiket ve not

NOTLAR

Pis su %2 eğimli.
Tüm ıslak hacimde sifonlu yer suzgeci.
SOKUM SONRASI İLK İS: mevcut pis su bağlantı kotunun ölçülmesi.

PROJE
MALTEPE / İDEALTEPE — GYM DÖNÜŞÜMÜ

DİSİPLİN
MEKANİK TESİSAT

PAFTA ADI
SİHHİ TESİSAT PLANI

PAFTA NO
M-03

TARİH
13 Eylül 2026


BİRİM
milimetre (mm)

ÖLÇEK
1 / 75

REVİZYON
Rev C

DURUM
ÖN TASARIM

Yerinde doğrulanmadan ve ruhsat alınmadan uygulama yapılamaz.

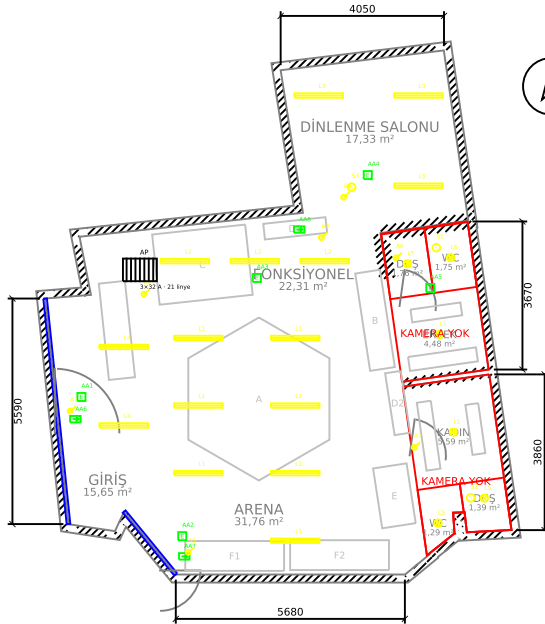

LEJANT

- Mimari — mevcut duvar (korunuyor)
- Mimari — yeni alçıpan bölme
- Elektrik — lineer LED armatür
- Elektrik — IP44 downlight
- Elektrik — acil aydınlatma / yönlendirme
- Elektrik — anahtar ve sensör
- Elektrik — ana dağıtım panosu
- Elektrik — etiket ve not

NOTLAR

Tesisat sıva altı spiral boru içinde,
NHXMH halojensiz kablo.
Acil aydınlatma 3 saat bataryalı.

PROJE

MALTEPE / İDEALTEPE — GYM DÖNÜŞÜMÜ

DİSİPLİN ELEKTRİK

PAFTA ADI AYDINLATMA PLANI

PAFTA NO
E-01

TARİH
13 Eylül 2026

BİRİM
milimetre (mm)

ÖLÇEK
1/75

REVİZYON
Rev C

DURUM
ÖN TASARIM


Yerinde doğrulanmadan ve ruhsat alınmadan uygulama yapılamaz.

— Mimari — mevcut duvar (korunuyor)
 — Mimari — yeni alçıpan bölme
 — Elektrik — priz
 — Elektrik — klima/ısıtıcı/fan beslemesi
 — Elektrik — ana dağıtım panosu
 — Elektrik — etiket ve not

Islak hacim linyeleri ayrı 30 mA
kacak akım rolesinden beslenir.
Kardiyo ekipmanı ayrı linyede (P4).



PROJE	
MALTEPE / İDEALTEPE — GYM DÖNÜŞÜMÜ	
DİSİPLİN ELEKTRİK	
PAFTA ADI PRİZ VE KUVVET PLANI	
PAFTA NO E-02	ÖLÇEK 1 / 75
TARİH 13 Eylül 2026	REVİZYON Rev C
BİRİM milimetre (mm)	DURUM ÖN TASARIM
Yerinde doğrulanmadan ve ruhsat alınmadan uygulama yapılamaz.	

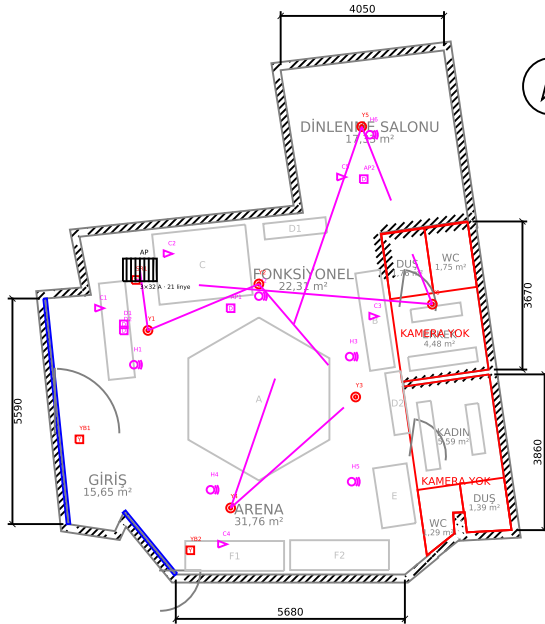

LEJANT

- Mimari — mevcut duvar (korunuyor)
- Mimari — yeni alçıpan bölme
- Elektrik — IP kamera
- Elektrik — tavan hoparlörü
- Elektrik — veri prizi ve rack
- Elektrik — dedektör, buton, siren
- Elektrik — yangın algılama çevrimi
- Elektrik — ana dağıtım panosu
- Elektrik — etiket ve not

NOTLAR

SOYUNMA VE WC İCİNE KAMERA KONULMAZ.
Yangın algılama panosu kesintisiz beslenir.
Topraklama direnci ≤ 10 ohm.

PROJE

MALTEPE / İDEALTEPE — GYM DÖNÜŞÜMÜ

DİSİPLİN
ELEKTRİK

PAFTA ADI
ZAYIF AKIM PLANI

PAFTA NO
E-03

TARİH
13 Eylül 2026


BİRİM
milimetre (mm)

Yerinde doğrulanmadan ve ruhsat alınmadan uygulama yapılamaz.

ÖLÇEK
1/75

REVİZYON
Rev C

DURUM
ÖN TASARIM

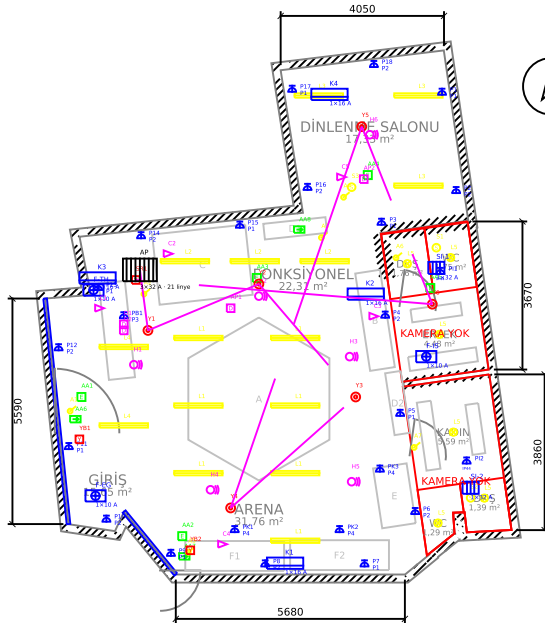

LEJANT

- Mimari — mevcut duvar (korunuyor)
- Mimari — yeni açılan bölme
- Elektrik — lineer LED armatür
- Elektrik — IP44 downlight
- Elektrik — acil aydınlatma / yönlendirme
- Elektrik — anahtar ve sensör
- Elektrik — priz
- Elektrik — klima/sıtıcı/fan beslemesi
- Elektrik — IP kamera
- Elektrik — tavan hoparlörü
- Elektrik — veri prizi ve rack
- Elektrik — dedektör, buton, siren
- Elektrik — yangın algılama çevrimi
- Elektrik — ana dağıtım panosu
- Elektrik — etiket ve not

NOTLAR

Elektrik disiplin genel yerleşimi.

Ayrıntı için E-01, E-02, E-03 paftaları.

PROJE

MALTEPE / İDEALTEPE — GYM DÖNÜŞÜMÜ

DISİPLİN
ELEKTRİK

PAFTA ADI
ELEKTRİK GENEL YERLEŞİM

PAFTA NO
E-04

ÖLÇEK
1/75

TARİH
13 Eylül 2026

REVİZYON
Rev C

BİRİM
milimetre (mm)

DURUM
ÖN TASARIM

Yerinde doğrulanmadan ve ruhsat alınmadan uygulama yapılamaz.