

MALTEPE / İDEALTEPE

MOBİLYA MAĞAZASI → FONKSİYONEL ANTRENMAN STÜDYOSU

UYGULAMA PROJESİ — MİMARİ · MEKANİK · ELEKTRİK

Proje no	GYM-25-001
Yapı	İdealtepe Mah. · zemin kat dükkân · 103,78 m² iç alan
İç alan	103,78 m²
Tarih	17 Eylül 2026
Revizyon	Rev H
Pafta boyutu	A1 (841×594) planlar · A3 (420×297) şemalar
Ölçek	Planlar 1:50 · şemalar ölçeksiz
Standartlar	TS EN ISO 5457 · TS EN ISO 7200 · ISO 128 · ISO 3098 · IEC 60617 · IEC 61439 · IEC 81346-2

PAFTA İNDEKSİ

BÖLÜM 1 — MİMARİ

A-01	MİMARİ ALTLIK	Mevcut durum · ölçü ve aks sistemi · 1:50
A-02	MİMARİ UYGULAMA PLANI	Bölme duvarlar · kapılar · mahal no · 1:50
A-03	ZEMİN KAPLAMA PLANI	Kaplama tipleri · kot · derz yönü · 1:50
A-04	TAVAN PLANI (RCP)	Tavan tipleri · kot · MEP koordinasyonu · 1:50
A-05	YANGIN VE TAHLİYE PLANI	Kaçış yolları · çıkışlar · söndürücü · 1:50

BÖLÜM 2 — MEKANİK TESİSAT

M-01	HAVALANDIRMA PLANI	Kanal güzergâhı · menfez debileri · 1:50
M-02	İKLİMLENDİRME PLANI	Split küme · bakır hat · drenaj · 1:50
M-03	SIHHİ TESİSAT PLANI	Temiz su · sıcak su · pis su · 1:50
M-04	MEKANİK GENEL YERLEŞİM	Disiplin genel yerleşimi · 1:50

BÖLÜM 3 — ELEKTRİK

E-01	AYDINLATMA PLANI	Armatür · anahtar · aydınlatma linyeleri · 1:50
E-02	PRİZ VE KUVVET PLANI	Priz · kuvvet linyeleri · cihazlar · 1:50
E-03	ZAYIF AKIM PLANI	Veri · CCTV · ses · yangın algılama · 1:50
E-04	ELEKTRİK GENEL YERLEŞİM	Disiplin genel yerleşimi · 1:50
E-05	TOPRAKLAMA PLANI	Elektrot grubu · ATB · EPDB · 1:50


BÖLÜM 4 — ADP ÇOK HATLI ŞEMA SETİ (A3)

ADP-01	Cover Sheet / Kapak
ADP-02	Panel Characteristics / Pano Karakteristiği
ADP-03	Symbol List / Sembol Listesi
ADP-04	Incoming Supply / Ana Besleme
ADP-05	Schematic Diagram / Şematik Diyagram
ADP-06	Schematic Diagram / Şematik Diyagram
ADP-07	Schematic Diagram / Şematik Diyagram
ADP-08	Schematic Diagram / Şematik Diyagram
ADP-09	Terminal Diagram / Klemens Planı
ADP-10	Panel Overview / Pano Önden Görünüş
ADP-11	Load Schedule / Yükleme Cetveli
ADP-12	Parts List / Malzeme Listesi

OKUMA NOTLARI

- Bu set ön tasarım aşamasındadır; yerinde röleve alınmadan ve ruhsat alınmadan uygulama yapılamaz.
- Ölçü alınmaz — yazılı ölçüler geçerlidir. Tüm ölçüler milimetredir.
- Aks sistemi yapının kendi doğrultusuna kurulmuştur (kuzeye göre 8,0°).
- Elektrik linye güzergâhları ortogonaldır; çapraz hat yoktur.
- Aydınlatma linyelerinde B eğrili, priz ve motor linyelerinde C eğrili kesici kullanılır.
- Ana kaçak akım rölesi ana şalterle orantılıdır (4×32 A → 4×40 A 300 mA S tipi).
- Yedek linyeler dâhil tüm son devreler 30 mA kaçak akım rölesi arkasındadır; yangın algılama paneli hariç.
- Mimari altlık tüm disiplin paftalarında ortaktır ve değiştirilmez.

REV	TARİH	AÇIKLAMA	ÇZ	KT	ON
A	17.09.2026	İlk yayın — ön tasarım	CC	—	—
B	18.09.2026	Aks sistemi, zincir ölçü, ISO 5457/7200 pafta	CC	—	—
C	18.09.2026	A1 pafta, tekil DXF, ADP şeması CAD'de	CC	—	—
D	18.09.2026	ADP çok hatlı şema (faz ayrımı), B eğrisi, ana RCD	CC	—	—
İŞVEREN					
ÖZEL — MALTEPE / İDEALTEPE					
PROJE					
MOBİLYA MAĞAZASI → FONKSİYONEL ANTRENMAN STÜDYOSU					
YAPI / MAHAL			DİSİPLİN		
İdealtepe Mah. · zemin kat dükkân · 103,78 m² iç alan			GENEL		
PAFTA ADI					
PAFTA İNDEKSİ			Proje kapağı ve pafta listesi		
PROJE MÜELLİFİ · ODA SİCİL NO					
— Oda sicil no: —					
ÇİZEN		KONTROL	ONAY		A
CC		—	—		
TARİH		ÖLÇEK	BİRİM		
17 Eylül 2026		—	milimetre (mm)		
DURUM		PAFTA NO	REV		
ÖN TASARIM		00	H		SONRAKİ: A-01

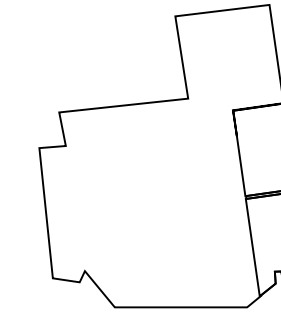


LEJANT

- Mimari — mevcut duvar (korunuyor)
- Mimari — yeni alçıpan bölme
- Mimari — cephe doğraması
- Mimari — kapı ve açılım
- Mimari — spor ekipmanı (işverence temin)
- Mimari — sabit mobilya
- Mimari — mahal adı ve alan

GENEL NOTLAR

- Mimari altlık — mevcut duvar korunur.
- Kırmızı: yeni alçıpan bölme.
- Ölçüler raster paftadan (+/-%3).

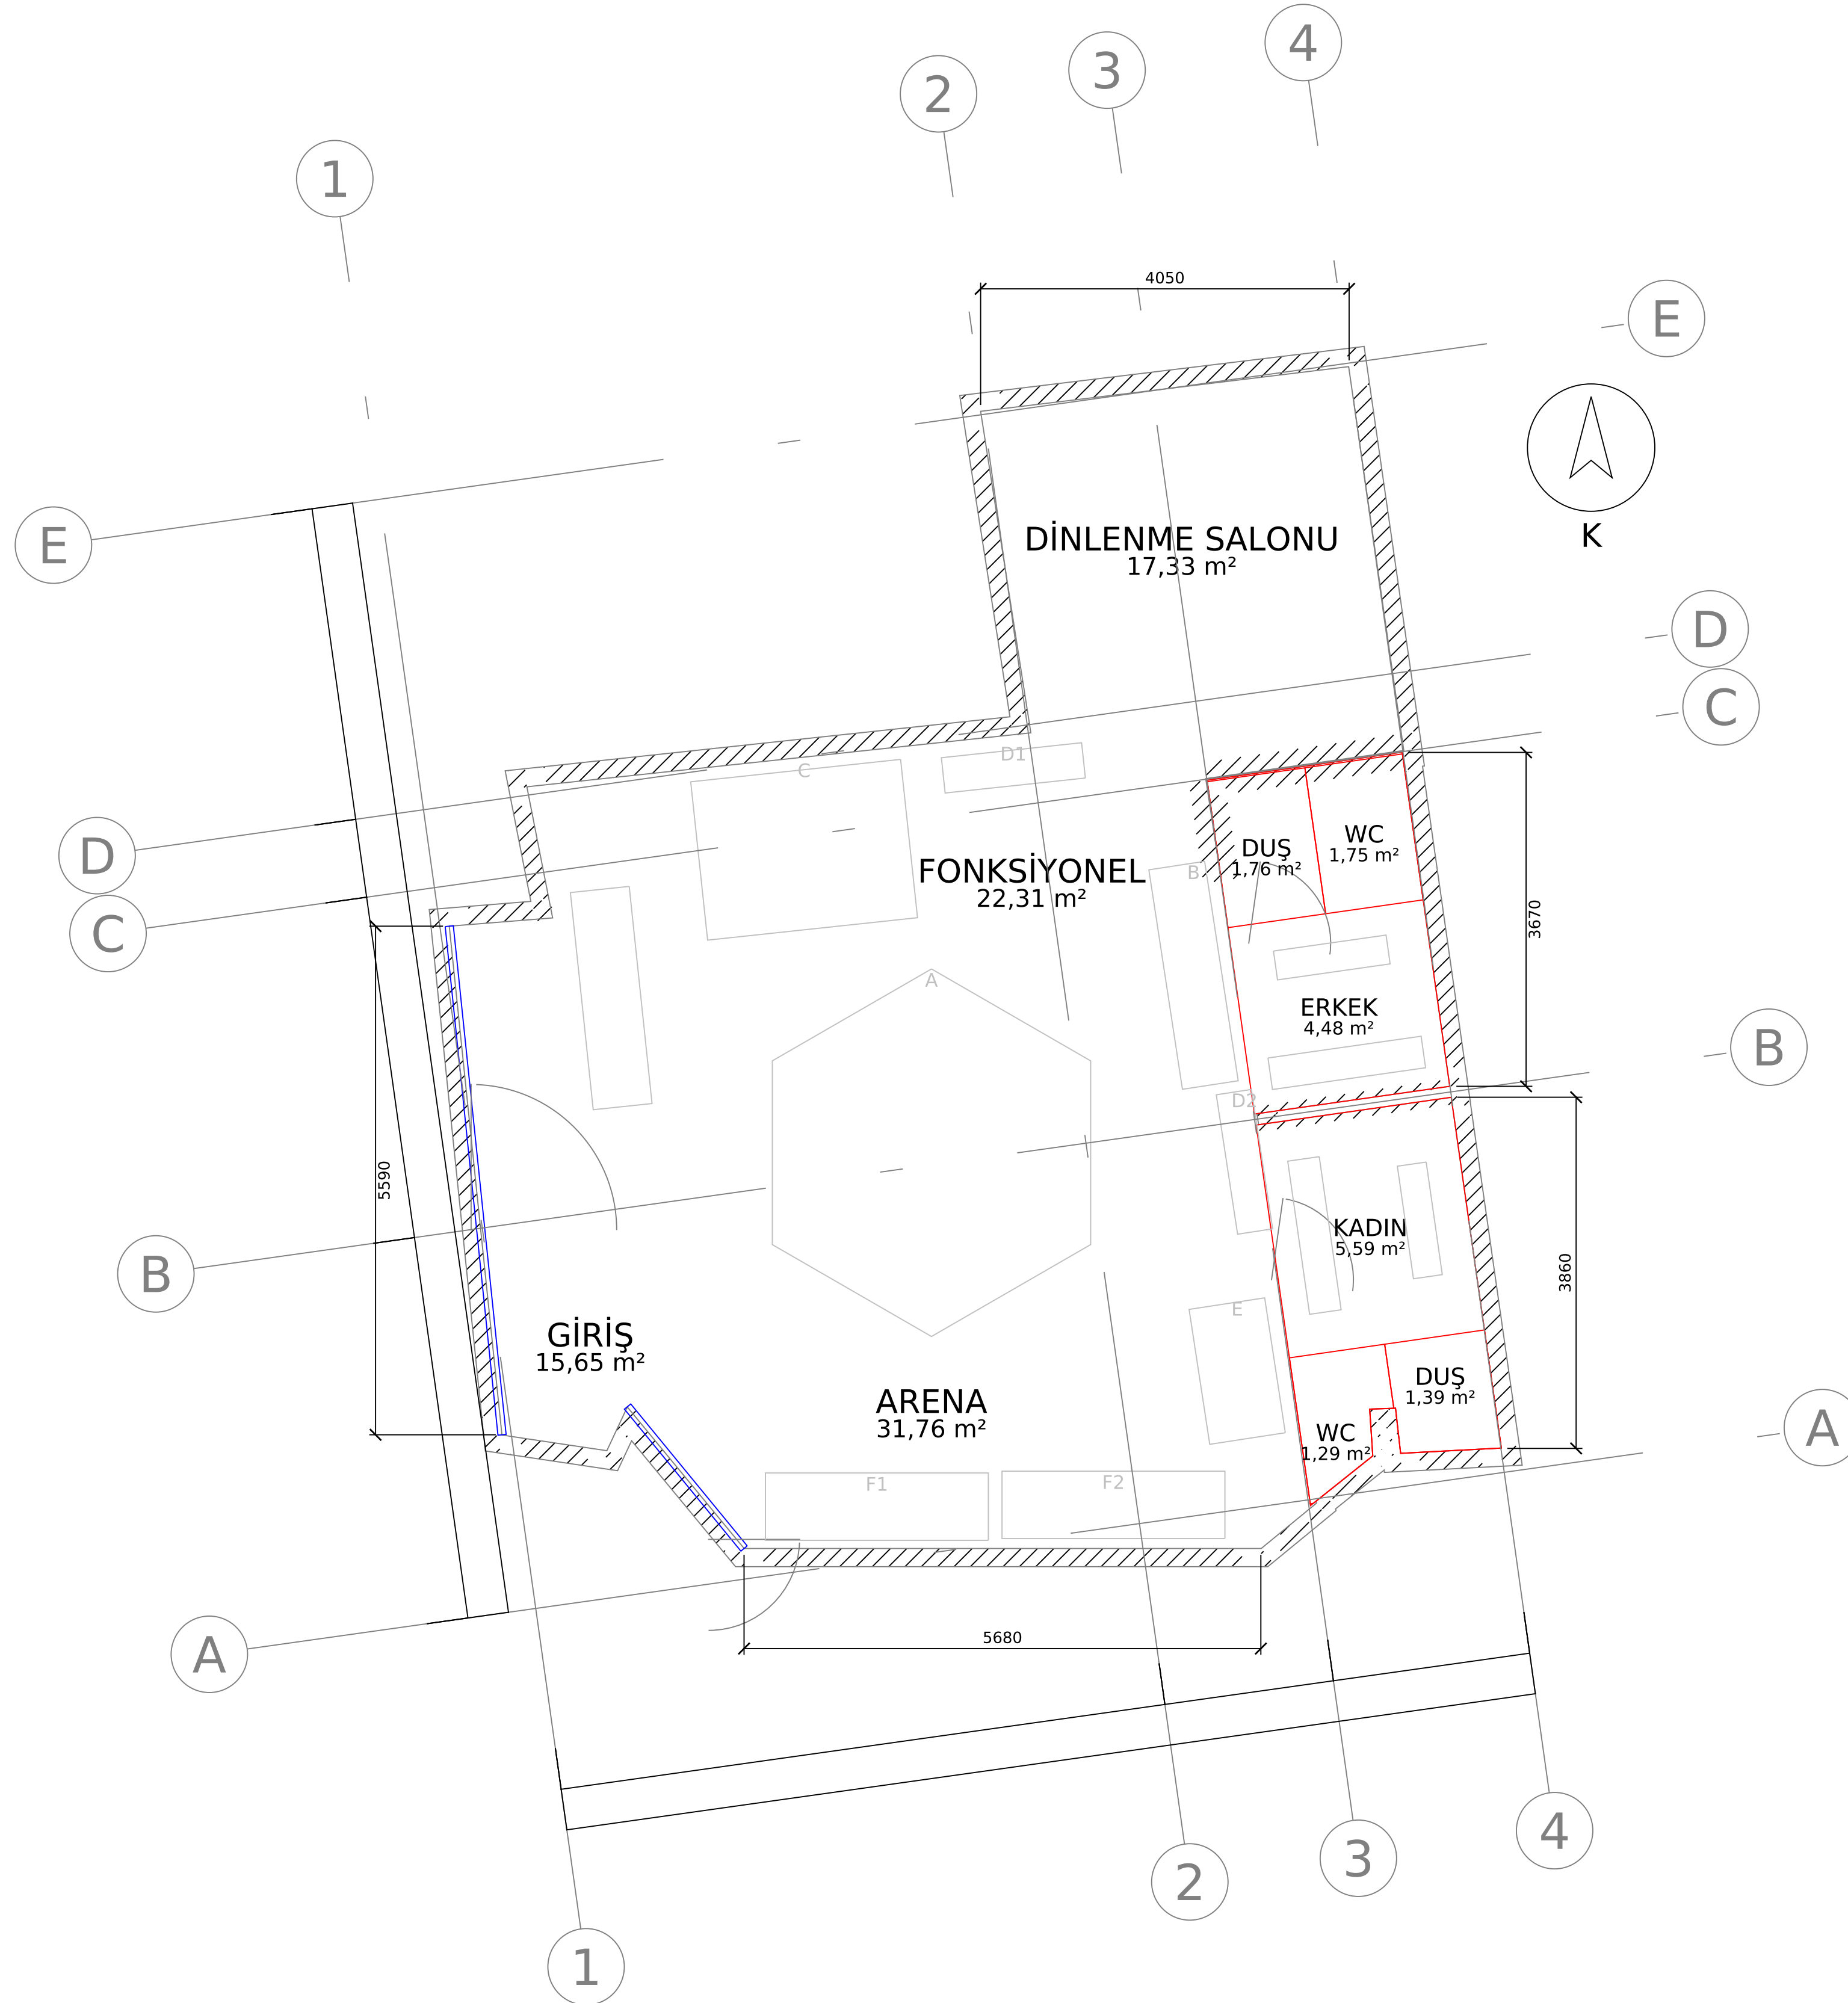

REV	TARİH	AÇIKLAMA	CZ	KT	ON
A	17.09.2026	İlk yayın — ön tasarım	CC	—	—
B	18.09.2026	Aks sistemi, zincir ölçü, ISO 5457/7200 pafta	CC	—	—
C	18.09.2026	A1 pafta, tekil DXF, ADP şeması CAD'de	CC	—	—
D	18.09.2026	ADP çok hatlı şema (faz ayrımı), B eğrisi, ana RCD	CC	—	—

İŞVEREN ÖZEL — MALTEPE / IDEALTEPE					
PROJE MOBİLYA MAĞAZASI → FONKSİYONEL ANTRENMAN STÜDYOSU					
YAPI / MAHAL İdealtepe Mah. · zemin kat dükkân · 103,78 m² iç alan			DİSİPLİN MİMARİ		
PAFTA ADI MİMARİ ALTLIK			Mevcut durum · ölçü ve aks sistemi		
PROJE MÜELLİFİ · ODA SİCİL NO — Oda sicil no: —					
ÇİZEN CC		KONTROL —		ONAY —	
TARİH 17 Eylül 2026		ÖLÇEK 1:50		BİRİM milimetre (mm)	
DURUM ÖN TASARIM		PAFTA NO A-01		REV H	
				SONRAKİ: A-02	

LEJANT

- Mimari — mevcut duvar (korunuyor)
- Mimari — yeni alçıpan bölme
- Mimari — cephe doğraması
- Mimari — kapı ve açılım
- Mimari — spor ekipmanı (işverence temini)
- Mimari — sabit mobilya
- Mimari — mahal adı ve alan
- Mimari — mahal numarası ve kapı kodu balonu
- Mimari — kesit ve görünüş hattı

GENEL NOTLAR

- Mahal no, kapı kodu, duvar tipi ve
- kesit hattı gösterilmiştir.
- Tüm alçıpan bölmeler yapısal döseme
- altına (+3.20) kadar yükselir.

ÖLÇEK 1:50
0 1 2 3 4 5 m

ÖN TASARIM — UYGULAMA İÇİN DEĞİLDİR

100 mm

REV	TARİH	AÇIKLAMA	CZ	KT	ON
A	17.09.2026	İlk yayın — ön tasarım	CC	—	—
B	18.09.2026	Aks sistemi, zincir ölçü, ISO 5457/7200 pafta	CC	—	—
C	18.09.2026	A1 pafta, tekil DXF, ADP şeması CAD'de	CC	—	—
D	18.09.2026	ADP çok hatlı şema (faz ayrımı), B eğrisi, ana RCD	CC	—	—

İŞVEREN	ÖZEL — MALTEPE / IDEALTEPE
PROJE	MOBİLYA MAĞAZASI → FONKSİYONEL ANTRENMAN STÜDYOSU
YAPI / MAHAL	İdealtepe Mah. · zemin kat dükkân · 103,78 m² iç alan
PAFTA ADI	MİMARİ UYGULAMA PLANI
PROJE MÜELLİFİ · ODA SİCİL NO	— Oda sicil no: —
ÇİZEN	CC
TARİH	17 Eylül 2026
DURUM	ÖN TASARIM
KONTROL	—
ÖLÇEK	1:50
PAFTA NO	A-02
ONAY	—
BİRİM	milimetre (mm)
REV	H
SONRAKİ:	A-03

LEJANT

- Mimari — mevcut duvar (korunuyor)
— Mimari — yeni alçıpan bölme
— Mimari — cephe doğraması
— Mimari — kapı ve açılım
— Mimari — mahal numarası ve kapı kodu balonu
— Mimari — zemin kaplama tipi sınırı
— Mimari — zemin kaplama tipi ve kotu
— Mimari — kauçuk karo derz ızgarası

GENEL NOTLAR

1. Bitmiş zemin kotu tüm kuru hacimde
2. +/-0,00; dus ve WC -0,02.
3. Tesviye sapı kalınlıkları farklıdır
4. (Z1:3 Z2:30 Z3:42 Z5:38 mm).
5. Kauçuk karo derz 1000x1000 mm.

ÖLÇEK 1:50
0 1 2 3 4 5 m


ÖN TASARIM — UYGULAMA İÇİN DEĞİLDİR

100 mm


REV	TARİH	AÇIKLAMA	CZ	KT	ON
A	17.09.2026	İlk yayın — ön tasarım	CC	—	—
B	18.09.2026	Aks sistemi, zincir ölçü, ISO 5457/7200 pafta	CC	—	—
C	18.09.2026	A1 pafta, tekil DXF, ADP şeması CAD'de	CC	—	—
D	18.09.2026	ADP çok hatlı şema (faz ayrımı), B eğrisi, ana RCD	CC	—	—

İŞVEREN ÖZEL — MALTEPE / IDEALTEPE PROJE MOBİLYA MAĞAZASI → FONKSİYONEL ANTRENMAN STÜDYOSU			YAPI / MAHAL İdealtepe Mah. · zemin kat dükkân · 103,78 m² iç alan		DISIPLIN MİMARİ
PAFTA ADI ZEMİN KAPLAMA PLANI			Kaplama tipleri · kot · derz yönü		
PROJE MÜELLİFİ · ODA SİCİL NO — Oda sicil no: —					
ÇİZEN CC		KONTROL —	ONAY —		A
TARİH 17 Eylül 2026		ÖLÇEK 1:50	BİRİM milimetre (mm)		
DURUM ÖN TASARIM		PAFTA NO A-03	REV H	SONRAKİ: A-04	

ÖLÇÜ ALINMAZ — YAZILI ÖLÇÜLER GEÇERLİDİR

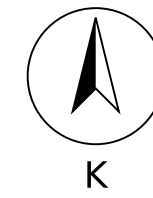

ANAHTAR PLAN

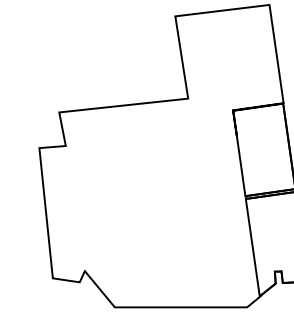

LEJANT

- Mimari — mevcut duvar (korunuyor)
- Mimari — yeni alçıpan bölme
- Mimari — cephe doğraması
- Mimari — kapı ve açılım
- Mimari — sabit mobilya
- Mimari — asma tavan tipi sınırı
- Mimari — asma tavan tipi ve kotu
- Mimari — revizyon kapağı 300x300
- Mekanik — taze hava kanalı
- Mekanik — egzoz kanalı
- Mekanik — ıslak hacim egzoz kanalı
- Mekanik — menfez ve valf
- Mekanik — menfez bransmanı
- Mekanik — fan ve panjur
- Mekanik — etiket ve not
- Elektrik — lineer LED armatür
- Elektrik — IP44 downlight
- Elektrik — acil aydınlatma / yönlendirme
- Elektrik — anahtar ve sensör
- Elektrik — aydınlatma lineyesi (ortogonal)
- Elektrik — anahtar kumanda sortisi
- Elektrik — ana dağıtım panosu
- Elektrik — etiket ve not


GENEL NOTLAR

- T1 açık tavan +3,20 · T2 +2,75
- T4 +2,60 · T3 +2,40.
- Tesisat askısı alçıpan karkasına
- asılmaz; ayrı askılanır.
- Her ıslak hacimde 300x300 revizyon.

ÖLÇEK 1:50
0 1 2 3 4 5 m

ÖN TASARIM — UYGULAMA İÇİN DEĞİLDİR

100 mm

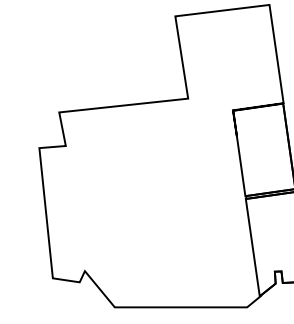


LEJANT

- Mimari — mevcut duvar (korunuyor)
- Mimari — yeni açılan bölme
- Mimari — cephe doğraması
- Mimari — kapı ve açılım
- Mimari — sabit mobilya
- Mimari — mahal adı ve alan
- Mimari — kaçış yolu ve çıkış
- Mimari — söndürücü, dolap, ihbar

GENEL NOTLAR

- İki bağımsız çıkış: Ç1 1,60 m, Ç2 1,00 m.
- En uzun kaçış yolu 13,4 m.
- Kaçış kapıları kaçış yönünde açılır.
- panik donanımlı, kilitli.

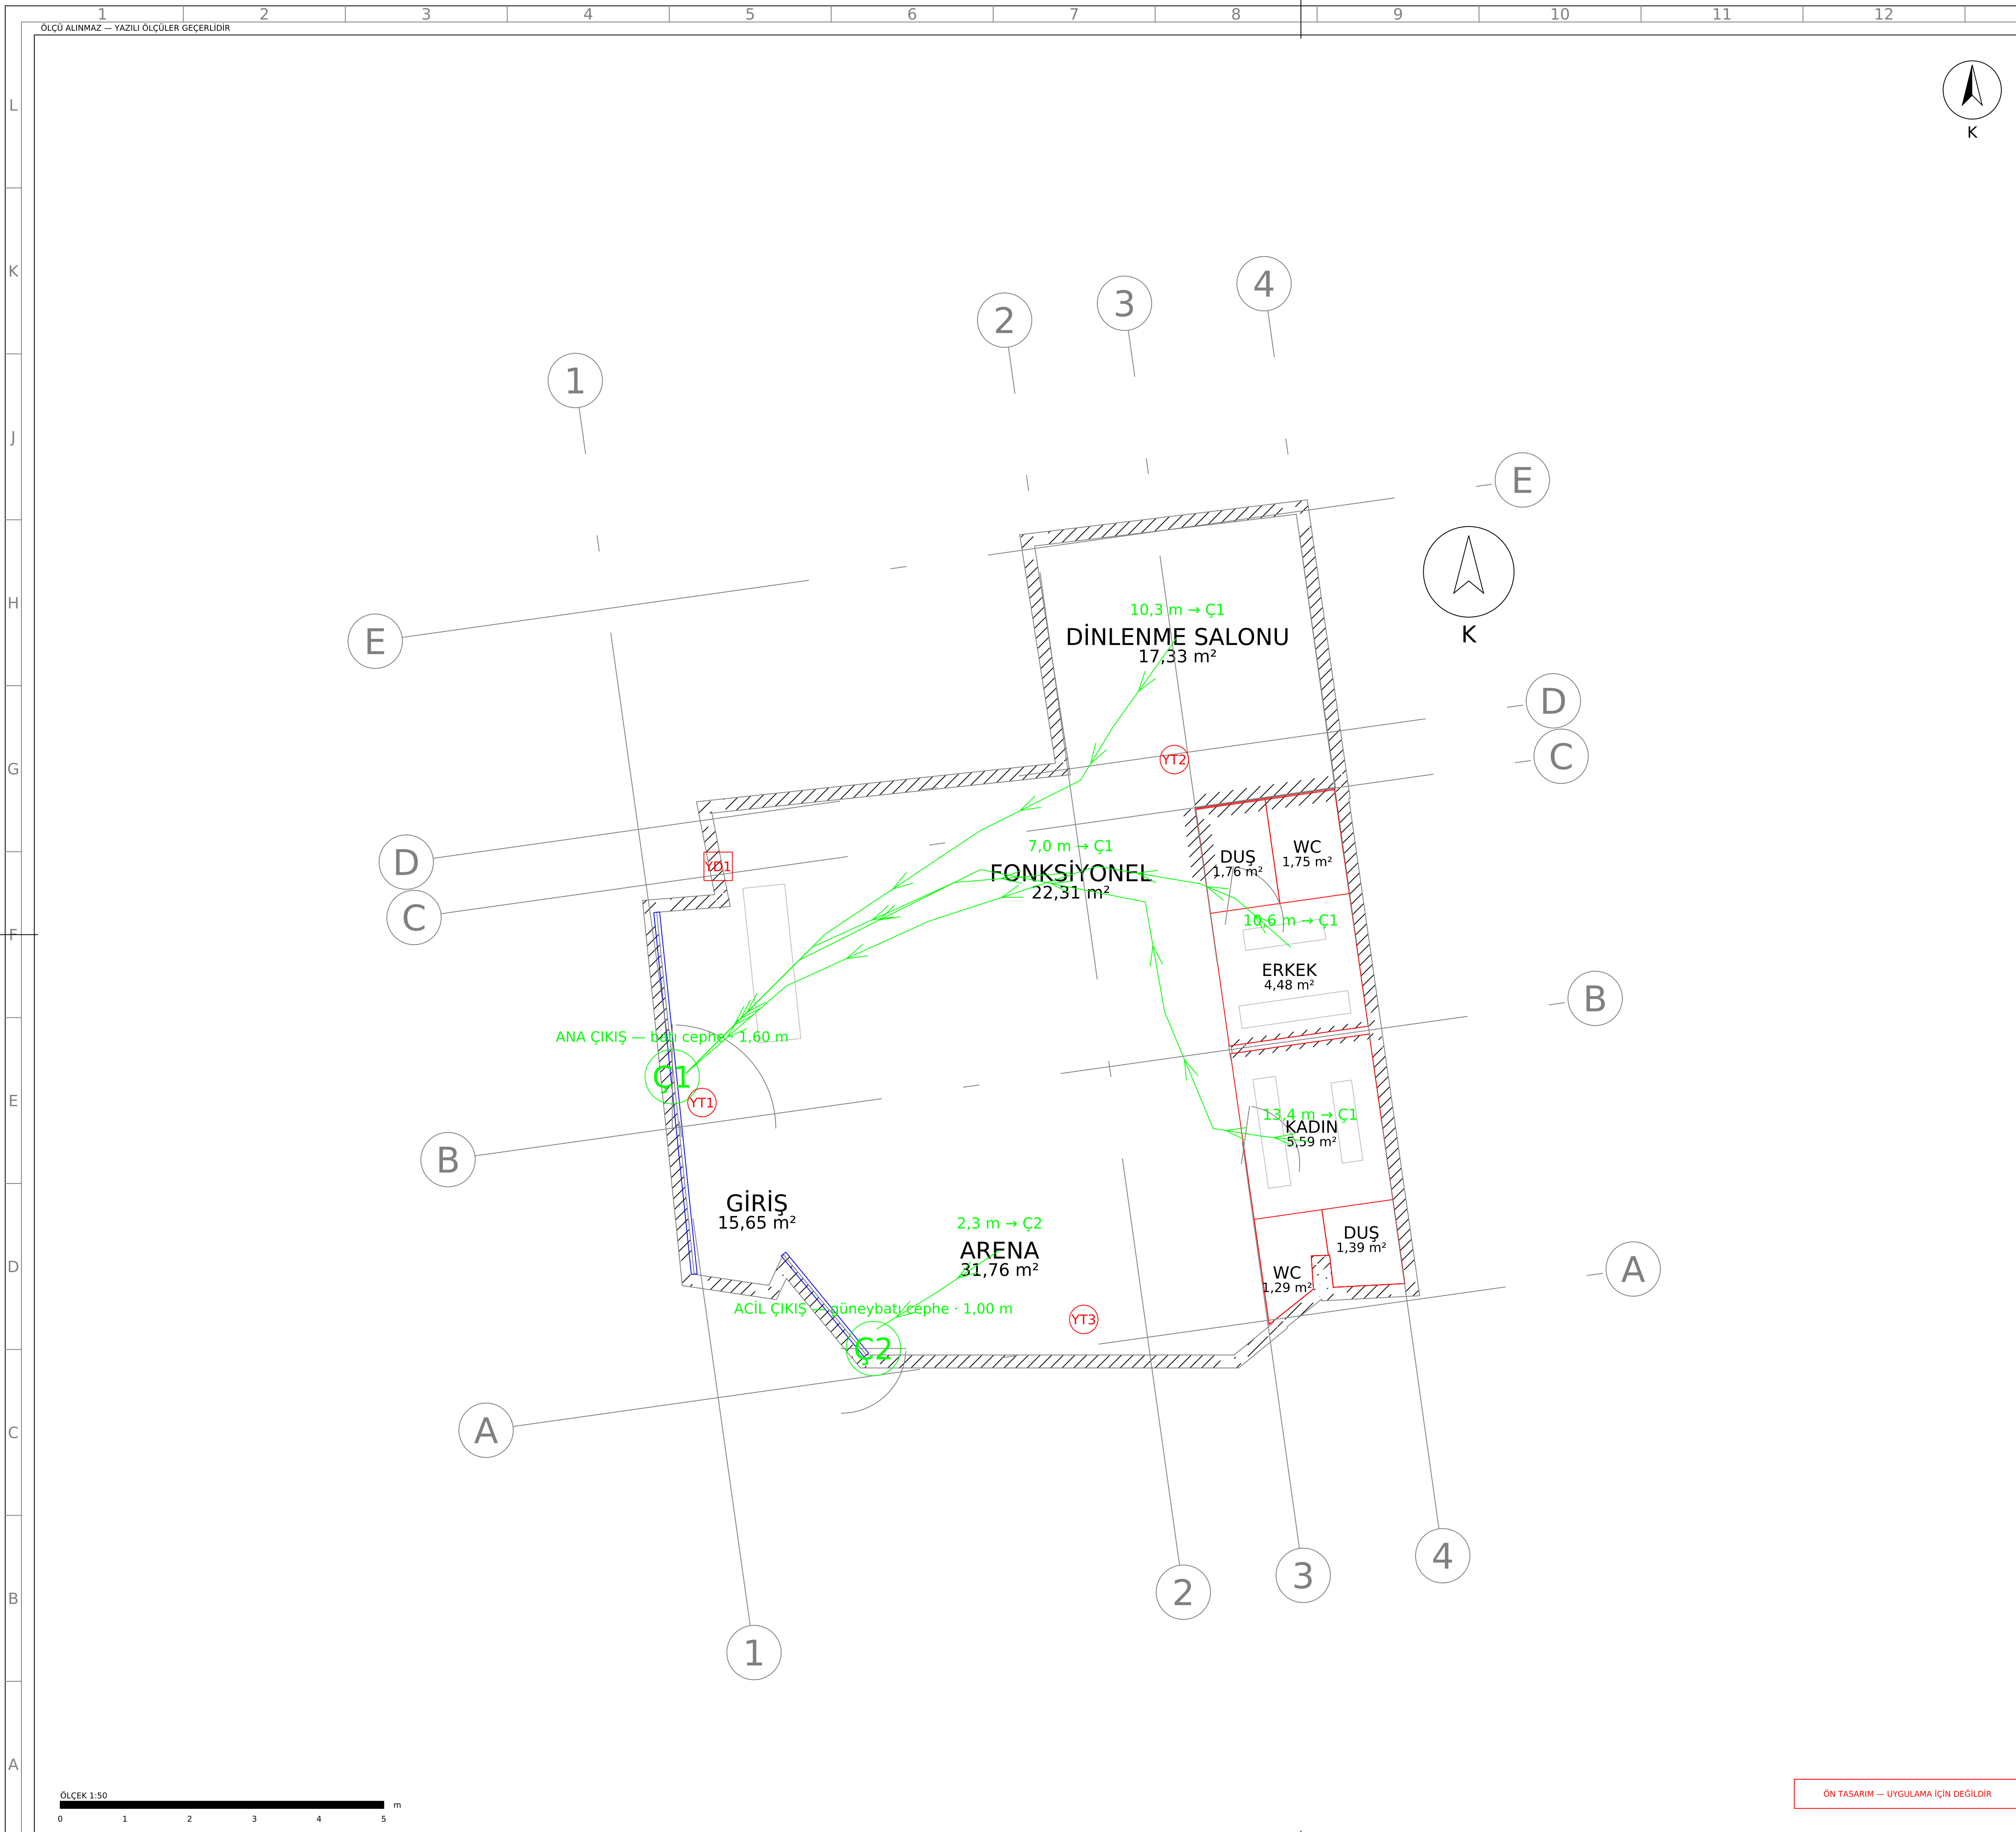

REV	TARİH	AÇIKLAMA	ÇZ	KT	ON
A	17.09.2026	İlk yayın — ön tasarım	CC	—	—
B	18.09.2026	Aks sistemi, zincir ölçü, ISO 5457/7200 pafta	CC	—	—
C	18.09.2026	A1 pafta, tekil DXF, ADP şeması CAD'de	CC	—	—
D	18.09.2026	ADP çok hatlı şema (faz ayrımı), B eğrisi, ana RCD	CC	—	—

İŞVEREN ÖZEL — MALTEPE / İDEALTEPE			E		
PROJE MOBİLYA MAĞAZASI → FONKSİYONEL ANTRENMAN STÜDYOSU					
YAPI / MAHAL İdealtepe Mah. · zemin kat dükkân · 103,78 m² iç alan		DİSİPLİN MİMARİ			
PAFTA ADI YANGIN VE TAHLİYE PLANI		Kaçış yolları · çıkışlar · söndürücü			
PROJE MÜELLİFİ · ODA SİCİL NO — Oda sicil no: —					
ÇİZEN CC	KONTROL —		ONAY —	A	
TARİH 17 Eylül 2026	ÖLÇEK 1:50		BİRİM milimetre (mm)		
DURUM ÖN TASARIM	PAFTA NO A-05		REV H	SONRAKİ: M-01	

ÖN TASARIM — UYGULAMA İÇİN DEĞİLDİR

LEJANT

- Mimari — mevcut duvar (korunuyor)
— Mimari — yeni alçıpan bölme
— Mimari — cephe doğraması
— Mimari — kapı ve açılım
— Mimari — spor ekipmanı (işverence temini)
— Mimari — sabit mobilya
— Mimari — mahal adı ve alan
— Mekanik — taze hava kanalı
— Mekanik — egzoz kanalı
— Mekanik — ıslak hacim egzoz kanalı
— Mekanik — menfez ve valf
— Mekanik — menfez bransmanı
— Mekanik — fan ve panjur
— Mekanik — etiket ve not

GENEL NOTLAR

1. Kanallar galvaniz sac, TS EN 1507 sınıf B.
2. Besleme ve egzoz hattı 19 mm izoleli.
3. Her bransman bası debi ayar damperli.
4. Devreye almada balanslama ve ölçüm raporu.

DİNLENME SALONU
17,33 m²

FONKSİYONEL
22,31 m²

DÜŞ
1,75 m²

ERKEK
4,48 m²

KADIN
5,59 m²

GİRİŞ
15,65 m²

ARENA
31,76 m²

DÜŞ
1,39 m²


WC
1,29 m²

ÖLÇEK 1:50
0 1 2 3 4 5 m

ÖN TASARIM — UYGULAMA İÇİN DEĞİLDİR

REV	TARİH	AÇIKLAMA	ÇZ	KT	ON
A	17.09.2026	İlk yayın — ön tasarım	CC	—	—
B	18.09.2026	Aks sistemi, zincir ölçü, ISO 5457/7200 pafta	CC	—	—
C	18.09.2026	A1 pafta, tekil DXF, ADP şeması CAD'de	CC	—	—
D	18.09.2026	ADP çok hatlı şema (faz ayrımı), B eğrisi, ana RCD	CC	—	—

İŞVEREN ÖZEL — MALTEPE / İDEALTEPE			B			
PROJE MOBİLYA MAĞAZASI → FONKSİYONEL ANTRENMAN STÜDYOSU						
YAPI / MAHAL İdealtepe Mah. · zemin kat dükkân · 103,78 m ² iç alan		DİSİPLİN MEKANİK TESİSAT				
PAFTA ADI HAVALANDIRMA PLANI		Kanal güzergâhı · menfez debileri				
PROJE MÜELLİFİ · ODA SİCİL NO — Oda sicil no: —						
ÇİZEN CC		KONTROL —		ONAY —		
TARİH 17 Eylül 2026		ÖLÇEK 1:50		BİRİM milimetre (mm)		
DURUM ÖN TASARIM		PAFTA NO M-01		REV H		
				SONRAKİ: M-02		

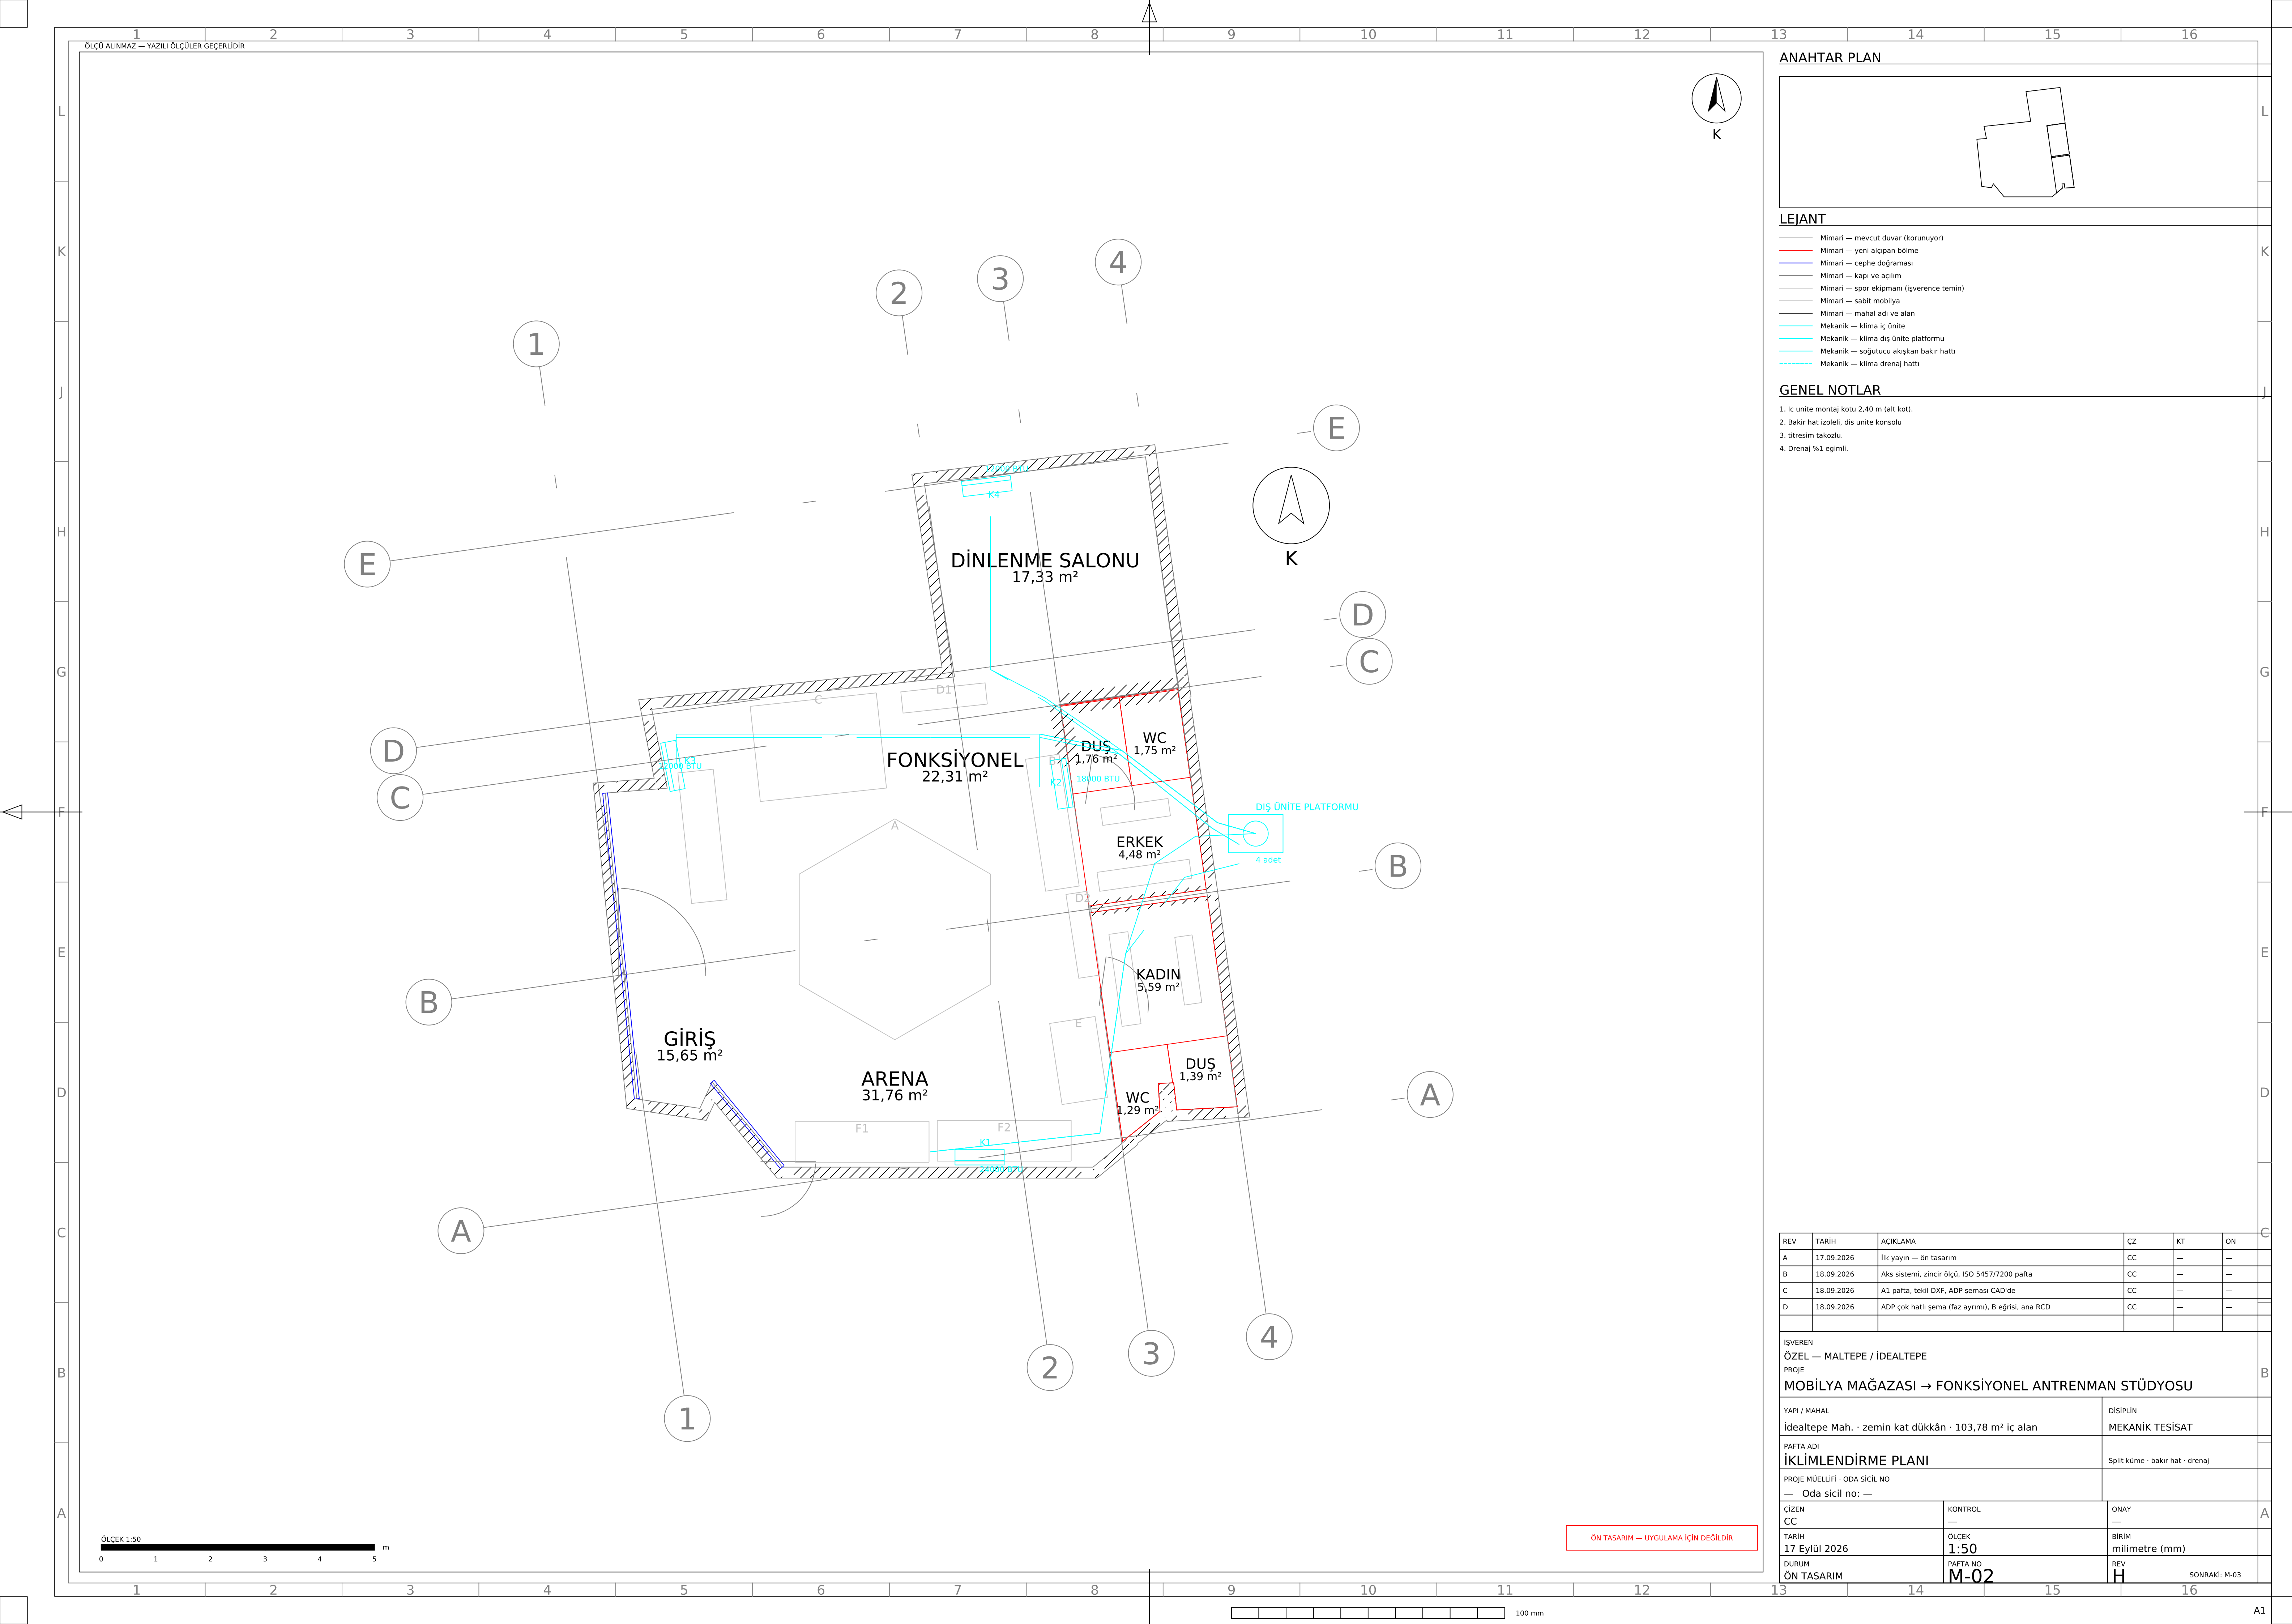

LEJANT

- Mimari — mevcut duvar (korunuyor)
- Mimari — yeni alçıpan bölme
- Mimari — cephe doğraması
- Mimari — kapı ve açılım
- Mimari — spor ekipmanı (işverence temin)
- Mimari — sabit mobilya
- Mimari — mahal adı ve alan
- Mekanik — temiz su PPRC
- Mekanik — sıcak su PPRC İzoleli
- Mekanik — pis su PVC
- Mekanik — vitrifiye ve su ısıtıcı

GENEL NOTLAR

- Pis su %2 eğimli.
- Tüm ıslak hacimde sifonlu yer suzgeci.
- SOKUM SONRASI İLK İS: mevcut pis su
- bağlantı kotunun ölçülmesi.

REV	TARİH	AÇIKLAMA	CZ	KT	ON
A	17.09.2026	İlk yayın — ön tasarım	CC	—	—
B	18.09.2026	Aks sistemi, zincir ölçü, ISO 5457/7200 pafta	CC	—	—
C	18.09.2026	A1 pafta, tekil DXF, ADP şeması CAD'de	CC	—	—
D	18.09.2026	ADP çok hatlı şema (faz ayrımı), B eğrisi, ana RCD	CC	—	—

İŞVEREN ÖZEL — MALTEPE / İDEALTEPE			B			
PROJE MOBİLYA MAĞAZASI → FONKSİYONEL ANTRENMAN STÜDYOSU						
YAPI / MAHAL İdealtepe Mah. · zemin kat dükkân · 103,78 m² iç alan		DİSİPLİN MEKANİK TESİSAT				
PAFTA ADI SİHHİ TESİSAT PLANI		Temiz su · sıcak su · pis su				
PROJE MÜELLİFİ · ODA SİCİL NO — Oda sicil no: —						
ÇİZEN CC		KONTROL —		ONAY —		
TARİH 17 Eylül 2026		ÖLÇEK 1:50		BİRİM milimetre (mm)		
DURUM ÖN TASARIM		PAFTA NO M-03		REV H		
				SONRAKİ: M-04		

ÖLÇEK 1:50
0 1 2 3 4 5 m

ÖN TASARIM — UYGULAMA İÇİN DEĞİLDİR

100 mm

LEJANT

- Mimari — mevcut duvar (korunuyor)
- Mimari — yeni alçıpan bölme
- Mimari — cephe doğraması
- Mimari — kapı ve açılım
- Mimari — spor ekipmanı (işverence temini)
- Mimari — sabit mobilya
- Mimari — mahal adı ve alan
- Mekanik — taze hava kanalı
- Mekanik — egzoz kanalı
- Mekanik — ıslak hacim egzoz kanalı
- Mekanik — menfez ve valf
- Mekanik — menfez bransmanı
- Mekanik — fan ve panjur
- Mekanik — klima iç ünite
- Mekanik — klima dış ünite platformu
- Mekanik — soğutucu akışkan bakır hattı
- Mekanik — klima drenaj hattı
- Mekanik — temiz su PPRC
- Mekanik — sıcak su PPRC izoleli
- Mekanik — pis su PVC
- Mekanik — vitrifiye ve su ısıtıcı
- Mekanik — etiket ve not

GENEL NOTLAR

- Mekanik disiplin genel yerleşimi.
- Ayrıntı için M-01, M-02, M-03 paftaları.

ÖLÇEK 1:50
0 1 2 3 4 5 m

ÖN TASARIM — UYGULAMA İÇİN DEĞİLDİR

LEJANT

- Mimari — mevcut duvar (korunuyor)
- Mimari — yeni açılan bölme
- Mimari — cephe doğraması
- Mimari — kapı ve açılım
- Mimari — spor ekipmanı (işverence temini)
- Mimari — sabit mobilya
- Mimari — mahal adı ve alan
- Elektrik — lineer LED armatür
- Elektrik — IP44 downlight
- Elektrik — acil aydınlatma / yönlendirme
- Elektrik — anahtar ve sensör
- Elektrik — aydınlatma linyesi (ortogonal)
- Elektrik — anahtar kumanda sortisi
- Elektrik — ana dağıtım panosu
- Elektrik — etiket ve not

GENEL NOTLAR

- Tesisat siva altı spiral boru içinde,
- NHXMH halojenizs kablo.
- Acil aydınlatma 3 saat bataryalı.

REV	TARİH	AÇIKLAMA	CZ	KT	ON
A	17.09.2026	İlk yayın — ön tasarım	CC	—	—
B	18.09.2026	Aks sistemi, zincir ölçü, ISO 5457/7200 pafta	CC	—	—
C	18.09.2026	A1 pafta, tekil DXF, ADP şeması CAD'de	CC	—	—
D	18.09.2026	ADP çok hatlı şema (faz ayrımı), B eğrisi, ana RCD	CC	—	—

İŞVEREN ÖZEL — MALTEPE / IDEALTEPE					
PROJE MOBİLYA MAĞAZASI → FONKSİYONEL ANTRENMAN STÜDYOSU					
YAPI / MAHAL İdealtepe Mah. · zemin kat dükkân · 103,78 m ² iç alan		DİSİPLİN ELEKTRİK			
PAFTA ADI AYDINLATMA PLANI		Armatür · anahtar · aydınlatma linyeleri			
PROJE MÜELLİFİ · ODA SİCİL NO — Oda sicil no: —					
ÇİZEN CC		KONTROL —		ONAY —	
TARİH 17 Eylül 2026		ÖLÇEK 1:50		BİRİM milimetre (mm)	
DURUM ÖN TASARIM		PAFTA NO E-01		REV H SONRAKİ: E-02	

ÖLÇEK 1:50
0 1 2 3 4 5 m

ÖN TASARIM — UYGULAMA İÇİN DEĞİLDİR

LEJANT

- Mimari — mevcut duvar (korunuyor)
- Mimari — yeni alçıpan bölme
- Mimari — cephe doğraması
- Mimari — kapı ve açılım
- Mimari — spor ekipmanı (işverence temin)
- Mimari — sabit mobilya
- Mimari — mahal adı ve alan
- Elektrik — priz
- Elektrik — klima/sıtıcıfan beslemesi
- Elektrik — priz ve kuvvet linyesi
- Elektrik — ana dağıtım panosu
- Elektrik — etiket ve not

GENEL NOTLAR

- Islak hacim linyeleri ayrı 30 mA
- kacak akım rolesinden beslenir.
- Kardiyo ekipmanı ayrı linyede (P4).

ÖLÇEK 1:50
0 1 2 3 4 5 m

ÖN TASARIM — UYGULAMA İÇİN DEĞİLDİR

REV	TARİH	AÇIKLAMA	CZ	KT	ON
A	17.09.2026	İlk yayın — ön tasarım	CC	—	—
B	18.09.2026	Aks sistemi, zincir ölçü, ISO 5457/7200 pafta	CC	—	—
C	18.09.2026	A1 pafta, tekil DXF, ADP şeması CAD'de	CC	—	—
D	18.09.2026	ADP çok hatlı şema (faz ayrımı), B eğrisi, ana RCD	CC	—	—

İŞVEREN ÖZEL — MALTEPE / İDEALTEPE			B		
PROJE MOBİLYA MAĞAZASI → FONKSİYONEL ANTRENMAN STÜDYOSU					
YAPI / MAHAL İdealtepe Mah. · zemin kat dükkân · 103,78 m ² iç alan			DISIPLİN ELEKTRİK		
PAFTA ADI PRİZ VE KUVVET PLANI			Priz · kuvvet linyeleri · cihaz beslemeleri		
PROJE MÜELLİFİ · ODA SİCİL NO — Oda sicil no: —					
ÇİZEN CC		KONTROL —		ONAY —	
TARİH 17 Eylül 2026		ÖLÇEK 1:50		BİRİM milimetre (mm)	
DURUM ÖN TASARIM		PAFTA NO E-02		REV H	
			SONRAKİ: E-03		

LEJANT

- Mimari — mevcut duvar (korunuyor)
- Mimari — yeni alçıpan bölme
- Mimari — cephe doğraması
- Mimari — kapı ve açılım
- Mimari — spor ekipmanı (işverence temin)
- Mimari — sabit mobilya
- Mimari — mahal adı ve alan
- Elektrik — IP kamera
- Elektrik — tavan hoparlörü
- Elektrik — veri prizi ve rack
- Elektrik — dedektör, buton, siren
- Elektrik — yangın algılama çevrimi
- Elektrik — zayıf akım kablo kanalı
- Elektrik — ana dağıtım panosu
- Elektrik — etiket ve not

GENEL NOTLAR

- SOYUNMA VE WC İÇİNE KAMERA KONULMAZ.
- Yangın algılama panosu kesintisiz beslenir.
- Topraklama direnci ≤ 10 ohm.

ÖLÇEK 1:50
0 1 2 3 4 5 m

ÖN TASARIM — UYGULAMA İÇİN DEĞİLDİR

100 mm

REV	TARİH	AÇIKLAMA	CZ	KT	ON
A	17.09.2026	İlk yayın — ön tasarım	CC	—	—
B	18.09.2026	Aks sistemi, zincir ölçü, ISO 5457/7200 pafta	CC	—	—
C	18.09.2026	A1 pafta, tekil DXF, ADP şeması CAD'de	CC	—	—
D	18.09.2026	ADP çok hatlı şema (faz ayrımı), B eğrisi, ana RCD	CC	—	—

İŞVEREN ÖZEL — MALTEPE / IDEALTEPE					
PROJE MOBİLYA MAĞAZASI → FONKSİYONEL ANTRENMAN STÜDYOSU					
YAPI / MAHAL İdealtepe Mah. · zemin kat dükkân · 103,78 m² iç alan		DİSİPLİN ELEKTRİK			
PAFTA ADI ZAYIF AKIM PLANI		Veri · CCTV · ses · yangın algılama			
PROJE MÜELLİFİ · ODA SİCİL NO — Oda sicil no: —					
ÇİZEN CC		KONTROL —		ONAY —	
TARİH 17 Eylül 2026		ÖLÇEK 1:50		BİRİM milimetre (mm)	
DURUM ÖN TASARIM		PAFTA NO E-03		REV H	
				SONRAKİ: E-04	

LEJANT

- Mimari — mevcut duvar (korunuyor)
- Mimari — yeni alçıpan bölme
- Mimari — cephe doğraması
- Mimari — kapı ve açılım
- Mimari — spor ekipmanı (işverence temin)
- Mimari — sabit mobilya
- Mimari — mahal adı ve alan
- Elektrik — lineer LED armatür
- Elektrik — IP44 downlight
- Elektrik — acil aydınlatma / yönlendirme
- Elektrik — anahtar ve sensör
- Elektrik — priz
- Elektrik — klima/sıtıcı/fan beslemesi
- Elektrik — IP kamera
- Elektrik — tavan hoparlörü
- Elektrik — veri prizi ve rack
- Elektrik — dedektör, buton, siren
- Elektrik — yangın algılama çevrimi
- Elektrik — aydınlatma lineyesi (ortogonal)
- Elektrik — anahtar kumanda sortisi
- Elektrik — priz ve kuvvet lineyesi
- Elektrik — zayıf akım kablo kanalı
- Elektrik — ana dağıtım panosu
- Elektrik — etiket ve not

GENEL NOTLAR

- Elektrik disiplin genel yerleşimi.
- Ayrıntı için E-01, E-02, E-03 paftaları.

REV	TARİH	AÇIKLAMA	CZ	KT	ON
A	17.09.2026	İlk yayın — ön tasarım	CC	—	—
B	18.09.2026	Aks sistemi, zincir ölçü, ISO 5457/7200 pafta	CC	—	—
C	18.09.2026	A1 pafta, tekil DXF, ADP şeması CAD'de	CC	—	—
D	18.09.2026	ADP çok hatlı şema (faz ayrımı), B eğrisi, ana RCD	CC	—	—

İŞVEREN	ÖZEL — MALTEPE / IDEALTEPE
PROJE	MOBİLYA MAĞAZASI → FONKSİYONEL ANTRENMAN STÜDYOSU
YAPI / MAHAL	İdealtepe Mah. · zemin kat dükkân · 103,78 m ² iç alan
PAFTA ADI	ELEKTRİK GENEL YERLEŞİM
PROJE MÜELLİFİ · ODA SİCİL NO	— Oda sicil no: —
ÇİZEN	CC
TARİH	17 Eylül 2026
DURUM	ÖN TASARIM
KONTROL	—
ÖLÇEK	1:50
PAFTA NO	E-04
ONAY	—
BİRİM	milimetre (mm)
REV	H
SONRAKİ:	E-05

ÖN TASARIM — UYGULAMA İÇİN DEĞİLDİR

LEJANT

- Mimari — mevcut duvar (korunuyor)
- Mimari — yeni alçıpan bölme
- Mimari — cephe doğraması
- Mimari — kapı ve açılım
- Mimari — spor ekipmanı (işverence temin)
- Mimari — sabit mobilya
- Mimari — mahal adı ve alan
- Elektrik — çubuk elektrot
- Elektrik — elektrot bağlantı şeridi
- Elektrik — topraklama iletkeni
- Elektrik — ATB / EPDB barası
- Elektrik — topraklama etiketi
- Elektrik — ana dağıtım panosu

GENEL NOTLAR

- Topraklama ve potansiyel dengeleme.
- Elektrot grubu yapı dışında, 4 adet 2 m Cu kaplı
- çelik çubuk, 3 m aralık. Ra hesap 15,5 ohm <= 20 ohm.
- ATB pano altında; her ıslak blokta EPDB bulunur.

ÖLÇEK 1:50
0 1 2 3 4 5 m



ÖN TASARIM — UYGULAMA İÇİN DEĞİLDİR


REV	TARİH	AÇIKLAMA	CZ	KT	ON
A	17.09.2026	İlk yayın — ön tasarım	CC	—	—
B	18.09.2026	Aks sistemi, zincir ölçü, ISO 5457/7200 pafta	CC	—	—
C	18.09.2026	A1 pafta, tekil DXF, ADP şeması CAD'de	CC	—	—
D	18.09.2026	ADP çok hatlı şema (faz ayrımı), B eğrisi, ana RCD	CC	—	—

İŞVEREN ÖZEL — MALTEPE / IDEALTEPE					
PROJE MOBİLYA MAĞAZASI → FONKSİYONEL ANTRENMAN STÜDYOSU					
YAPI / MAHAL İdealtepe Mah. · zemin kat dükkân · 103,78 m² iç alan			DİSİPLİN ELEKTRİK		
PAFTA ADI TOPRAKLAMA VE POTANSİYEL DENGELEME PLANI			Elektrot grubu · ATB · EPDB		
PROJE MÜELLİFİ · ODA SİCİL NO — Oda sicil no: —					
ÇİZEN CC		KONTROL —	ONAY —		A
TARİH 17 Eylül 2026		ÖLÇEK 1:50	BİRİM milimetre (mm)		
DURUM ÖN TASARIM		PAFTA NO E-05	REV H		SONRAKİ: ADP-01


	0	1	2	3	4	5	6	7			
A	ADP — ANA DAĞITIM PANOSU ÇOK HATLI ŞEMATİK DİYAGRAM SETİ / MULTI-LINE SCHEMATIC SET								A		
B	Müşteri / Customer	ÖZEL — MALTEPE / İDEALTEPE							B		
	Proje / Project	MOBİLYA MAĞAZASI → FONKSİYONEL ANTRENMAN STÜDYOSU									
	Pano / Panel	ADP									
	Proje No / Project No	GYM-25-001-001									
	Tarih / Date	17 Eylül 2026									
	Revizyon / Revision	Rev H									
	Standartlar / Standards	IEC 61439-1&2 · IEC 60617 · IEC 81346-2 · TS HD 60364 · Elektrik İç Tesisleri Yönetmeliği									
C	SAYFA İÇERİĞİ / SHEET INDEX								C		
	01	Cover Sheet / Kapak									
	02	Panel Characteristics / Pano Karakteristiği									
	03	Symbol List / Sembol Listesi									
	04	Incoming Supply / Ana Besleme									
	05	Schematic Diagram / Şematik Diyagram									
	06	Schematic Diagram / Şematik Diyagram									
	07	Schematic Diagram / Şematik Diyagram									
	08	Schematic Diagram / Şematik Diyagram									
	09	Terminal Diagram / Klemens Planı									
	10	Panel Overview / Pano Önden Görünüş									
	11	Load Schedule / Yükleme Cetveli									
	12	Parts List / Malzeme Listesi									
D									D		
E									E		
F									F		
Drawn By / Çizen		CC	Customer Name / Müşteri Adı		ÖZEL — MALTEPE / İDEALTEPE			Project Number / Proje Numarası	GYM-25-001-001	Sheet: / Sayfa	1
Checked By / Kontrol Eden		—	Project Description / Proje Açıklaması		MOBİLYA MAĞAZASI → FONKSİYONEL ANTRENMAN STÜDYOSU					Next sheet: / Sonraki	2
Approved By / Onaylayan		—	Panel Name / Pano Adı		ADP			Revision / Revizyon	Rev H	Total sheets: / Toplam	12
Project Date / Proje Tarihi		17 Eylül 2026	Page Description / Sayfa Açıklaması		Cover Sheet / Kapak			Standards / Standartlar	IEC 61439-1&2 · IEC 60617	Sheet size / Kâğıt	A3

	0	1	2	3	4	5	6	7										
A	PANO KARAKTERİSTİK TABLOSU / PANEL CHARACTERISTICS STANDARTLAR / STANDARDS Tip testli pano / Type tested assembly IEC 61439-1 & IEC 61439-2 Semboller / Symbols IEC 60617 Referans işaretleri / Designations IEC 81346-2 Tesisat / Installation TS HD 60364 · Elektrik İç Tes. Yön. BESLEME / POWER SUPPLY Anma işletme gerilimi / Rated voltage 400/230 V 50 Hz Faz sayısı / Number of phases 3F + N + PE Nötr işletmesi / Neutral operation TN-S Anma akımı / Rated current 32 A Kısa devre dayanımı / Icw 6 kA 1 s Ana besleme kablosu / Main cable NYY 5×10 mm² · 25 m KORUMA / PROTECTION Ana şalter / Main switch 4×32 A Ana kaçak akım / Main RCD 4×40 A / 300 mA S tipi Son devre kaçak akım / Final RCD 30 mA A tipi Aşırı gerilim / SPD Tip 2 · Up 1,4 kV · In 20 kA Kesici eğrisi / MCB curve Aydınlatma B · Priz ve motor C · tümü 6 kA GÖVDE / ENCLOSURE Koruma sınıfı / Degree of protection IP 54 Ayrıştırma / Segregation Form 2b Gövde / Enclosure Sac · RAL 7035 Bara / Busbar Bakır · nötr tam kesit Montaj / Mounting Sabit · kapı arkası kumanda Etiketleme / Labelling PVC · Türkçe · vidalı ÖZET / SUMMARY Linye sayısı / Number of circuits 22 + 4 yedek Bağlı güç / Connected load 20,59 kW Talep gücü / Demand 14,63 kW Faz dengesizliği / Imbalance %1,0 Toplam ΔU / Total voltage drop %2,49 <td></td><td></td><td></td><td></td><td></td><td></td><td></td><td></td><td></td><td></td>																	

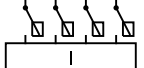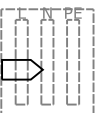
	0	1	2	3	4	5	6	7		
A	SEMBOL LİSTESİ / SYMBOL LIST — IEC 60617									
		-F	Otomatik sigorta, 1 kutup / MCB 1P							
		-F	Otomatik sigorta, 1F+N / MCB 1P+N							
B		-ID	Kaçak akım rölesi 2 kutup / RCD 2P							
		-ID	Kaçak akım rölesi 4 kutup / RCD 4P							
		-F0	Aşırı gerilim koruma Tip 2 / SPD Type 2							
C		-X	Klemens / Terminal							
		PE	Koruma topraklaması / Protective earth							
			Bağlantı noktası / Junction							
D		P	Saha cihazı ve kablo / Field device and cable							
			L1 L2 L3 N Potansiyel rayı / Potential rail							
			Sayfalar arası referans / Cross-page reference							
E										
F										
Drawn By / Çizen		CC	Customer Name / Müşteri Adı	ÖZEL — MALTEPE / İDEALTEPE			Project Number / Proje Numarası	GYM-25-001-001	Sheet: / Sayfa	3
Checked By / Kontrol Eden		—	Project Description / Proje Açıklaması	MOBİLYA MAĞAZASI → FONKSİYONEL ANTRENMAN STÜDYOSU					Next sheet: / Sonraki	4
Approved By / Onaylayan		—	Panel Name / Pano Adı	ADP			Revision / Revizyon	Rev H	Total sheets: / Toplam	12
Project Date / Proje Tarihi		17 Eylül 2026	Page Description / Sayfa Açıklaması	Symbol List / Sembol Listesi			Standards / Standartlar	IEC 61439-1&2 · IEC 60617	Sheet size / Kâğıt	A3

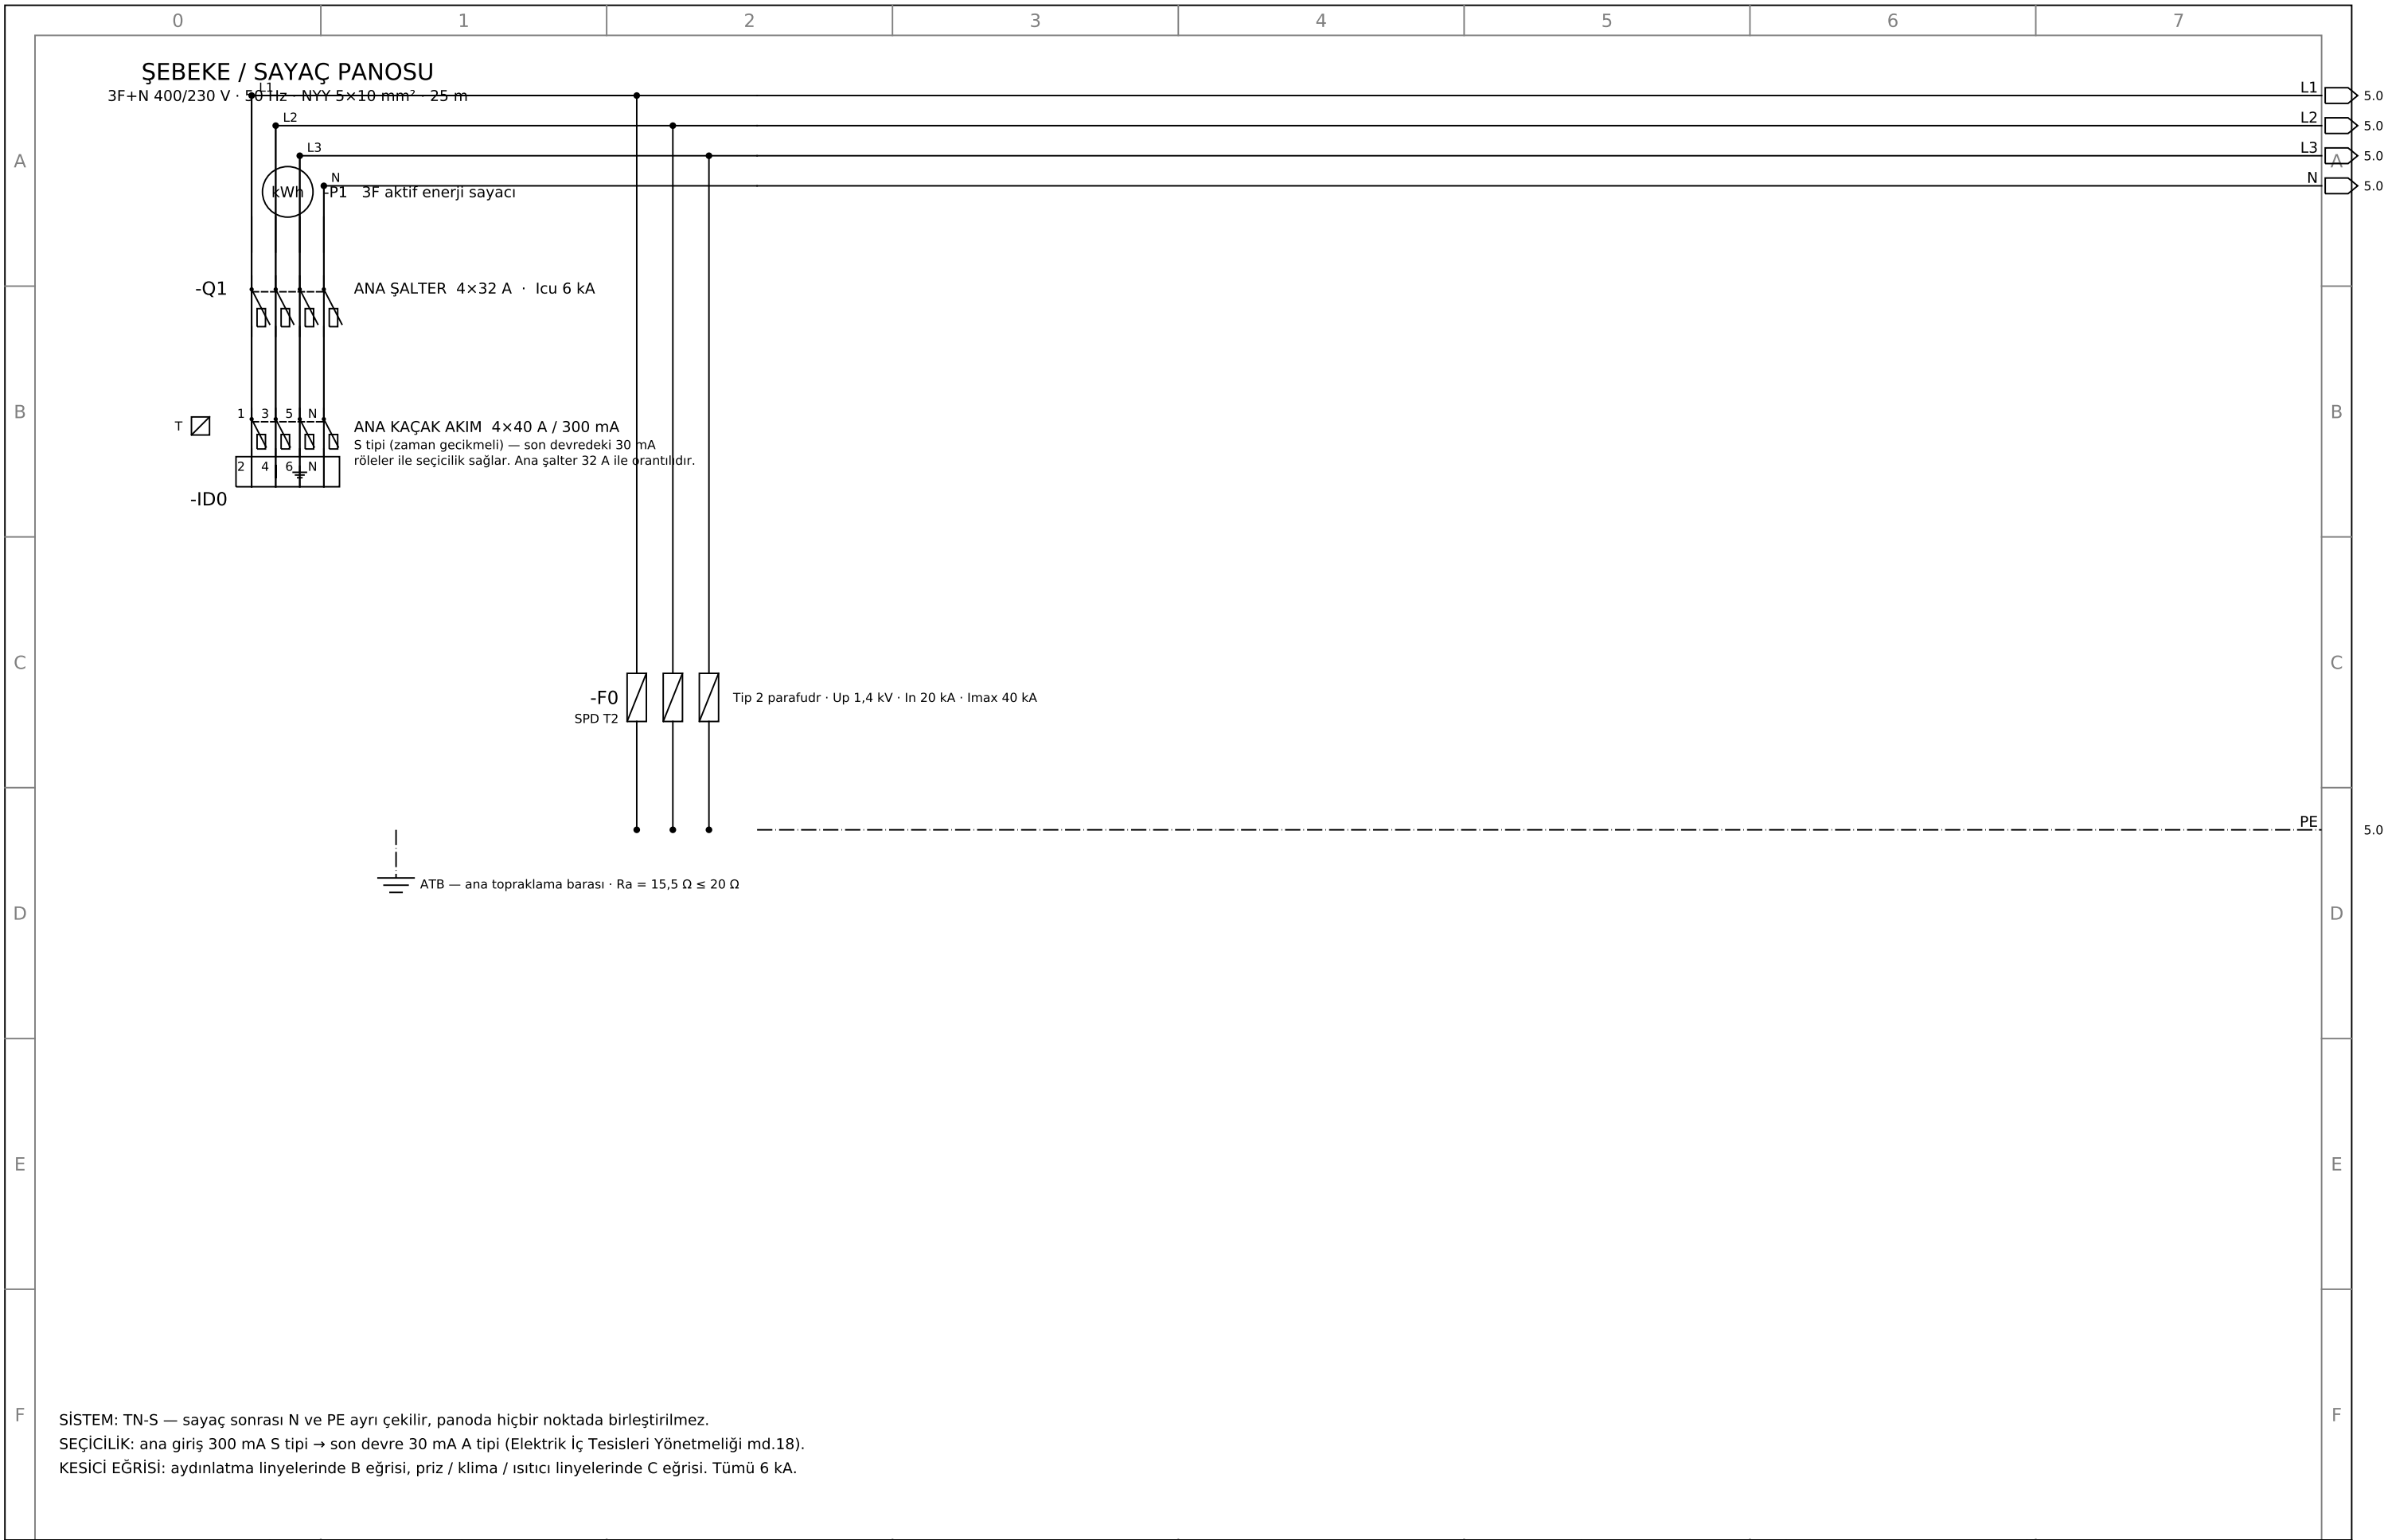


Drawn By / Çizen	CC	Customer Name / Müşteri Adı	ÖZEL — MALTEPE / İDEALTEPE	Project Number / Proje Numarası	GYM-25-001-001	Sheet: / Sayfa	4
Checked By / Kontrol Eden	—	Project Description / Proje Açıklaması	MOBİLYA MAĞAZASI → FONKSİYONEL ANTRENMAN STÜDYOSU			Next sheet: / Sonraki	5
Approved By / Onaylayan	—	Panel Name / Pano Adı	ADP	Revision / Revizyon	Rev H	Total sheets: / Toplam	12
Project Date / Proje Tarihi	17 Eylül 2026	Page Description / Sayfa Açıklaması	Incoming Supply / Ana Besleme	Standards / Standartlar	IEC 61439-1&2 · IEC 60617	Sheet size / Kâğıt	A3

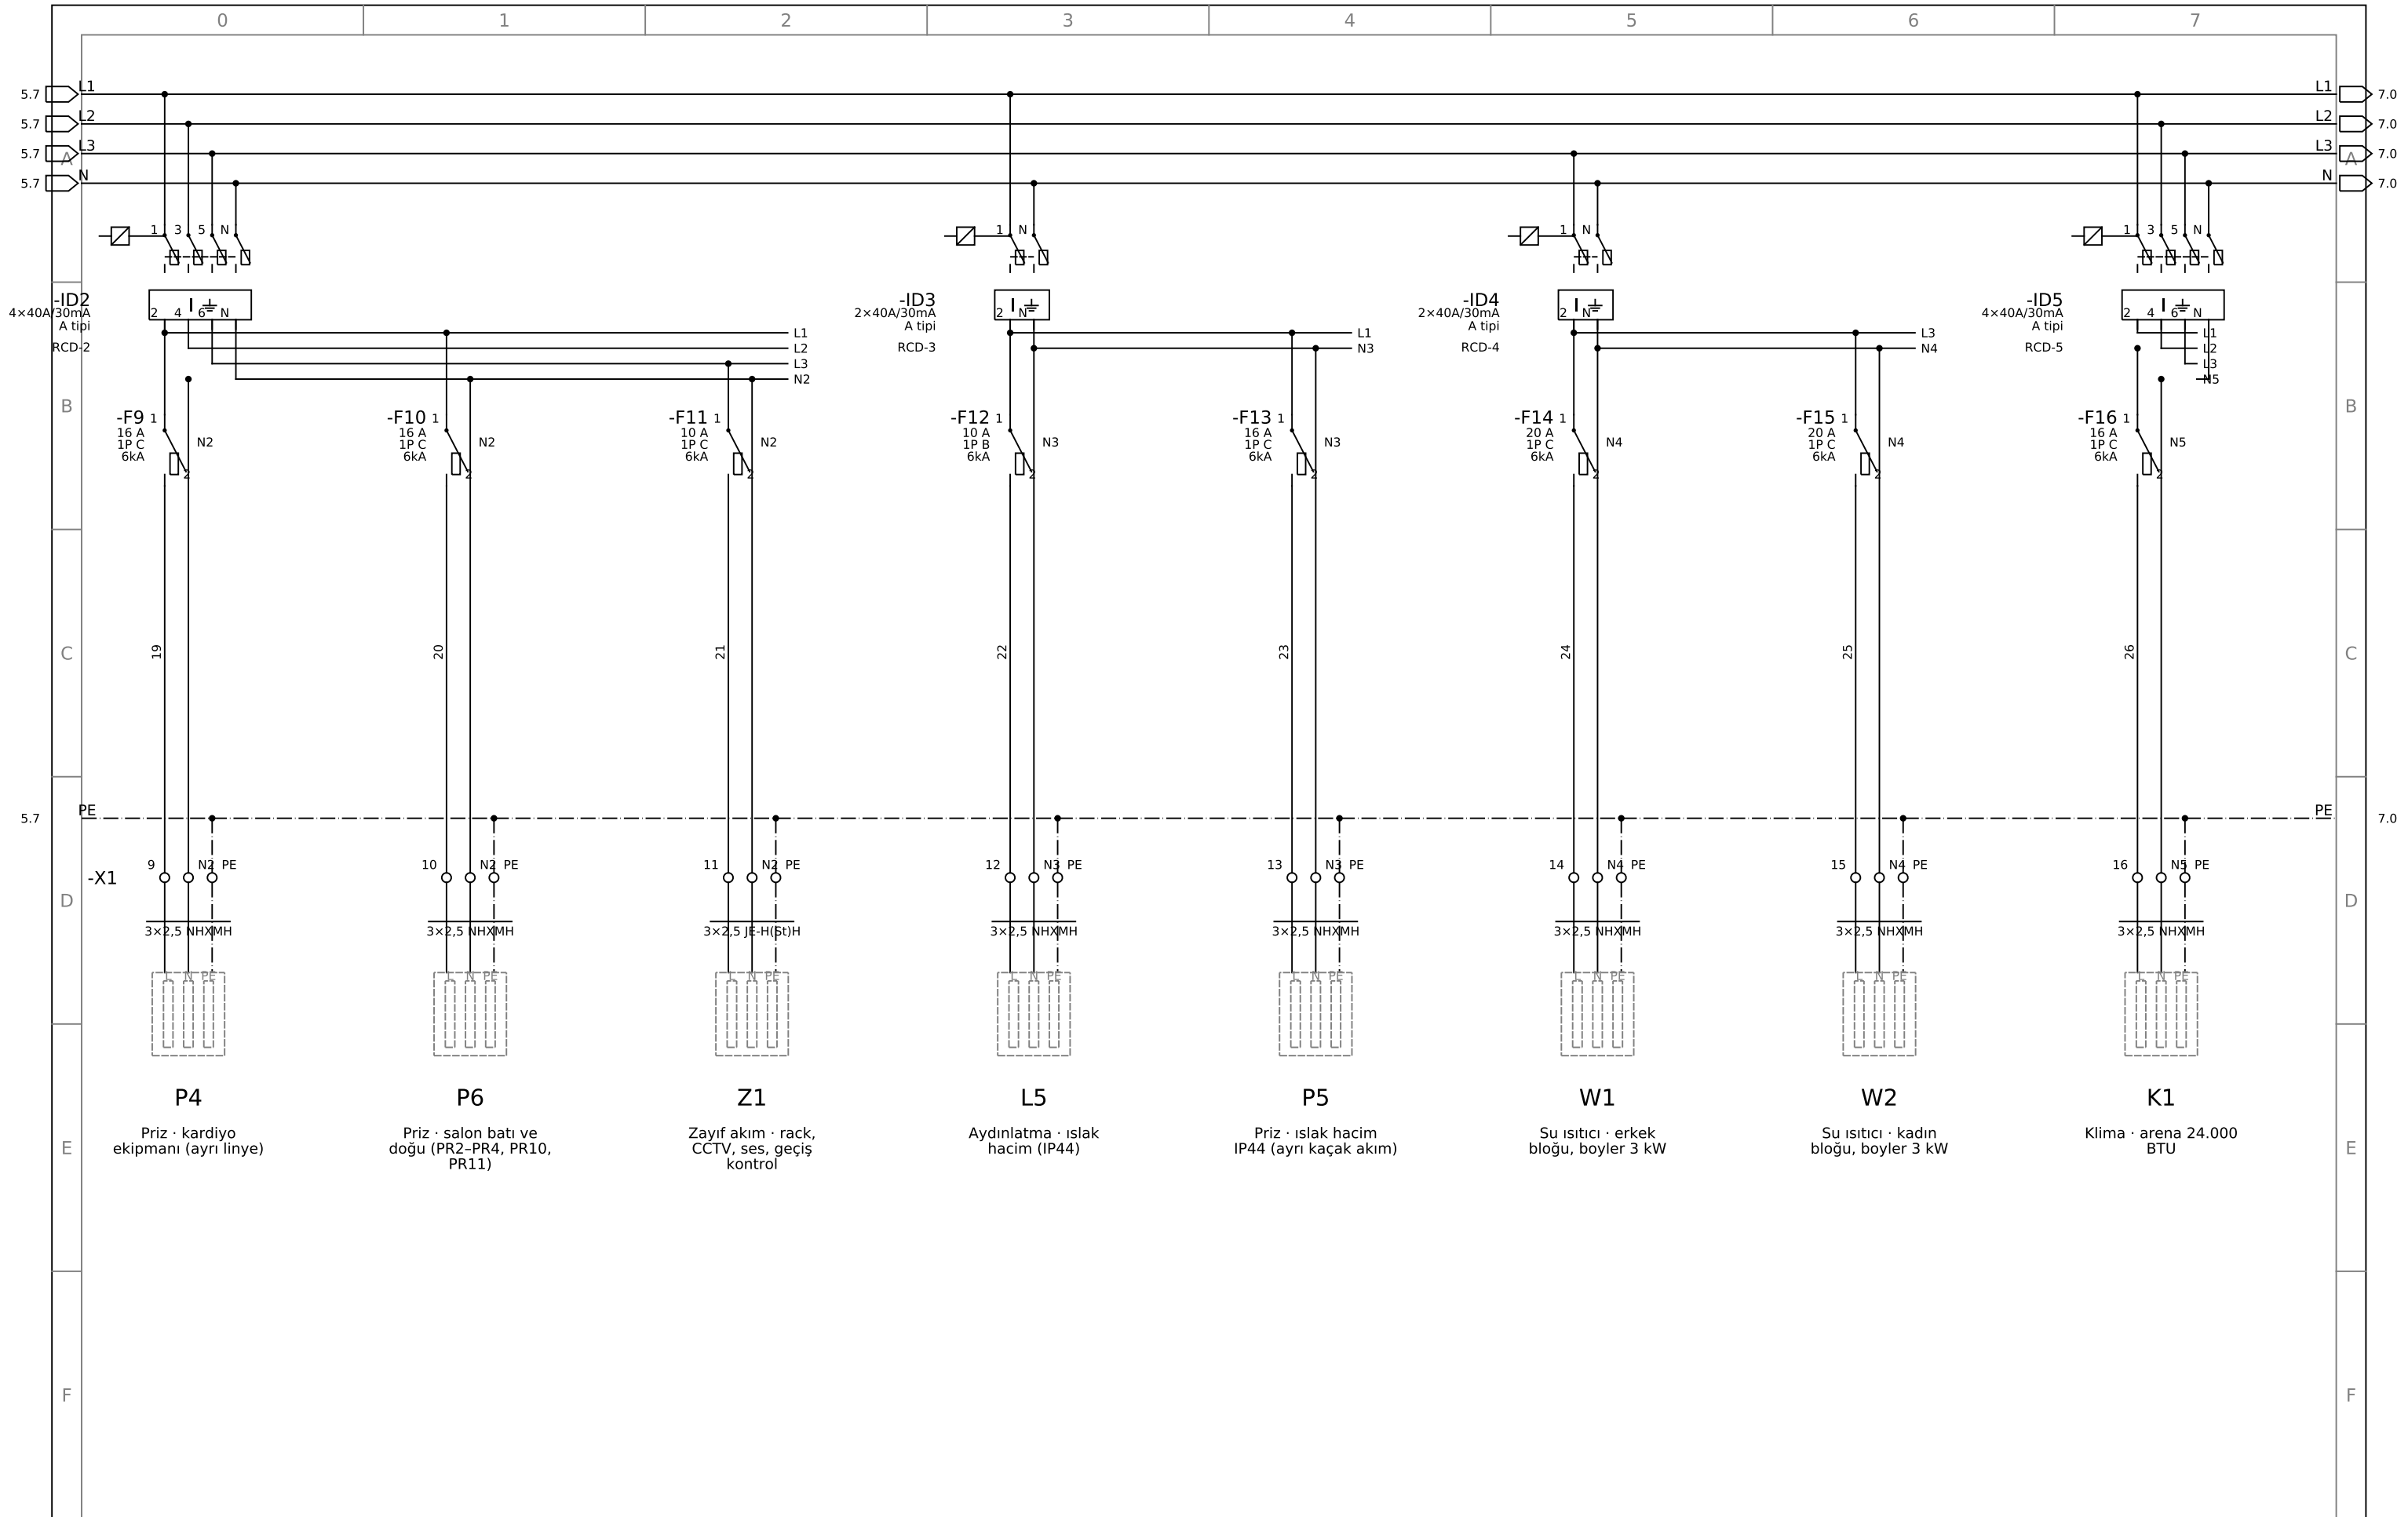

Drawn By / Çizen	CC	Customer Name / Müşteri Adı	ÖZEL — MALTEPE / İDEALTEPE		Project Number / Proje Numarası	GYM-25-001-001	Sheet: / Sayfa	6
Checked By / Kontrol Eden	—	Project Description / Proje Açıklaması	MOBİLYA MAĞAZASI → FONKSİYONEL ANTRENMAN STÜDYOSU				Next sheet: / Sonraki	7
Approved By / Onaylayan	—	Panel Name / Pano Adı	ADP		Revision / Revizyon	Rev H	Total sheets: / Toplam	12
Project Date / Proje Tarihi	17 Eylül 2026	Page Description / Sayfa Açıklaması	Schematic Diagram / Şematik Diyagram		Standards / Standartlar	IEC 61439-1&2 · IEC 60617	Sheet size / Kâğıt	A3

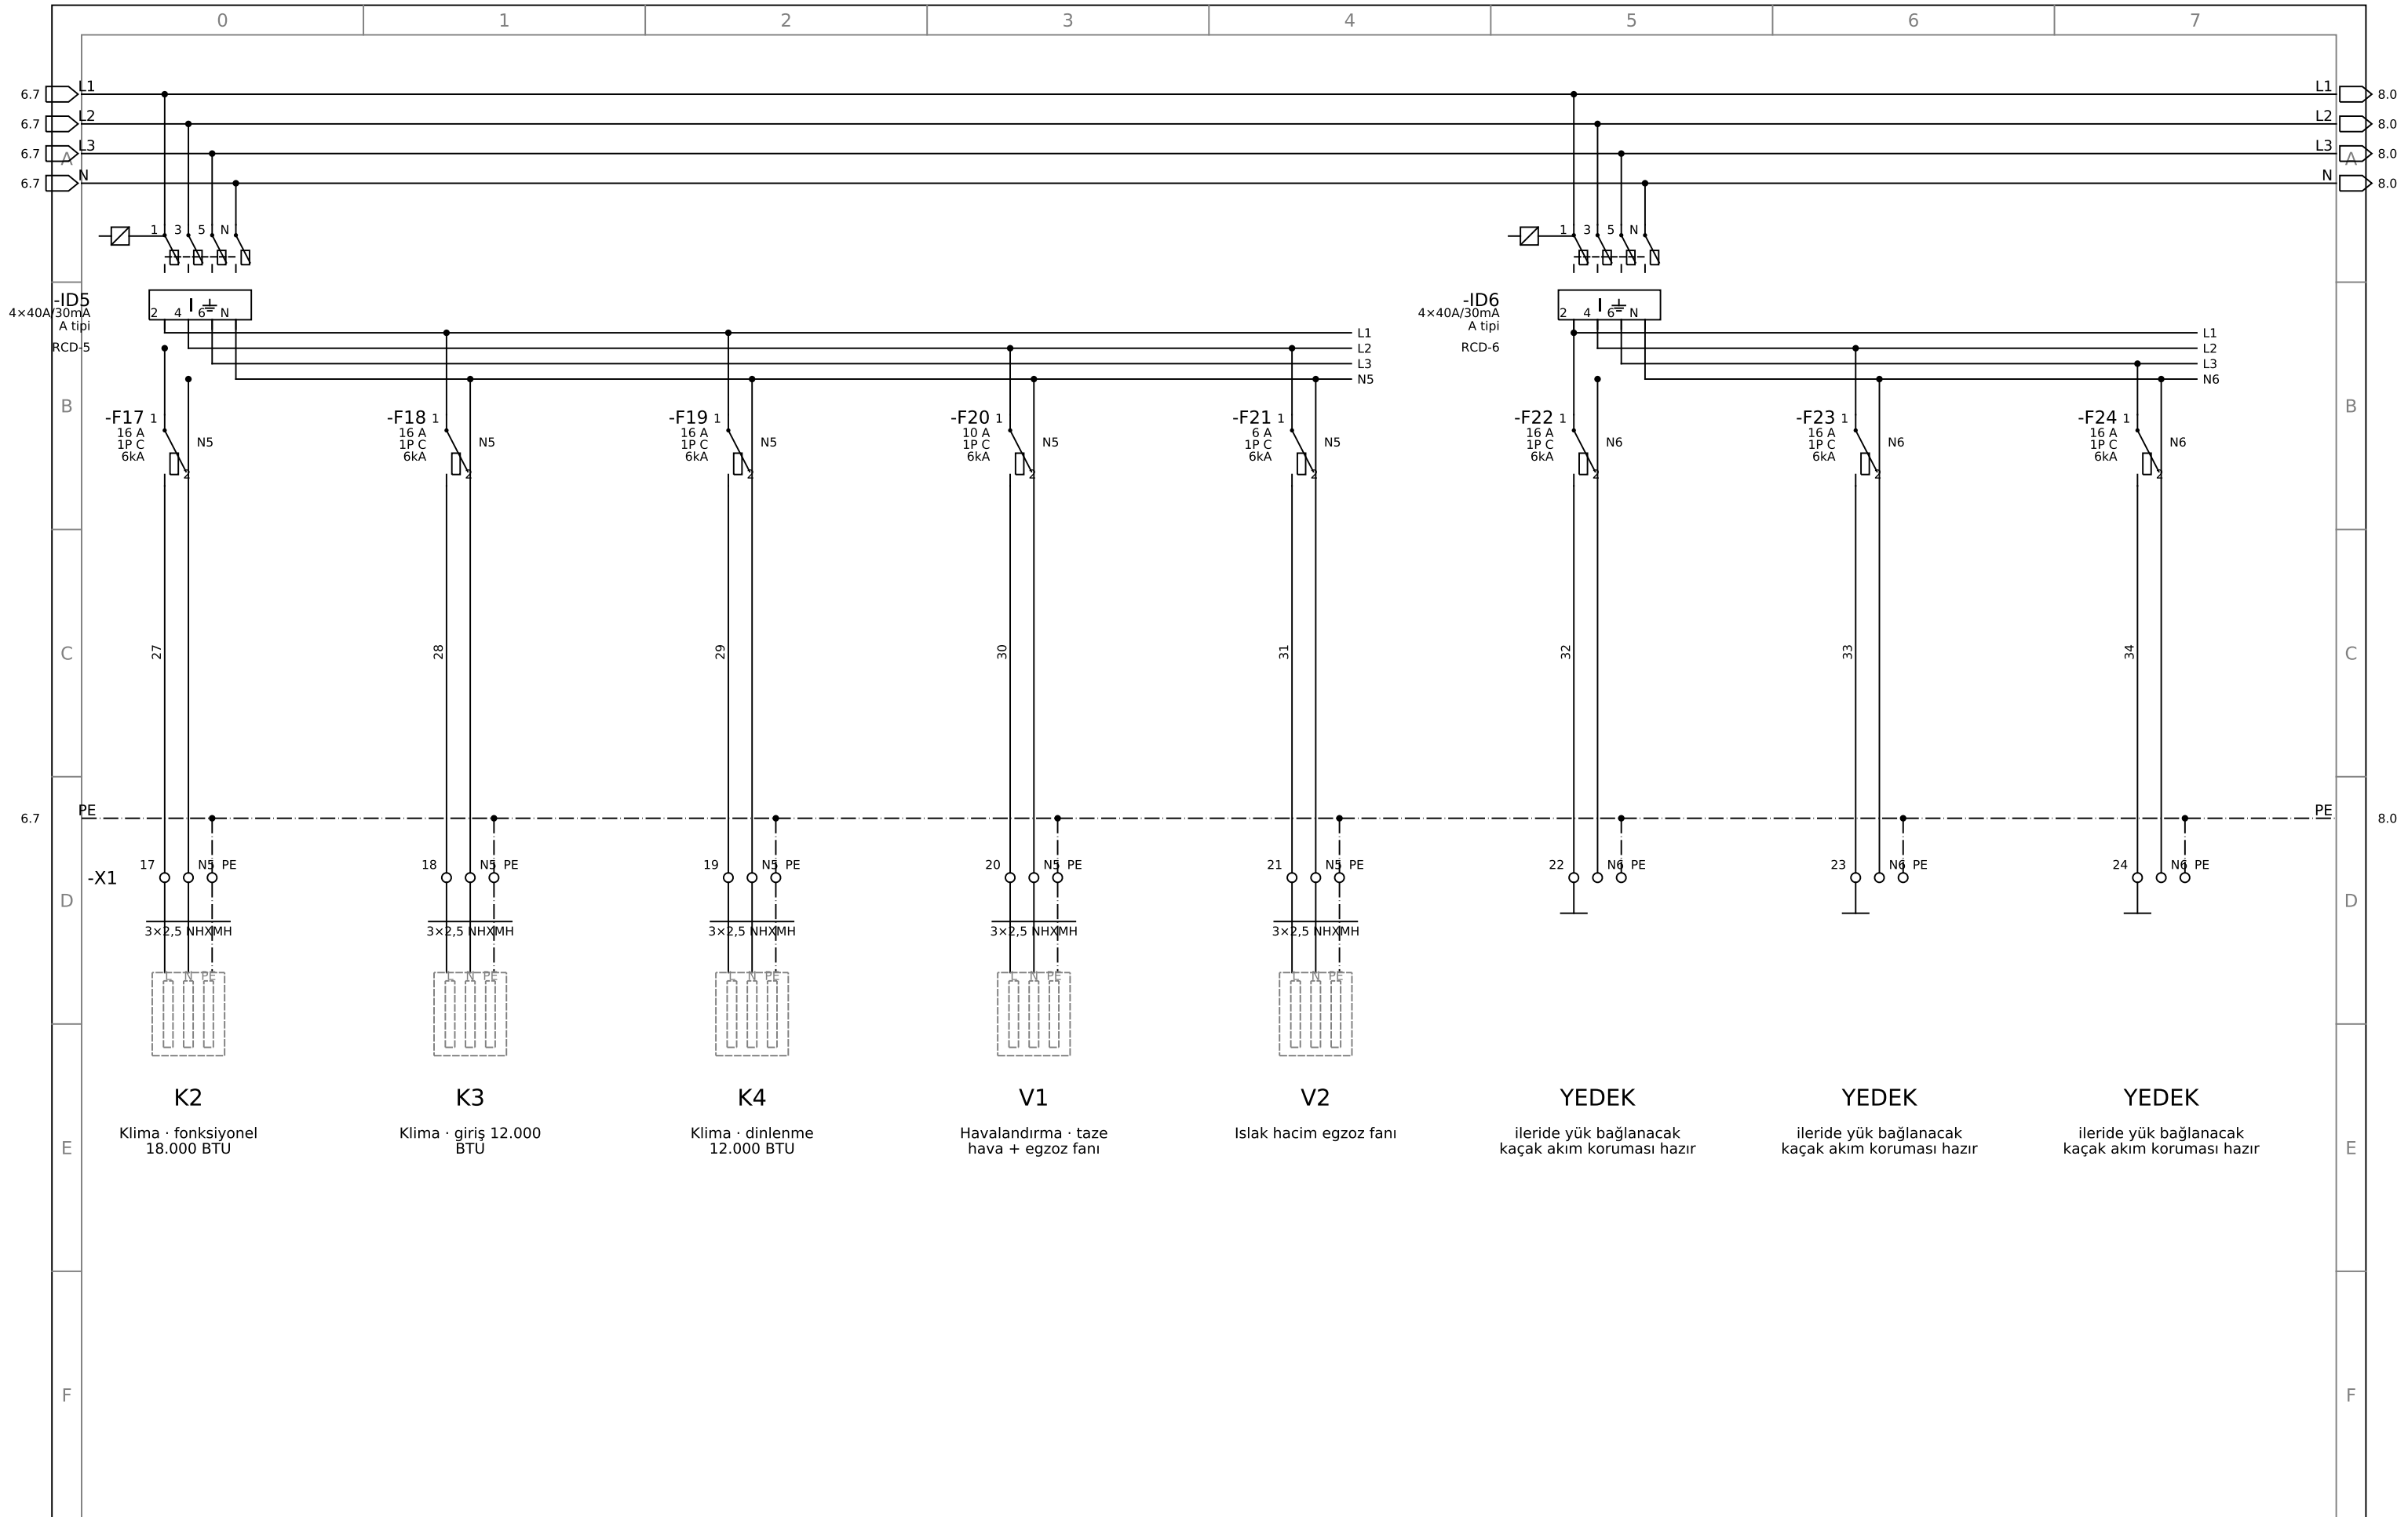

Drawn By / Çizen	CC	Customer Name / Müşteri Adı	ÖZEL — MALTEPE / İDEALTEPE	Project Number / Proje Numarası	GYM-25-001-001	Sheet: / Sayfa	7
Checked By / Kontrol Eden	—	Project Description / Proje Açıklaması	MOBİLYA MAĞAZASI → FONKSİYONEL ANTRENMAN STÜDYOSU			Next sheet: / Sonraki	8
Approved By / Onaylayan	—	Panel Name / Pano Adı	ADP	Revision / Revizyon	Rev H	Total sheets: / Toplam	12
Project Date / Proje Tarihi	17 Eylül 2026	Page Description / Sayfa Açıklaması	Schematic Diagram / Şematik Diyagram	Standards / Standartlar	IEC 61439-1&2 · IEC 60617	Sheet size / Kâğıt	A3

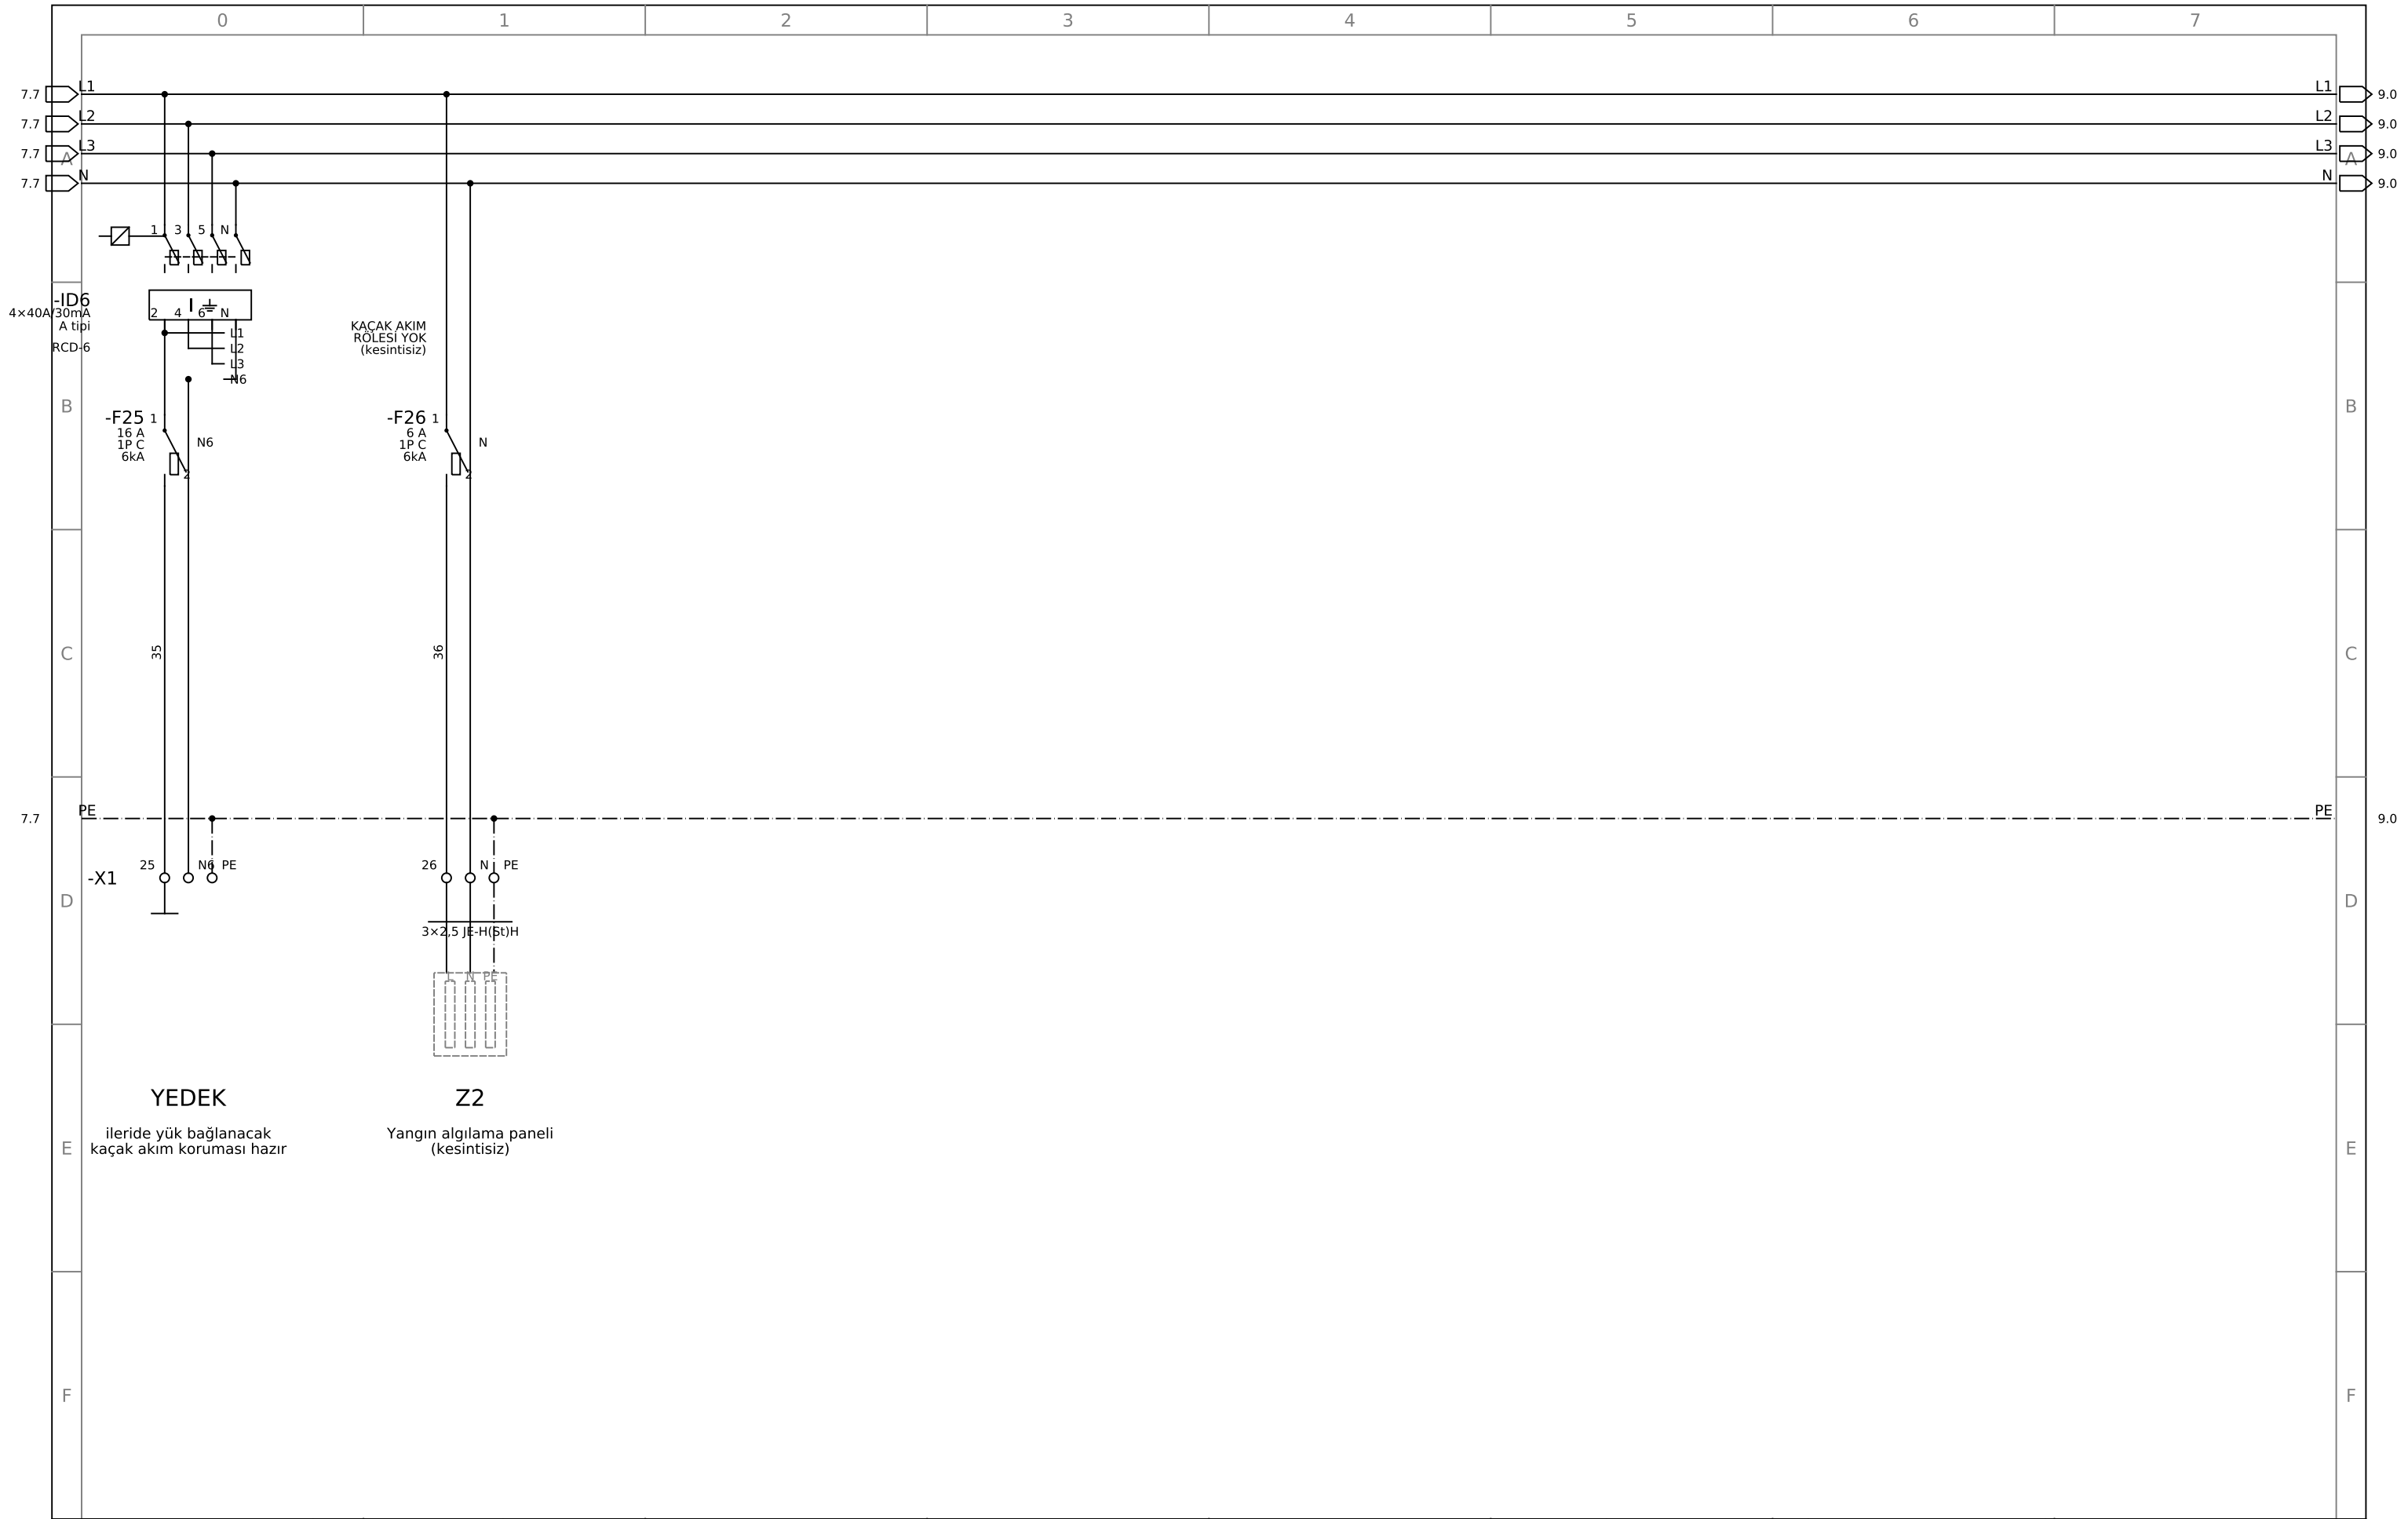

Drawn By / Çizen	CC	Customer Name / Müşteri Adı	ÖZEL — MALTEPE / İDEALTEPE	Project Number / Proje Numarası	GYM-25-001-001	Sheet: / Sayfa	8
Checked By / Kontrol Eden	—	Project Description / Proje Açıklaması	MOBİLYA MAĞAZASI → FONKSİYONEL ANTRENMAN STÜDYOSU			Next sheet: / Sonraki	9
Approved By / Onaylayan	—	Panel Name / Pano Adı	ADP	Revision / Revizyon	Rev H	Total sheets: / Toplam	12
Project Date / Proje Tarihi	17 Eylül 2026	Page Description / Sayfa Açıklaması	Schematic Diagram / Şematik Diyagram	Standards / Standartlar	IEC 61439-1&2 · IEC 60617	Sheet size / Kâğıt	A3

0		1		2		3		4		5		6		7	
KLEMENS PLANI / TERMINAL DIAGRAM — -X1															
A	KLEMENS	LİNYE	İLETKEN	TEL NO	KABLO	HEDEF / DESTINATION	SAYFA	KAÇAK AKIM							
	1	L1	L	11	NHXMH 3×2,5	Aydınlatma — arena / serbest ağırlık	5	RCD-1							
		L1	N	N1	NHXMH 3×2,5	Aydınlatma — arena / serbest ağırlık	5	RCD-1							
B		L1	PE	PE	NHXMH 3×2,5	Aydınlatma — arena / serbest ağırlık	5	RCD-1							
	2	L2	L	12	NHXMH 3×2,5	Aydınlatma — fonksiyonel / kardiyo	5	RCD-1							
		L2	N	N1	NHXMH 3×2,5	Aydınlatma — fonksiyonel / kardiyo	5	RCD-1							
C		L2	PE	PE	NHXMH 3×2,5	Aydınlatma — fonksiyonel / kardiyo	5	RCD-1							
	3	L3	L	13	NHXMH 3×2,5	Aydınlatma — dinlenme salonu	5	RCD-1							
		L3	N	N1	NHXMH 3×2,5	Aydınlatma — dinlenme salonu	5	RCD-1							
D		L3	PE	PE	NHXMH 3×2,5	Aydınlatma — dinlenme salonu	5	RCD-1							
	4	L4	L	14	NHXMH 3×2,5	Aydınlatma — giriş / banko	5	RCD-1							
		L4	N	N1	NHXMH 3×2,5	Aydınlatma — giriş / banko	5	RCD-1							
E		L4	PE	PE	NHXMH 3×2,5	Aydınlatma — giriş / banko	5	RCD-1							
	5	L6	L	15	NHXMH 3×2,5	Acil aydınlatma ve yönlendirme	5	RCD-1							
		L6	N	N1	NHXMH 3×2,5	Acil aydınlatma ve yönlendirme	5	RCD-1							
F		L6	PE	PE	NHXMH 3×2,5	Acil aydınlatma ve yönlendirme	5	RCD-1							
	6	P1	L	16	NHXMH 3×2,5	Priz — salon kuzey (PR12-PR16, PR1)	5	RCD-2							
		P1	N	N2	NHXMH 3×2,5	Priz — salon kuzey (PR12-PR16, PR1)	5	RCD-2							
A		P1	PE	PE	NHXMH 3×2,5	Priz — salon kuzey (PR12-PR16, PR1)	5	RCD-2							
	7	P2	L	17	NHXMH 3×2,5	Priz — salon güney (PR5-PR9)	5	RCD-2							
		P2	N	N2	NHXMH 3×2,5	Priz — salon güney (PR5-PR9)	5	RCD-2							
B		P2	PE	PE	NHXMH 3×2,5	Priz — salon güney (PR5-PR9)	5	RCD-2							
	8	P3	L	18	NHXMH 3×2,5	Priz — banko, POS, veri	5	RCD-2							
		P3	N	N2	NHXMH 3×2,5	Priz — banko, POS, veri	5	RCD-2							
C		P3	PE	PE	NHXMH 3×2,5	Priz — banko, POS, veri	5	RCD-2							
	9	P4	L	19	NHXMH 3×2,5	Priz — kardiyo ekipmanı (ayrı linye)	6	RCD-2							
		P4	N	N2	NHXMH 3×2,5	Priz — kardiyo ekipmanı (ayrı linye)	6	RCD-2							
D		P4	PE	PE	NHXMH 3×2,5	Priz — kardiyo ekipmanı (ayrı linye)	6	RCD-2							
	10	P6	L	20	NHXMH 3×2,5	Priz — salon batı ve doğu (PR2-PR4, PR10, PR	6	RCD-2							
		P6	N	N2	NHXMH 3×2,5	Priz — salon batı ve doğu (PR2-PR4, PR10, PR	6	RCD-2							
E		P6	PE	PE	NHXMH 3×2,5	Priz — salon batı ve doğu (PR2-PR4, PR10, PR	6	RCD-2							
	11	Z1	L	21	JE-H(St)H 3×2,5	Zayıf akım — rack, CCTV, ses, geçiş kontrol	6	RCD-2							
		Z1	N	N2	JE-H(St)H 3×2,5	Zayıf akım — rack, CCTV, ses, geçiş kontrol	6	RCD-2							
F		Z1	PE	PE	JE-H(St)H 3×2,5	Zayıf akım — rack, CCTV, ses, geçiş kontrol	6	RCD-2							
	12	L5	L	22	NHXMH 3×2,5	Aydınlatma — ıslak hacim (IP44)	6	RCD-3							
		L5	N	N3	NHXMH 3×2,5	Aydınlatma — ıslak hacim (IP44)	6	RCD-3							
A		L5	PE	PE	NHXMH 3×2,5	Aydınlatma — ıslak hacim (IP44)	6	RCD-3							
	13	P5	L	23	NHXMH 3×2,5	Priz — ıslak hacim IP44 (ayrı kaçak akım)	6	RCD-3							
		P5	N	N3	NHXMH 3×2,5	Priz — ıslak hacim IP44 (ayrı kaçak akım)	6	RCD-3							
B		P5	PE	PE	NHXMH 3×2,5	Priz — ıslak hacim IP44 (ayrı kaçak akım)	6	RCD-3							
	14	W1	L	24	NHXMH 3×2,5	Su ısıtıcı — erkek bloğu, boyler 3 kW	6	RCD-4							
		W1	N	N4	NHXMH 3×2,5	Su ısıtıcı — erkek bloğu, boyler 3 kW	6	RCD-4							
C		W1	PE	PE	NHXMH 3×2,5	Su ısıtıcı — erkek bloğu, boyler 3 kW	6	RCD-4							
	15	W2	L	25	NHXMH 3×2,5	Su ısıtıcı — kadın bloğu, boyler 3 kW	6	RCD-4							
		W2	N	N4	NHXMH 3×2,5	Su ısıtıcı — kadın bloğu, boyler 3 kW	6	RCD-4							
D		W2	PE	PE	NHXMH 3×2,5	Su ısıtıcı — kadın bloğu, boyler 3 kW	6	RCD-4							
	16	K1	L	26	NHXMH 3×2,5	Klima — arena 24.000 BTU	6	RCD-5							
		K1	N	N5	NHXMH 3×2,5	Klima — arena 24.000 BTU	6	RCD-5							
E		K1	PE	PE	NHXMH 3×2,5	Klima — arena 24.000 BTU	6	RCD-5							
	17	K2	L	27	NHXMH 3×2,5	Klima — fonksiyonel 18.000 BTU	7	RCD-5							
		K2	N	N5	NHXMH 3×2,5	Klima — fonksiyonel 18.000 BTU	7	RCD-5							
F		K2	PE	PE	NHXMH 3×2,5	Klima — fonksiyonel 18.000 BTU	7	RCD-5							
	18	K3	L	28	NHXMH 3×2,5	Klima — giriş 12.000 BTU	7	RCD-5							
		K3	N	N5	NHXMH 3×2,5	Klima — giriş 12.000 BTU	7	RCD-5							
A		K3	PE	PE	NHXMH 3×2,5	Klima — giriş 12.000 BTU	7	RCD-5							
	19	K4	L	29	NHXMH 3×2,5	Klima — dinlenme 12.000 BTU	7	RCD-5							
		K4	N	N5	NHXMH 3×2,5	Klima — dinlenme 12.000 BTU	7	RCD-5							
B		K4	PE	PE	NHXMH 3×2,5	Klima — dinlenme 12.000 BTU	7	RCD-5							
	20	V1	L	30	NHXMH 3×2,5	Havalandırma — taze hava + egzoz fanı	7	RCD-5							
		V1	N	N5	NHXMH 3×2,5	Havalandırma — taze hava + egzoz fanı	7	RCD-5							
C	Drawn By / Çizen	CC	Customer Name / Müşteri Adı	ÖZEL — MALTEPE / IDEALTEPE	HEAVEN — TAZE HAVA + EGZUZ FANI										
	Checked By / Kontrol Eden	V1	Project Description / Proje Açıklaması	PEMOBİLYA MAĞAZASI — FONKSİYONEL ANTRENMAN STÜDYOSU	HEAVEN — TAZE HAVA + EGZUZ FANI	7		RCD-5							
	Approved By / Onaylayan	V2	Panel Name / Pano Adı	ADP	Islak hacim egzoz fanı	7		RCD-5							
D	Project Date / Proje Tarihi	17 Eylül 2026	Page Description / Sayfa Açıklaması	Terminal Diagram / Klemens Planı	Islak hacim egzoz fanı	7		RCD-5							
		26	Z2	L	36	JE-H(St)H 3×2,5	Yangın algılama paneli (kesintisiz)	8							
			Z2	N	N0	JE-H(St)H 3×2,5	Yangın algılama paneli (kesintisiz)	8							
E			Z2	PE	PE	JE-H(St)H 3×2,5	Yangın algılama paneli (kesintisiz)	8							
F															
A															
B															
C															
D															
E															
F															
Project Number / Proje Numarası							GYM-25-001-001		Sheet: / Sayfa		9				
Revision / Revizyon							Rev H		Next sheet: / Sonraki		10				
Standards / Standartlar							IEC 61439-1&2 · IEC 60617		Total sheets: / Toplam		12				
									Sheet size / Kâğıt		A3				

	0	1	2	3	4	5	6	7
A	PANO ÖNDEN GÖRÜNÜŞ / PANEL FRONT VIEW — ölçek 1:5 ADP · 800×1000×250 mm · IP54 · Form 2b · sac gövde RAL 7035 R1 -Q1 -ID0 -F0 BOŞ 12 MOD 4 4 4 R2 -ID1 -F1 -F2 -F3 -F4 -F5 -ID2 BOŞ 1 MOD 4 3 3 3 3 3 4 R3 -F6 -F7 -F8 -F9 -F10 -F11 -ID3 -F12 BOŞ 1 MOD 3 3 3 3 3 3 2 3 R4 -F13 -ID4 -F14 -F15 -ID5 -F16 -F17 -F18 -F19 -F20 -F21 -ID6 -F22 -F23 -F24 -F25 -F26 3 2 3 3 4 3 3 3 3 3 3 4 1 1 1 1 3							
B								
C								
D								
E								
F								

SIRA	CİHAZ	MODÜL	AÇIKLAMA
R1	-Q1	4	ANA ŞALTER 4×32 A
R1	-ID0	4	ANA KAÇAK AKIM 4×40 A/300 mA
R1	-F0	4	SPD Tip 2
R2	-ID1	4	4×40 A / 30 mA, A tipi
R2	-F1	3	L1 10A B
R2	-F2	3	L2 10A B
R2	-F3	3	L3 10A B
R2	-F4	3	L4 10A B
R2	-F5	3	L6 6A B
R2	-ID2	4	4×40 A / 30 mA, A tipi
R3	-F6	3	P1 16A C
R3	-F7	3	P2 16A C
R3	-F8	3	P3 16A C
R3	-F9	3	P4 16A C
R3	-F10	3	P6 16A C
R3	-F11	3	Z1 10A C
R3	-ID3	2	2×40 A / 30 mA, A tipi
R3	-F12	3	L5 10A B
R4	-F13	3	P5 16A C
R4	-ID4	2	2×40 A / 30 mA, A tipi
R4	-F14	3	W1 20A C
R4	-F15	3	W2 20A C
R4	-ID5	4	4×40 A / 30 mA, A tipi
R4	-F16	3	K1 16A C
R4	-F17	3	K2 16A C
R4	-F18	3	K3 16A C
R4	-F19	3	K4 16A C
R4	-F20	3	V1 10A C
R4	-F21	3	V2 6A C
R4	-ID6	4	4×40 A / 30 mA, A tipi
R4	-F22	1	Y1 16A C
R4	-F23	1	Y2 16A C
R4	-F24	1	Y3 16A C
R4	-F25	1	Y4 16A C
R4	-F26	3	Z2 6A C

Drawn By / Çizen	CC	Customer Name / Müşteri Adı	ÖZEL — MALTEPE / İDEALTEPE	Project Number / Proje Numarası	GYM-25-001-001	Sheet: / Sayfa	10
Checked By / Kontrol Eden	—	Project Description / Proje Açıklaması	MOBİLYA MAĞAZASI → FONKSİYONEL ANTRENMAN STÜDYOSU			Next sheet: / Sonraki	11
Approved By / Onaylayan	—	Panel Name / Pano Adı	ADP	Revision / Revizyon	Rev H	Total sheets: / Toplam	12
Project Date / Proje Tarihi	17 Eylül 2026	Page Description / Sayfa Açıklaması	Panel Overview / Pano Önden Görünüş	Standards / Standartlar	IEC 61439-1&2 · IEC 60617	Sheet size / Kâğıt	A3

ADP YÜKLEME CETVELİ / LOAD SCHEDULE

Grup kaçak akım röleleri ve kapsadıkları linyeler ayrı sütunda gösterilmiştir.

NO	LİNYE	MAHAL / YÜK	FAZ	KESİCİ	KAÇAK AKIM (GRUP)	KABLO	BORU	UZUNLUK	Pb (kW)	cos φ	Ib (A)	ΔU (%)	SONUÇ
1	L1	Aydınlatma — arena / serbest ağırlık	L2	10 A · 1P B · 6 kA	RCD-1 · 4×40 A / 30 mA A tipi	NHXXMH 3×2,5	Ø20	14 m	0,28	0,95	1,3	0,13	UYGUN
2	L2	Aydınlatma — fonksiyonel / kardiyo	L3	10 A · 1P B · 6 kA	↑ aynı grup	NHXXMH 3×2,5	Ø20	11 m	0,12	0,95	0,5	0,05	UYGUN
3	L3	Aydınlatma — dinlenme salonu	L1	10 A · 1P B · 6 kA	↑ aynı grup	NHXXMH 3×2,5	Ø20	14 m	0,12	0,95	0,5	0,06	UYGUN
4	L4	Aydınlatma — giriş / banko	L3	10 A · 1P B · 6 kA	↑ aynı grup	NHXXMH 3×2,5	Ø20	12 m	0,08	0,95	0,4	0,03	UYGUN
5	L6	Acil aydınlatma ve yönlendirme	L2	6 A · 1P B · 6 kA	↑ aynı grup	NHXXMH 3×2,5	Ø20	10 m	0,06	0,95	0,3	0,02	UYGUN
6	P1	Priz — salon kuzey (PR12-PR16, PR1)	L1	16 A · 1P C · 6 kA	RCD-2 · 4×40 A / 30 mA A tipi	NHXXMH 3×2,5	Ø20	8 m	0,90	0,90	4,3	0,24	UYGUN
7	P2	Priz — salon güney (PR5-PR9)	L3	16 A · 1P C · 6 kA	↑ aynı grup	NHXXMH 3×2,5	Ø20	17 m	0,75	0,90	3,6	0,42	UYGUN
8	P3	Priz — banko, POS, veri	L2	16 A · 1P C · 6 kA	↑ aynı grup	NHXXMH 3×2,5	Ø20	9 m	1,00	0,90	4,8	0,30	UYGUN
9	P4	Priz — kardiyo ekipmanı (ayrı linye)	L1	16 A · 1P C · 6 kA	↑ aynı grup	NHXXMH 3×2,5	Ø20	17 m	2,40	0,90	11,6	1,40	UYGUN
10	P6	Priz — salon batı ve doğu (PR2-PR4, PR	L1	16 A · 1P C · 6 kA	↑ aynı grup	NHXXMH 3×2,5	Ø20	10 m	0,75	0,90	3,6	0,27	UYGUN
11	Z1	Zayıf akım — rack, CCTV, ses, geçiş ko	L3	10 A · 1P C · 6 kA	↑ aynı grup	JE-H(St)H 3×2,5	Ø20	9 m	0,60	0,90	2,9	0,18	UYGUN
12	L5	Aydınlatma — ıslak hacim (IP44)	L1	10 A · 1P B · 6 kA	RCD-3 · 2×40 A / 30 mA A tipi	NHXXMH 3×2,5	Ø20	16 m	0,11	0,95	0,5	0,06	UYGUN
13	P5	Priz — ıslak hacim IP44 (ayrı kaçak ak	L3	16 A · 1P C · 6 kA	↑ aynı grup	NHXXMH 3×2,5	Ø20	16 m	0,50	0,90	2,4	0,27	UYGUN
14	W1	Su ısıtıcı — erkek bloğu, boyler 3 kW	L3	20 A · 1P C · 6 kA	RCD-4 · 2×40 A / 30 mA A tipi	NHXXMH 3×2,5	Ø20	16 m	3,00	1,00	13,0	1,66	UYGUN
15	W2	Su ısıtıcı — kadın bloğu, boyler 3 kW	L3	20 A · 1P C · 6 kA	↑ aynı grup	NHXXMH 3×2,5	Ø20	19 m	3,00	1,00	13,0	1,97	UYGUN
16	K1	Klima — arena 24.000 BTU	L2	16 A · 1P C · 6 kA	RCD-5 · 4×40 A / 30 mA A tipi	NHXXMH 3×2,5	Ø20	18 m	2,20	0,85	11,3	1,32	UYGUN
17	K2	Klima — fonksiyonel 18.000 BTU	L2	16 A · 1P C · 6 kA	↑ aynı grup	NHXXMH 3×2,5	Ø20	13 m	1,70	0,85	8,7	0,73	UYGUN
18	K3	Klima — giriş 12.000 BTU	L1	16 A · 1P C · 6 kA	↑ aynı grup	NHXXMH 3×2,5	Ø20	12 m	1,15	0,85	5,9	0,48	UYGUN
19	K4	Klima — dinlenme 12.000 BTU	L1	16 A · 1P C · 6 kA	↑ aynı grup	NHXXMH 3×2,5	Ø20	15 m	1,15	0,85	5,9	0,58	UYGUN
20	V1	Havalandırma — taze hava + egzoz fanı	L2	10 A · 1P C · 6 kA	↑ aynı grup	NHXXMH 3×2,5	Ø20	14 m	0,45	0,85	2,3	0,21	UYGUN
21	V2	Islak hacim egzoz fanı	L2	6 A · 1P C · 6 kA	↑ aynı grup	NHXXMH 3×2,5	Ø20	16 m	0,12	0,85	0,6	0,07	UYGUN
22	Y1	YEDEK — ileride yük bağlanacak	L1	16 A · 1P C · 6 kA	RCD-6 · 4×40 A / 30 mA A tipi	—	—	—	—	—	—	—	YEDEK
23	Y2	YEDEK — ileride yük bağlanacak	L2	16 A · 1P C · 6 kA	↑ aynı grup	—	—	—	—	—	—	—	YEDEK
24	Y3	YEDEK — ileride yük bağlanacak	L3	16 A · 1P C · 6 kA	↑ aynı grup	—	—	—	—	—	—	—	YEDEK
25	Y4	YEDEK — ileride yük bağlanacak	L1	16 A · 1P C · 6 kA	↑ aynı grup	—	—	—	—	—	—	—	YEDEK
26	Z2	Yangın algılama paneli (kesintisiz)	L1	6 A · 1P C · 6 kA	— kaçak akım rölesi yok (kesintisiz)	JE-H(St)H 3×2,5	Ø20	10 m	0,15	0,90	0,7	0,05	UYGUN

ÖZET / SUMMARY

Bağlı güç / Connected	20,59 kW	Talep gücü / Demand	14,63 kW	L1 / L2 / L3 (kW)	4,86 / 4,91 / 4,87	Faz dengesizliği / Imbalance	%1,0
Ana şalter / Main switch	4x32 A	Ana kaçak akım / Main RCD	4x40 A / 300 mA S tipi	Grup kaçak akım sayısı / RCD groups	7 adet	Toplam ΔU / Total	%2,49

Drawn By / Çizen	CC	Customer Name / Müşteri Adı	ÖZEL — MALTEPE / İDEALTEPE	Project Number / Proje Numarası	GYM-25-001-001	Sheet: / Sayfa	11
Checked By / Kontrol Eden	—	Project Description / Proje Açıklaması	MOBİLYA MAĞAZASI → FONKSİYONEL ANTRENMAN STÜDYOSU			Next sheet: / Sonraki	12
Approved By / Onaylayan	—	Panel Name / Pano Adı	ADP	Revision / Revizyon	Rev H	Total sheets: / Toplam	12
Project Date / Proje Tarihi	17 Eylül 2026	Page Description / Sayfa Açıklaması	Load Schedule / Yükleme Cetveli	Standards / Standartlar	IEC 61439-1&2 · IEC 60617	Sheet size / Kâğıt	A3

	0	1	2	3	4	5	6	7	
A	MALZEME LİSTESİ / PARTS LIST <table><tr><th>S.NO</th><th>MALZEME / MATERIAL</th><th>BİRİM</th><th>MİKTAR</th></tr><tr><td>1</td><td>Otomatik sigorta 2×16 A C eğrisi · 6 kA</td><td>adet</td><td>10</td></tr><tr><td>2</td><td>Otomatik sigorta 2×10 A B eğrisi · 6 kA</td><td>adet</td><td>5</td></tr><tr><td>3</td><td>Otomatik sigorta 1×16 A C eğrisi · 6 kA</td><td>adet</td><td>4</td></tr><tr><td>4</td><td>Kaçak akım rölesi 4×40 A / 30 mA, A tipi</td><td>adet</td><td>4</td></tr><tr><td>5</td><td>Otomatik sigorta 2×10 A C eğrisi · 6 kA</td><td>adet</td><td>2</td></tr><tr><td>6</td><td>Otomatik sigorta 2×20 A C eğrisi · 6 kA</td><td>adet</td><td>2</td></tr><tr><td>7</td><td>Otomatik sigorta 2×6 A C eğrisi · 6 kA</td><td>adet</td><td>2</td></tr><tr><td>8</td><td>Kaçak akım rölesi 2×40 A / 30 mA, A tipi</td><td>adet</td><td>2</td></tr><tr><td>9</td><td>Otomatik sigorta 2×6 A B eğrisi · 6 kA</td><td>adet</td><td>1</td></tr><tr><td>10</td><td>Ana şalter 4×32 A yük ayırıcı</td><td>adet</td><td>1</td></tr><tr><td>11</td><td>Ana kaçak akım rölesi 4×40 A / 300 mA S tipi</td><td>adet</td><td>1</td></tr><tr><td>12</td><td>Parafudr Tip 2 · Up 1,4 kV · In 20 kA (3F+N)</td><td>adet</td><td>1</td></tr><tr><td>13</td><td>Pano gövdesi 800×1000×250 mm IP54 Form 2b</td><td>adet</td><td>1</td></tr><tr><td>14</td><td>Bakır bara seti 3F+N+PE</td><td>adet</td><td>1</td></tr><tr><td>15</td><td>Klemens sırası -X1 (vidalı, 4 mm²)</td><td>adet</td><td>66</td></tr><tr><td>16</td><td>Etiket seti (PVC, Türkçe, vidalı)</td><td>adet</td><td>1</td></tr></table>								S.NO	MALZEME / MATERIAL	BİRİM	MİKTAR	1	Otomatik sigorta 2×16 A C eğrisi · 6 kA	adet	10	2	Otomatik sigorta 2×10 A B eğrisi · 6 kA	adet	5	3	Otomatik sigorta 1×16 A C eğrisi · 6 kA	adet	4	4	Kaçak akım rölesi 4×40 A / 30 mA, A tipi	adet	4	5	Otomatik sigorta 2×10 A C eğrisi · 6 kA	adet	2	6	Otomatik sigorta 2×20 A C eğrisi · 6 kA	adet	2	7	Otomatik sigorta 2×6 A C eğrisi · 6 kA	adet	2	8	Kaçak akım rölesi 2×40 A / 30 mA, A tipi	adet	2	9	Otomatik sigorta 2×6 A B eğrisi · 6 kA	adet	1	10	Ana şalter 4×32 A yük ayırıcı	adet	1	11	Ana kaçak akım rölesi 4×40 A / 300 mA S tipi	adet	1	12	Parafudr Tip 2 · Up 1,4 kV · In 20 kA (3F+N)	adet	1	13	Pano gövdesi 800×1000×250 mm IP54 Form 2b	adet	1	14	Bakır bara seti 3F+N+PE	adet	1	15	Klemens sırası -X1 (vidalı, 4 mm²)	adet	66	16	Etiket seti (PVC, Türkçe, vidalı)	adet	1	A
S.NO									MALZEME / MATERIAL	BİRİM	MİKTAR	
1									Otomatik sigorta 2×16 A C eğrisi · 6 kA	adet	10	
2									Otomatik sigorta 2×10 A B eğrisi · 6 kA	adet	5	
3									Otomatik sigorta 1×16 A C eğrisi · 6 kA	adet	4	
4									Kaçak akım rölesi 4×40 A / 30 mA, A tipi	adet	4	
5									Otomatik sigorta 2×10 A C eğrisi · 6 kA	adet	2	
6									Otomatik sigorta 2×20 A C eğrisi · 6 kA	adet	2	
7									Otomatik sigorta 2×6 A C eğrisi · 6 kA	adet	2	
8									Kaçak akım rölesi 2×40 A / 30 mA, A tipi	adet	2	
9									Otomatik sigorta 2×6 A B eğrisi · 6 kA	adet	1	
10									Ana şalter 4×32 A yük ayırıcı	adet	1	
11									Ana kaçak akım rölesi 4×40 A / 300 mA S tipi	adet	1	
12									Parafudr Tip 2 · Up 1,4 kV · In 20 kA (3F+N)	adet	1	
13									Pano gövdesi 800×1000×250 mm IP54 Form 2b	adet	1	
14									Bakır bara seti 3F+N+PE	adet	1	
15	Klemens sırası -X1 (vidalı, 4 mm²)	adet	66	
16	Etiket seti (PVC, Türkçe, vidalı)	adet	1	
B	B	
C	C	
D	D	
E	E	
F	F	
Drawn By / Çizen		CC	Customer Name / Müşteri Adı		ÖZEL — MALTEPE / İDEALTEPE		Project Number / Proje Numarası	GYM-25-001-001	Sheet: / Sayfa	12	
Checked By / Kontrol Eden		—	Project Description / Proje Açıklaması		MOBİLYA MAĞAZASI → FONKSİYONEL ANTRENMAN STÜDYOSU				Next sheet: / Sonraki	—	
Approved By / Onaylayan		—	Panel Name / Pano Adı		ADP		Revision / Revizyon	Rev H	Total sheets: / Toplam	12	
Project Date / Proje Tarihi		17 Eylül 2026		Page Description / Sayfa Açıklaması		Parts List / Malzeme Listesi		Standards / Standartlar	IEC 61439-1&2 · IEC 60617	Sheet size / Kâğıt	A3	