

Customer Name / Müşteri Adı	
Project Description / Proje Açıklaması	
Project Number / Proje Numarası	Y-24-003-001
Panel Name / Pano Adı	ADP

Created By / Çizen		Creation Date / Çizim Tarihi	4.03.2025
Responsible For Project / Proje Sorumlusu		Revision Date / Revizyon Tarihi	10.03.2025
Location / Konum			





	0	1	2	3	4	5	6	7
A	STANDARDS STANDARTLAR		POWER SUPPLY GÜÇ KAYNAĞI		APPARATUS CİHAZ		DEGREE OF PROTECTION KORUMA DERECEŚİ	
B	TYPE TESTED ASSEMBLIES TİP TESTLER IEC 61439-1&2, VDE 0660, DIN 41-488 BS 5486, EN 439-1		RATED SERVICE VOLTAGE _____ : 400V ANMA GERİLİMİ RATED CURRENT _____ : 630A ANMA AKIMI RATED SHORT TIME WITHSTAND CURRENT _____ : 36 kA ANMA KISA DEVRE DAYANIM AKIMI		MOUNTING MONTAJ ☒ FIXED SABİT ☐ DRAW OUT ÇEKMECELİ ☐ PLUG-IN SOKETLİ OPERATION İŞLEM ☐ BEHIND DOOR KAPI ARKASI ☐ THROUGH DOOR KAPI İLE ☒ FRONT PLATE+DOOR ÖN PLAKA+KAPI		PROTECTION KORUMA ☒ IP 30 ☐ IP 41 ☐ IP 43 ☐ IP 54 ☐ IP65 SEGREGATION BÖLÜMLEME ☒ FORM 1 ☐ FORM 2a ☐ FORM 3a ☐ FORM 4 type 2 ☐ PARTITIONING ☐ FORM 2b ☐ FORM 3b ☐ FORM 4b	
	GENERAL CHARACTERISTICS GENEL ÖZELLİKLER		NEUTRAL OPERATION NÖTR OPERASYONU ☐ IT ☐ TT ☐ TN-C ☒ TN-S		CONNECTIONS BAĞLANTILAR		CIRCUIT MARKING DEVRE MARKALAMA	
C	NUMBER OF PHASES _____ : 3 FAZ SAYISI RATED INSULATION VOLTAGE _____ : 690V ANMA İZOLASYON GERİLİMİ RATED INS. VOLTAGE FOR MAIN BUSBARS _____ : 1000V ANA BARA İZOLASYON GERİLİMİ RATED FREQUENCY _____ : 50 Hz ANMA FREKANS DIELECTRICAL WITHSTAND VOLTAGE _____ : 1.89kV / 1s DIELEKTRİK DAYANMA GERİLİMİ OVERVOLTAGE CATEGORY _____ : iv AŞIRI GERİLİM KATEGORİSİ RATED IMPULSE WITHSTAND VOLTAGE _____ : 6kV (FOR MAIN BUSBARS) BARA ANMA DARBE DAYANIM GERİLİMİ		BUSBARS BARALAR		TYPE OF CONNECTION BAĞLANTI TİPİ		LABELS ETİKETLEME	
	CLIMATIC CONDITION İKLİM DURUMU		MATERIAL MALZEME COATING KAPLAMA NEUTRAL NÖTR EARTHING TOPRAKLAMA MAIN BUSBARS (L1-L2-L3) : 630A ANA BARA(L1-L2-L3) NEUTRAL BUSBARS (N) : 630A NOTR BARASI(N)		INCOMING GİRİŞ OUTGOING ÇIKIŞ		MOUNTING TYPE MONTAJ TİPİ	
D	AMBIENT TEMPERATURE ☐ 35° ☒ 40° ORTAM SICAKLIĞI INSTALLATION MONTAJ ATMOSPHERE ATMOSFER TEMPERATURE DAILY AVERAGE GÜNLÜK ORTALAMA SICAKLIK MAX. OBSERVED TEMPERATURE GÜNLÜK MAKSİMUM SICAKLIK HUMIDITY NEM		SUPPLY OF AUXILIARIES YARDIMCI AKSESURLAR KAYNAĞI		ACCESS ERİŞİM		COLOR RENK	
	AUXILIARY WIRING KABLO YARDIMCI		VOLTAGE GERİLİM CONTROL _____ : 24VDC KONTROL _____ : 24VAC 230VAC ORIGIN KÖKEN ☐ FROM BUSBAR BARADAN ☐ AUX. TRANSFORMER YARDIMCI TRAFO ☐ EXTERNAL HARİCİ		ENTRY GİRİŞ ☐ TOP ÜST ☒ BOTTOM ALT		LANGUAGE	
E	CONTROL AND SIGNALLING KONTROL VE SİNYALİZASYON		LANGUAGE OF DRAWINGS ÇİZİM DİLİ		PARTICULAR NOTES BELİRLENEN NOTLAR		ADDITIONAL REQUESTS EK İSTEKLERİ	
	SECONDARY VOLTAGE SEKONDER VOLTAGE		PACKING TYPE PAKETLEME TİPİ				HEATER ISITICI LIGHTING AYDINLATMA VENTILATION FAN FAN EARTHQUAKE OPTION DEPREM SEÇENEĞİ SUPPLEMENTARY PLINTH EK FIRÇA	
F	CURRENT AKIM		LANGUAGE OF DRAWINGS ÇİZİM DİLİ					
	ENCLOSURES PANO ÖZELLİĞİ		LANGUAGE OF DRAWINGS ÇİZİM DİLİ					
	TYPE TİP ☒ LOCAL ☐ ☐ ☐ ☐		COLOR PAINTING BOYA RENGİ ☐ RAL 9006 ☒ RAL 7035 ☐ RAL 7032 ☐ RAL.....					
			WOODEN CAGE KAPALI KASA FULLY ENCLOSED WOODEN TAM KAPALI KASA OVERSEAS DENİZ AŞIRI					







Drawn By / Çizen		Customer Name / Müşteri Adı		Project Number / Proje Numarası	Y-24-003-001	Sheet:	2
Checked By / Kontrol Eden		Project Description / Proje Açıklaması				Next sheet:	3
Approved By / Onaylayan		Panel Name / Pano Adı	ADP			Total sheets:	34
Project Date / Proje Tarihi	4.03.2025	Page Description / Sayfa Açıklaması	Panel Characteristics Table				

Symbol List / Sembol Listesi


MISCELLANEOUS COMPONENTS / MUHTELİF BİLEŞENLER	IEC SYMBOL / SEMBOLLER	DESCRIPTION / AÇIKLAMA
		COIL / BOBIN
		RESISTOR / DİRENÇ
		AMMETER / AMPERMETRE
		VOLTMETER / VOLTMETRE
		WATTMETER / VATMETRE
		FREQUENCY-METER / FREKANS METRE
		POWER-FACTOR METER GÜÇ-FAKTÖR METRE
		THERMOSTAT / TERMOSTAT
		INDICATOR / SİNYAL

CONTACTS / KONTAKLAR	IEC SYMBOL / SEMBOLLER	DESCRIPTION / AÇIKLAMA
		CONTACT N/O / AÇIK KONTAK
		CONTACT N/C / KAPALI KONTAK
		INSTANTANEOUS CONTACT / ENVERSÖR KONTAK
		PUSH BUTTON N/O / AÇIK KONTAKLI BUTON
		PUSH BUTTON N/C / KAPALI KONTAKLI BUTON
		SELLECTOR SWITCH / SELEKTÖR ANAHTARI
		THERFAL FAULT CONTACT N/O / AÇIK TERMİK HATA KONTAĞI
		THERFAL FAULT CONTACT N/C / KAPALI TERMİK HATA KONTAĞI
		FUSE CARRIER / SIGORTA TAŞIYICISI

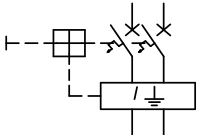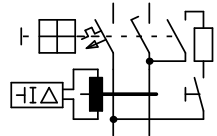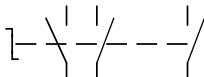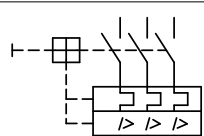
SWITCHING DEVICES / ANAHTARLAMA CİHAZLARI	IEC SYMBOL / SEMBOLLER	DESCRIPTION / AÇIKLAMA
		SWITCH / ANAHTAR
		CIRCUIT BREAKER / DEVRE KESİCİ
		RESIDUAL CURRENT SWITCH / KAÇAK AKIM ANAHTARI
		RESUDIAL CURRENT CIRCUIT BREAKER / KAÇAK AKIM DEVRE KESİCİ
		1-0-2 SELECTOR SWITCH / 1-0-2 SEÇİCİ ANAHTARI
		TROID RELAY / TOROID RÖLESİ
		CONTACTOR / KONTAKTÖR
		THERMAL RELAY / TERMİK RÖLE
		MAGNETIC THERMAL CIRCUIT BREAKER / TERMİK MANYETİK DEVRE KESİCİ

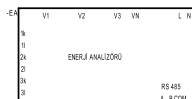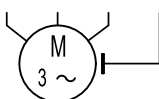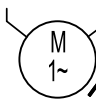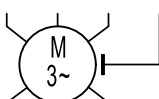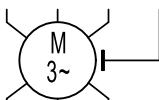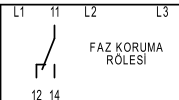SWITCHING DEVICES & MOTORS / ANAHTARLAMA VE MOTORLAR	IEC SYMBOL / SEMBOLLER	DESCRIPTION / AÇIKLAMA
		FAN
		LIGHTING / AYDINLATMA
		ENERGY ANALYZER / ENERJİ ANALİZÖRÜ
		CURRENT TRANSFORMER / MEVCUT TRANSFORMATÖR
		3 PHASE AC MOTOR / 3 FAZLI AC MOTOR
		1 PHASE AC MOTOR / 1 FAZLI AC MOTOR
		2 SPEED 3 PHASE AC MOTOR / 2 HIZLI 3 FAZLI AC MOTOR
		STAR DELTA 3 PHASE AC MOTOR / YILDIZ ÜÇGEN 3 FAZLI AC MOTOR
		PHASE PROTECTION RELAY / FAZ KORUMA RÖLESİ


0		1		2		3		4		5		6		7			
A															A		
B															B		
C															C		
D															D		
E															E		
F															F		
Drawn By / Çizen		Customer Name / Müşteri Adı									Project Number / Proje Numarası	Y-24-003-001				Sheet:	4
Checked By / Kontrol Eden		Project Description / Proje Açıklaması													Next sheet:	1	
Approved By / Onaylayan		Panel Name / Pano Adı	ADP												Total sheets:	34	
Project Date / Proje Tarihi	4.03.2025	Page Description / Sayfa Açıklaması	Panel Overview														

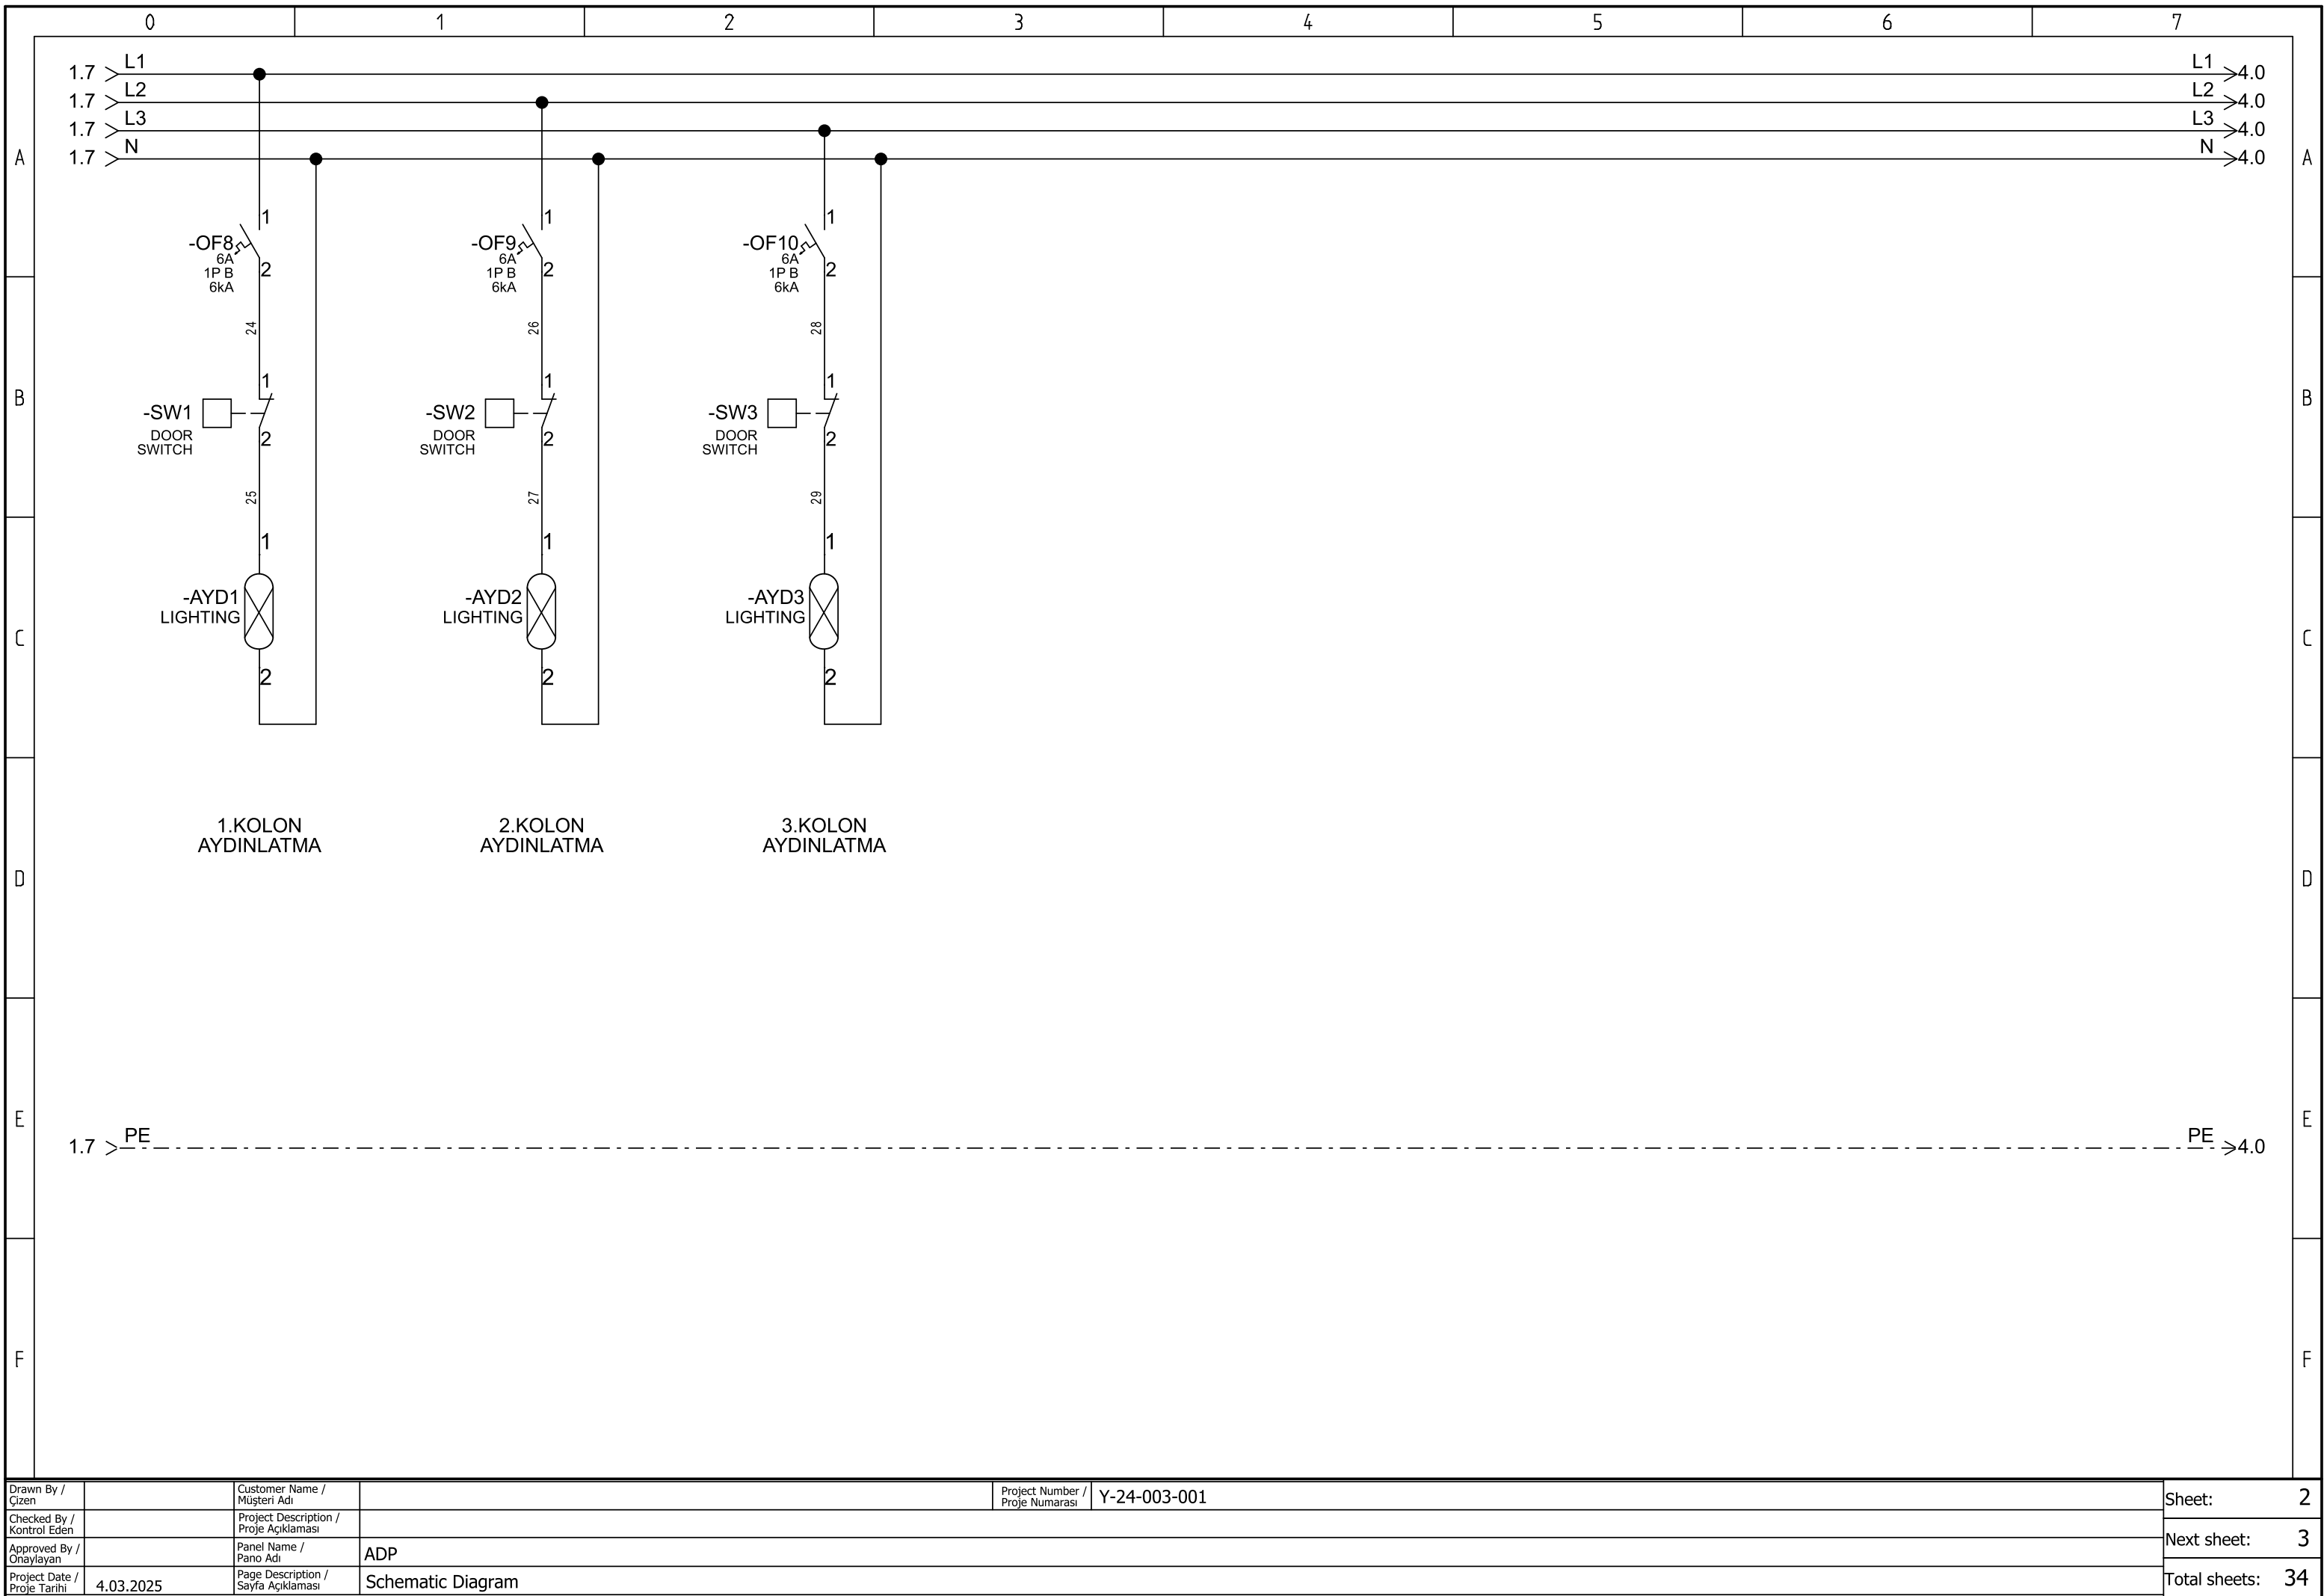


Drawn By / Çizen		Customer Name / Müşteri Adı		Project Number / Proje Numarası	Y-24-003-001	Sheet:	2
Checked By / Kontrol Eden		Project Description / Proje Açıklaması				Next sheet:	3
Approved By / Onaylayan		Panel Name / Pano Adı	ADP			Total sheets:	34
Project Date / Proje Tarihi	4.03.2025	Page Description / Sayfa Açıklaması	Schematic Diagram				

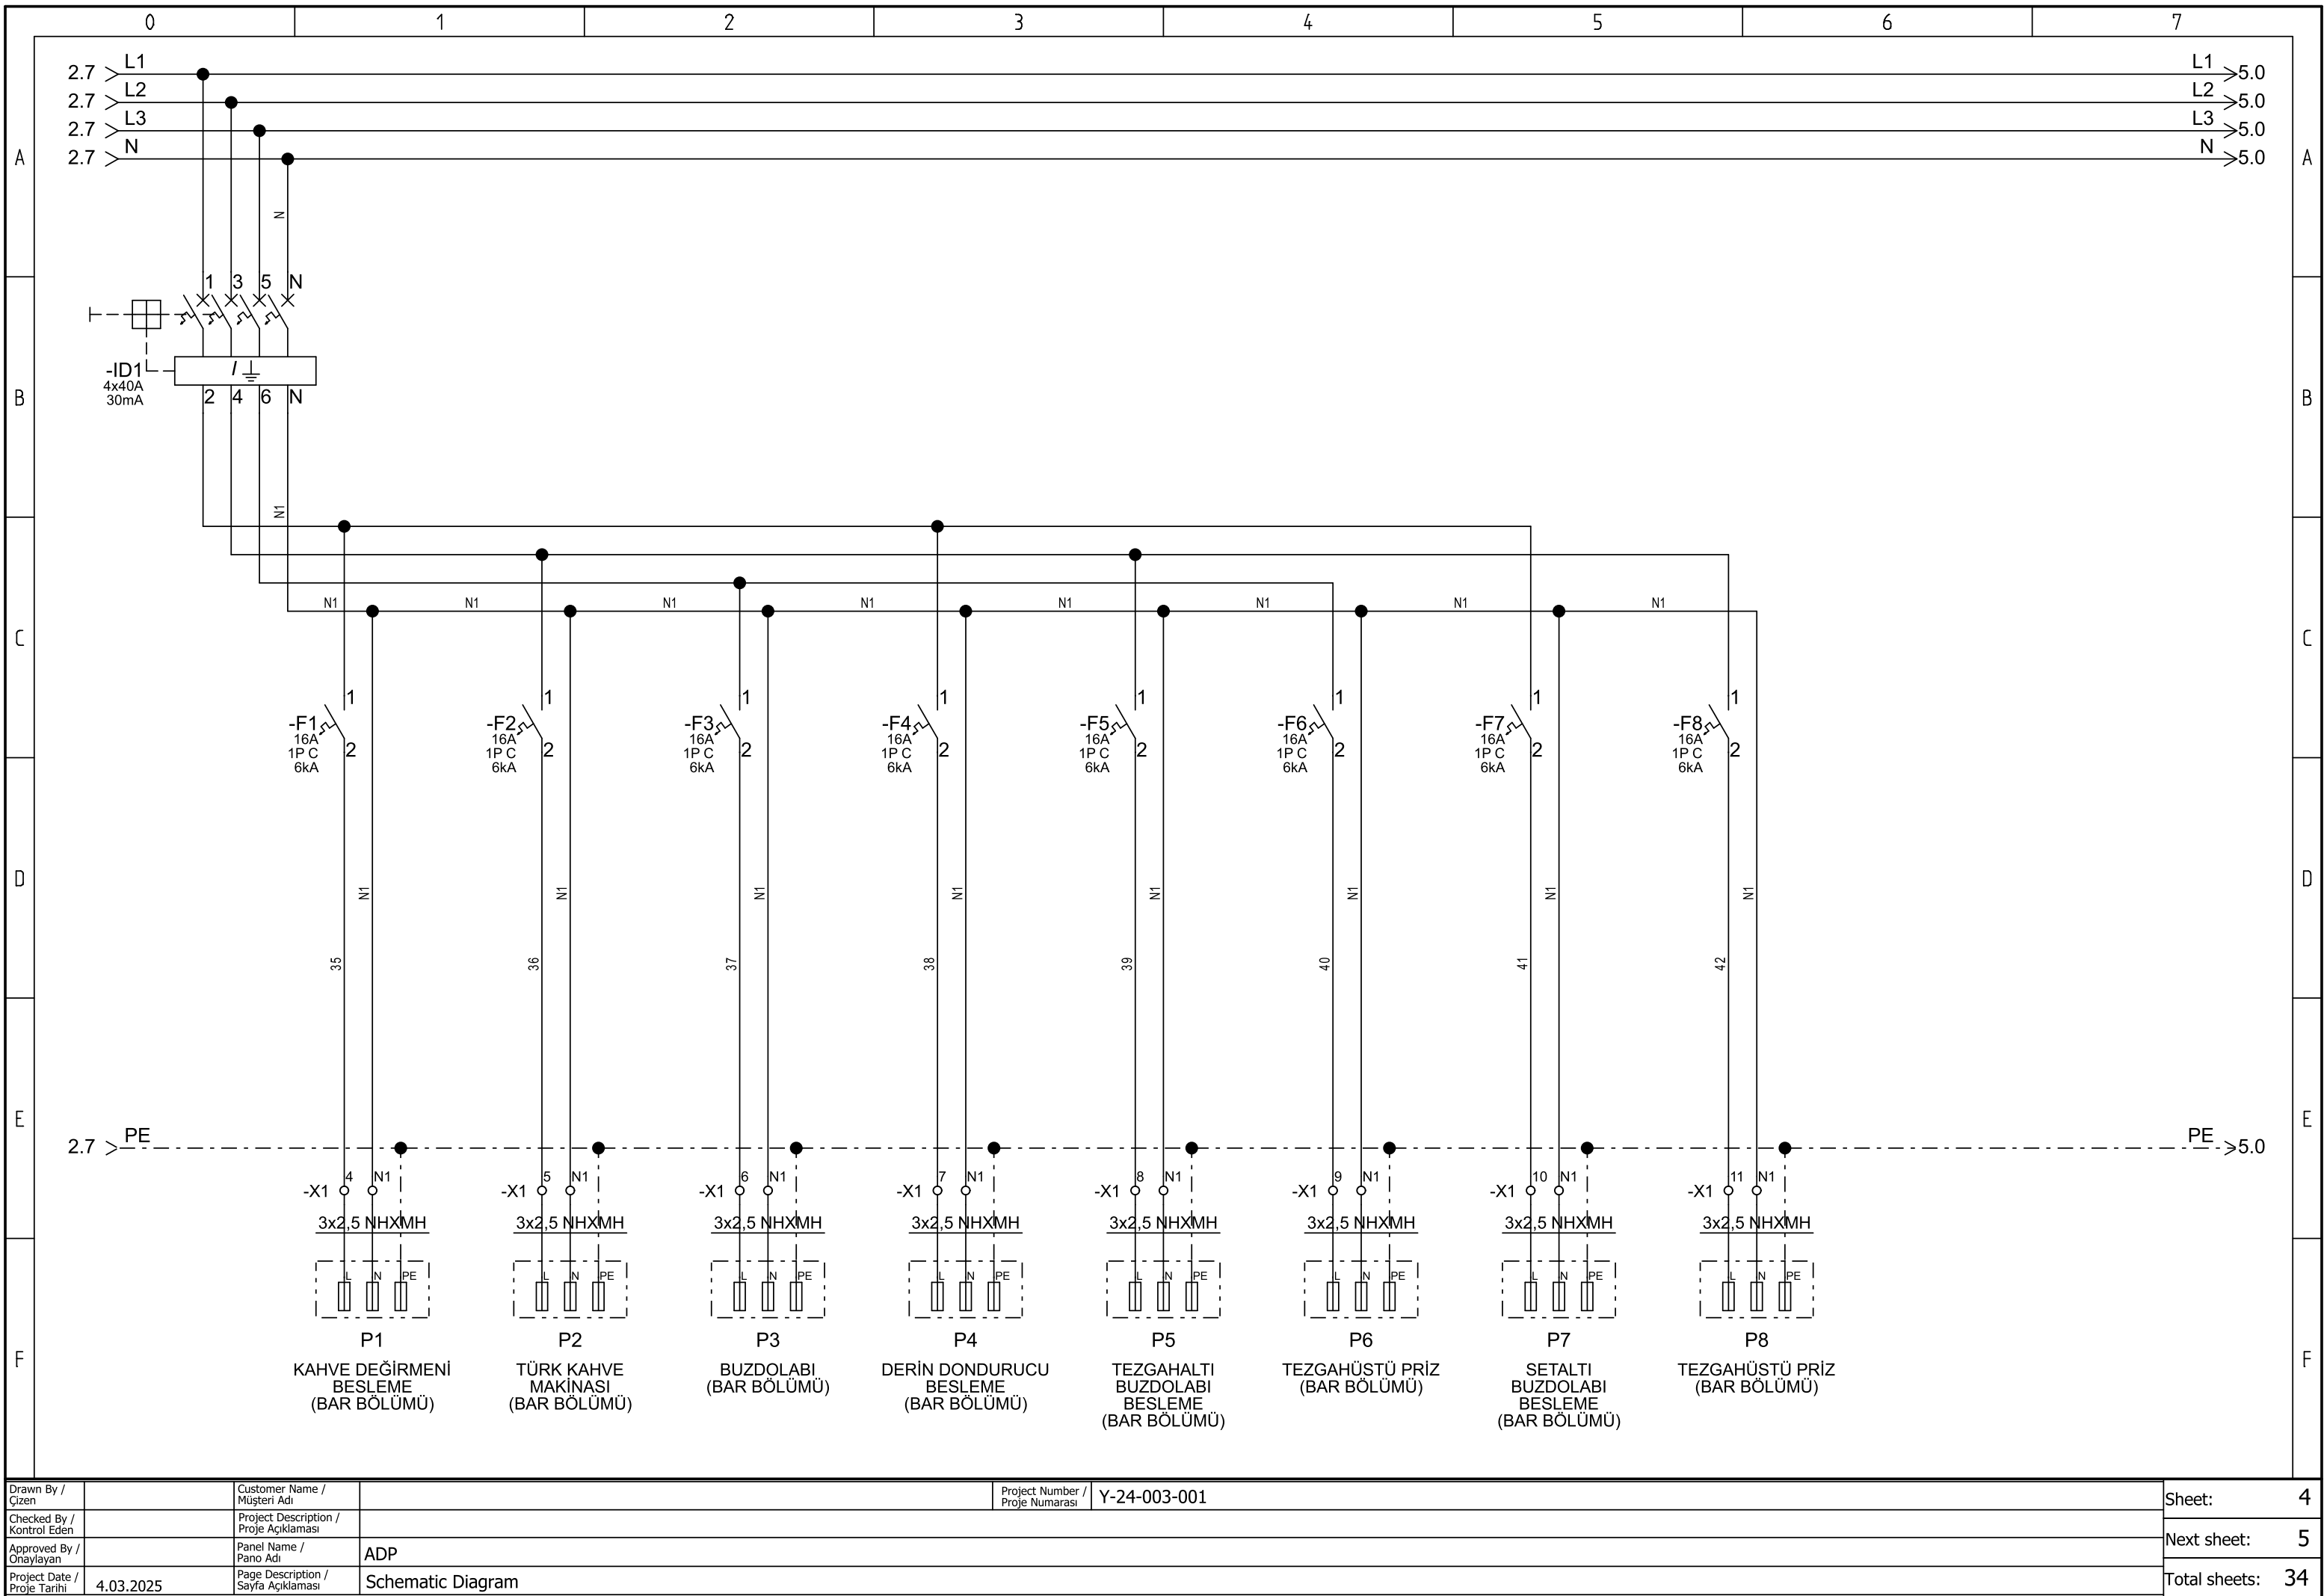


Drawn By / Çizen		Customer Name / Müşteri Adı		Project Number / Proje Numarası	Y-24-003-001	Sheet:	4
Checked By / Kontrol Eden		Project Description / Proje Açıklaması				Next sheet:	5
Approved By / Onaylayan		Panel Name / Pano Adı	ADP			Total sheets:	34
Project Date / Proje Tarihi	4.03.2025	Page Description / Sayfa Açıklaması	Schematic Diagram				

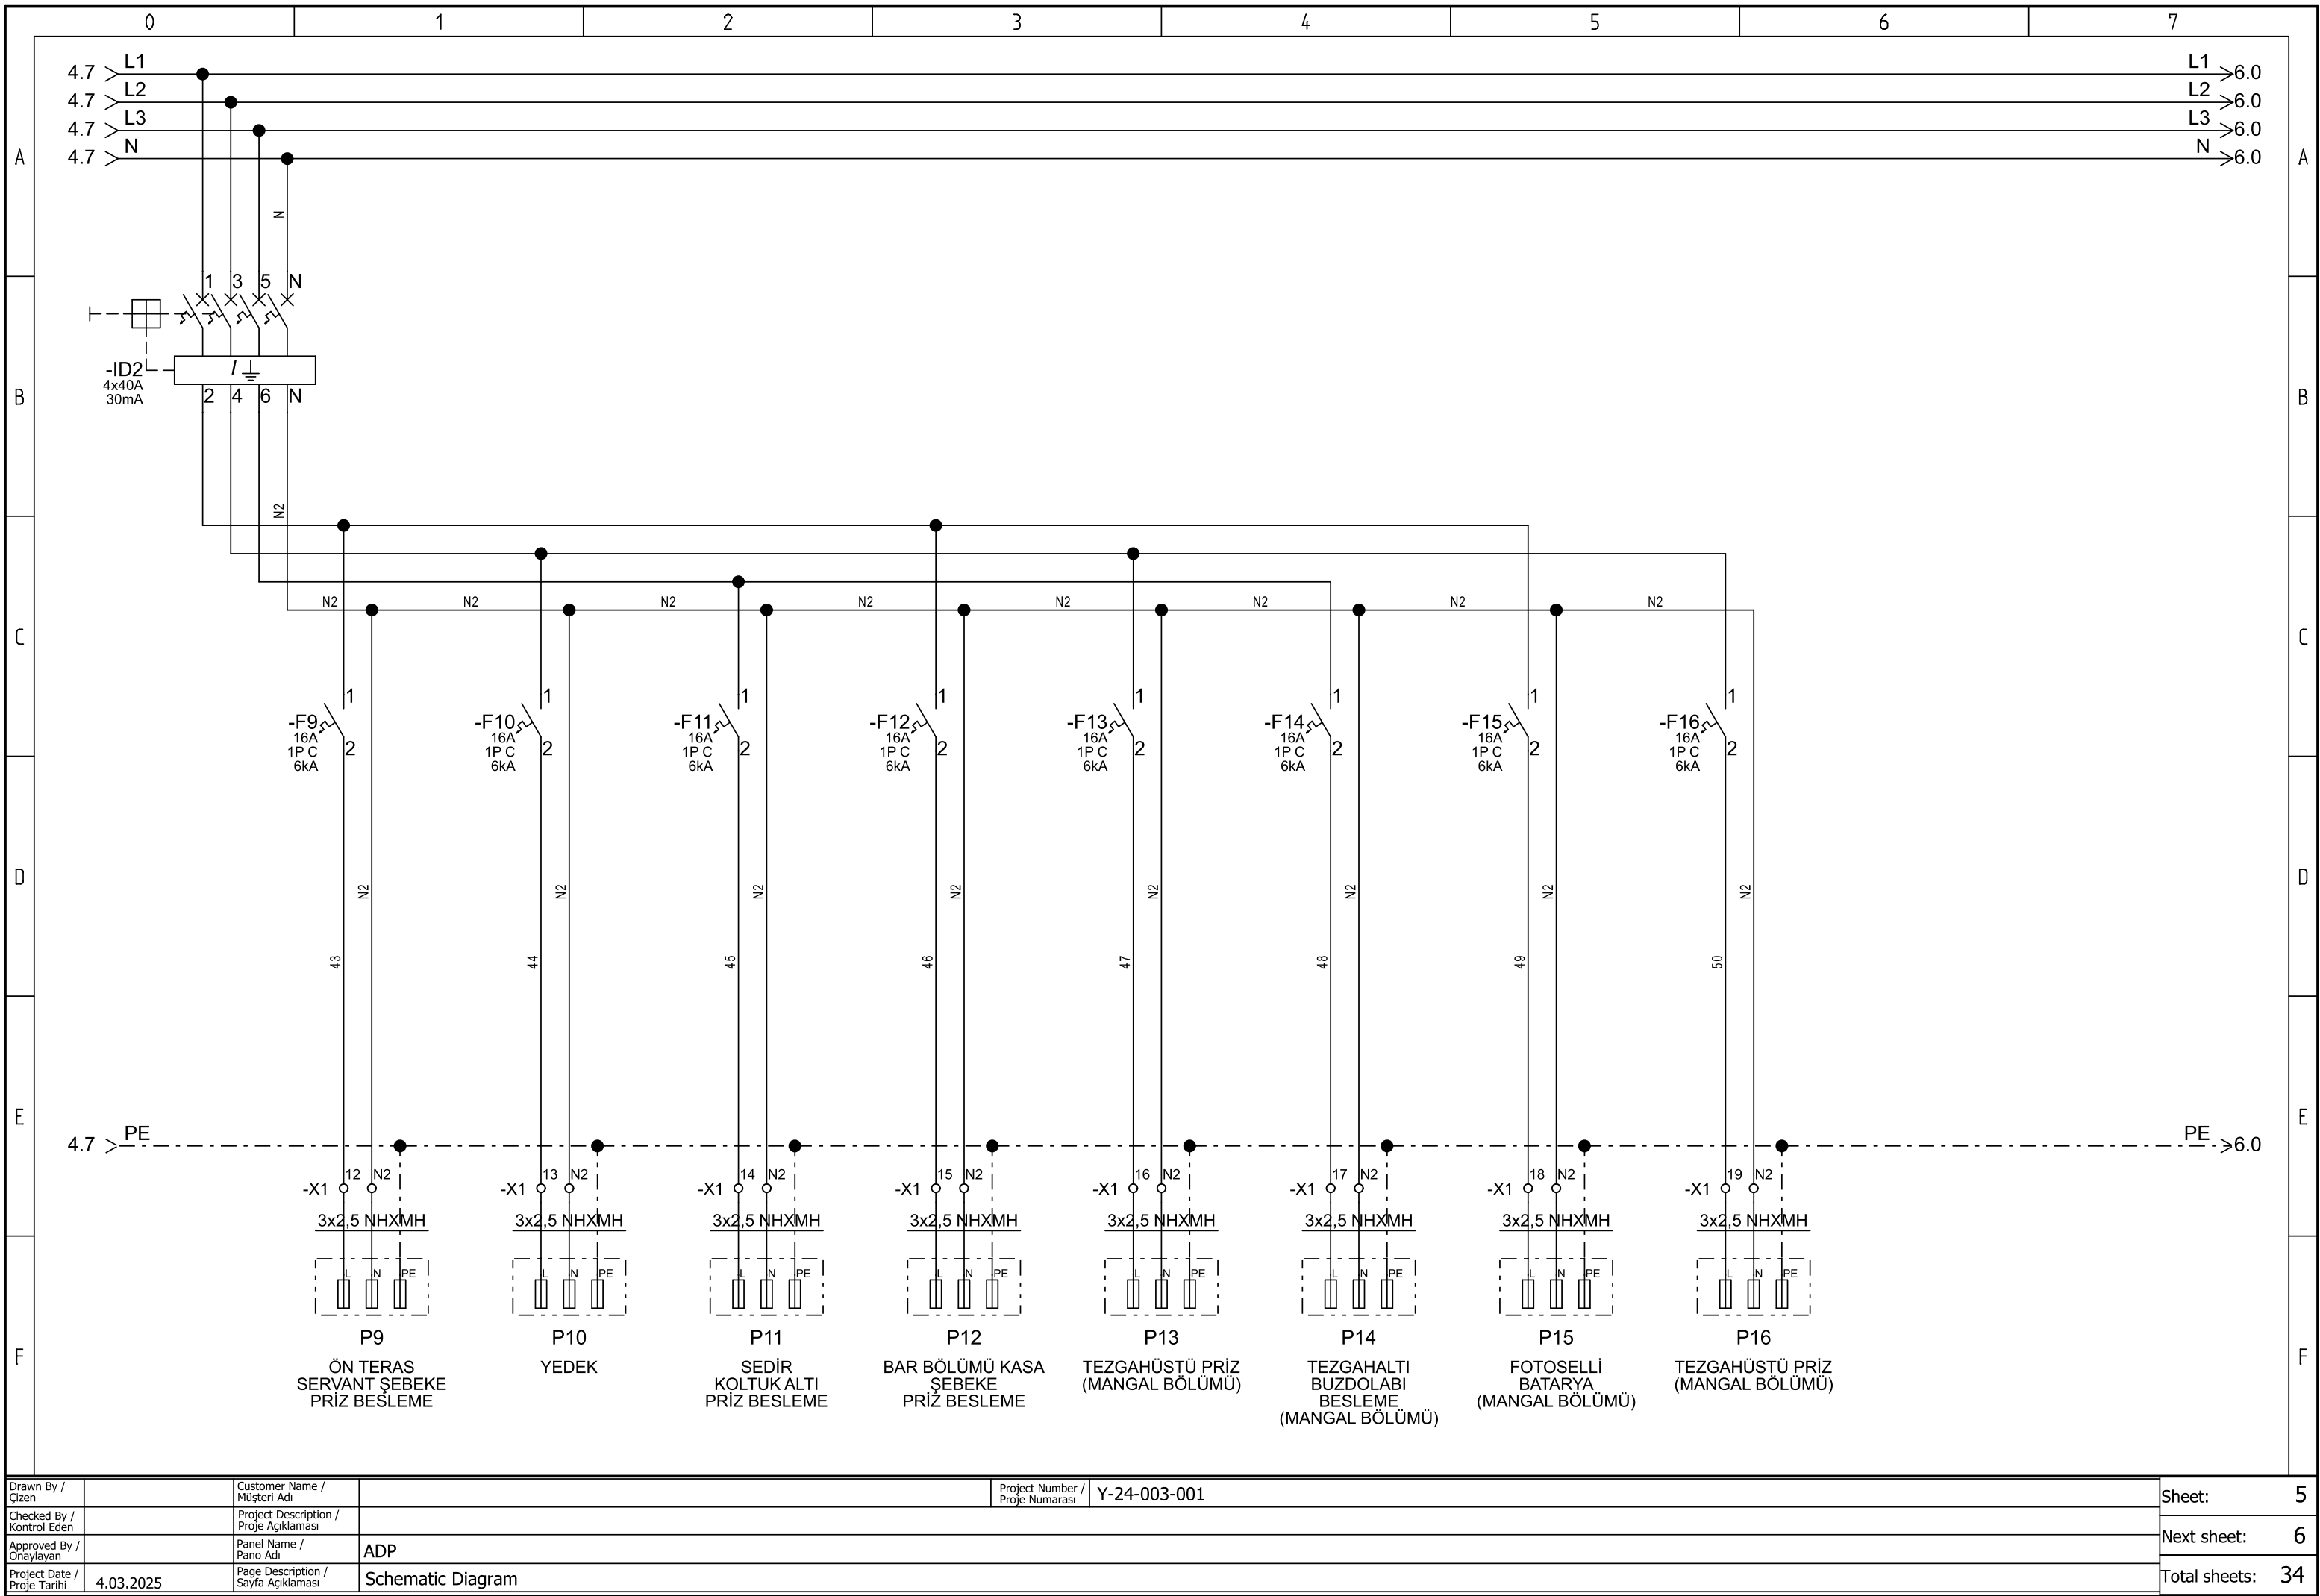


Drawn By / Çizen		Customer Name / Müşteri Adı		Project Number / Proje Numarası	Y-24-003-001	Sheet:	5
Checked By / Kontrol Eden		Project Description / Proje Açıklaması				Next sheet:	6
Approved By / Onaylayan		Panel Name / Pano Adı	ADP			Total sheets:	34
Project Date / Proje Tarihi	4.03.2025	Page Description / Sayfa Açıklaması	Schematic Diagram				

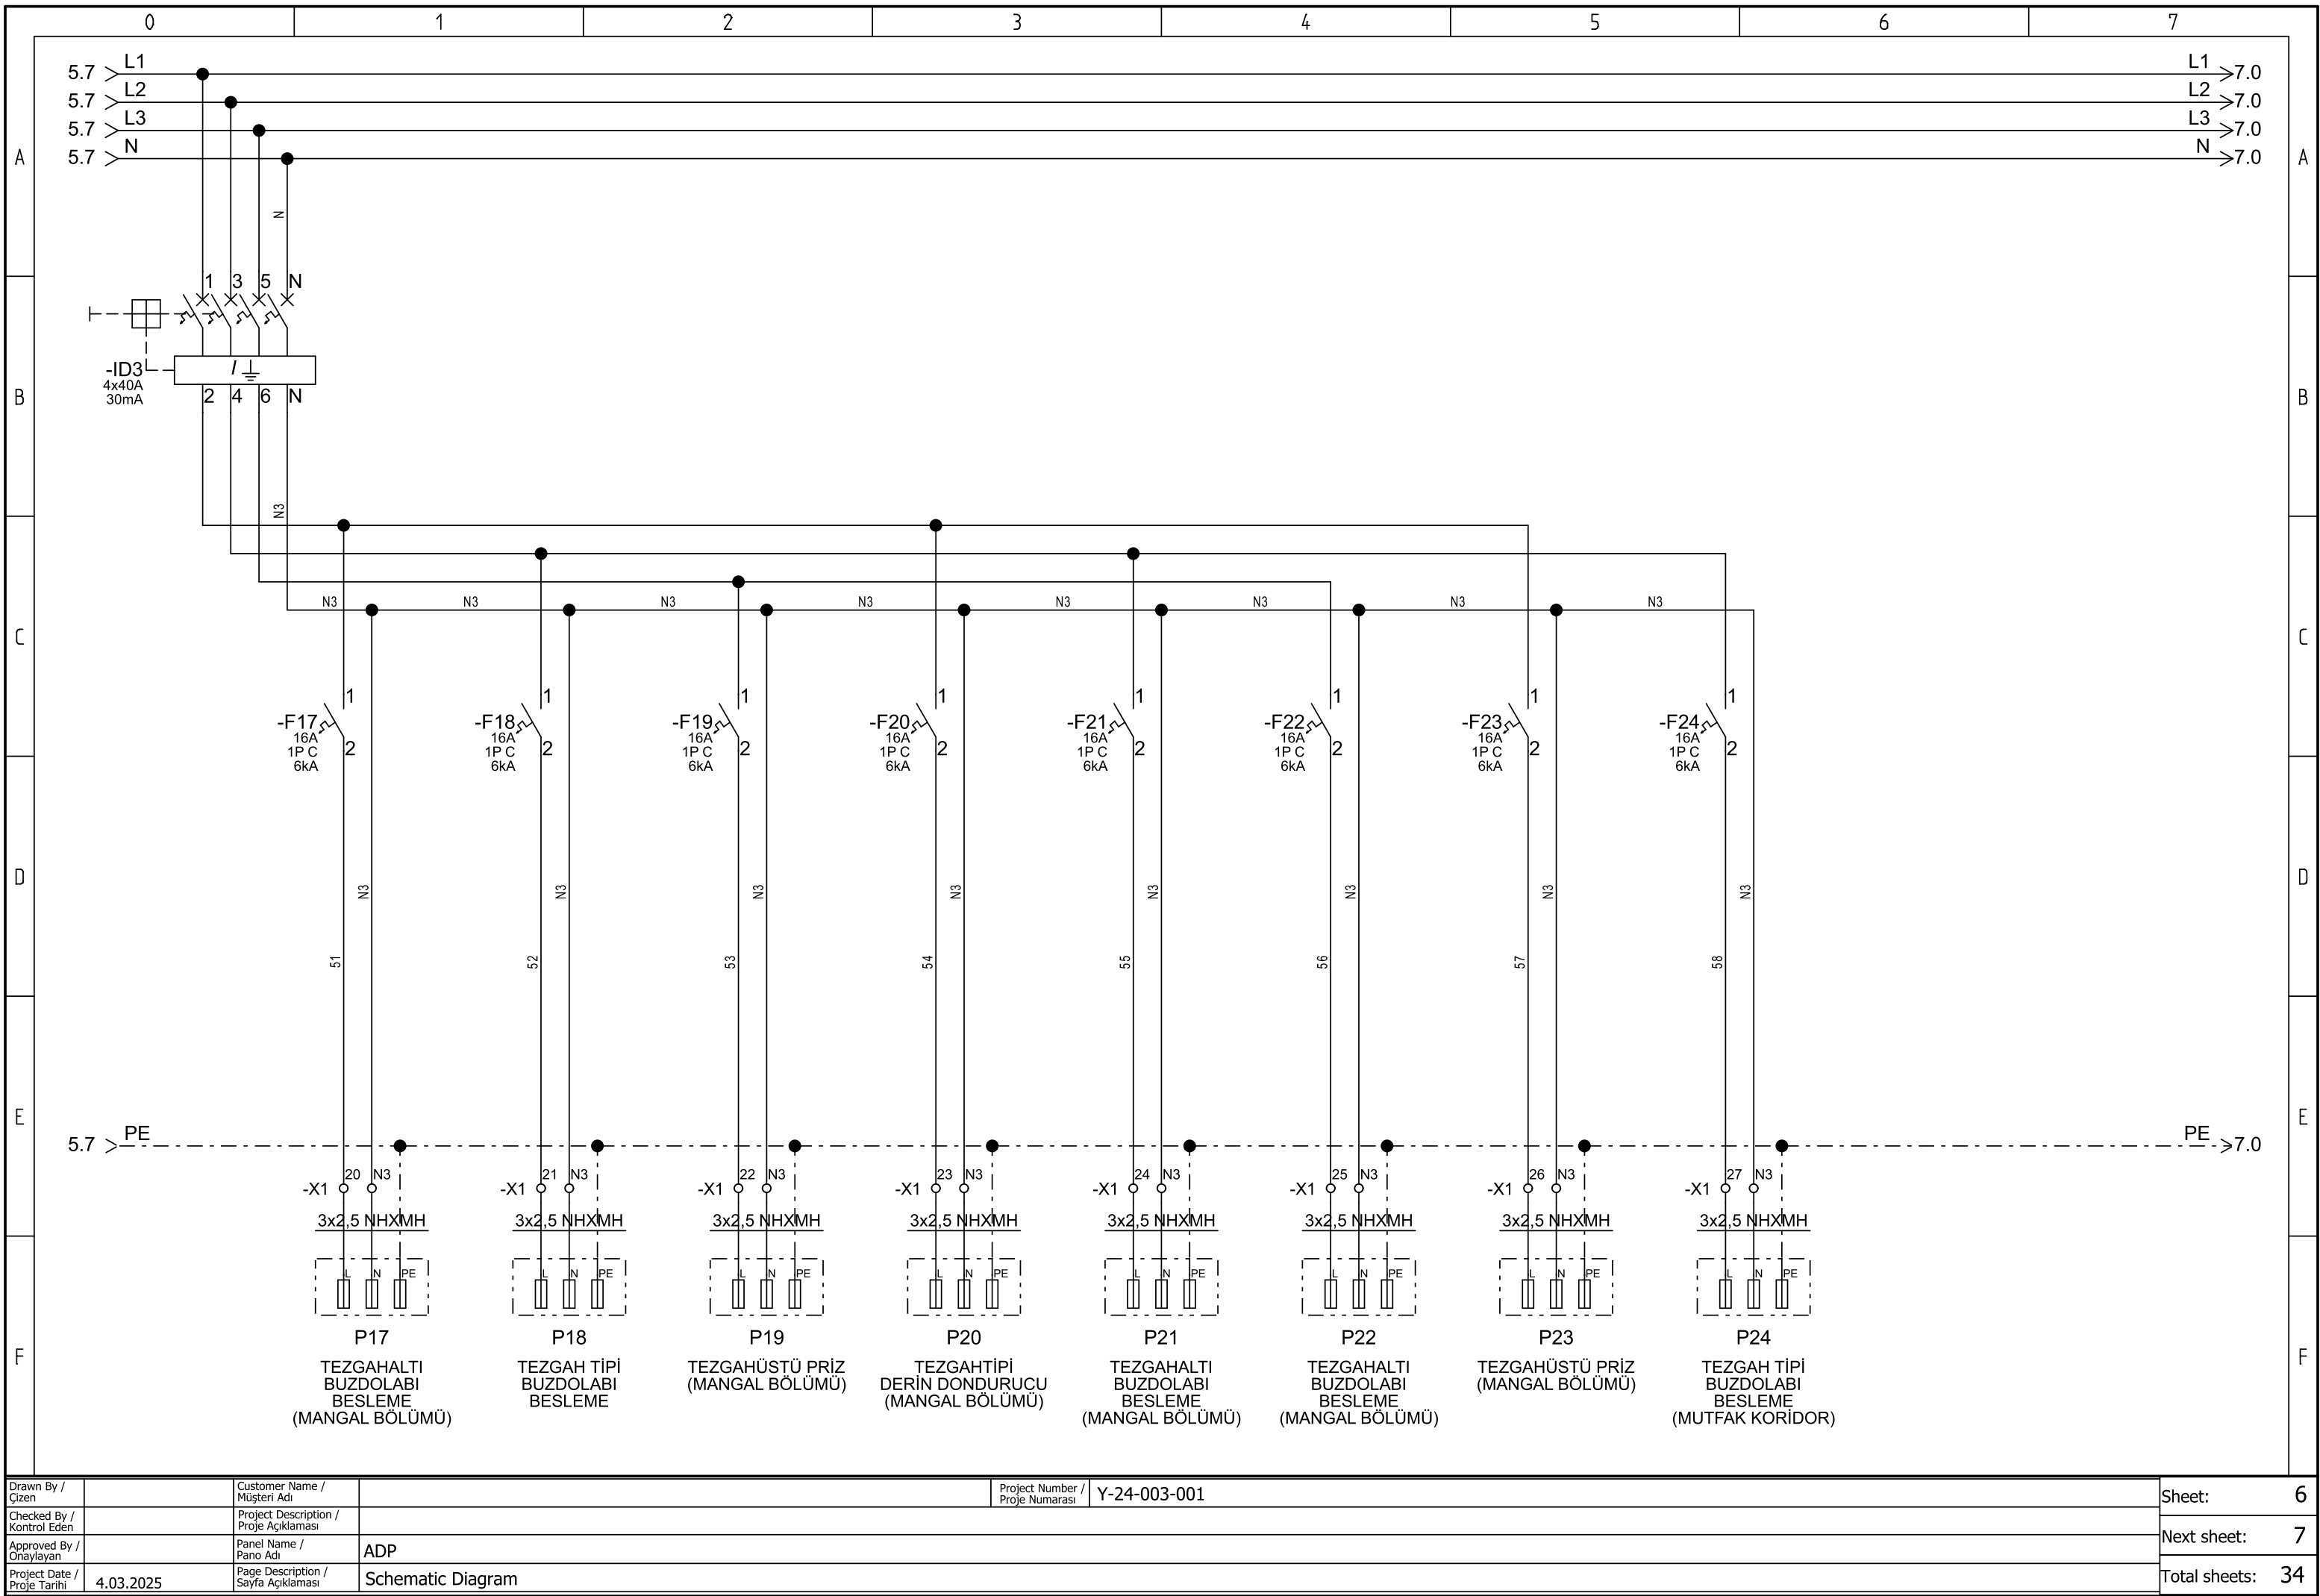


Drawn By / Çizen		Customer Name / Müşteri Adı		Project Number / Proje Numarası	Y-24-003-001	Sheet:	6
Checked By / Kontrol Eden		Project Description / Proje Açıklaması				Next sheet:	7
Approved By / Onaylayan		Panel Name / Pano Adı	ADP			Total sheets:	34
Project Date / Proje Tarihi	4.03.2025	Page Description / Sayfa Açıklaması	Schematic Diagram				

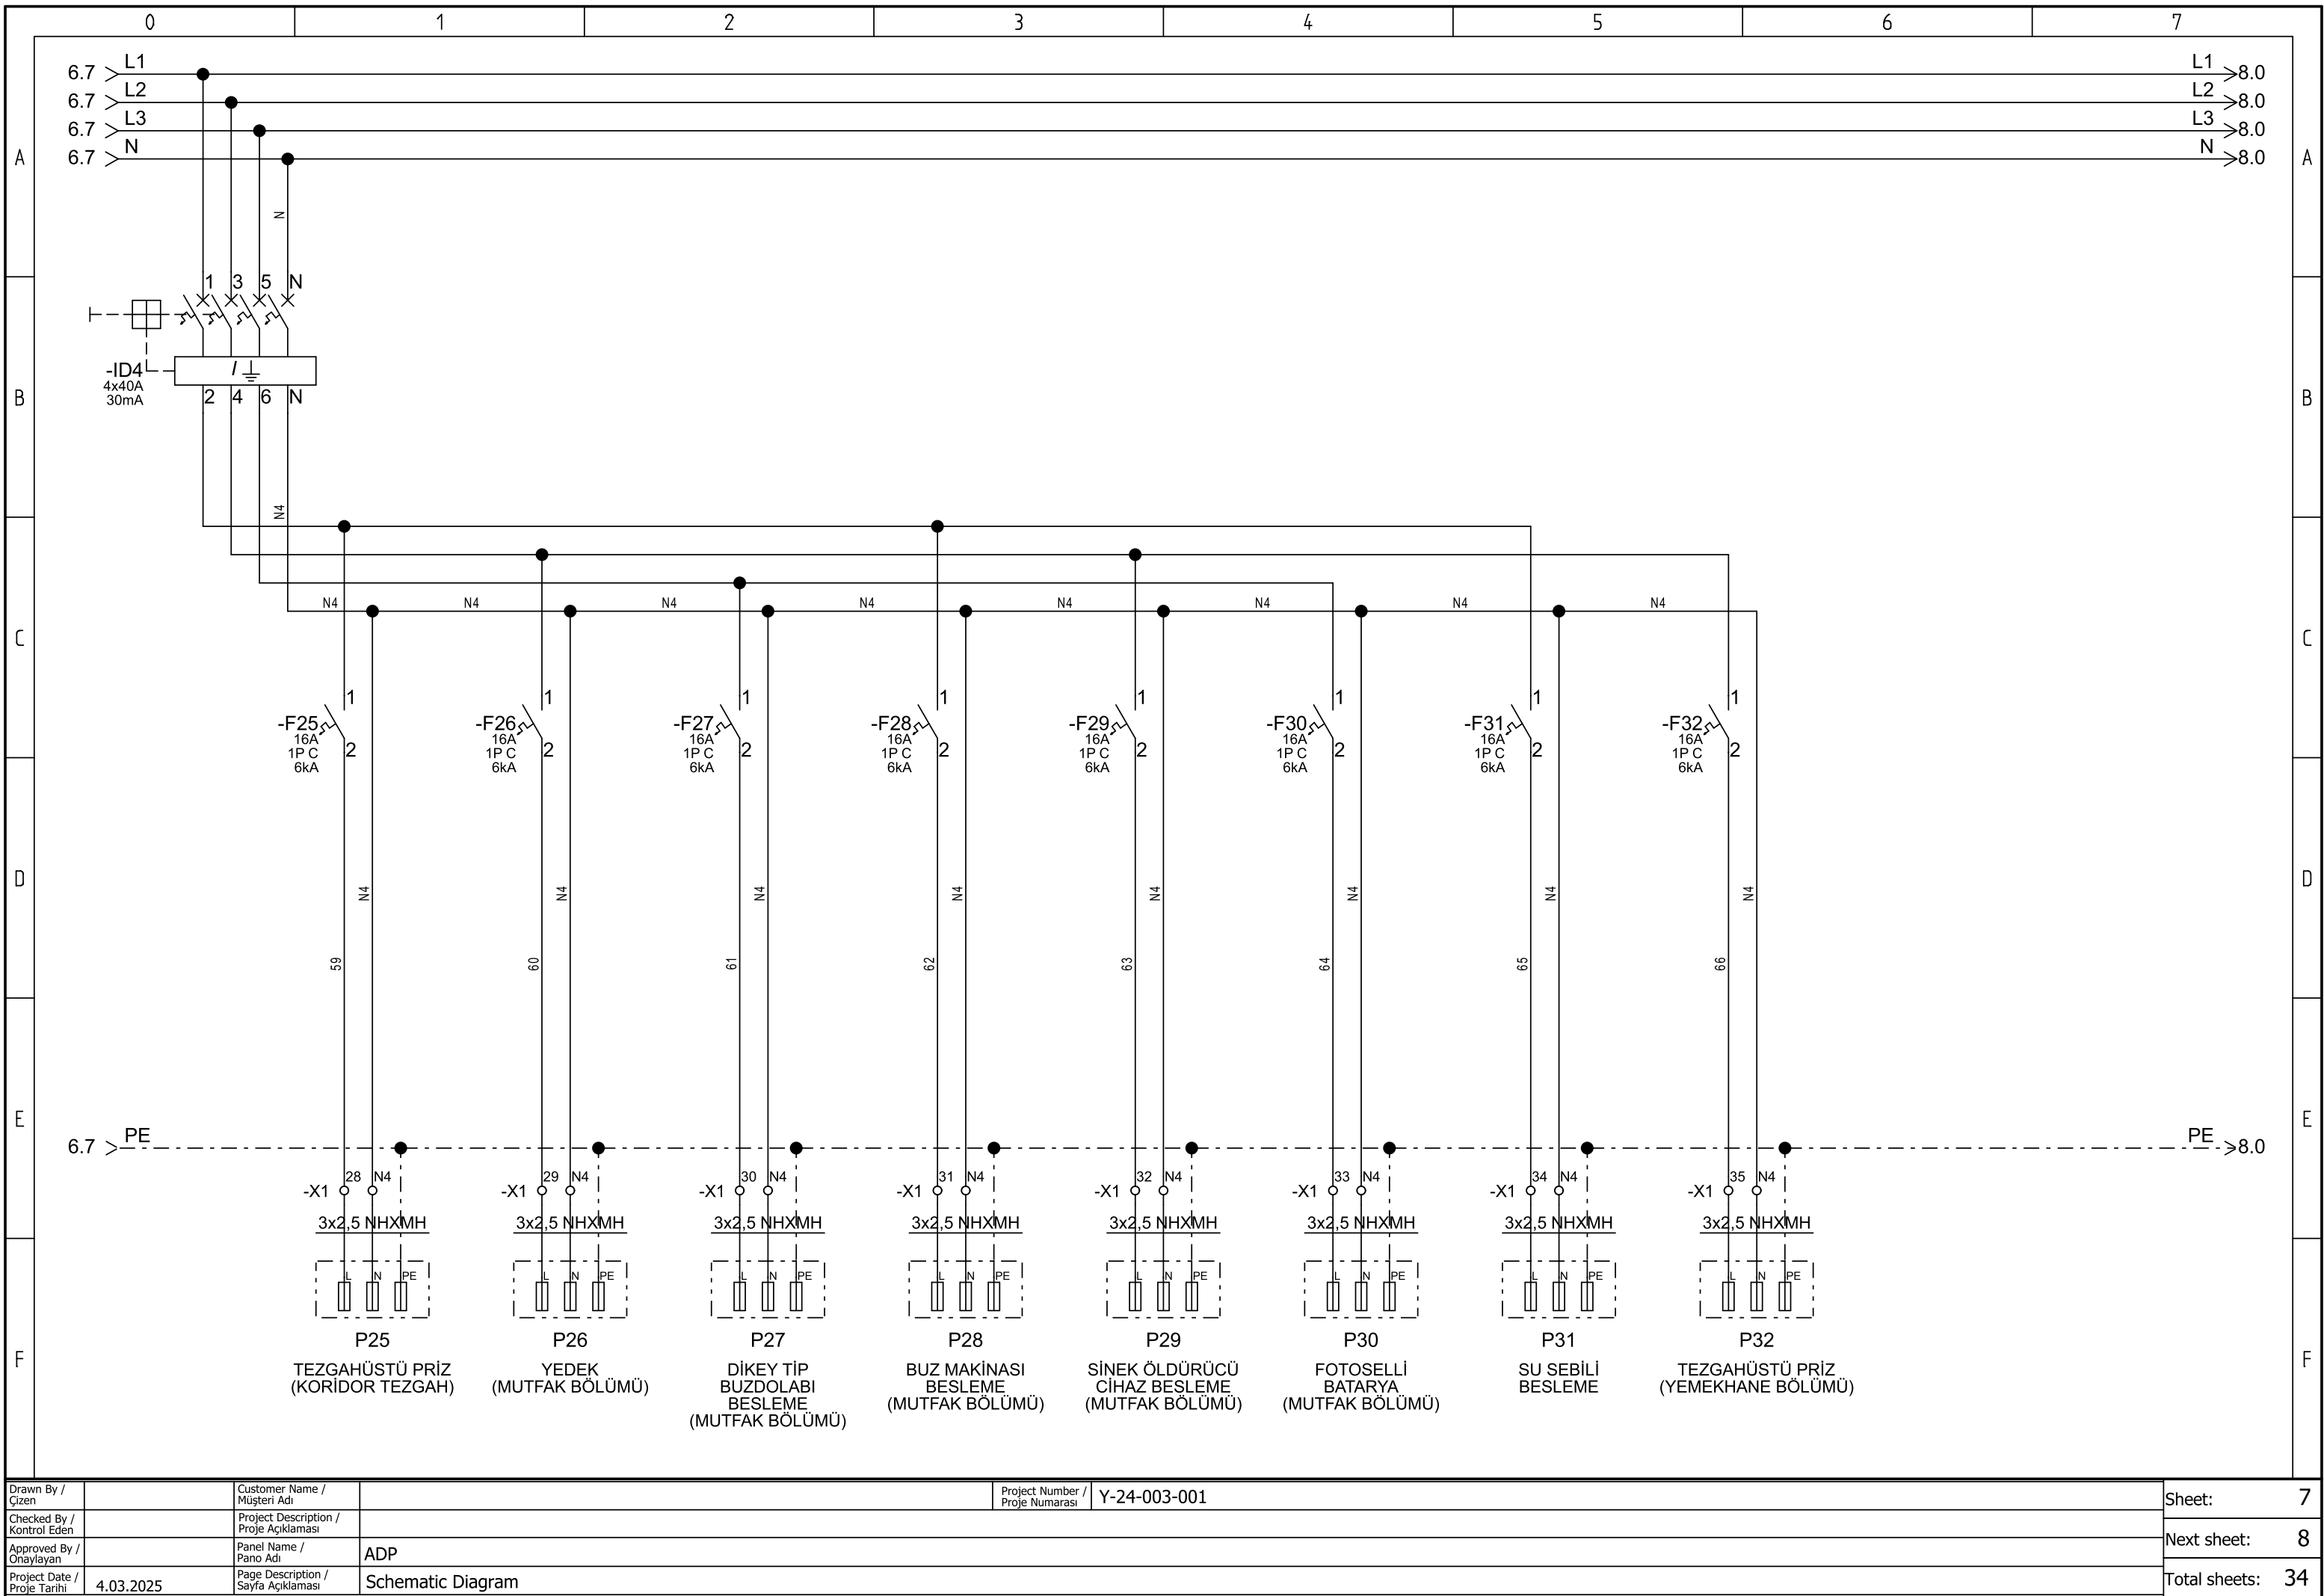


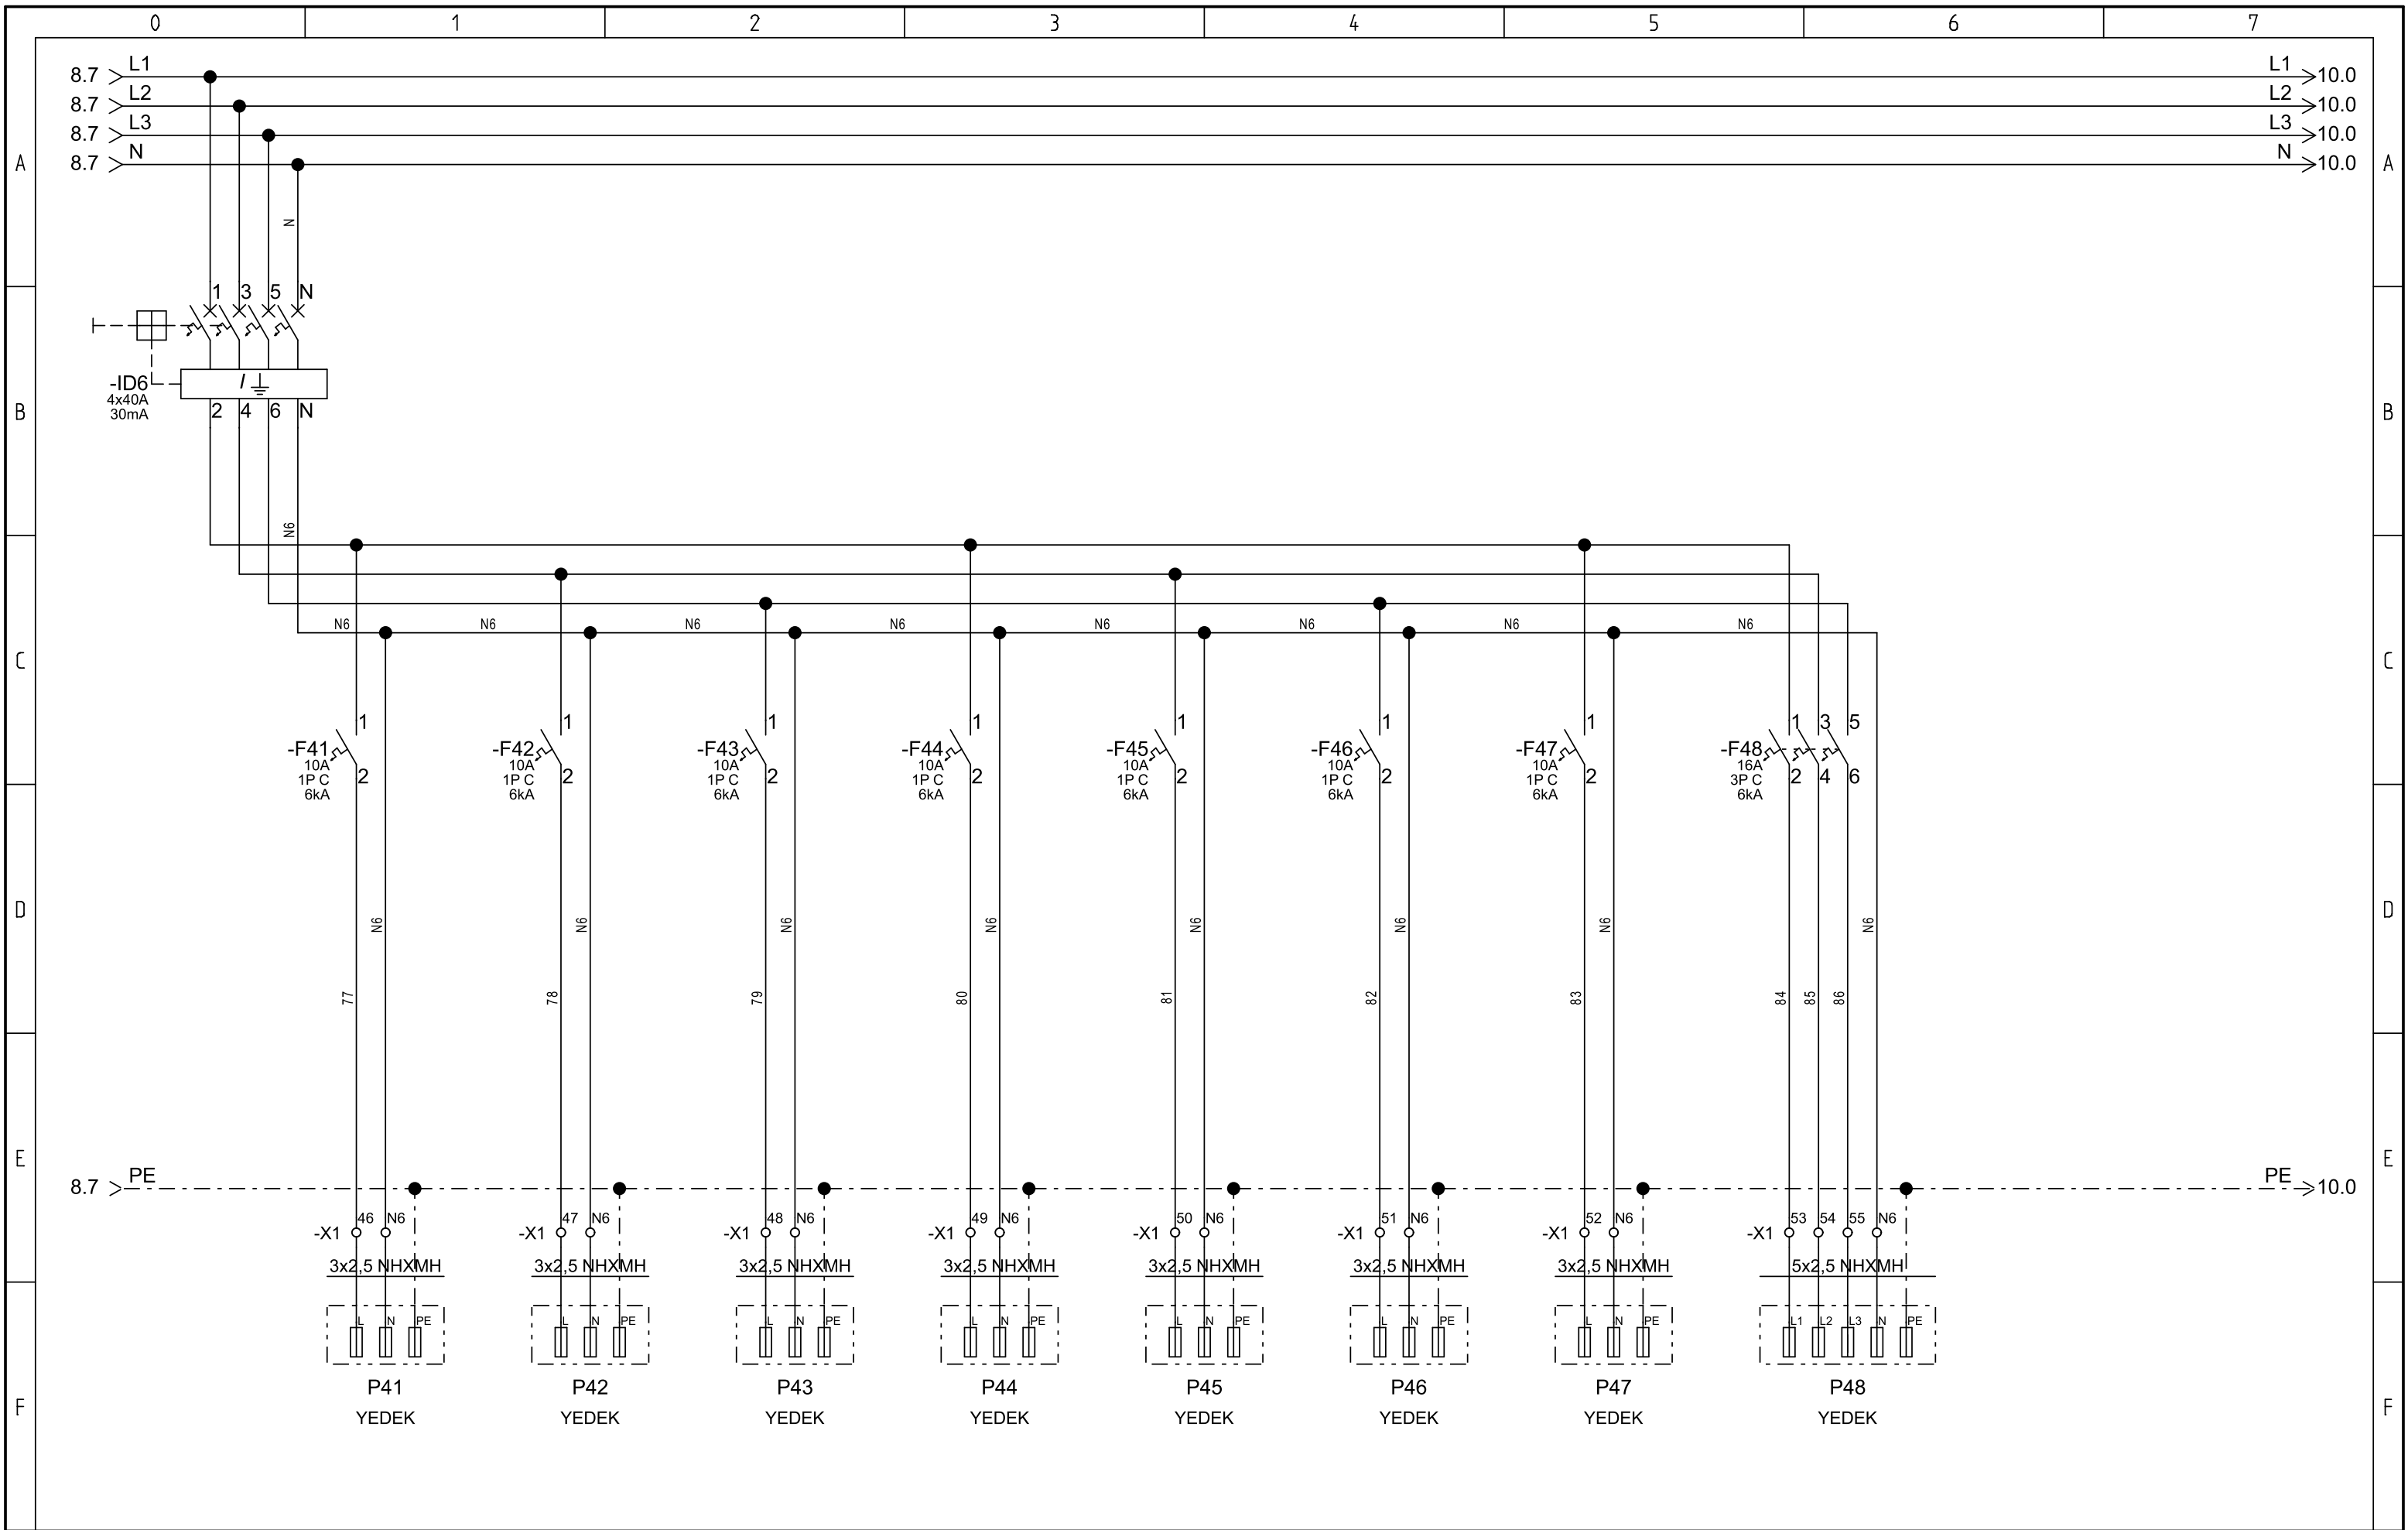


Drawn By / Çizen		Customer Name / Müşteri Adı		Project Number / Proje Numarası	Y-24-003-001	Sheet:	9
Checked By / Kontrol Eden		Project Description / Proje Açıklaması				Next sheet:	10
Approved By / Onaylayan		Panel Name / Pano Adı	ADP			Total sheets:	34
Project Date / Proje Tarihi	4.03.2025	Page Description / Sayfa Açıklaması	Schematic Diagram				

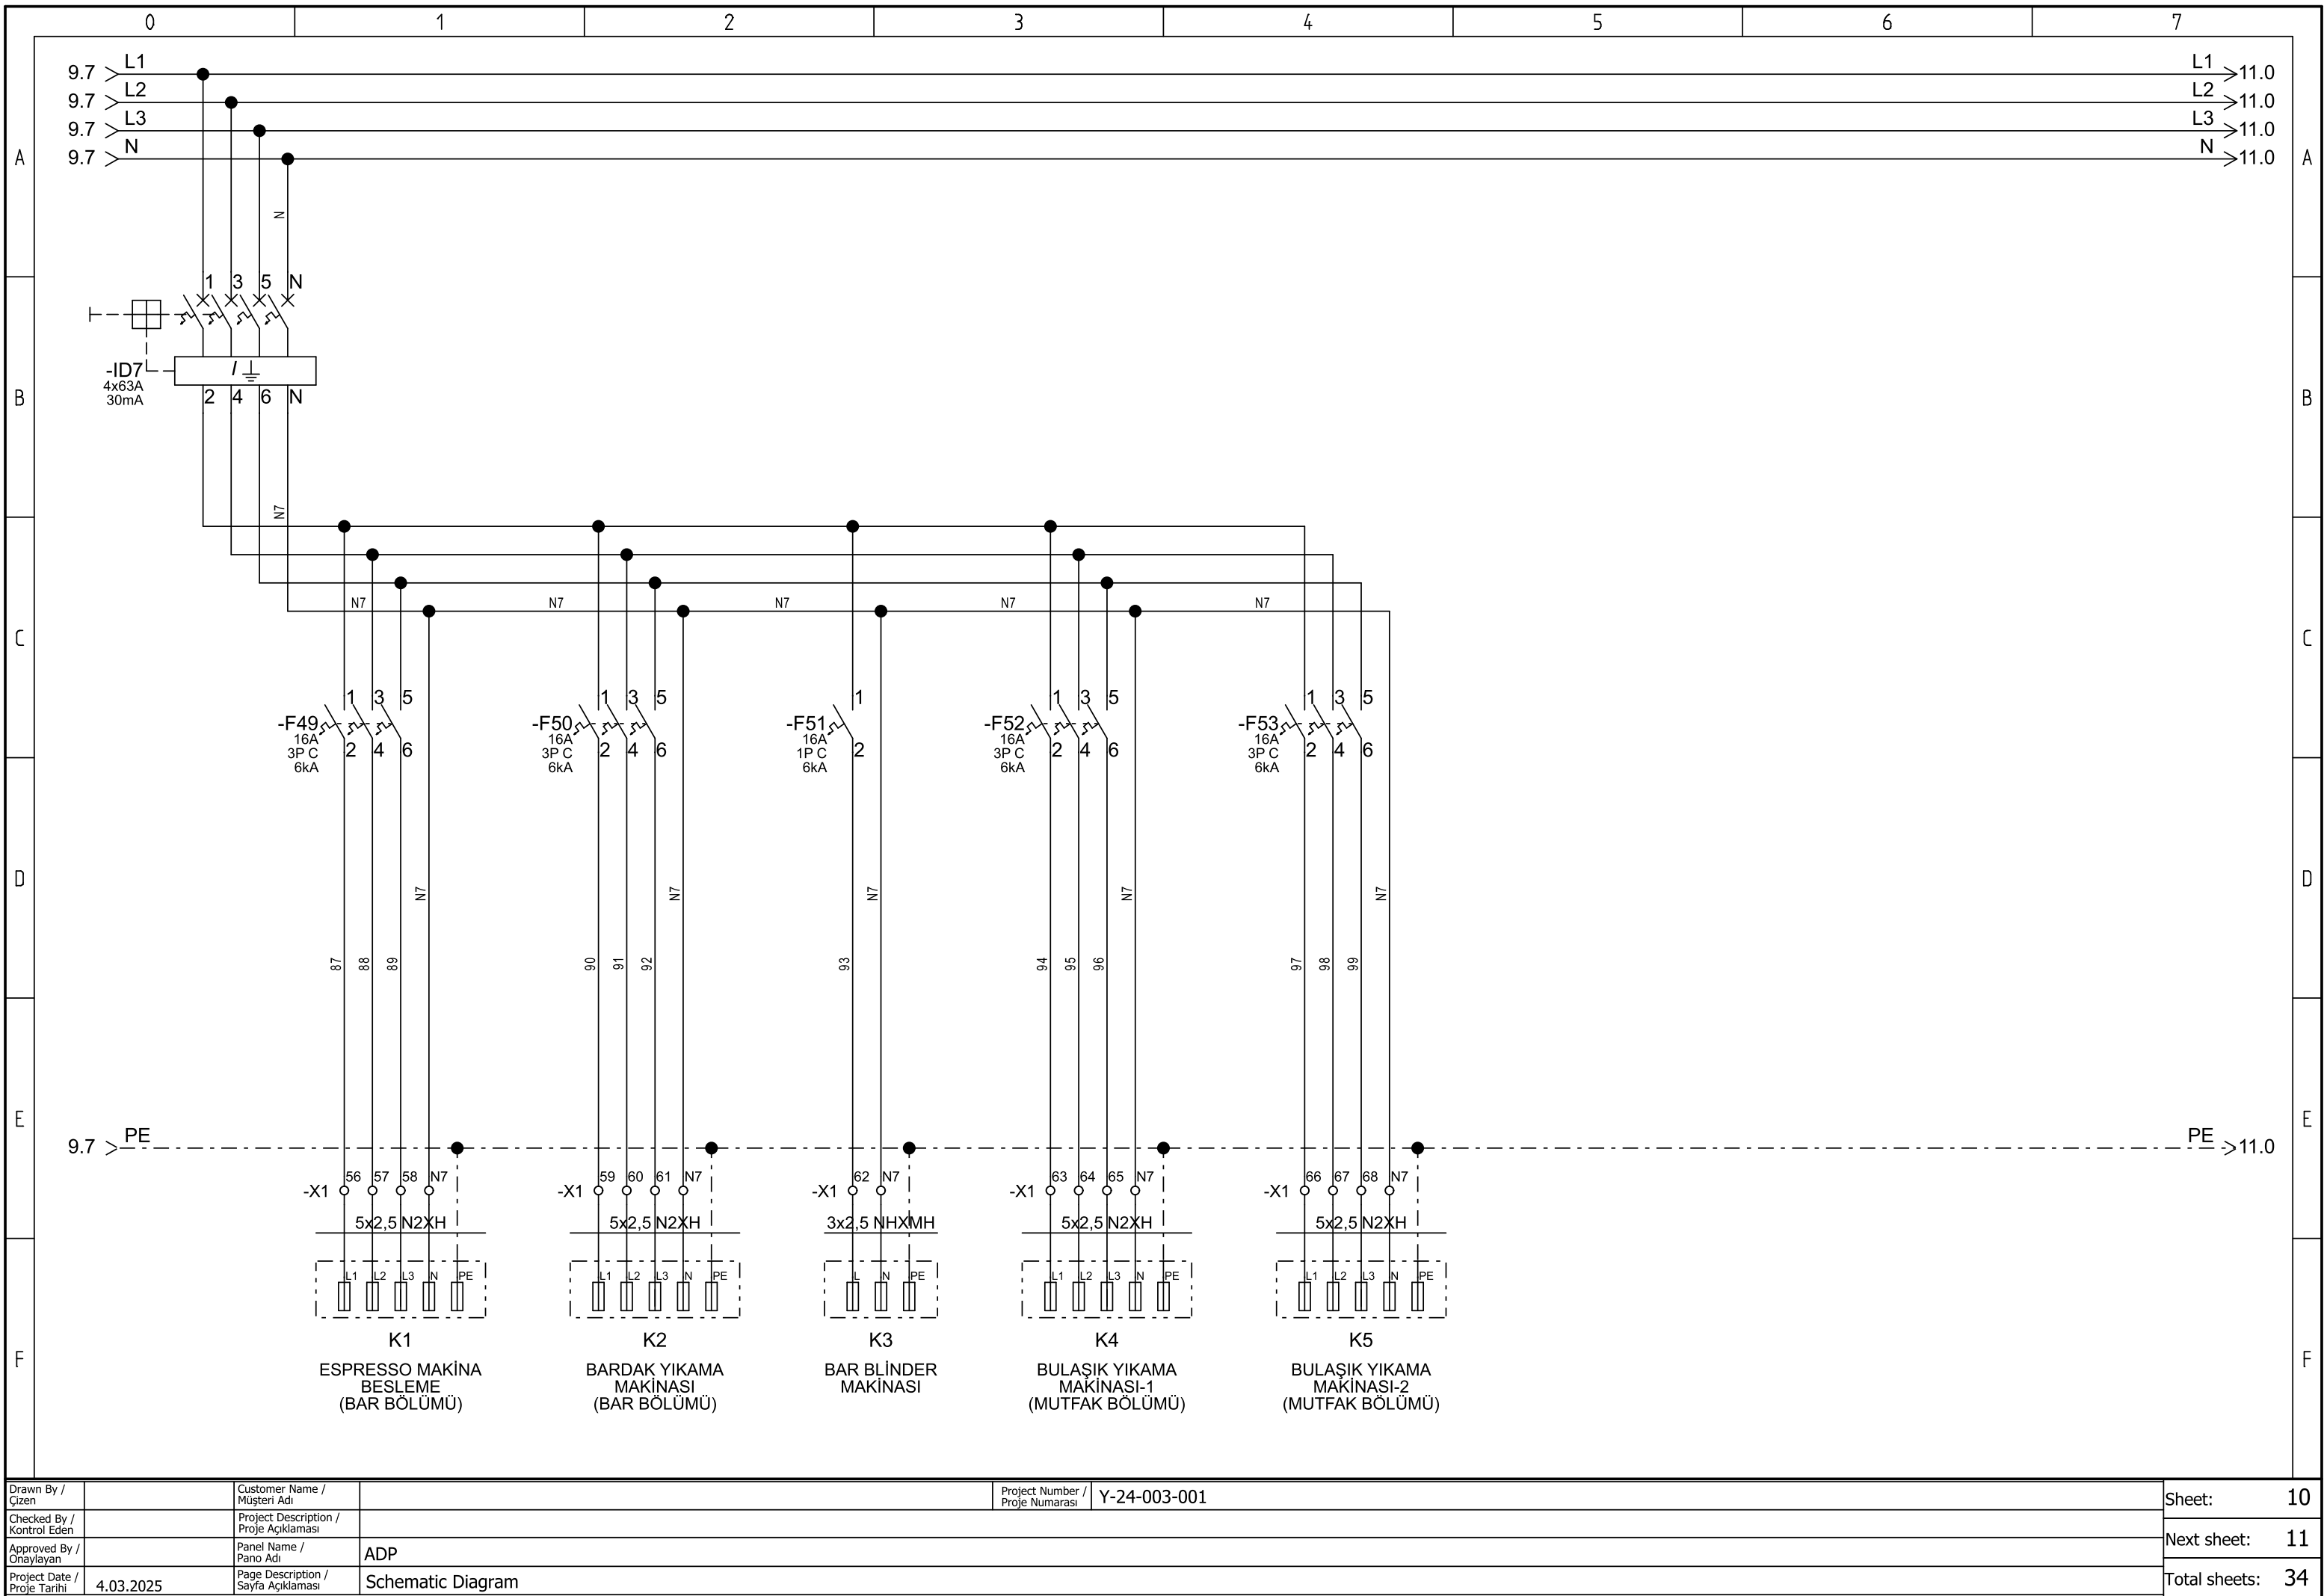


Drawn By / Çizen		Customer Name / Müşteri Adı		Project Number / Proje Numarası	Y-24-003-001	Sheet:	10
Checked By / Kontrol Eden		Project Description / Proje Açıklaması				Next sheet:	11
Approved By / Onaylayan		Panel Name / Pano Adı	ADP			Total sheets:	34
Project Date / Proje Tarihi	4.03.2025	Page Description / Sayfa Açıklaması	Schematic Diagram				

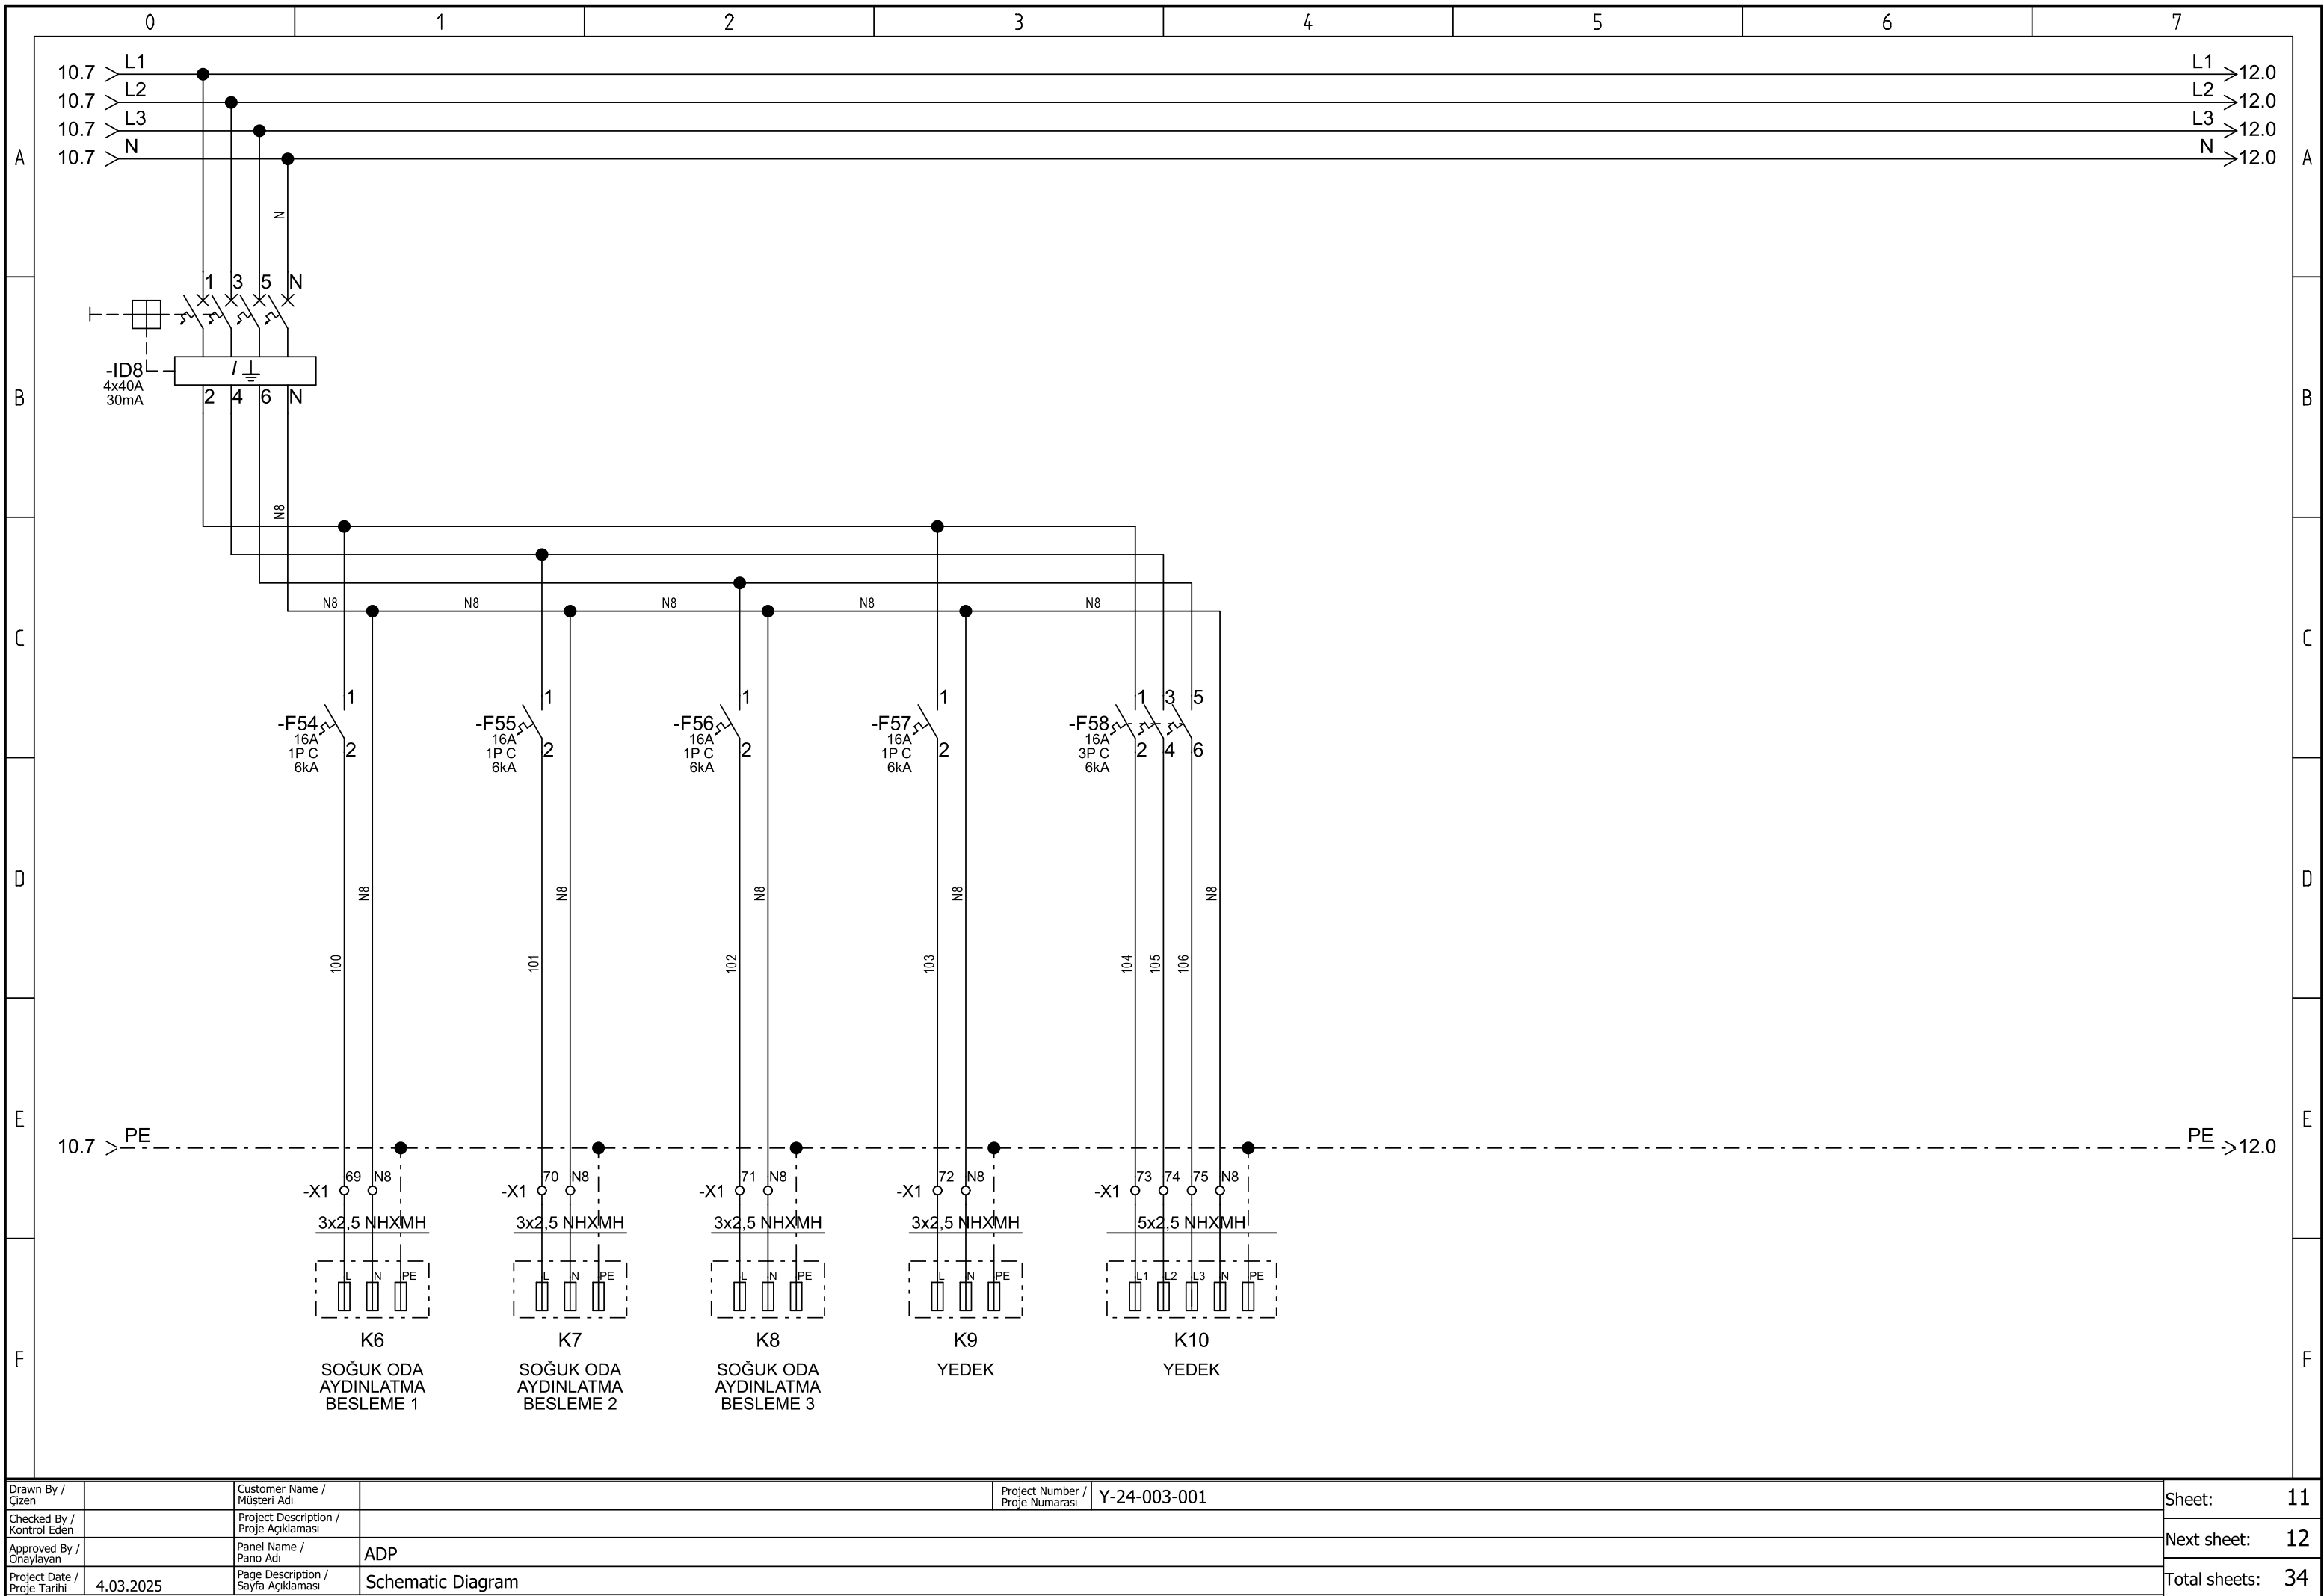


Drawn By / Çizen		Customer Name / Müşteri Adı		Project Number / Proje Numarası	Y-24-003-001	Sheet:	11
Checked By / Kontrol Eden		Project Description / Proje Açıklaması				Next sheet:	12
Approved By / Onaylayan		Panel Name / Pano Adı	ADP			Total sheets:	34
Project Date / Proje Tarihi	4.03.2025	Page Description / Sayfa Açıklaması	Schematic Diagram				

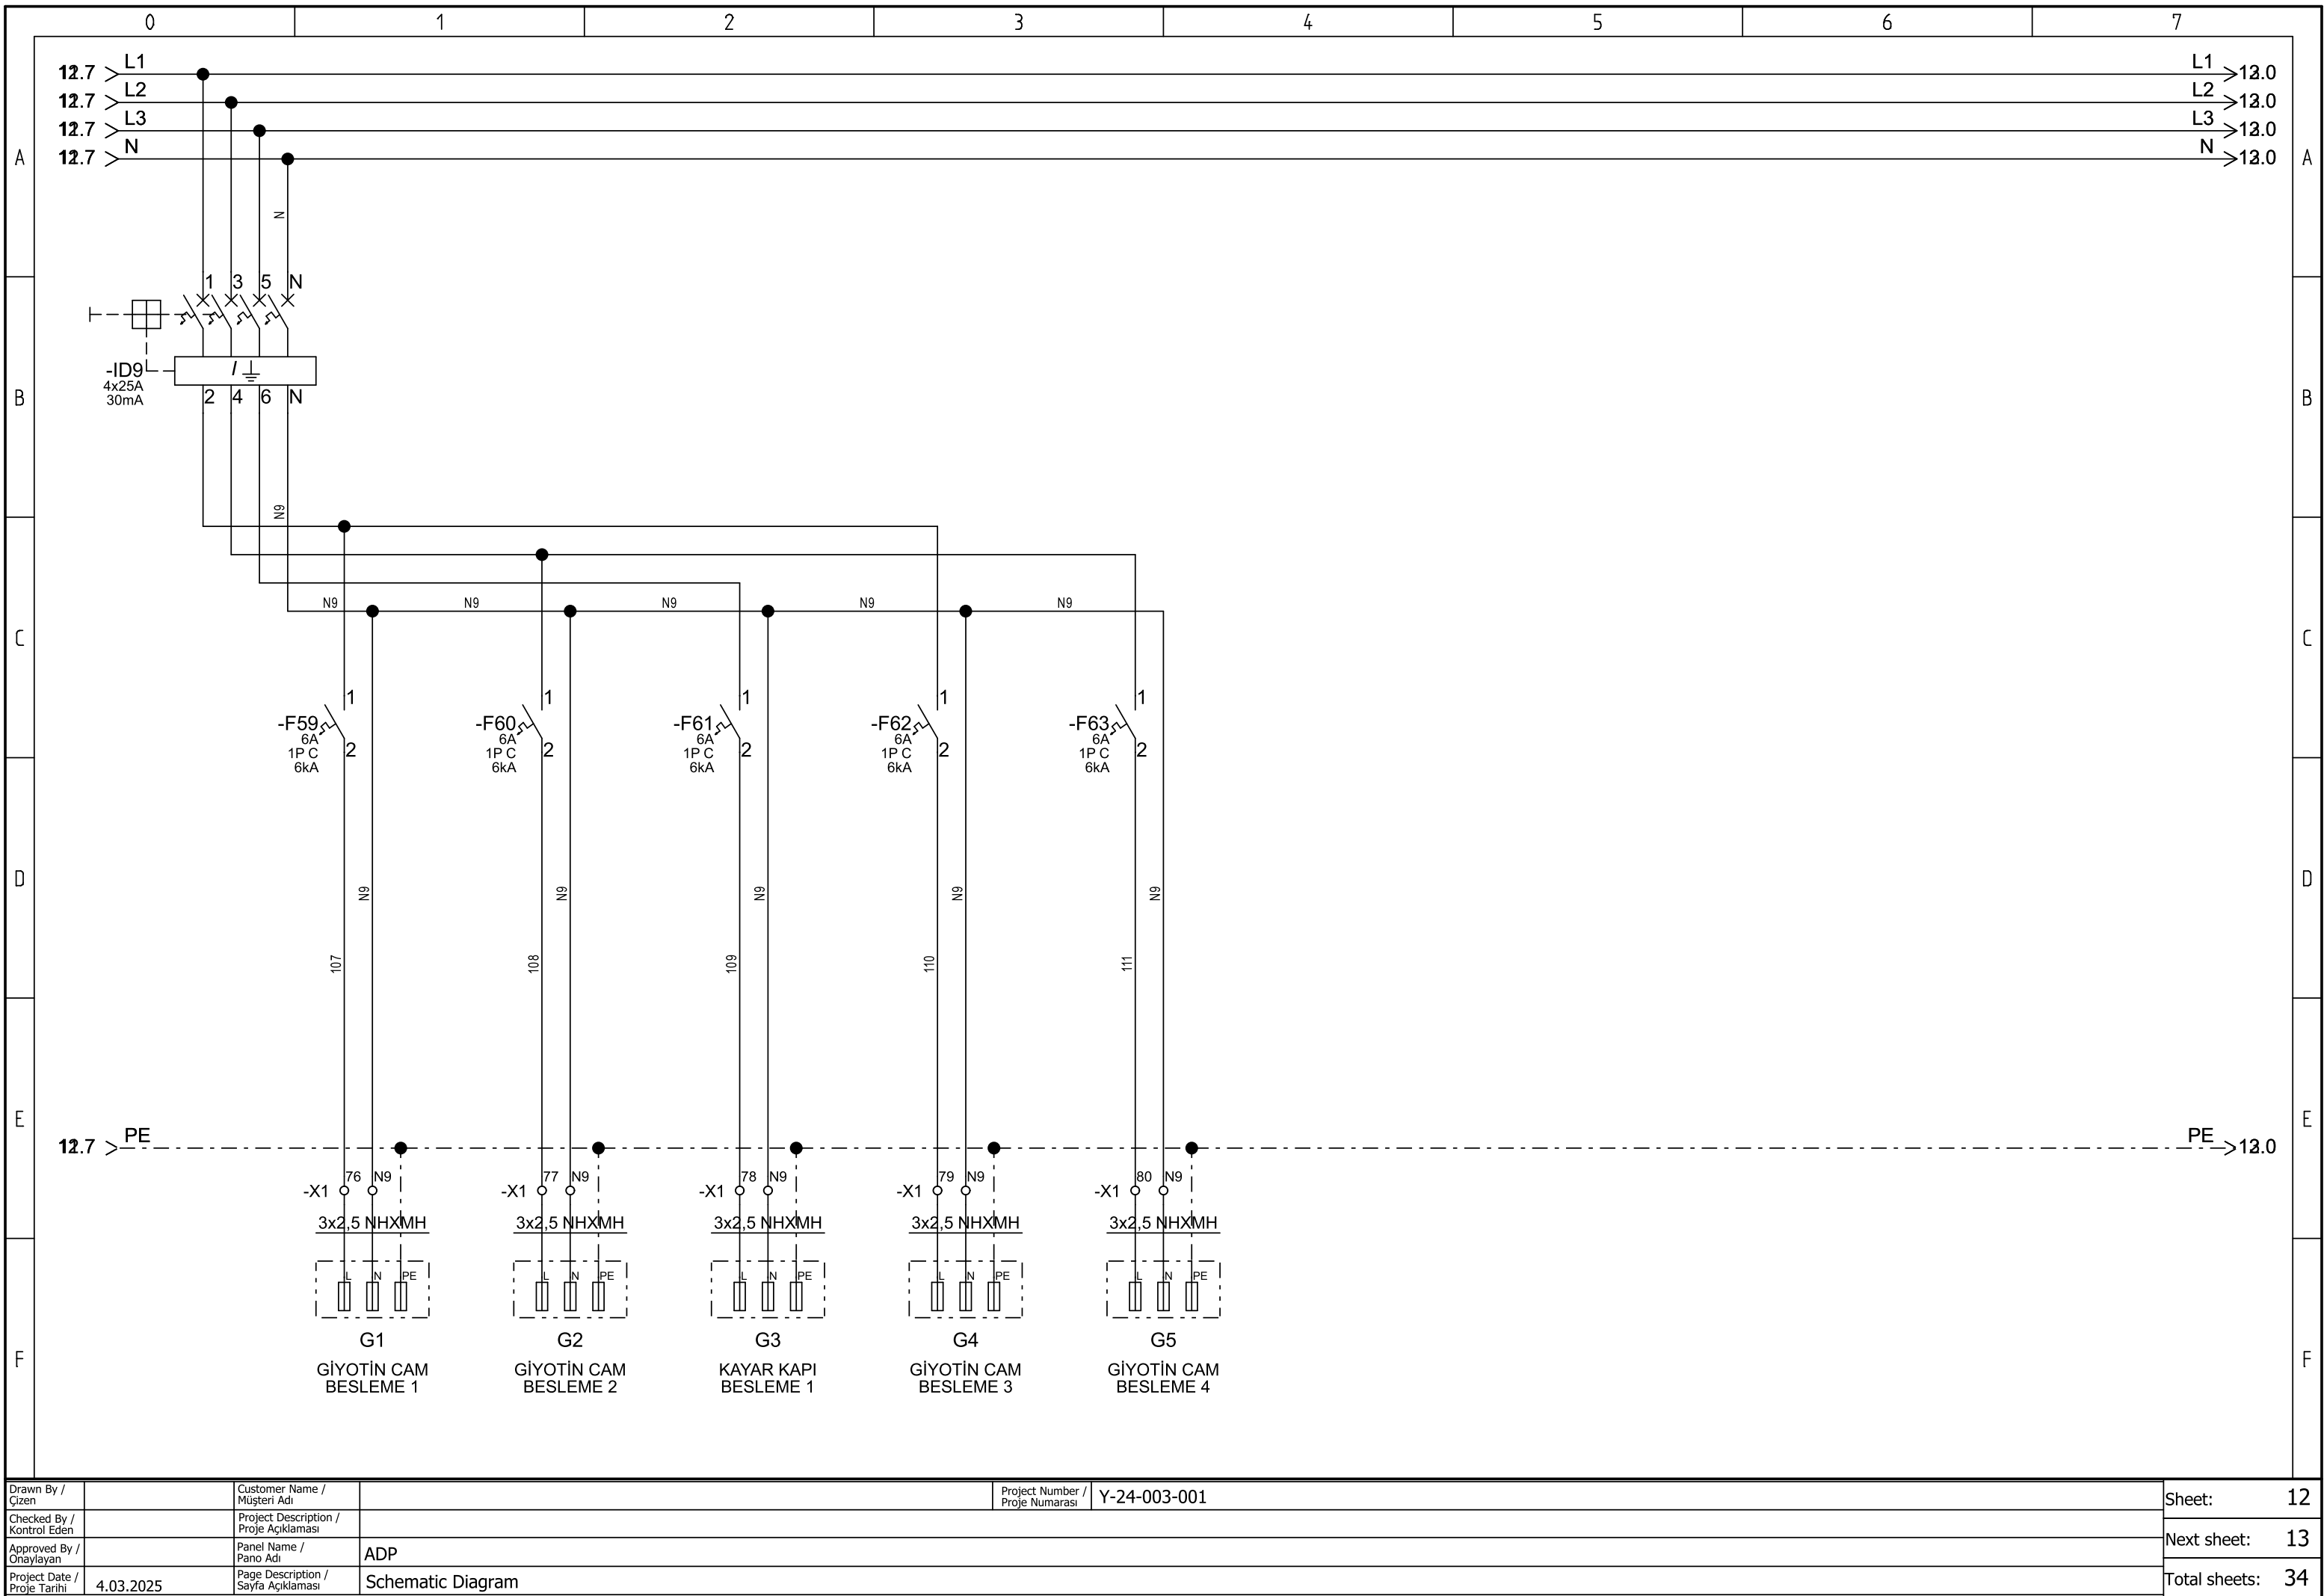


Drawn By / Çizen		Customer Name / Müşteri Adı		Project Number / Proje Numarası	Y-24-003-001	Sheet:	12
Checked By / Kontrol Eden		Project Description / Proje Açıklaması				Next sheet:	13
Approved By / Onaylayan		Panel Name / Pano Adı	ADP			Total sheets:	34
Project Date / Proje Tarihi	4.03.2025	Page Description / Sayfa Açıklaması	Schematic Diagram				

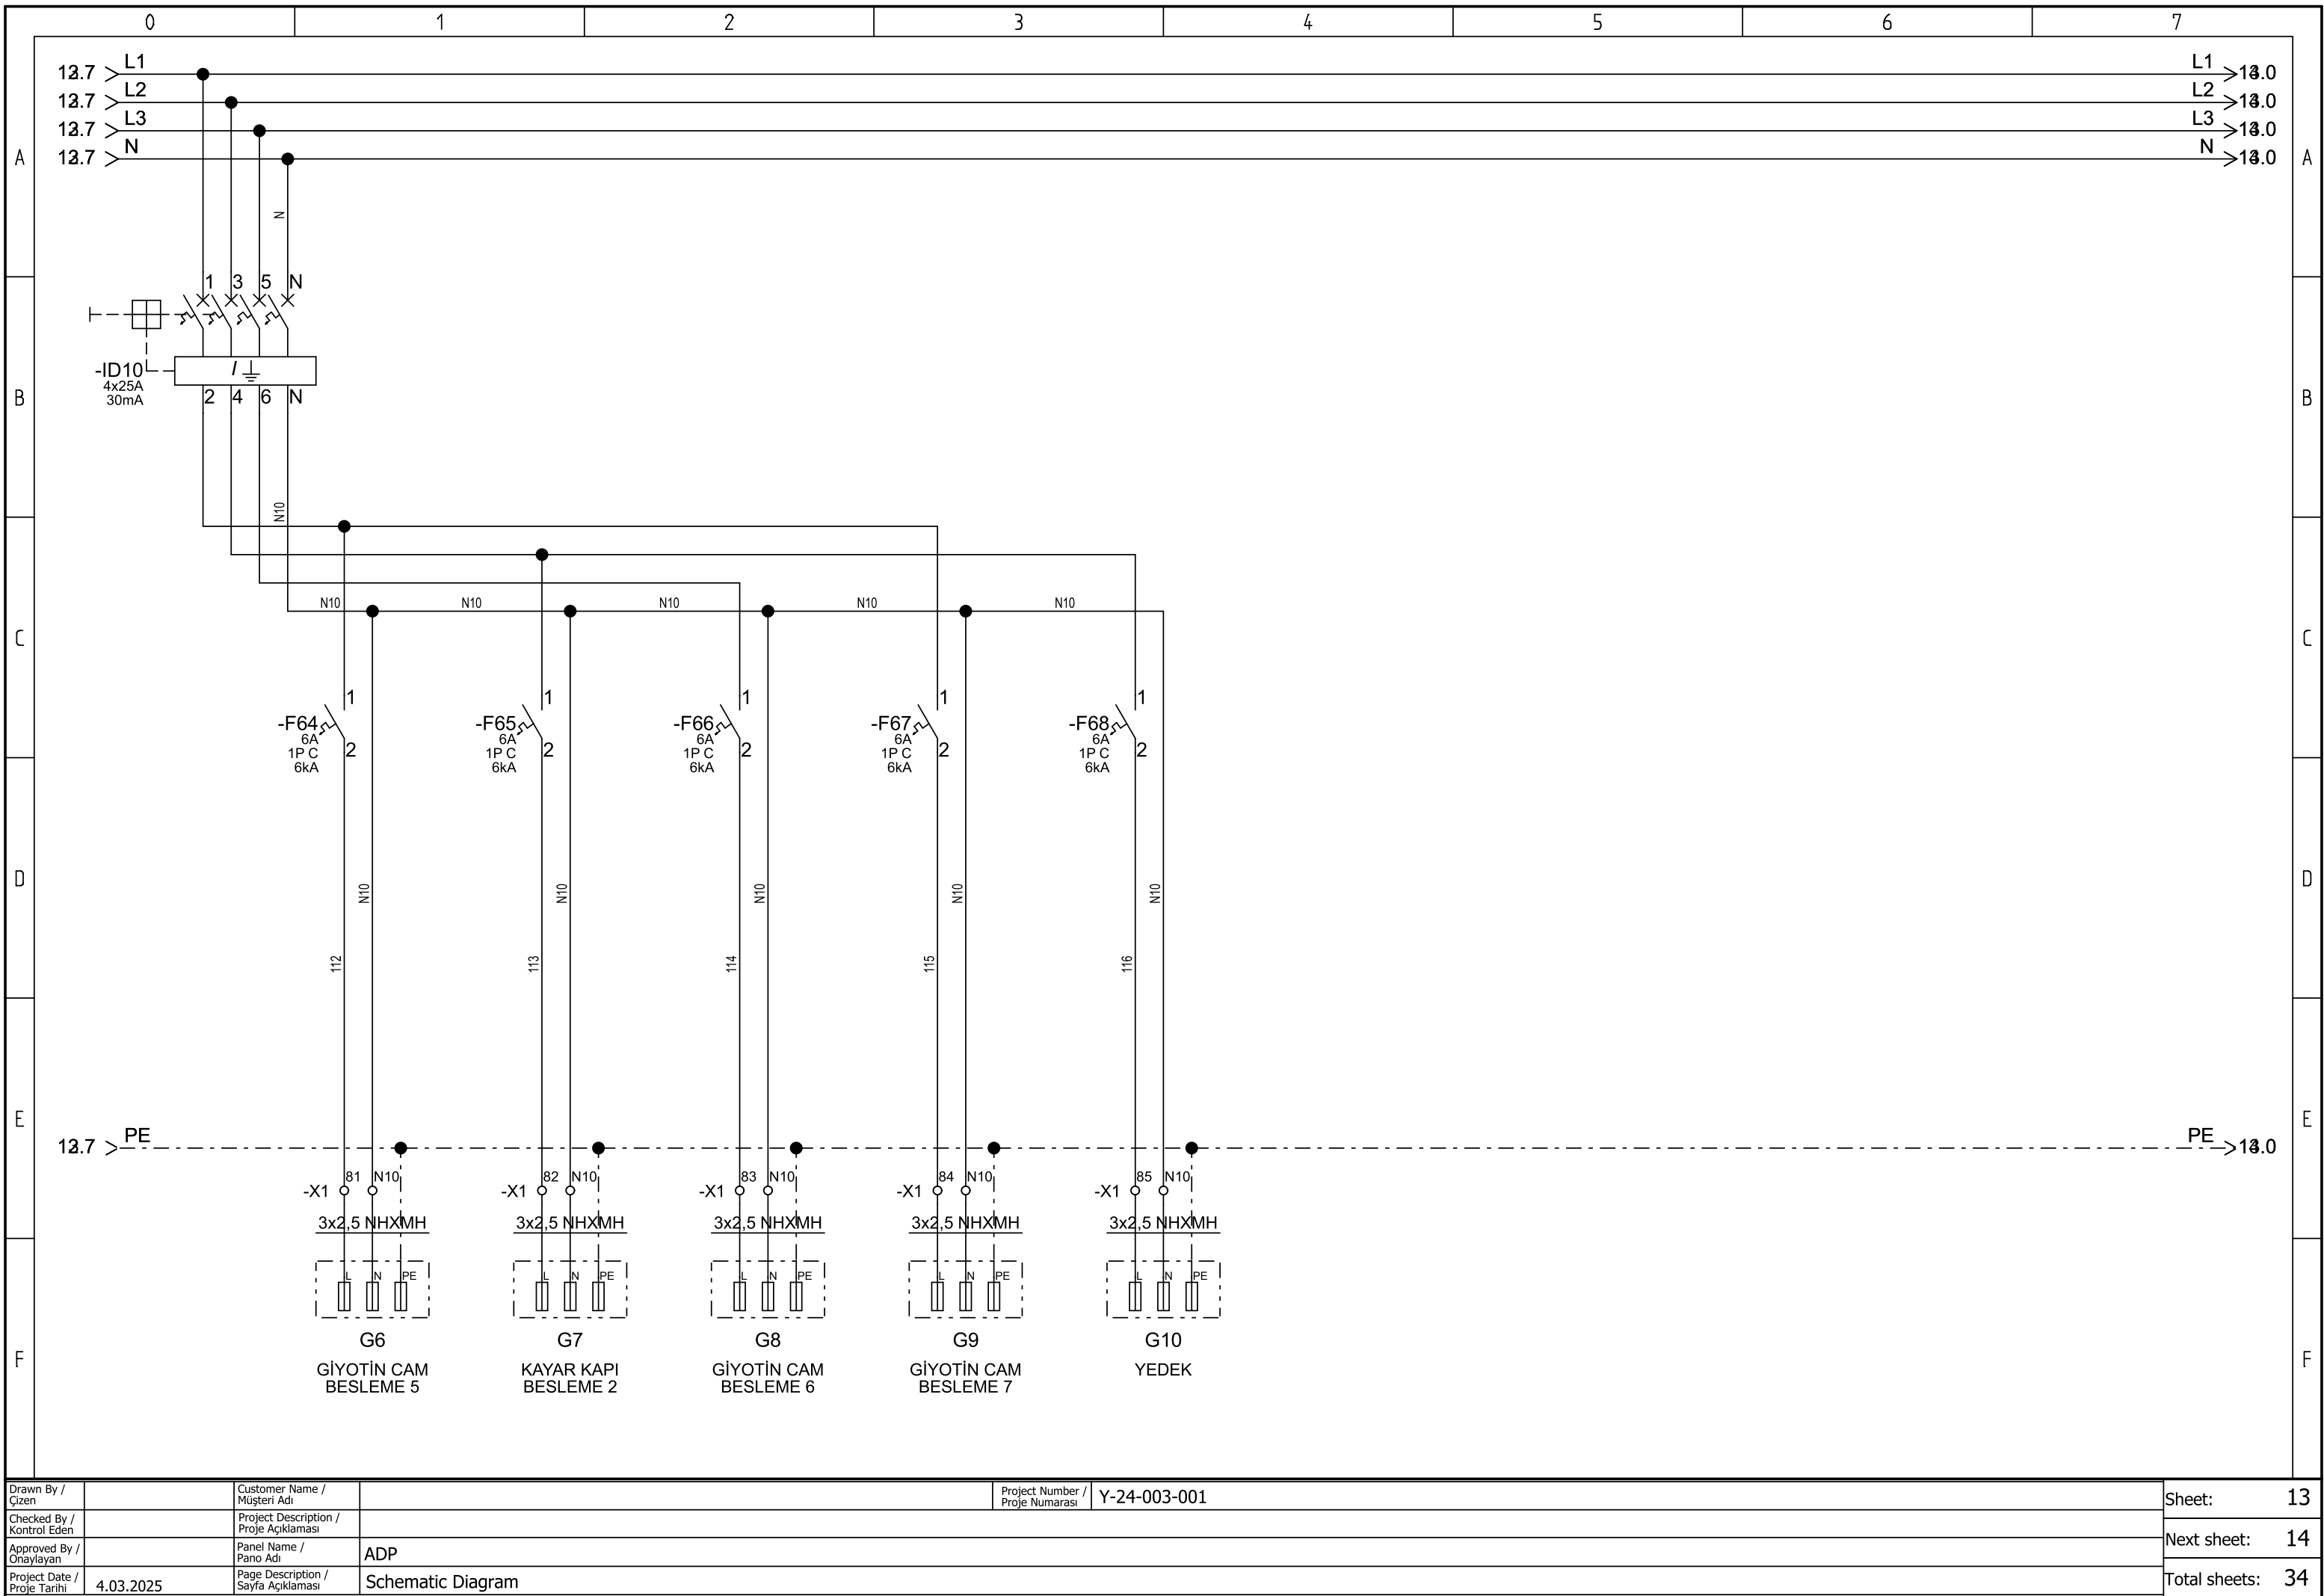


Drawn By / Çizen		Customer Name / Müşteri Adı		Project Number / Proje Numarası	Y-24-003-001	Sheet:	13
Checked By / Kontrol Eden		Project Description / Proje Açıklaması				Next sheet:	14
Approved By / Onaylayan		Panel Name / Pano Adı	ADP			Total sheets:	34
Project Date / Proje Tarihi	4.03.2025	Page Description / Sayfa Açıklaması	Schematic Diagram				

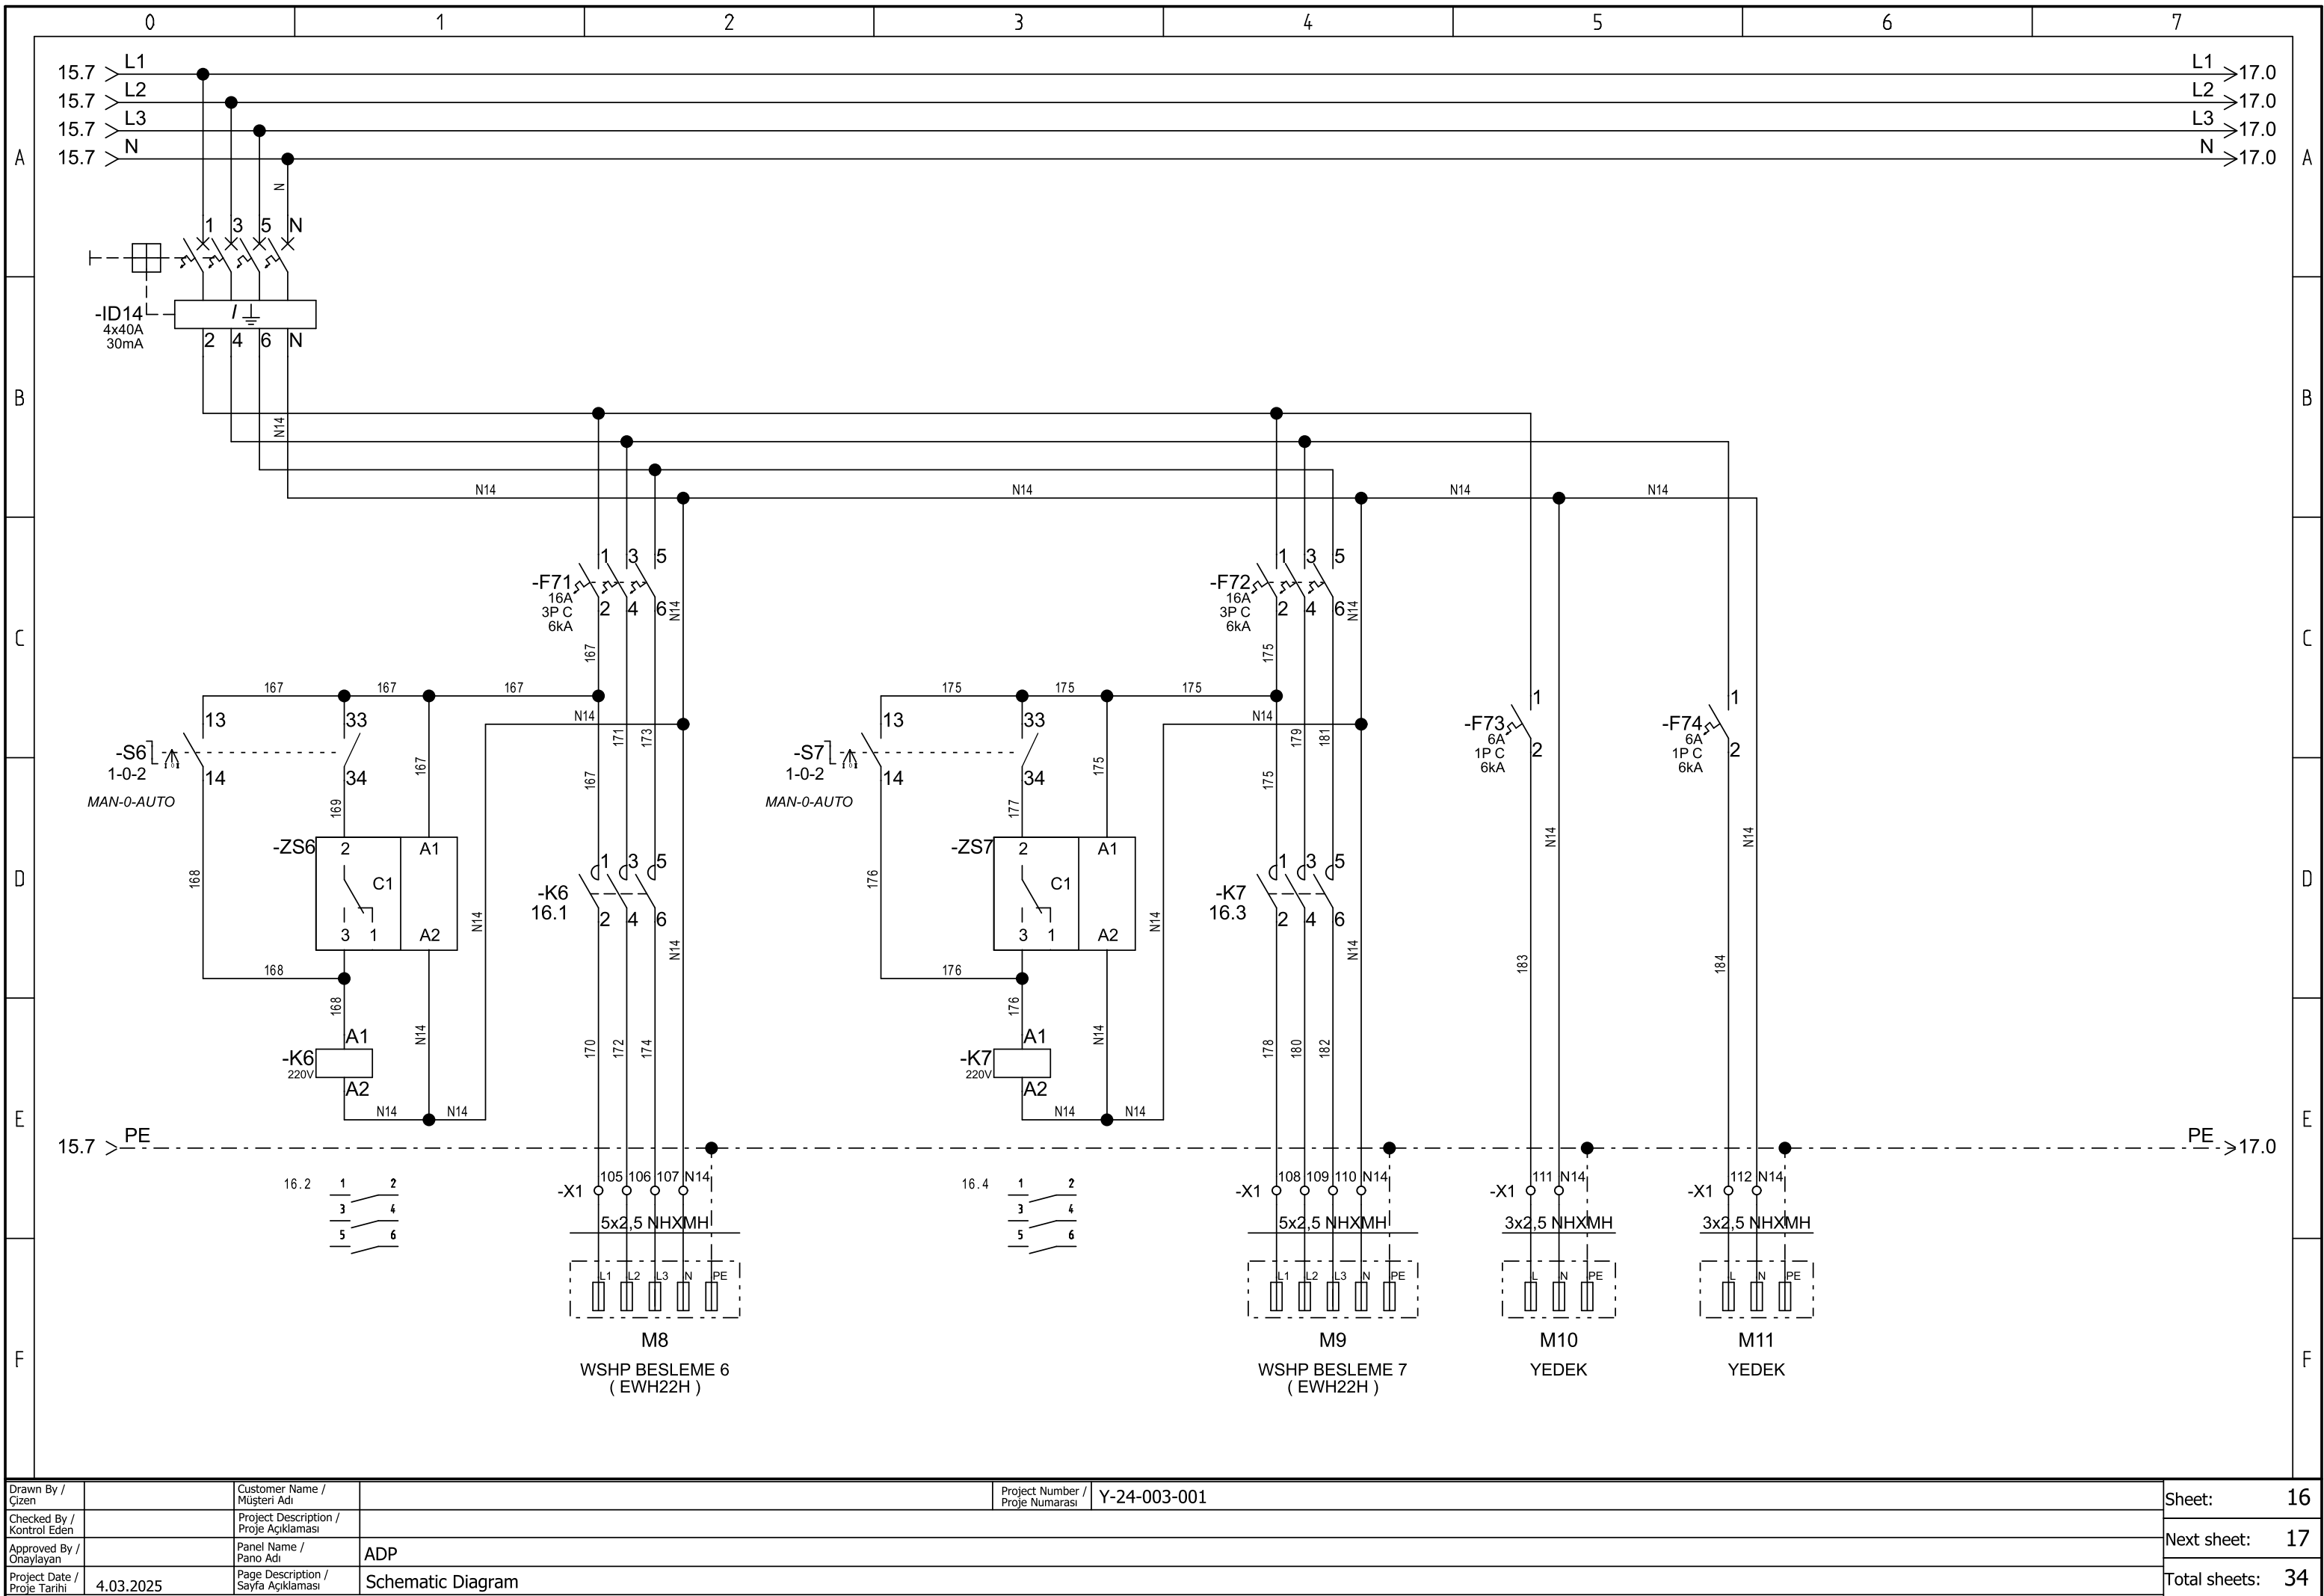


Drawn By / Çizen		Customer Name / Müşteri Adı		Project Number / Proje Numarası	Y-24-003-001	Sheet:	16
Checked By / Kontrol Eden		Project Description / Proje Açıklaması				Next sheet:	17
Approved By / Onaylayan		Panel Name / Pano Adı	ADP			Total sheets:	34
Project Date / Proje Tarihi	4.03.2025	Page Description / Sayfa Açıklaması	Schematic Diagram				

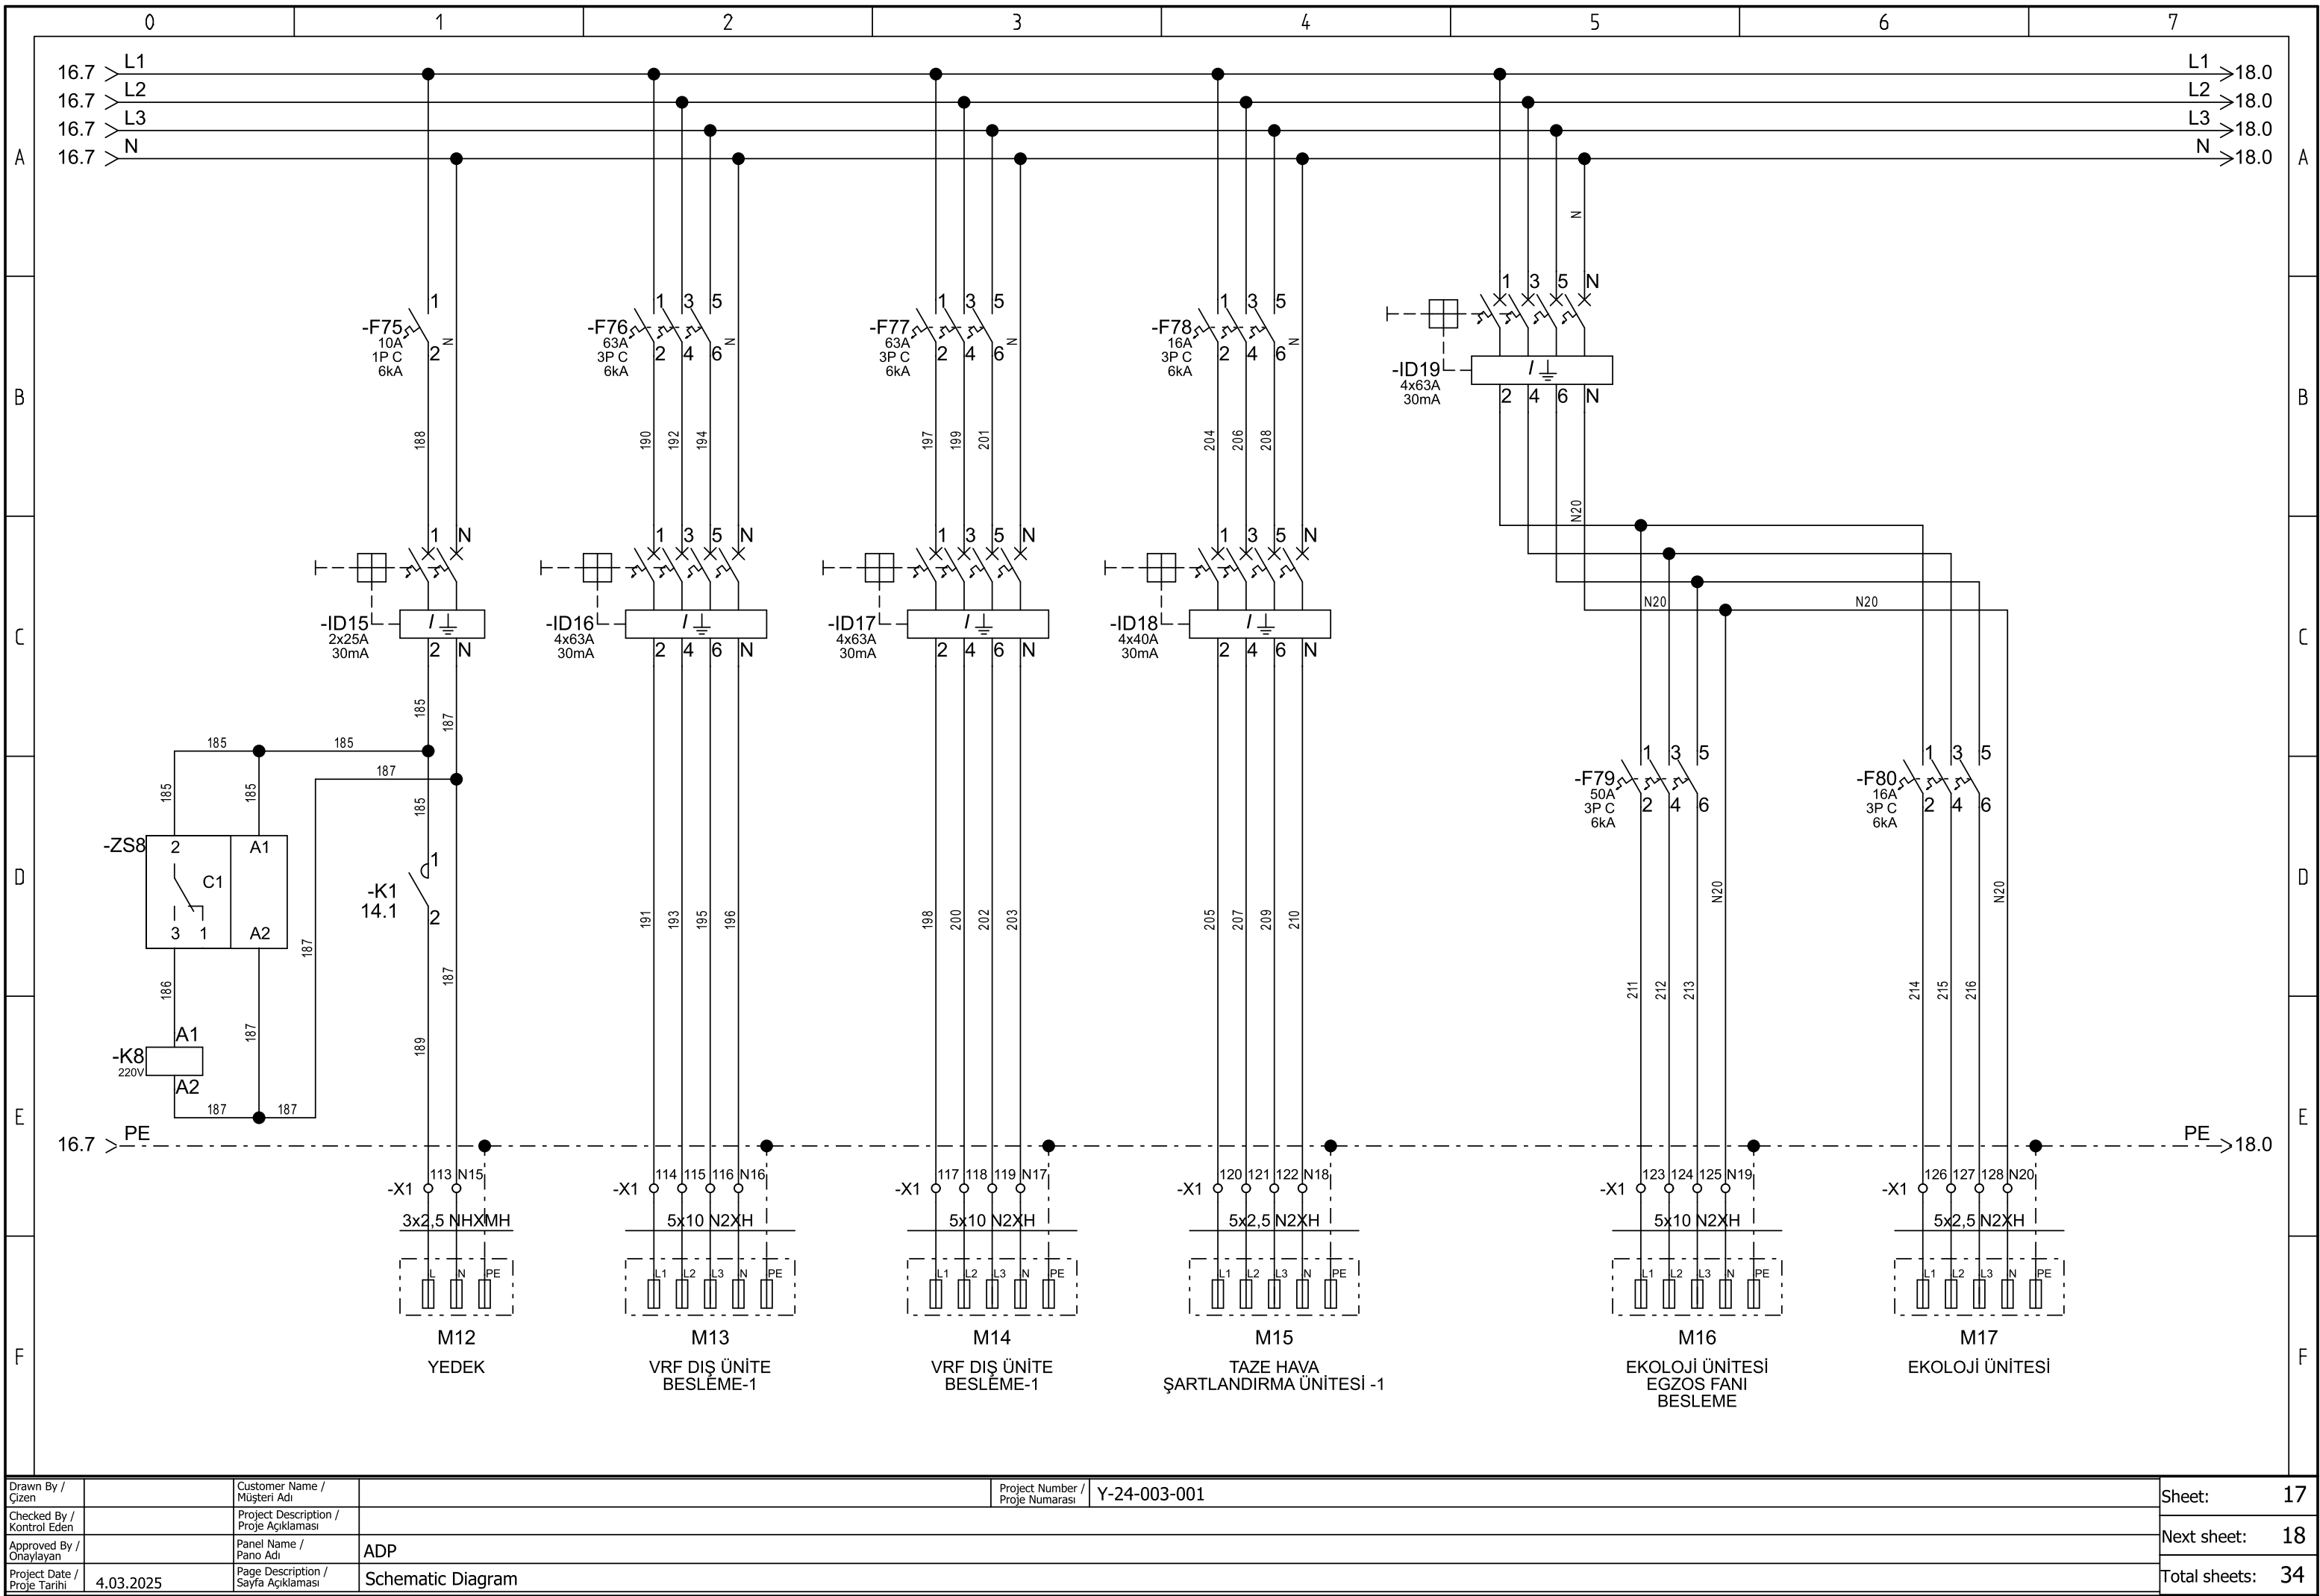


Drawn By / Çizen		Customer Name / Müşteri Adı		Project Number / Proje Numarası	Y-24-003-001	Sheet:	17
Checked By / Kontrol Eden		Project Description / Proje Açıklaması				Next sheet:	18
Approved By / Onaylayan		Panel Name / Pano Adı	ADP			Total sheets:	34
Project Date / Proje Tarihi	4.03.2025	Page Description / Sayfa Açıklaması	Schematic Diagram				

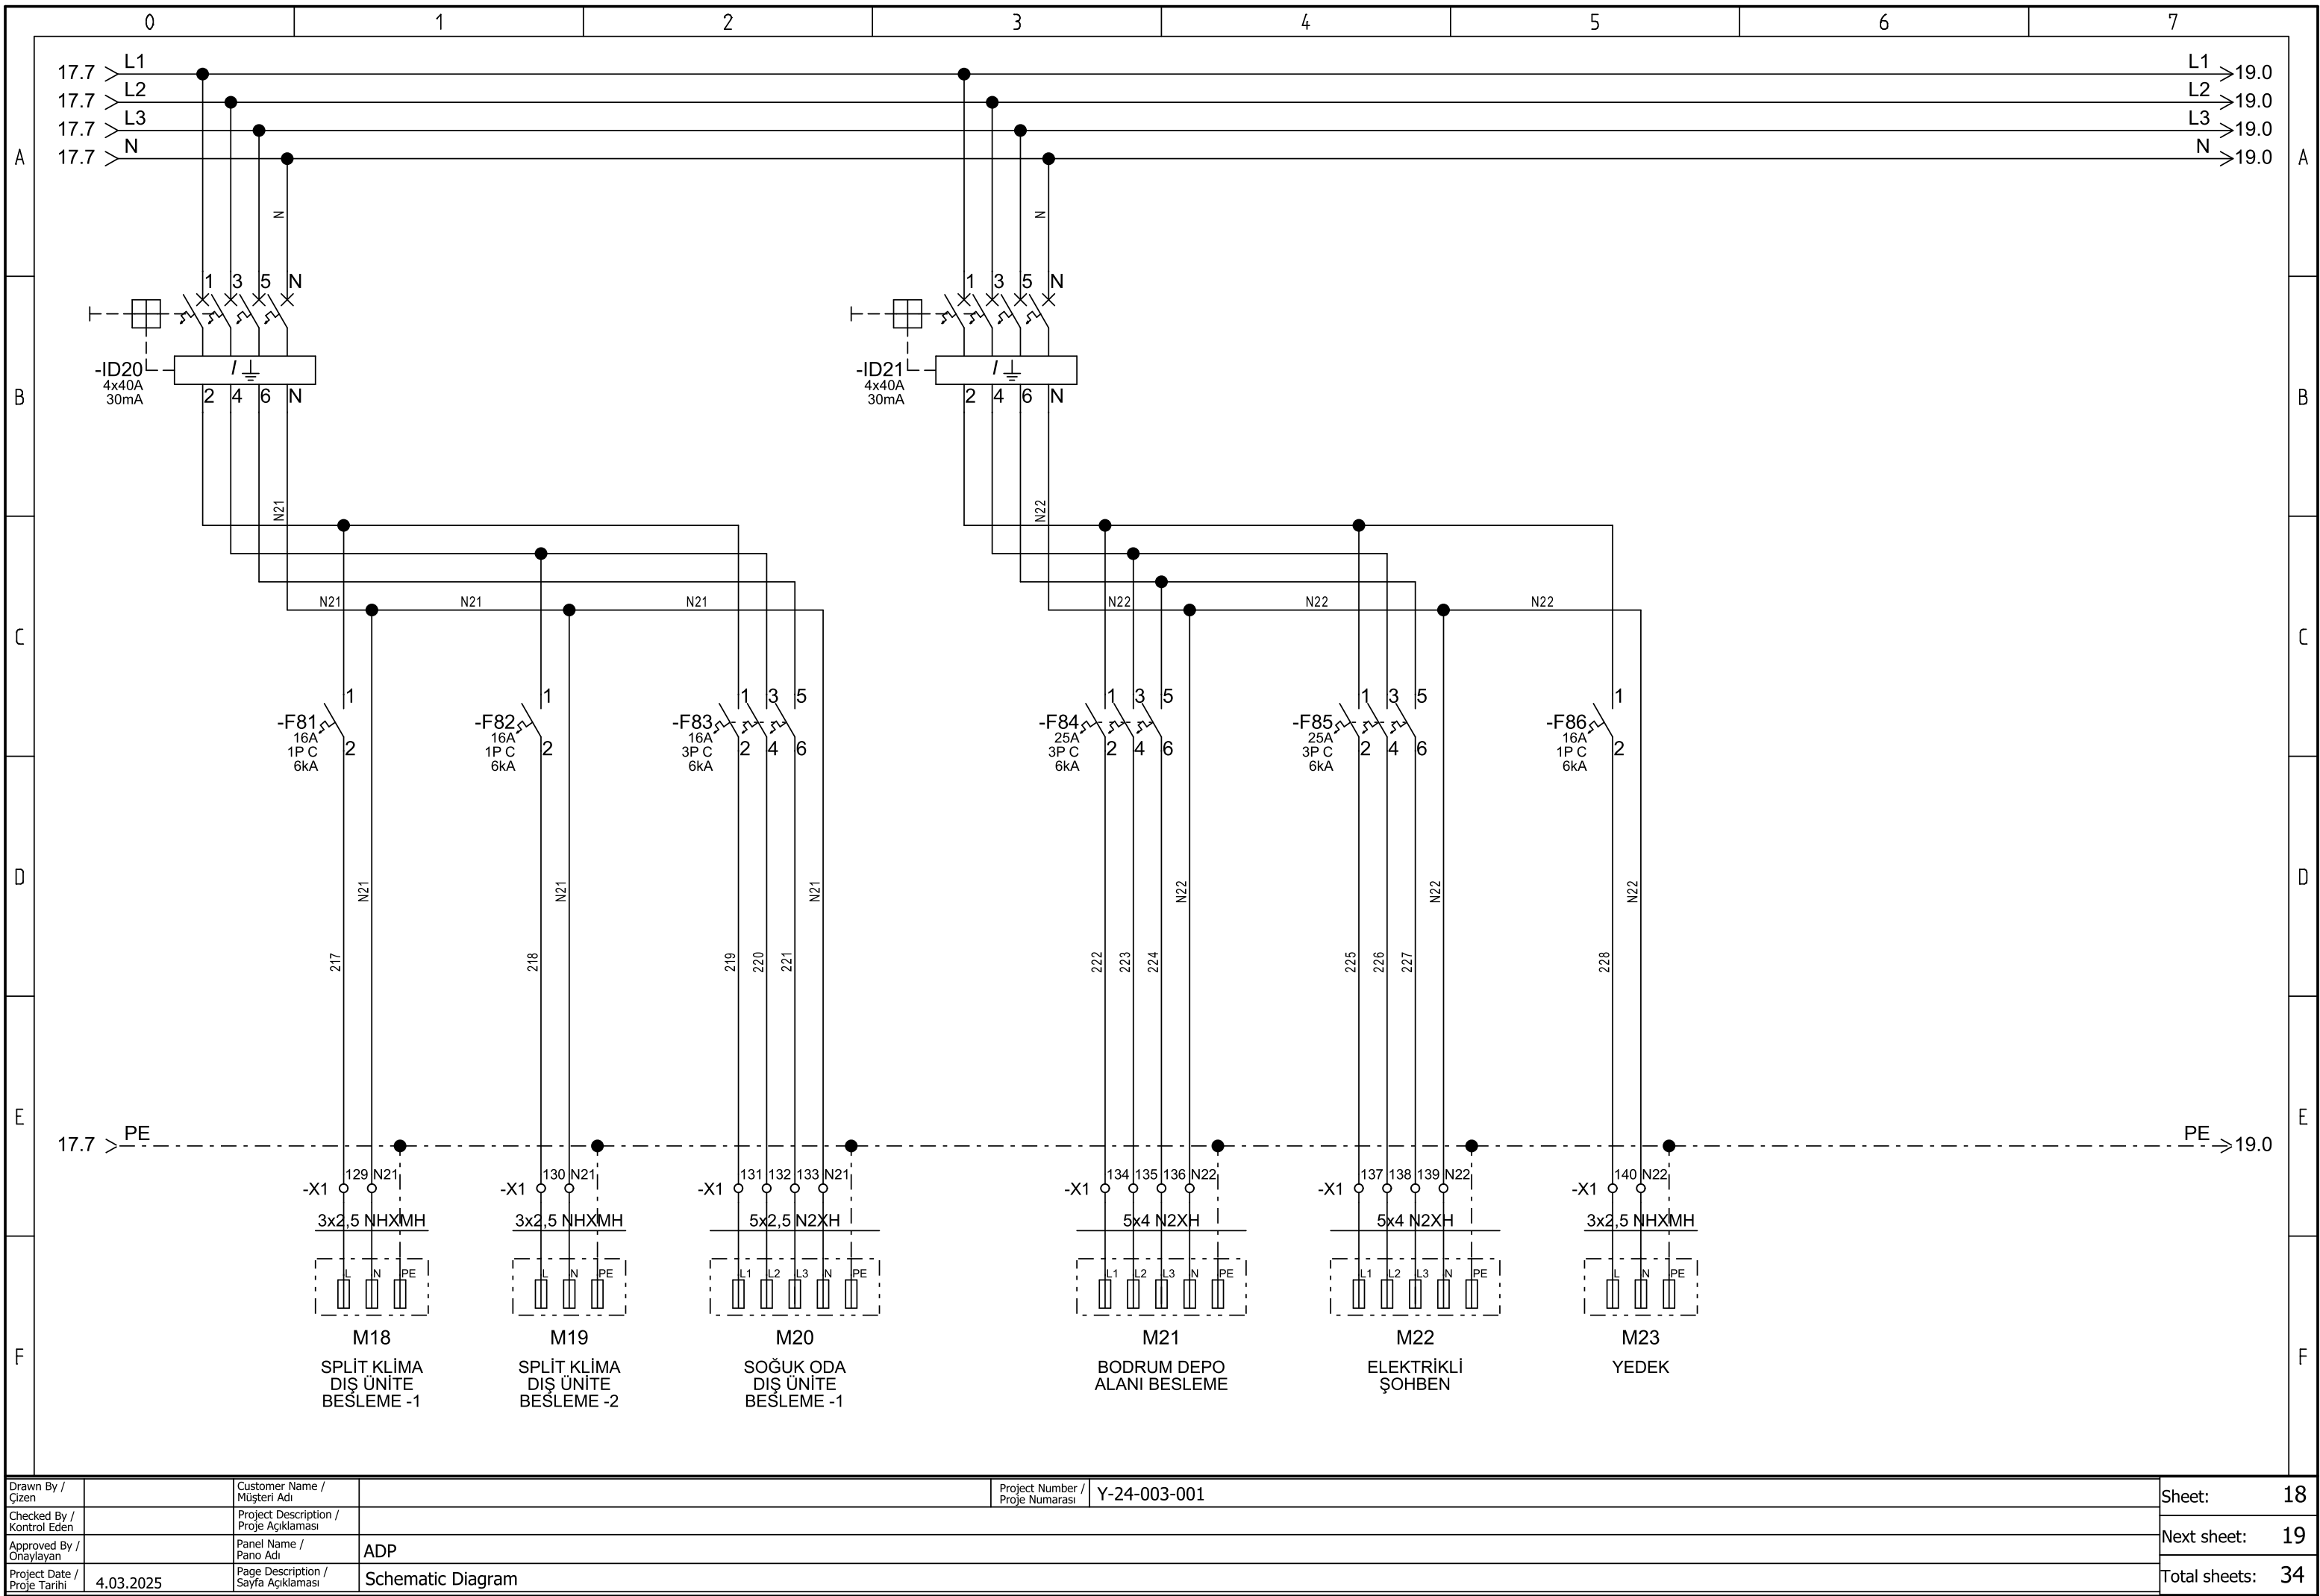


Drawn By / Çizen		Customer Name / Müşteri Adı		Project Number / Proje Numarası	Y-24-003-001	Sheet:	18
Checked By / Kontrol Eden		Project Description / Proje Açıklaması				Next sheet:	19
Approved By / Onaylayan		Panel Name / Pano Adı	ADP			Total sheets:	34
Project Date / Proje Tarihi	4.03.2025	Page Description / Sayfa Açıklaması	Schematic Diagram				

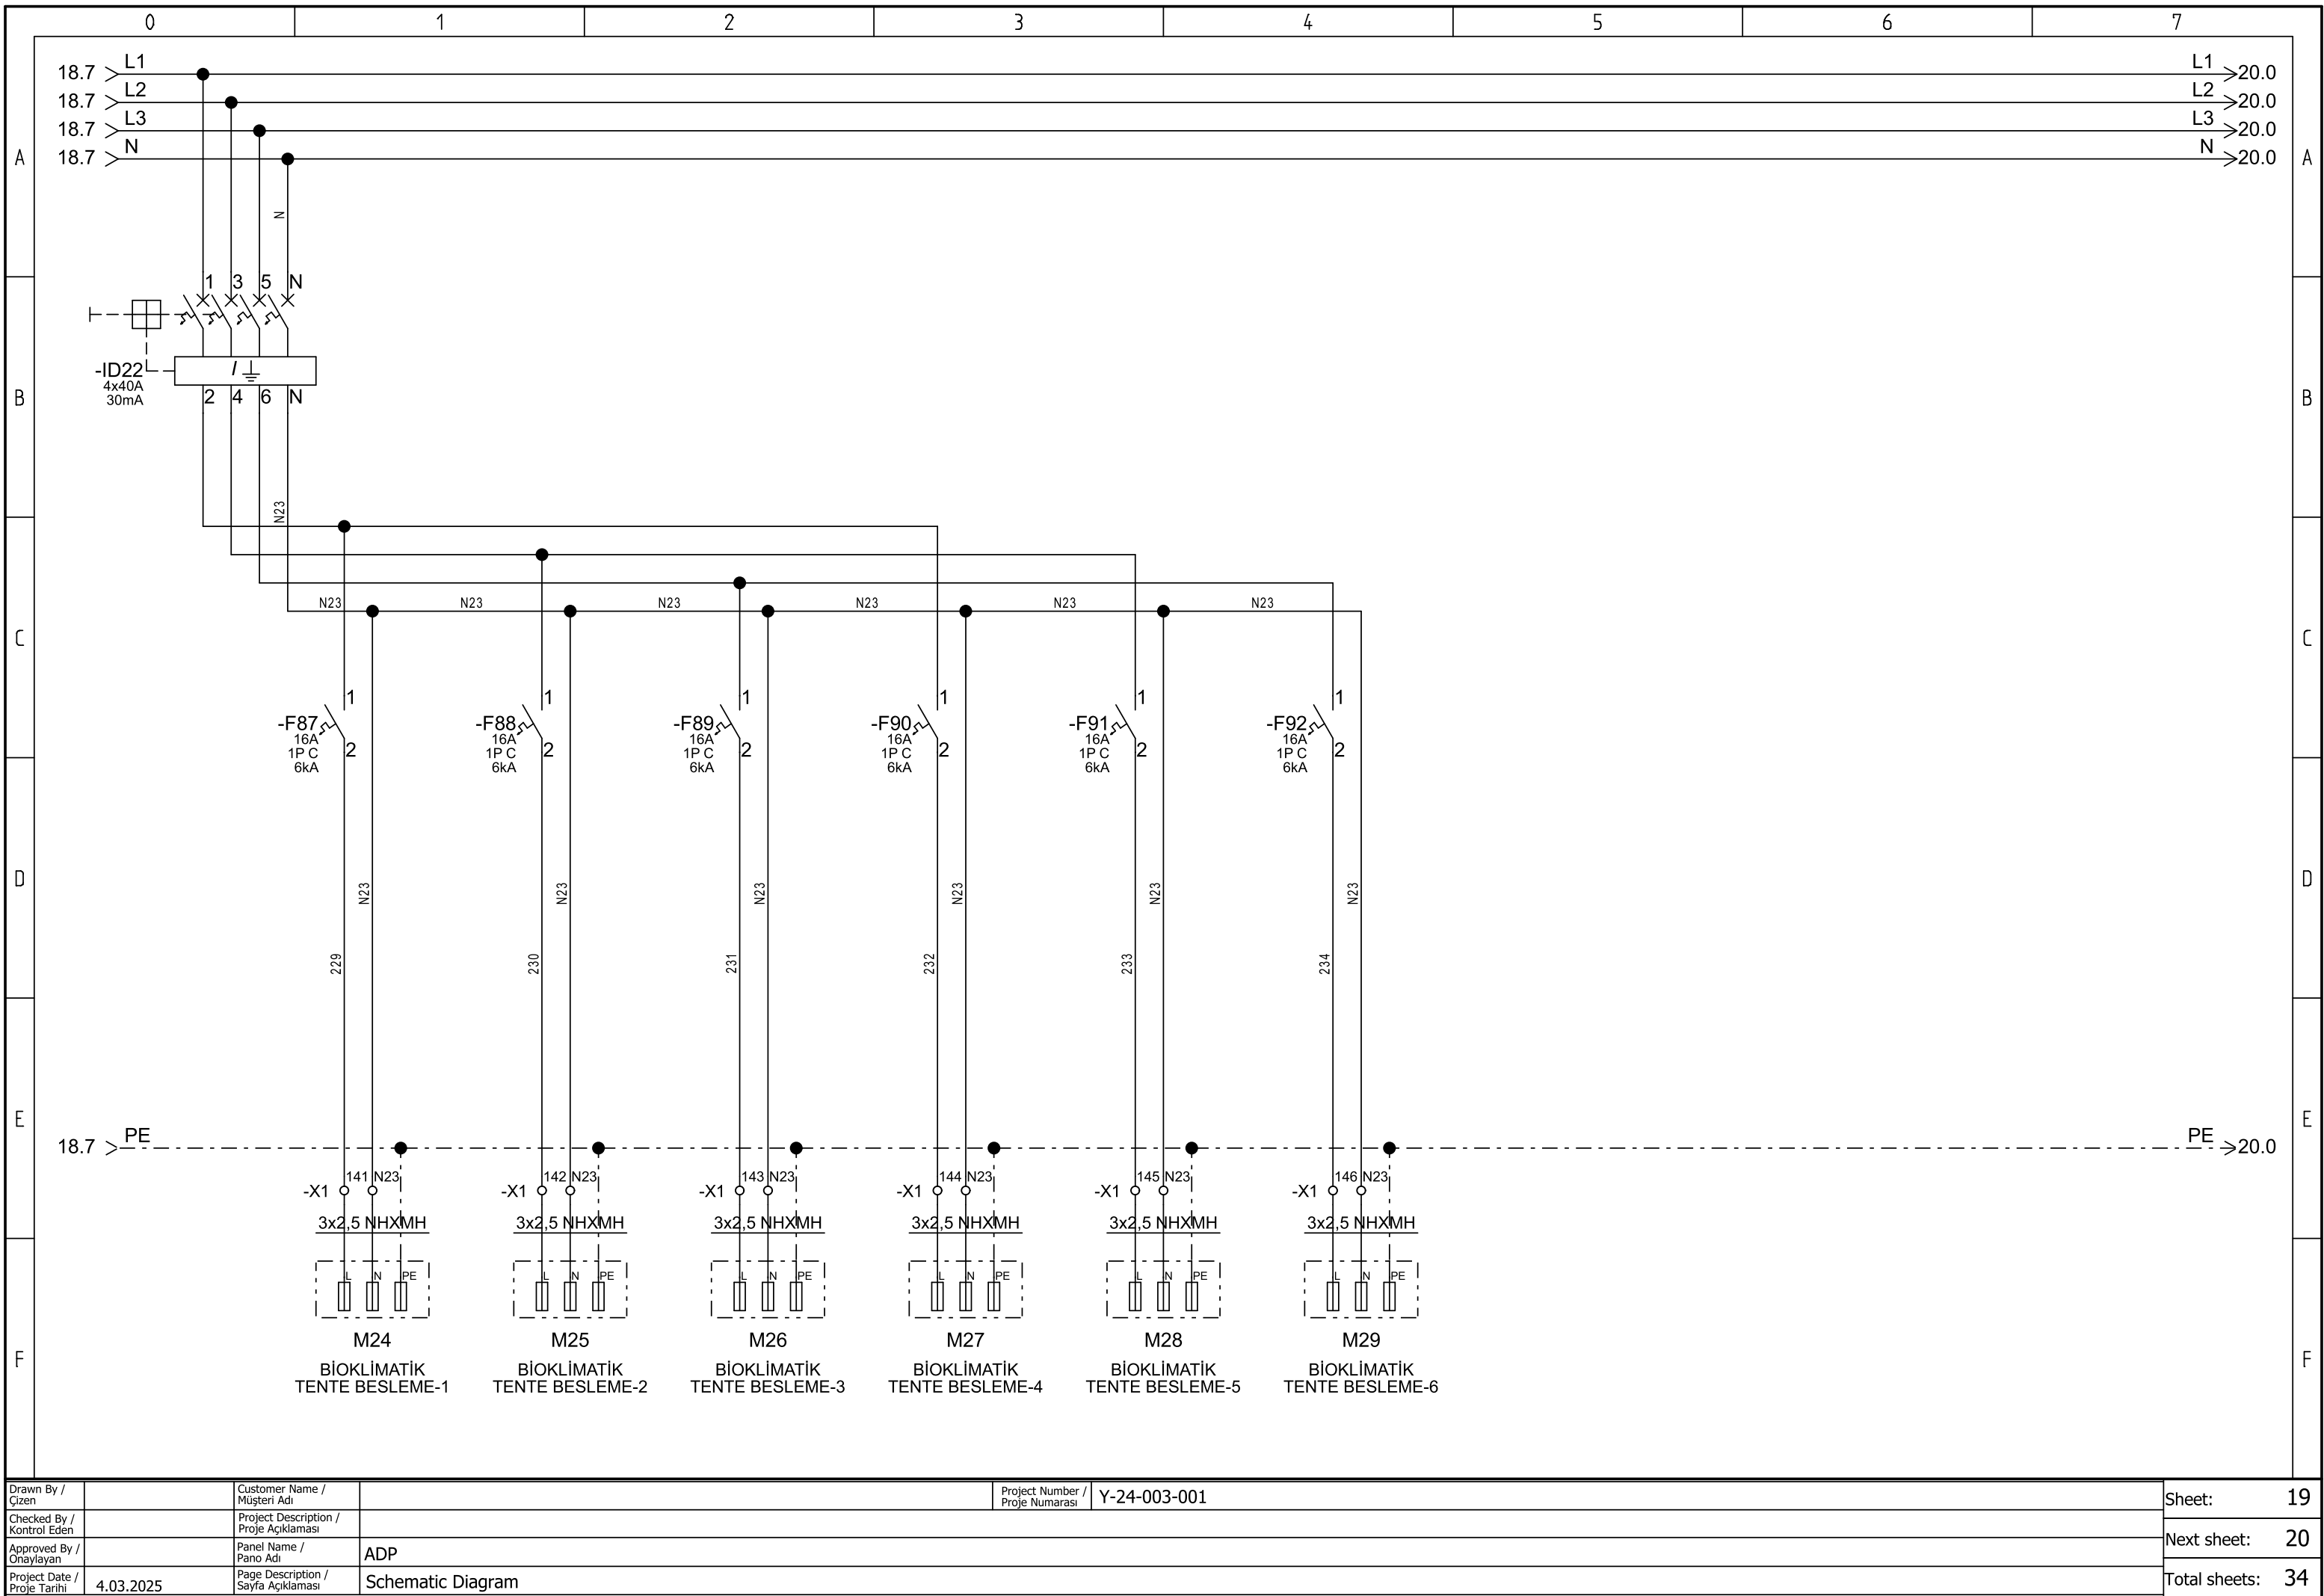


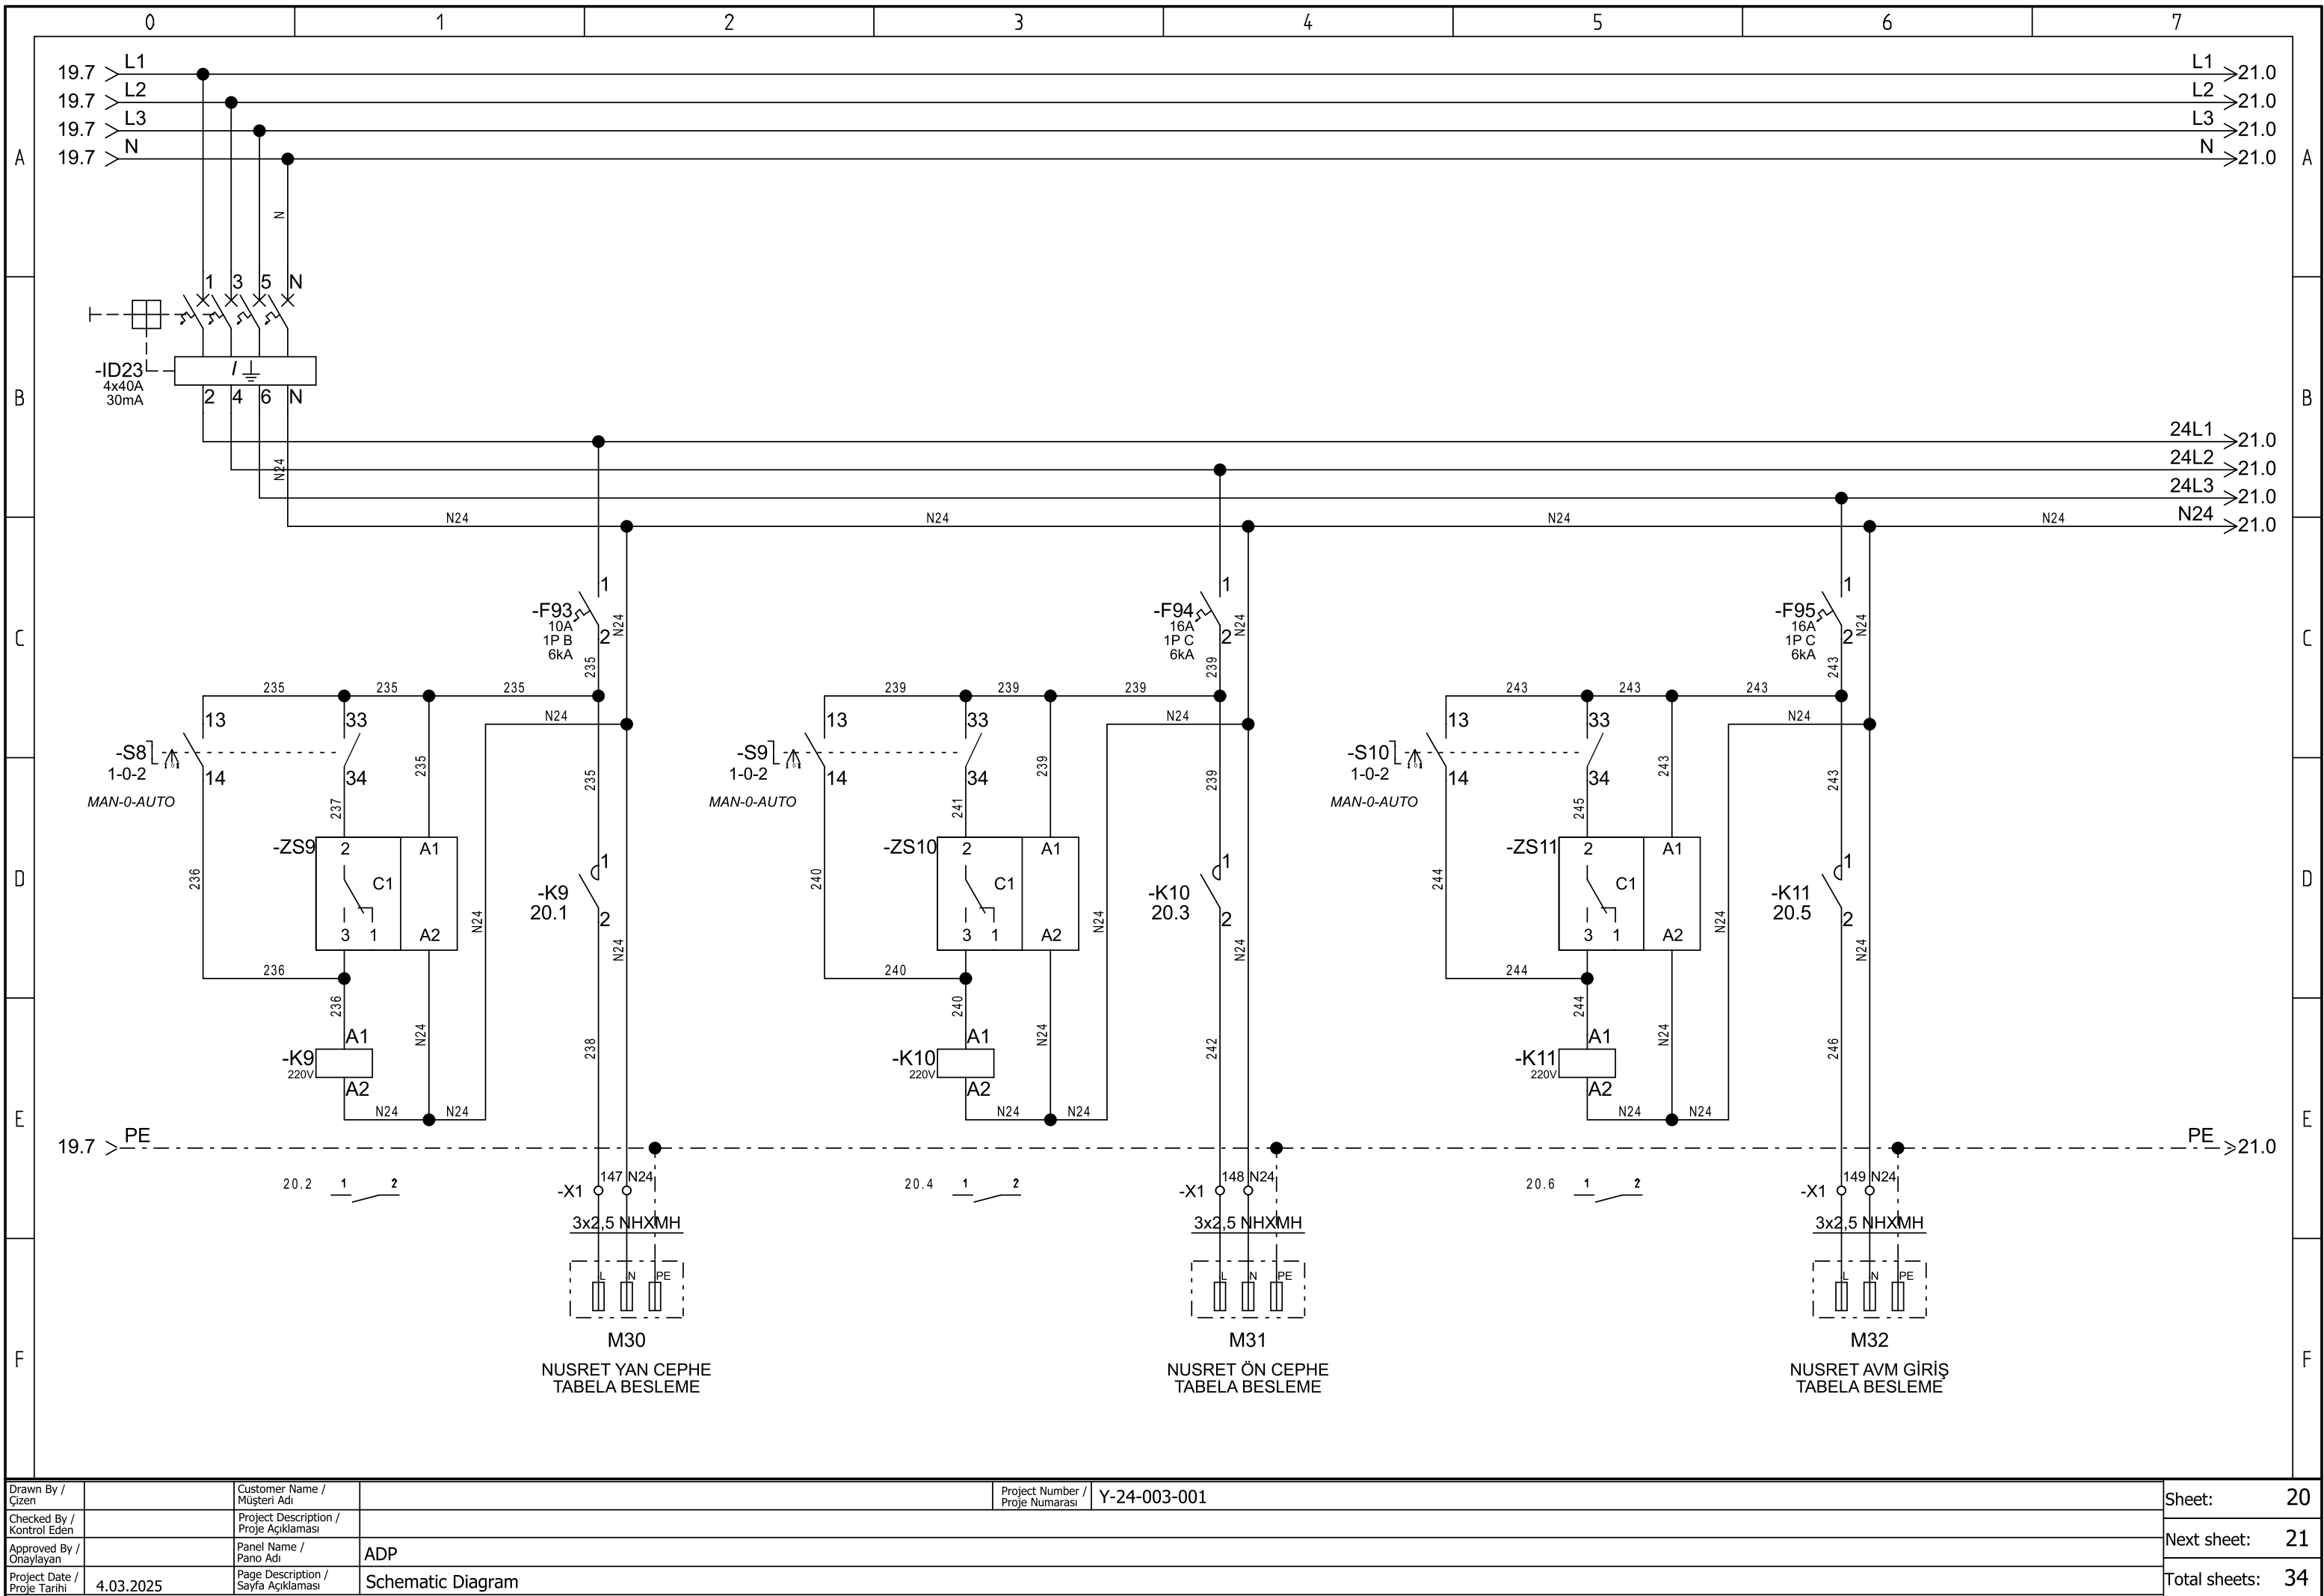


Drawn By / Çizen		Customer Name / Müşteri Adı		Project Number / Proje Numarası	Y-24-003-001	Sheet:	20
Checked By / Kontrol Eden		Project Description / Proje Açıklaması				Next sheet:	21
Approved By / Onaylayan		Panel Name / Pano Adı	ADP			Total sheets:	34
Project Date / Proje Tarihi	4.03.2025	Page Description / Sayfa Açıklaması	Schematic Diagram				

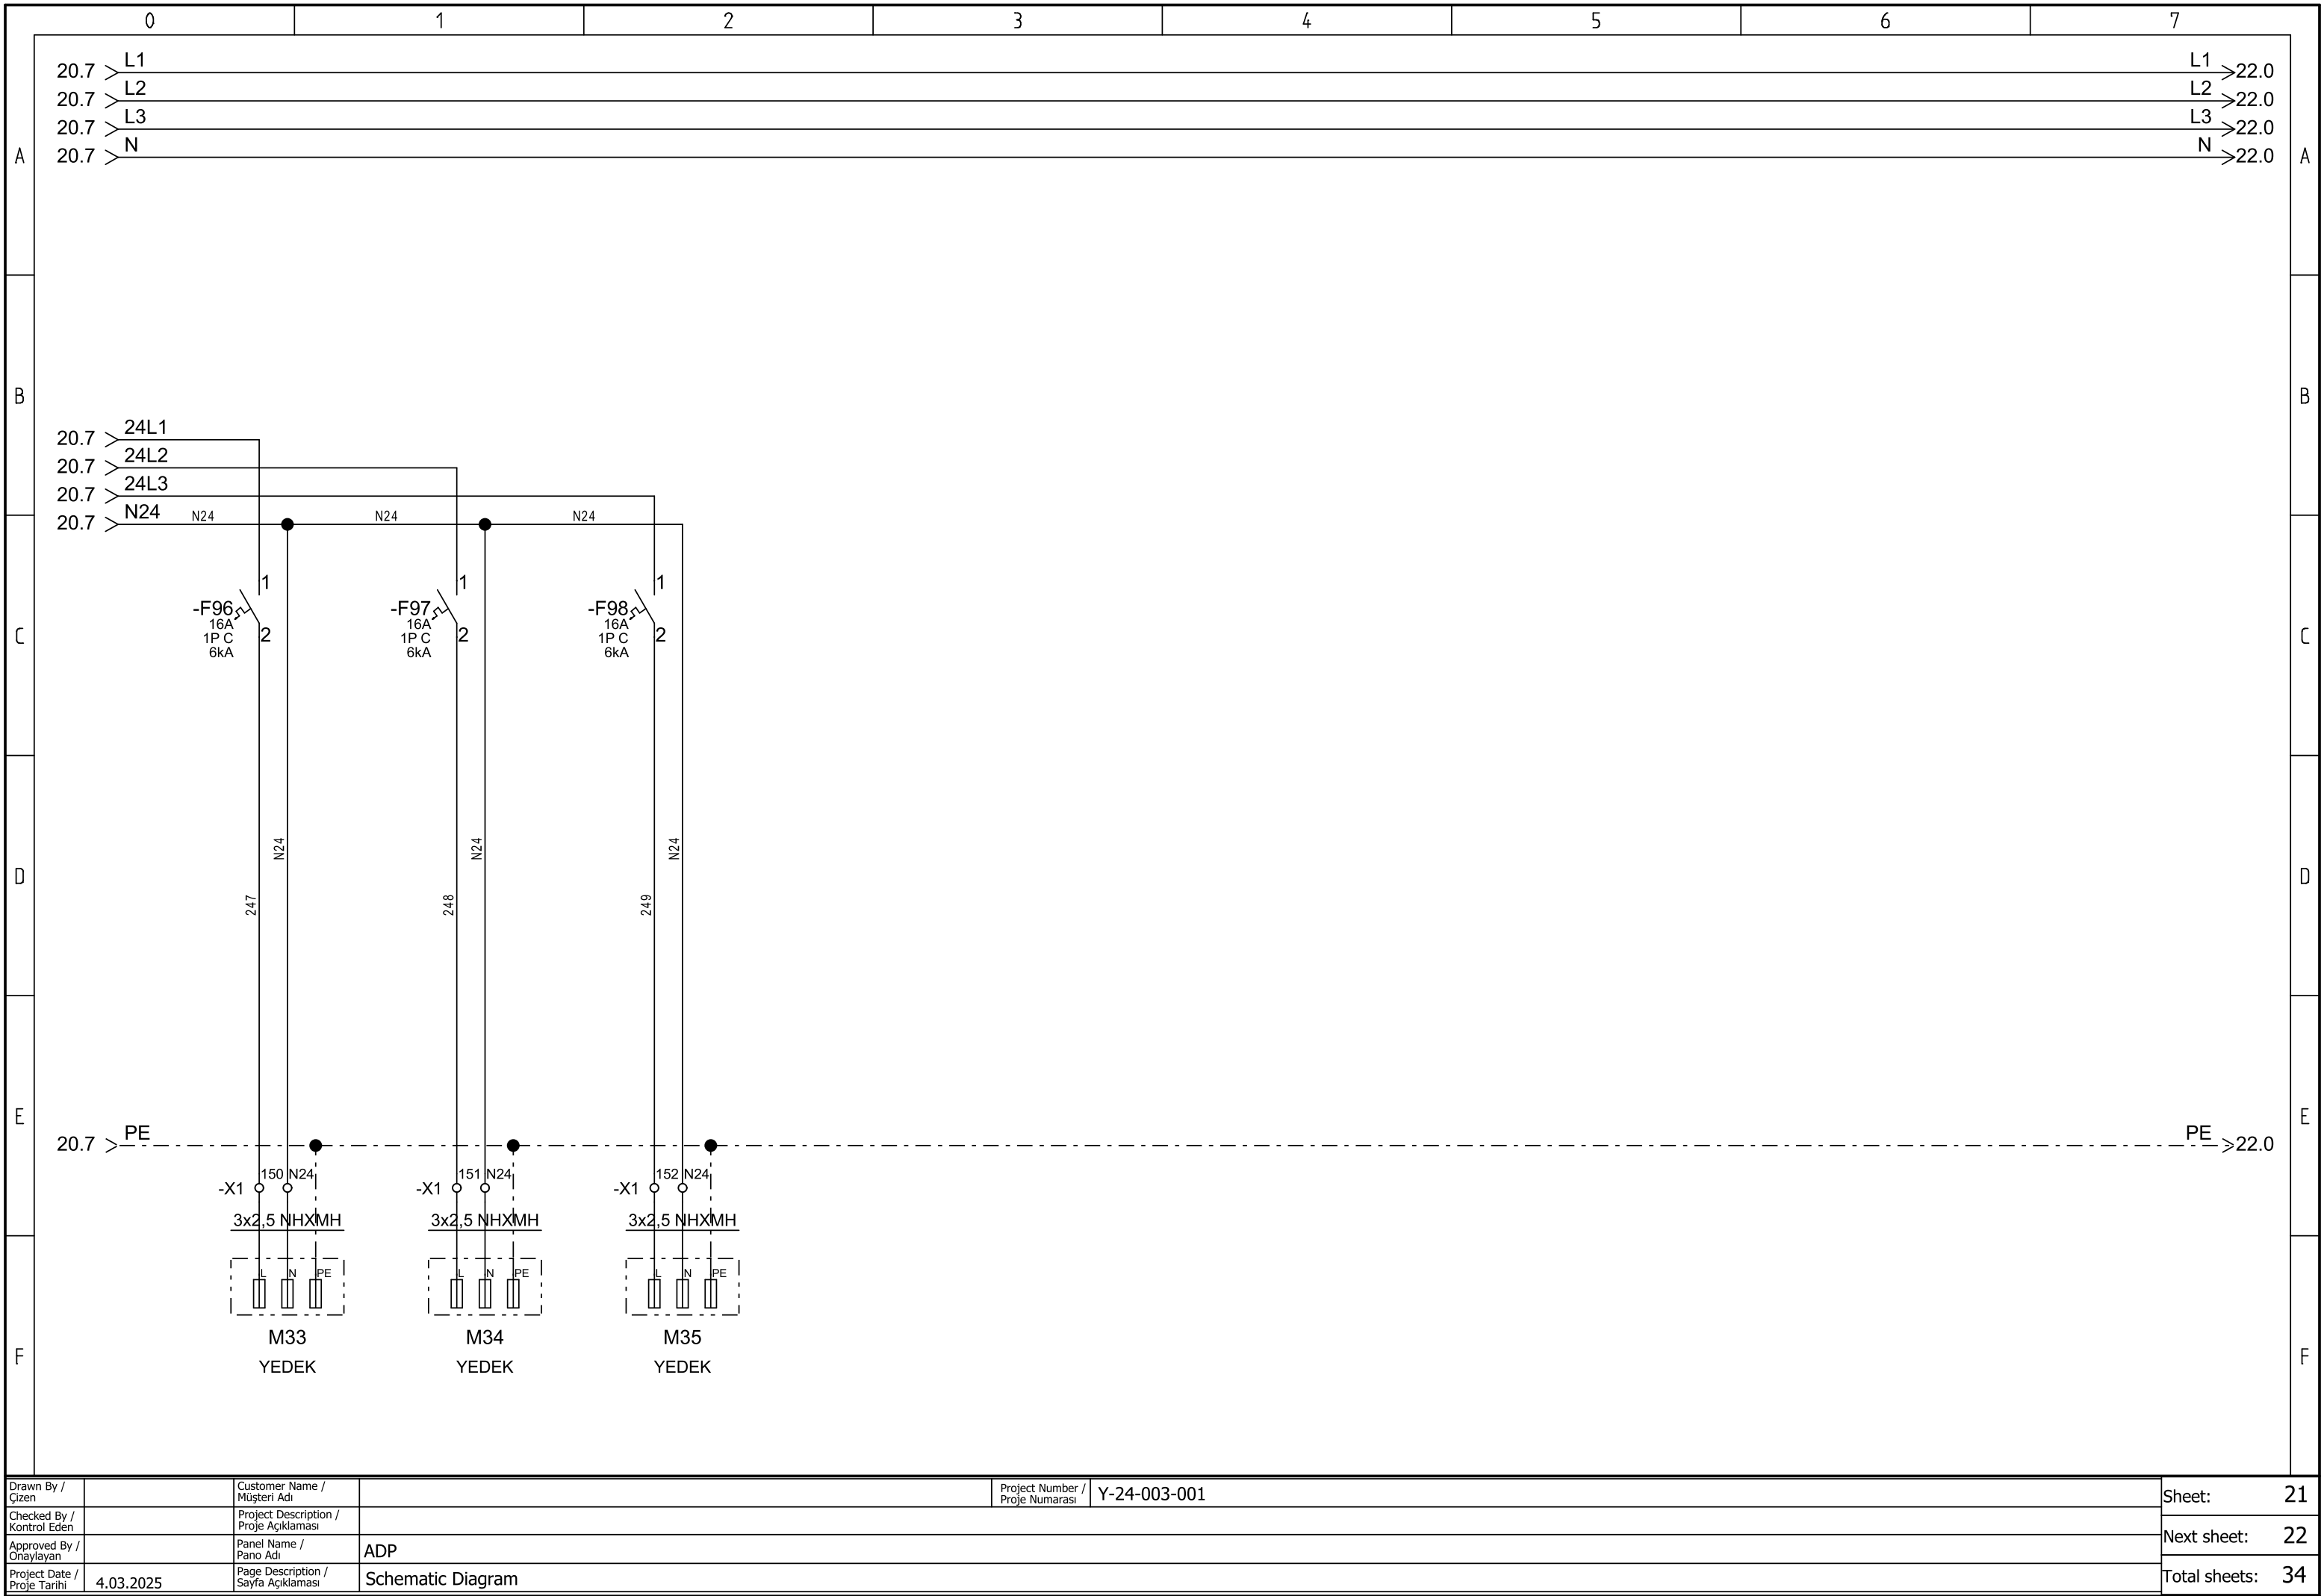


Drawn By / Çizen		Customer Name / Müşteri Adı		Project Number / Proje Numarası	Y-24-003-001	Sheet:	21
Checked By / Kontrol Eden		Project Description / Proje Açıklaması				Next sheet:	22
Approved By / Onaylayan		Panel Name / Pano Adı	ADP			Total sheets:	34
Project Date / Proje Tarihi	4.03.2025	Page Description / Sayfa Açıklaması	Schematic Diagram				

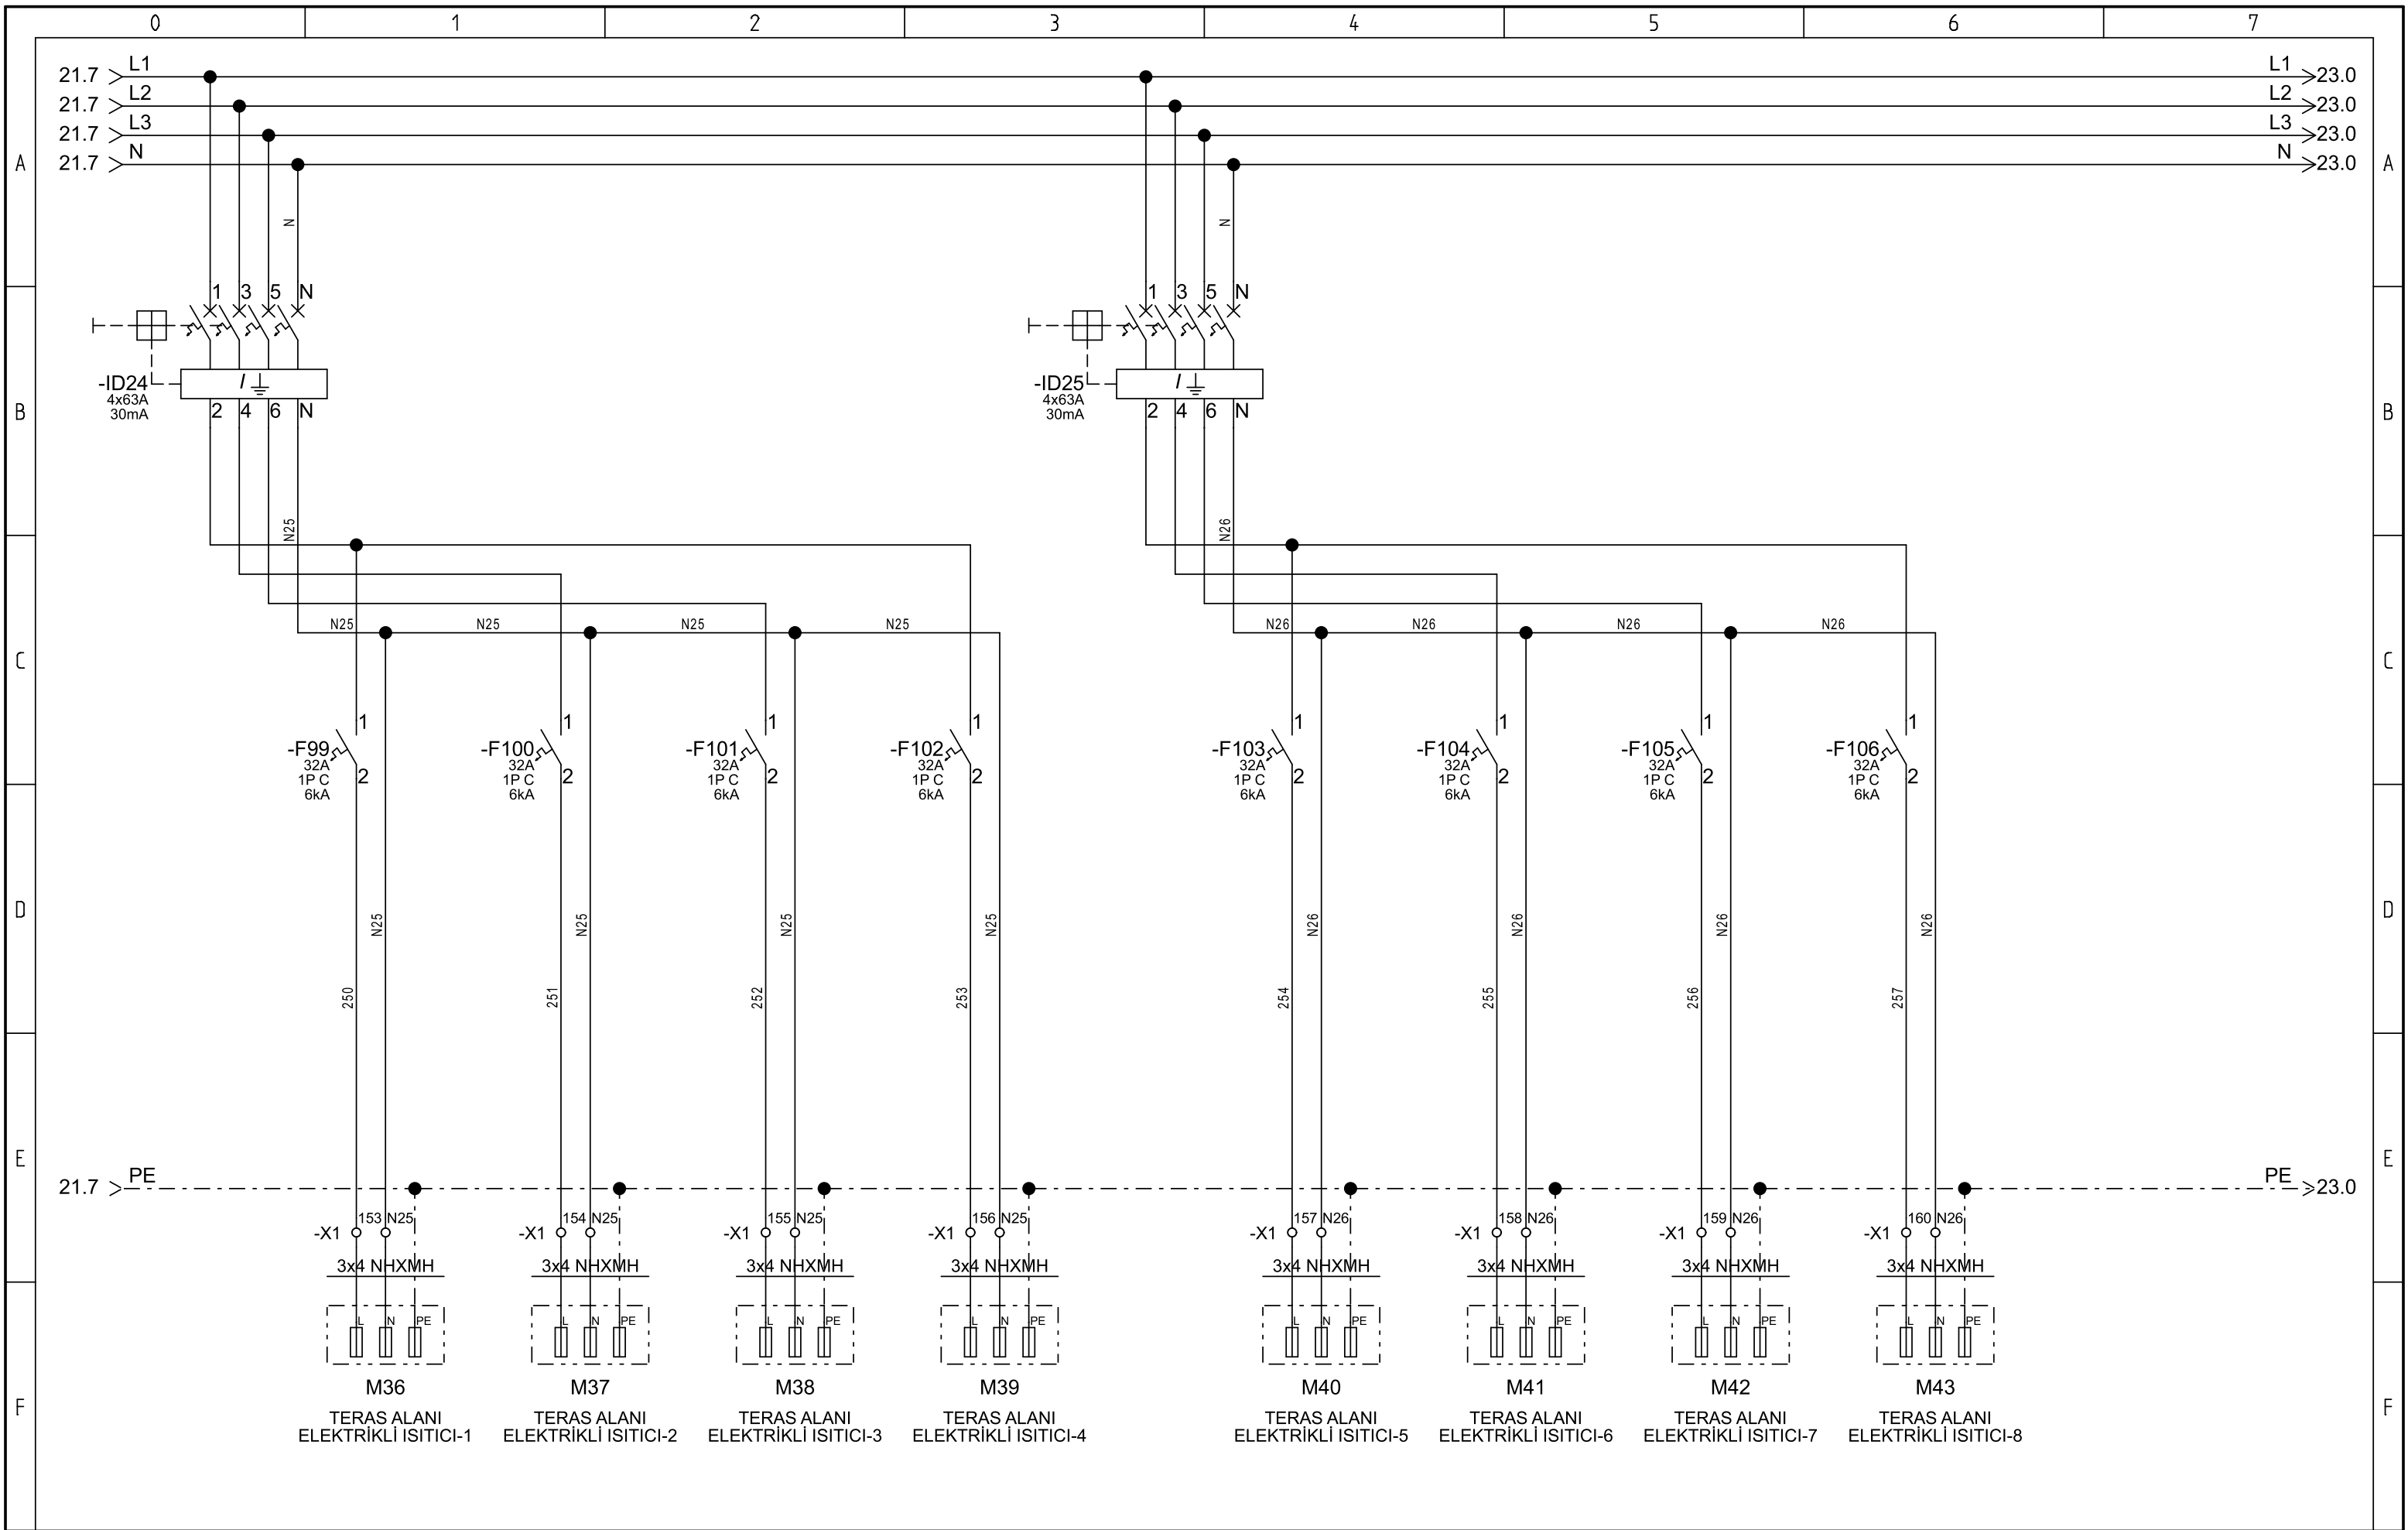


Drawn By / Çizen		Customer Name / Müşteri Adı		Project Number / Proje Numarası	Y-24-003-001	Sheet:	22
Checked By / Kontrol Eden		Project Description / Proje Açıklaması				Next sheet:	23
Approved By / Onaylayan		Panel Name / Pano Adı	ADP			Total sheets:	34
Project Date / Proje Tarihi	4.03.2025	Page Description / Sayfa Açıklaması	Schematic Diagram				

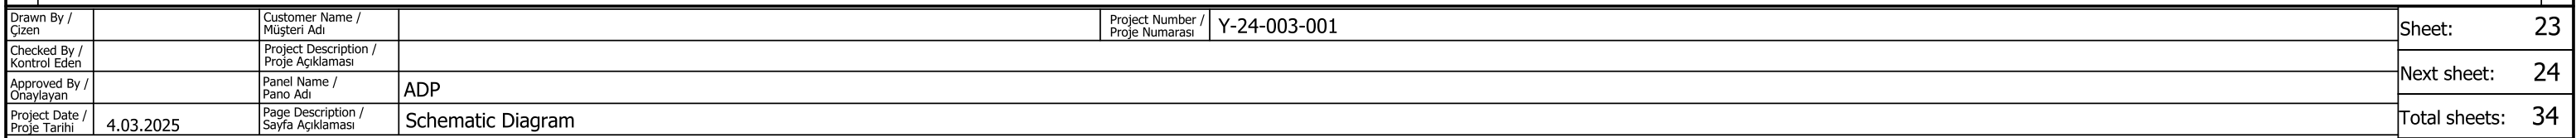


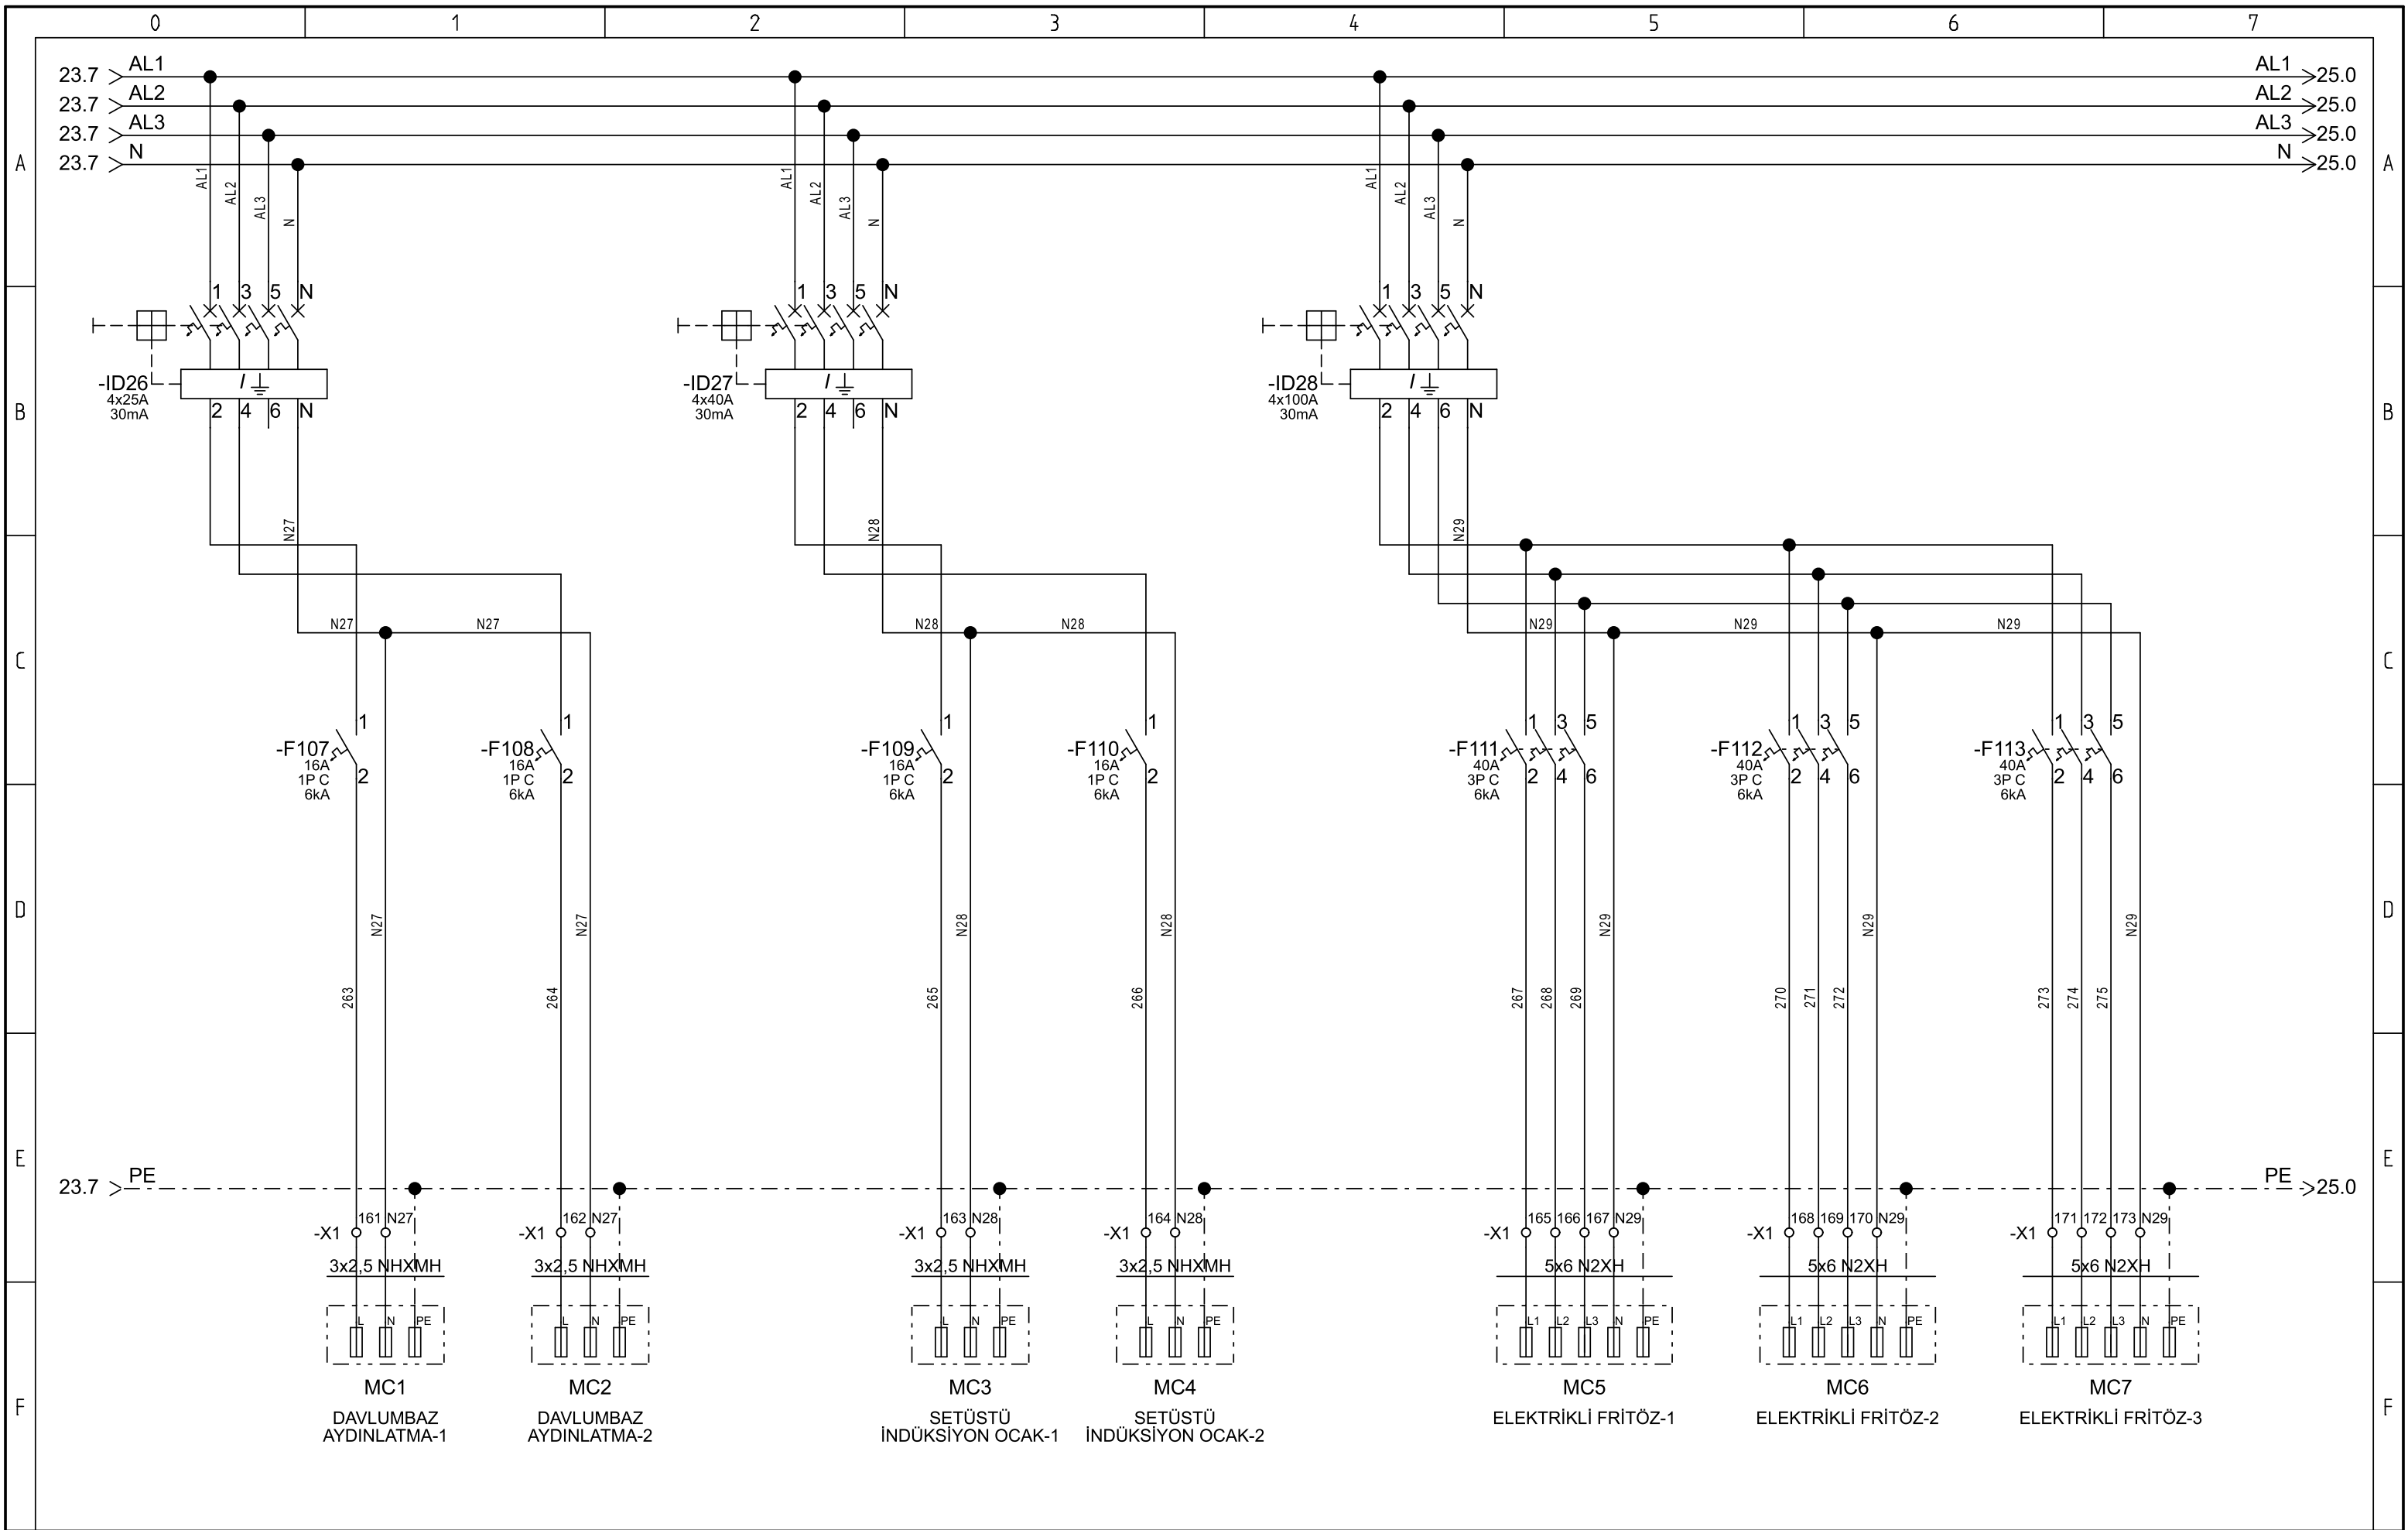


Drawn By / Çizen		Customer Name / Müşteri Adı		Project Number / Proje Numarası	Y-24-003-001	Sheet:	24
Checked By / Kontrol Eden		Project Description / Proje Açıklaması				Next sheet:	25
Approved By / Onaylayan		Panel Name / Pano Adı	ADP			Total sheets:	34
Project Date / Proje Tarihi	4.03.2025	Page Description / Sayfa Açıklaması	Schematic Diagram				

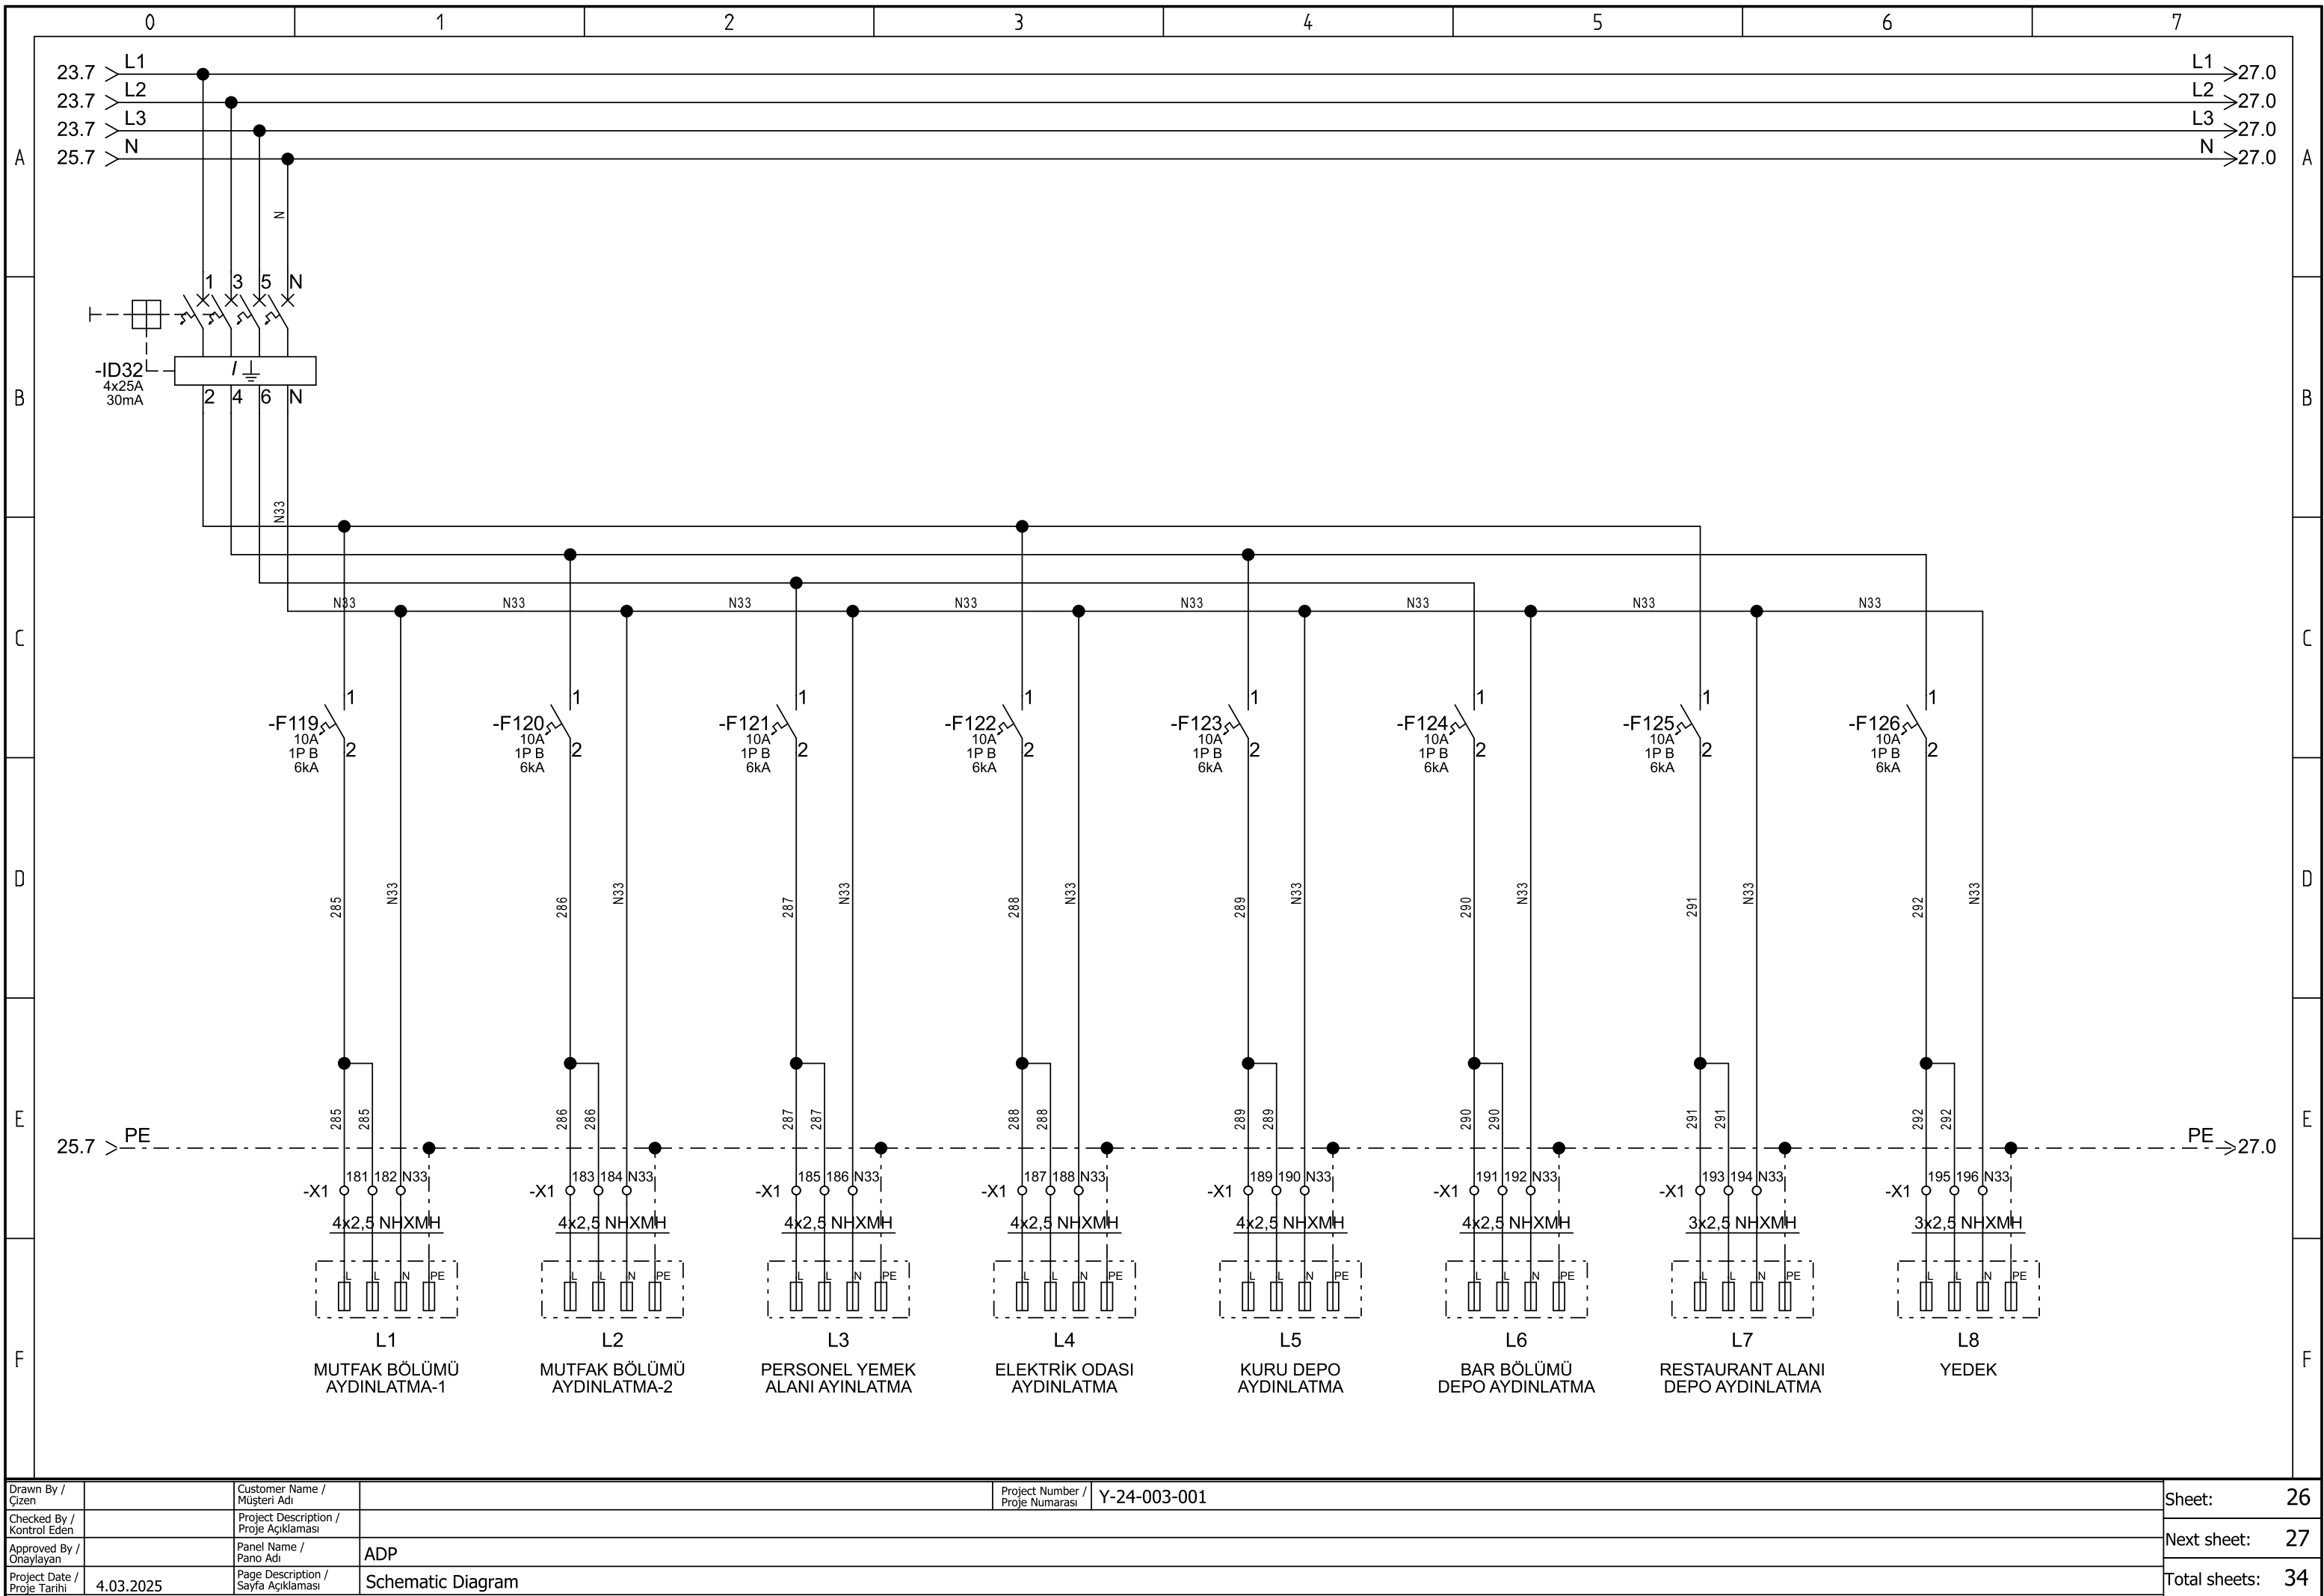


Drawn By / Çizen		Customer Name / Müşteri Adı		Project Number / Proje Numarası	Y-24-003-001	Sheet:	26
Checked By / Kontrol Eden		Project Description / Proje Açıklaması				Next sheet:	27
Approved By / Onaylayan		Panel Name / Pano Adı	ADP			Total sheets:	34
Project Date / Proje Tarihi	4.03.2025	Page Description / Sayfa Açıklaması	Schematic Diagram				

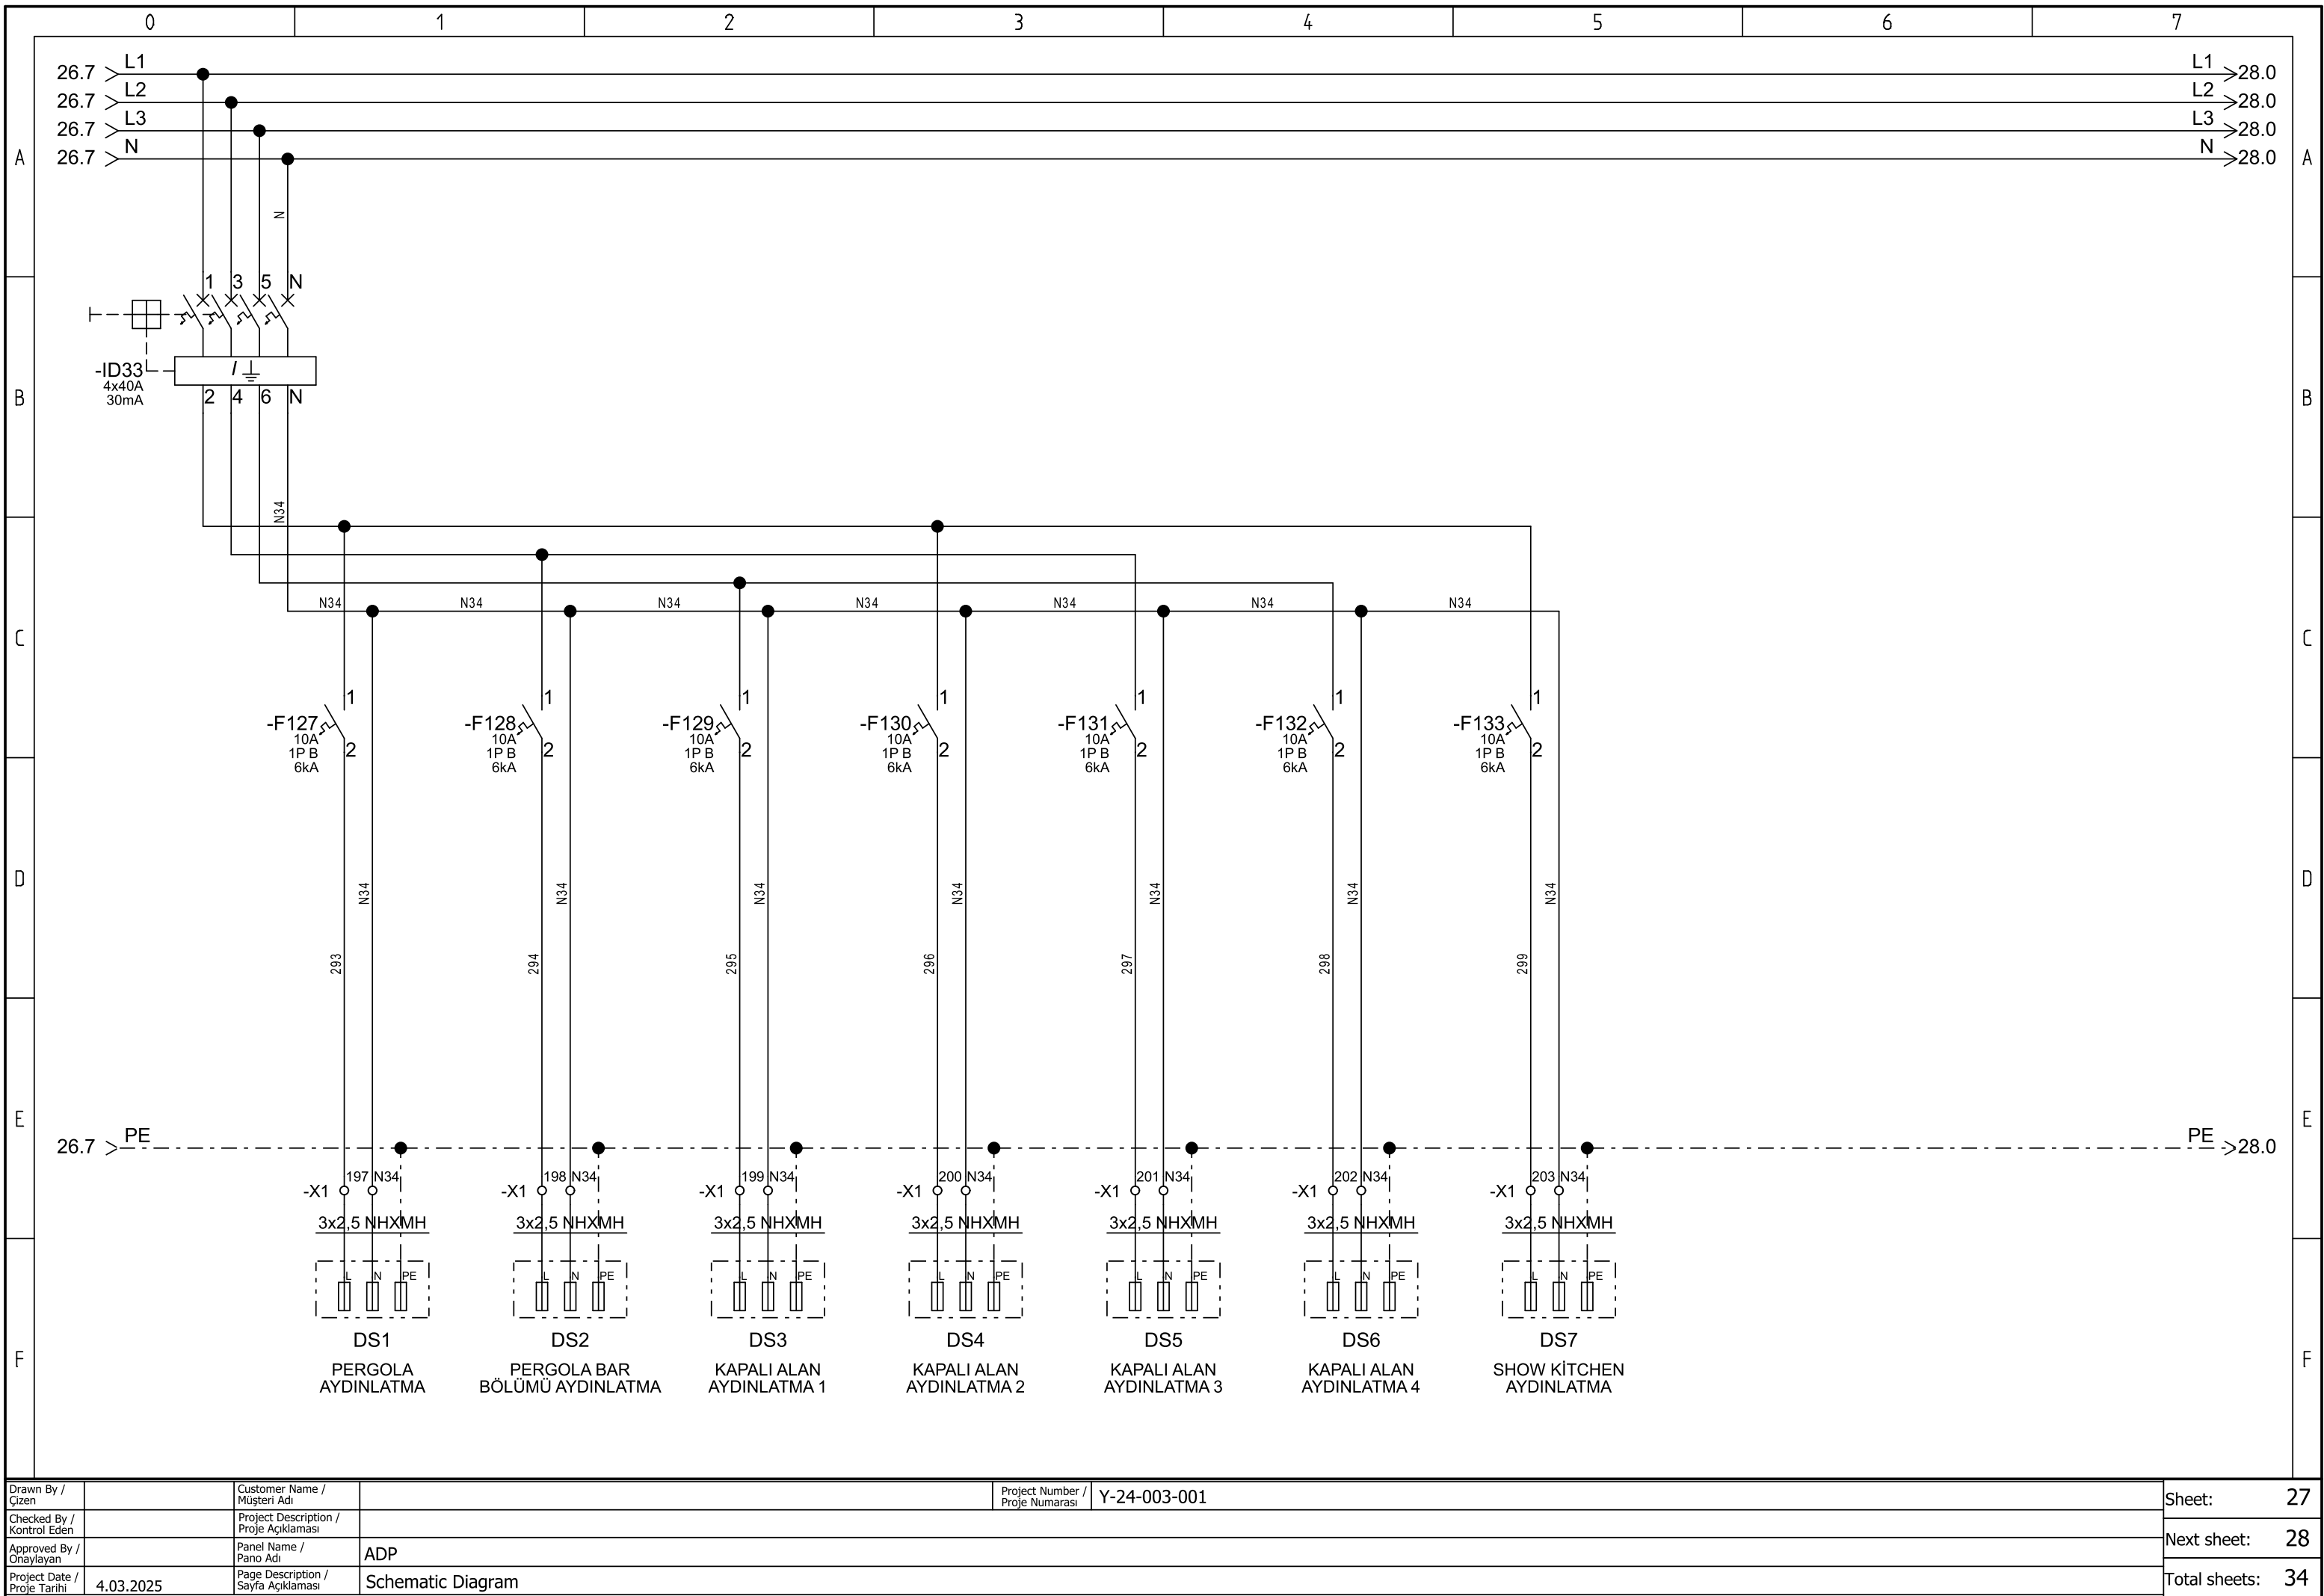


Drawn By / Çizen		Customer Name / Müşteri Adı		Project Number / Proje Numarası	Y-24-003-001	Sheet:	27
Checked By / Kontrol Eden		Project Description / Proje Açıklaması				Next sheet:	28
Approved By / Onaylayan		Panel Name / Pano Adı	ADP			Total sheets:	34
Project Date / Proje Tarihi	4.03.2025	Page Description / Sayfa Açıklaması	Schematic Diagram				

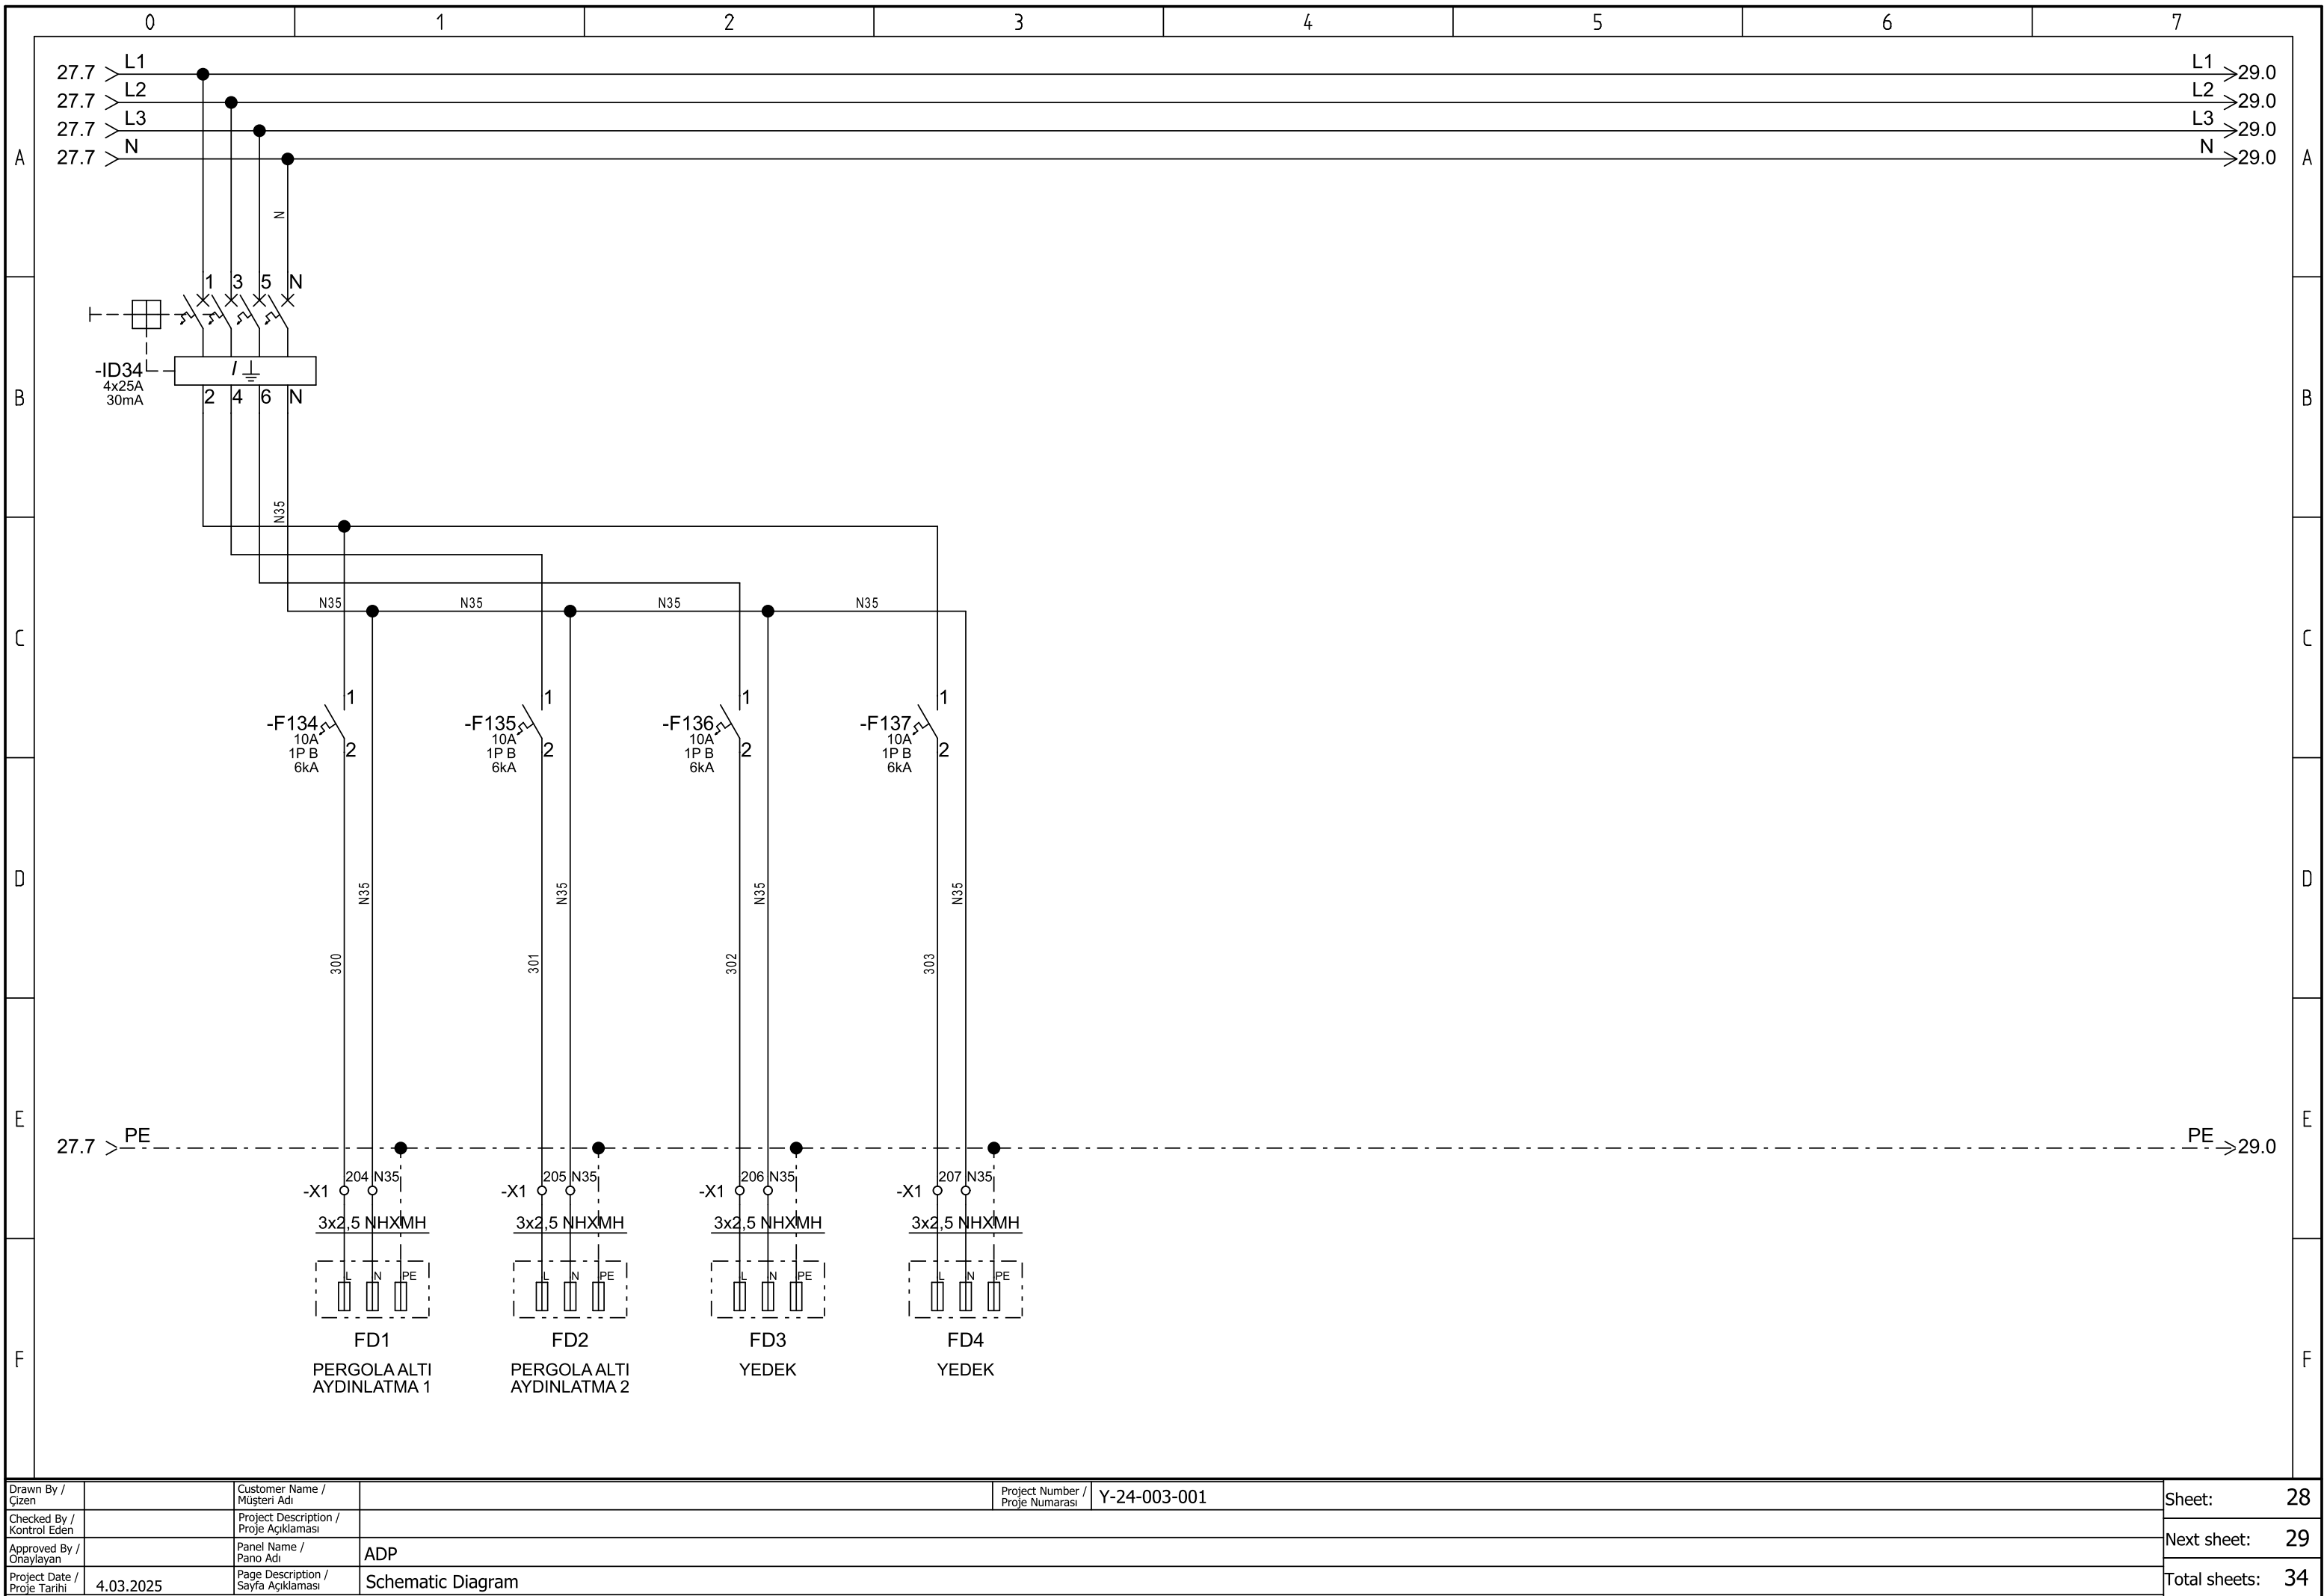

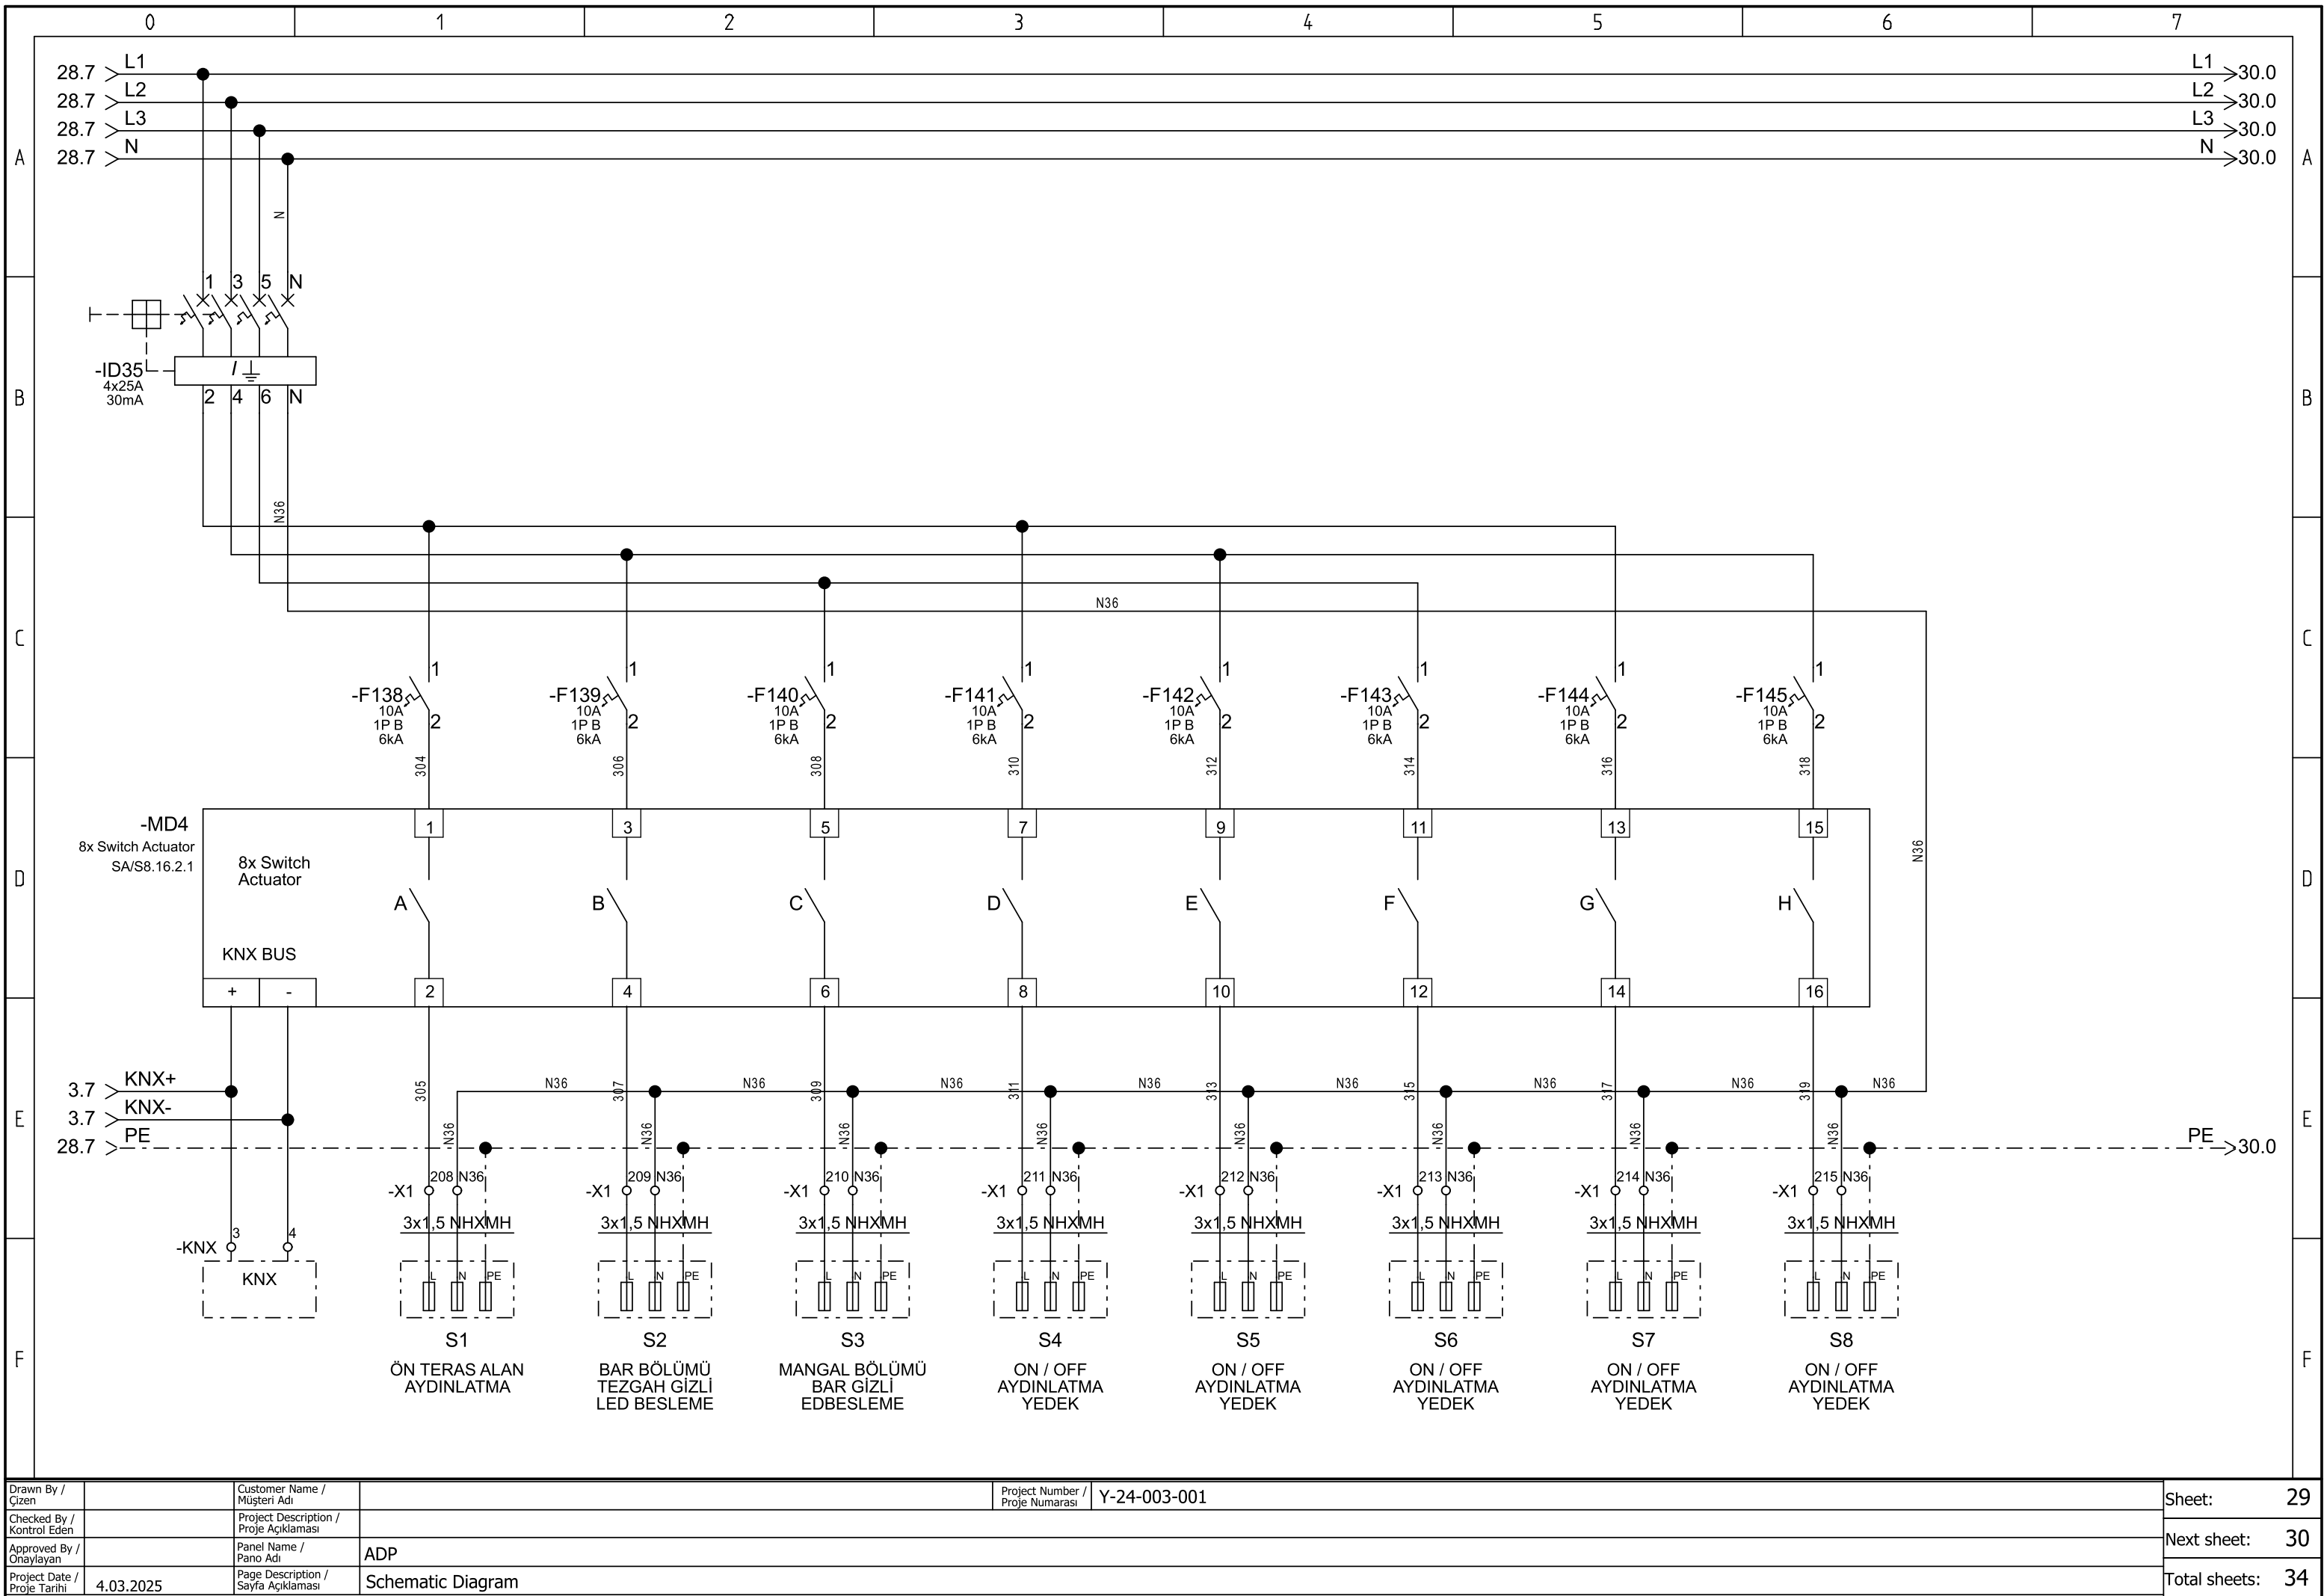

Drawn By / Çizen		Customer Name / Müşteri Adı		Project Number / Proje Numarası	Y-24-003-001	Sheet:	29
Checked By / Kontrol Eden		Project Description / Proje Açıklaması				Next sheet:	30
Approved By / Onaylayan		Panel Name / Pano Adı	ADP			Total sheets:	34
Project Date / Proje Tarihi	4.03.2025	Page Description / Sayfa Açıklaması	Schematic Diagram				

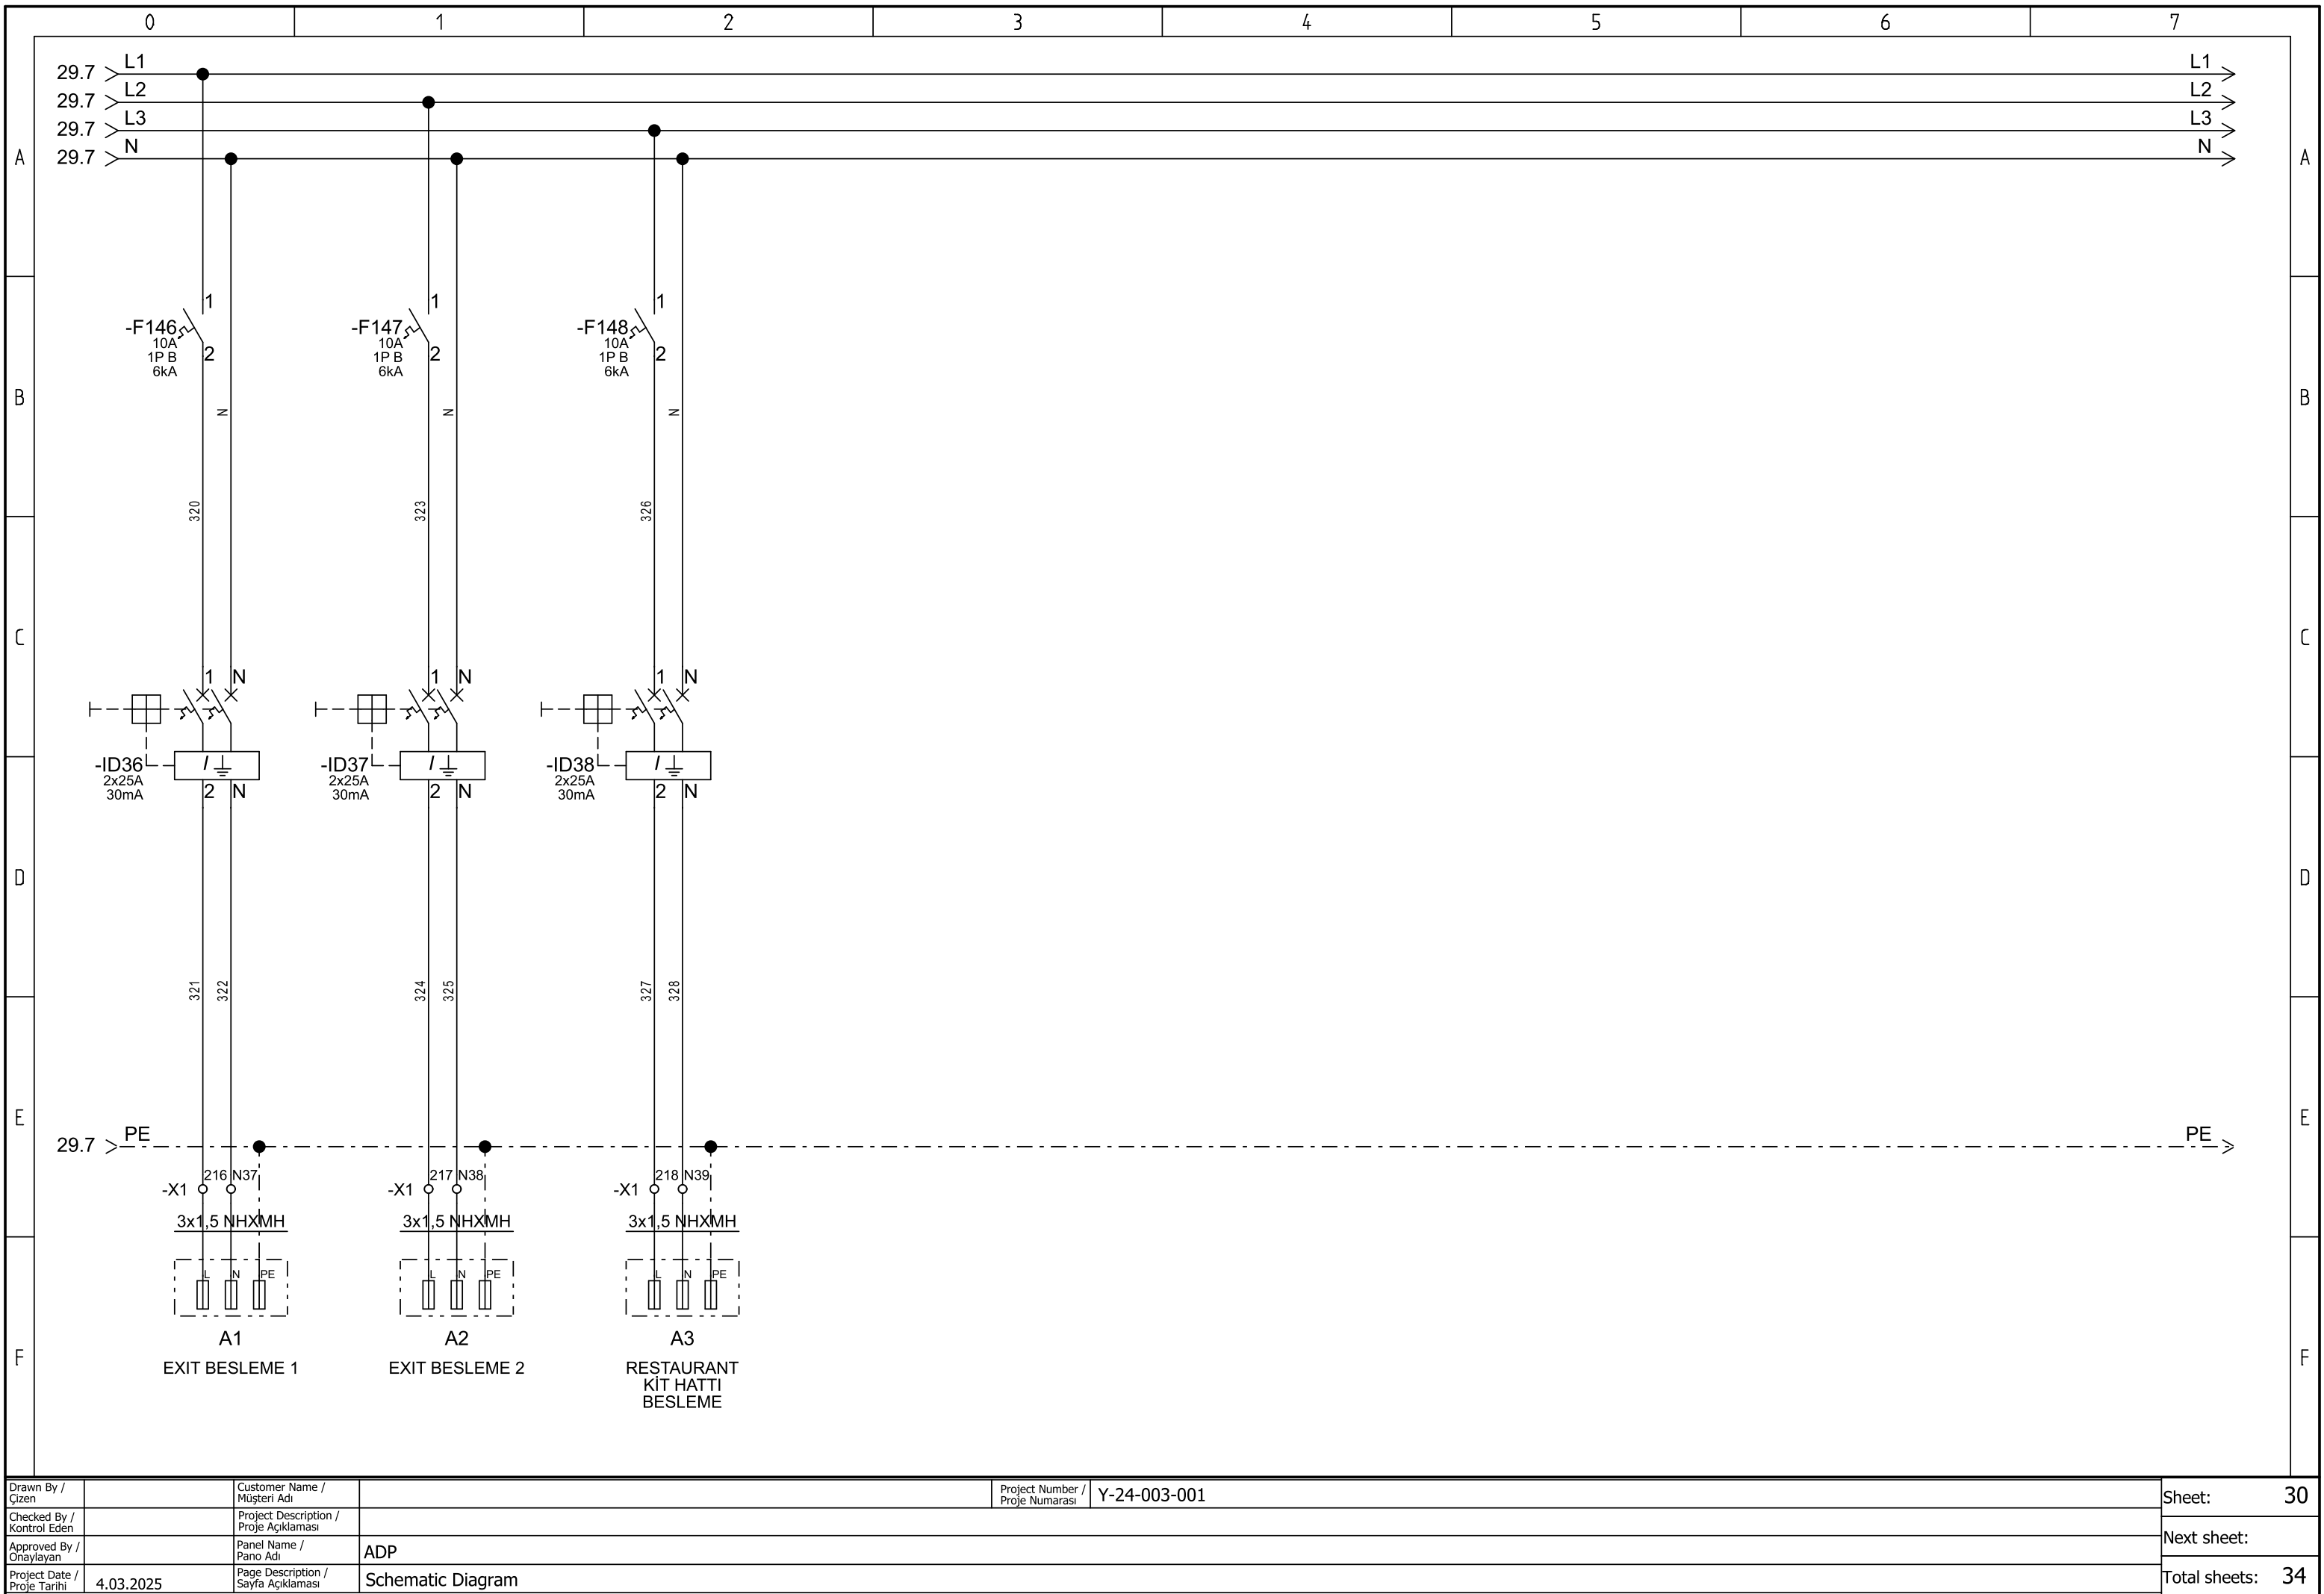

Drawn By / Çizen		Customer Name / Müşteri Adı		Project Number / Proje Numarası	Y-24-003-001	Sheet:	30
Checked By / Kontrol Eden		Project Description / Proje Açıklaması				Next sheet:	
Approved By / Onaylayan		Panel Name / Pano Adı	ADP			Total sheets:	34
Project Date / Proje Tarihi	4.03.2025	Page Description / Sayfa Açıklaması	Schematic Diagram				