


LEJANT

- Mimari — mevcut duvar (korunuyor)
- Mimari — yeni alçıpan bölme
- Mimari — cephe doğraması
- Mimari — kapı ve açılım
- Mimari — spor ekipmanı (işverence temin)
- Mimari — sabit mobilya
- Mimari — mahal adı ve alan

GENEL NOTLAR

- Mimari altlık — mevcut duvar korunur.
- Kırmızı: yeni alçıpan bölme.
- Ölçüler raster paftadan (+/-%3).

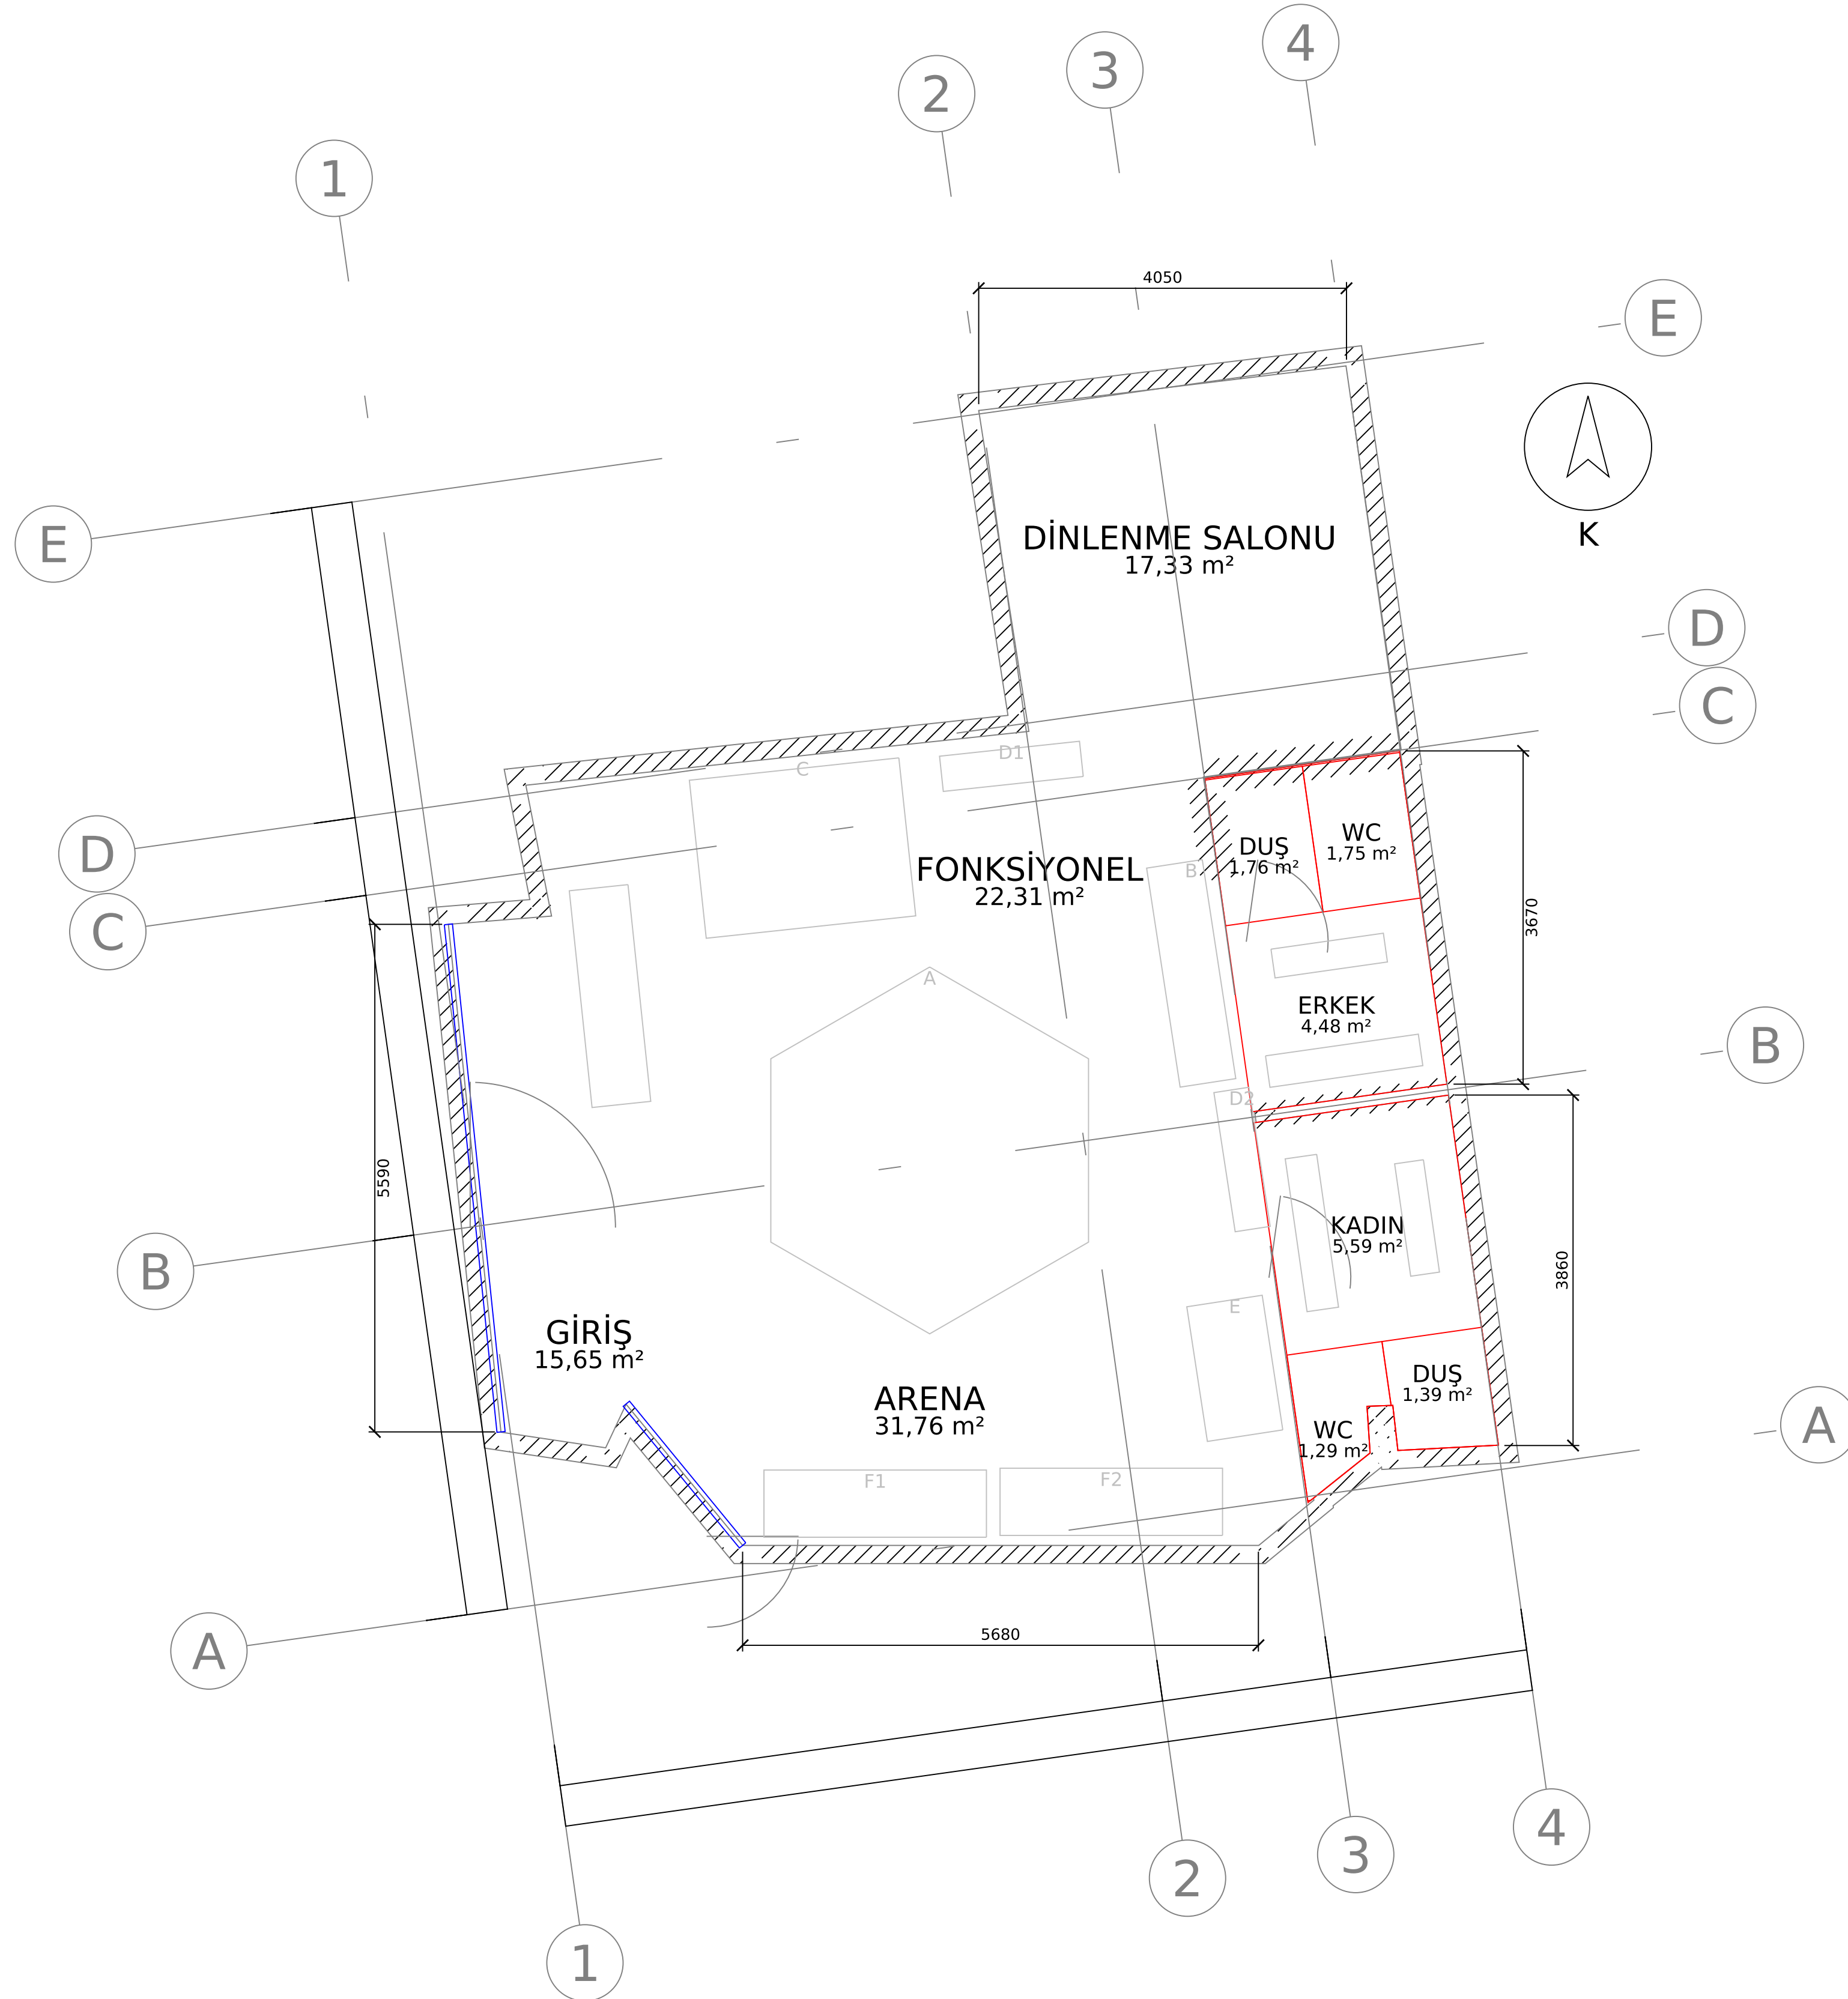

REV	TARİH	AÇIKLAMA	CZ	KT	ON
A	17.09.2026	İlk yayın — ön tasarım	CC	—	—
B	18.09.2026	Aks sistemi, zincir ölçü, ISO 5457/7200 pafta	CC	—	—
C	18.09.2026	A1 pafta, tekil DXF, ADP şeması CAD'de	CC	—	—
D	18.09.2026	ADP çok hatlı şema (faz ayrımı), B eğrisi, ana RCD	CC	—	—

İŞVEREN ÖZEL — MALTEPE / IDEALTEPE			B		
PROJE MOBİLYA MAĞAZASI → FONKSİYONEL ANTRENMAN STÜDYOSU					
YAPI / MAHAL İdealtepe Mah. · zemin kat dükkân · 103,78 m² iç alan			DİSİPLİN MİMARİ		
PAFTA ADI MİMARİ ALTLIK			Mevcut durum - ölçü ve aks sistemi		
PROJE MÜELLİFİ - ODA SİCİL NO — Oda sicil no: —					
ÇİZEN CC		KONTROL —		ONAY —	
TARİH 17 Eylül 2026		ÖLÇEK 1:50		BİRİM milimetre (mm)	
DURUM ÖN TASARIM		PAFTA NO A-01		REV H	
				SONRAKİ: A-02	

LEJANT

- Mimari — mevcut duvar (korunuyor)
- Mimari — yeni alçıpan bölme
- Mimari — cephe doğraması
- Mimari — kapı ve açılım
- Mimari — spor ekipmanı (işverence temini)
- Mimari — sabit mobilya
- Mimari — mahal adı ve alan
- Mimari — mahal numarası ve kapı kodu balonu
- Mimari — kesit ve görünüş hattı

GENEL NOTLAR

- Mahal no, kapı kodu, duvar tipi ve
- kesit hattı gösterilmiştir.
- Tüm alçıpan bölmeler yapısal döseme
- altına (+3.20) kadar yükselir.

ÖLÇEK 1:50
0 1 2 3 4 5 m


ÖN TASARIM — UYGULAMA İÇİN DEĞİLDİR

100 mm


REV	TARİH	AÇIKLAMA	CZ	KT	ON
A	17.09.2026	İlk yayın — ön tasarım	CC	—	—
B	18.09.2026	Aks sistemi, zincir ölçü, ISO 5457/7200 pafta	CC	—	—
C	18.09.2026	A1 pafta, tekil DXF, ADP şeması CAD'de	CC	—	—
D	18.09.2026	ADP çok hatlı şema (faz ayrımı), B eğrisi, ana RCD	CC	—	—

İŞVEREN ÖZEL — MALTEPE / IDEALTEPE PROJE MOBİLYA MAĞAZASI → FONKSİYONEL ANTRENMAN STÜDYOSU			DISİPLİN MİMARİ	
YAPI / MAHAL İdealtepe Mah. · zemin kat dükkân · 103,78 m² iç alan			Bölme duvarlar · kapılar · mahal numaraları	
PAFTA ADI MİMARİ UYGULAMA PLANI				
PROJE MÜELLİFİ · ODA SİCİL NO — Oda sicil no: —				
ÇİZEN CC		KONTROL —	ONAY —	
TARİH 17 Eylül 2026		ÖLÇEK 1:50	BİRİM milimetre (mm)	
DURUM ÖN TASARIM		PAFTA NO A-02	REV H	SONRAKİ: A-03

ÖLÇÜ ALINMAZ — YAZILI ÖLÇÜLER GEÇERLİDİR

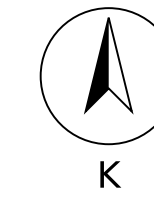

ANAHTAR PLAN

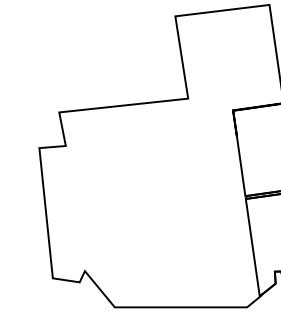

LEJANT

- Mimari — mevcut duvar (korunuyor)
- Mimari — yeni açılan bölme
- Mimari — cephe doğraması
- Mimari — kapı ve açılım
- Mimari — mahal numarası ve kapı kodu balonu
- Mimari — zemin kaplama tipi sınırı
- Mimari — zemin kaplama tipi ve kotu
- Mimari — kauçuk karo derz ızgarası

GENEL NOTLAR


- Bitmiş zemin kotu tüm kuru hacimde
- +/-0,00; dus ve WC -0,02.
- Tesviye sapı kalınlıkları farklıdır
- (Z1:3 Z2:30 Z3:42 Z5:38 mm).
- Kaucuk karo derz 1000x1000 mm.


ÖLÇEK 1:50
0 1 2 3 4 5 m

ÖN TASARIM — UYGULAMA İÇİN DEĞİLDİR

REV	TARİH	AÇIKLAMA	CZ	KT	ON
A	17.09.2026	İlk yayın — ön tasarım	CC	—	—
B	18.09.2026	Aks sistemi, zincir ölçü, ISO 5457/7200 pafta	CC	—	—
C	18.09.2026	A1 pafta, tekil DXF, ADP şeması CAD'de	CC	—	—
D	18.09.2026	ADP çok hatlı şema (faz ayrımı), B eğrisi, ana RCD	CC	—	—

İŞVEREN ÖZEL — MALTEPE / IDEALTEPE			B		
PROJE MOBİLYA MAĞAZASI → FONKSİYONEL ANTRENMAN STÜDYOSU					
YAPI / MAHAL İdealtepe Mah. · zemin kat dükkân · 103,78 m² iç alan		DISIPLIN MİMARİ			
PAFTA ADI ZEMİN KAPLAMA PLANI		Kaplama tipleri · kot · derz yönü			
PROJE MÜELLİFİ · ODA SİCİL NO — Oda sicil no: —					
ÇİZEN CC	KONTROL —	ONAY —	A		
TARİH 17 Eylül 2026	ÖLÇEK 1:50	BİRİM milimetre (mm)			
DURUM ÖN TASARIM	PAFTA NO A-03	REV H	SONRAKİ: A-04		

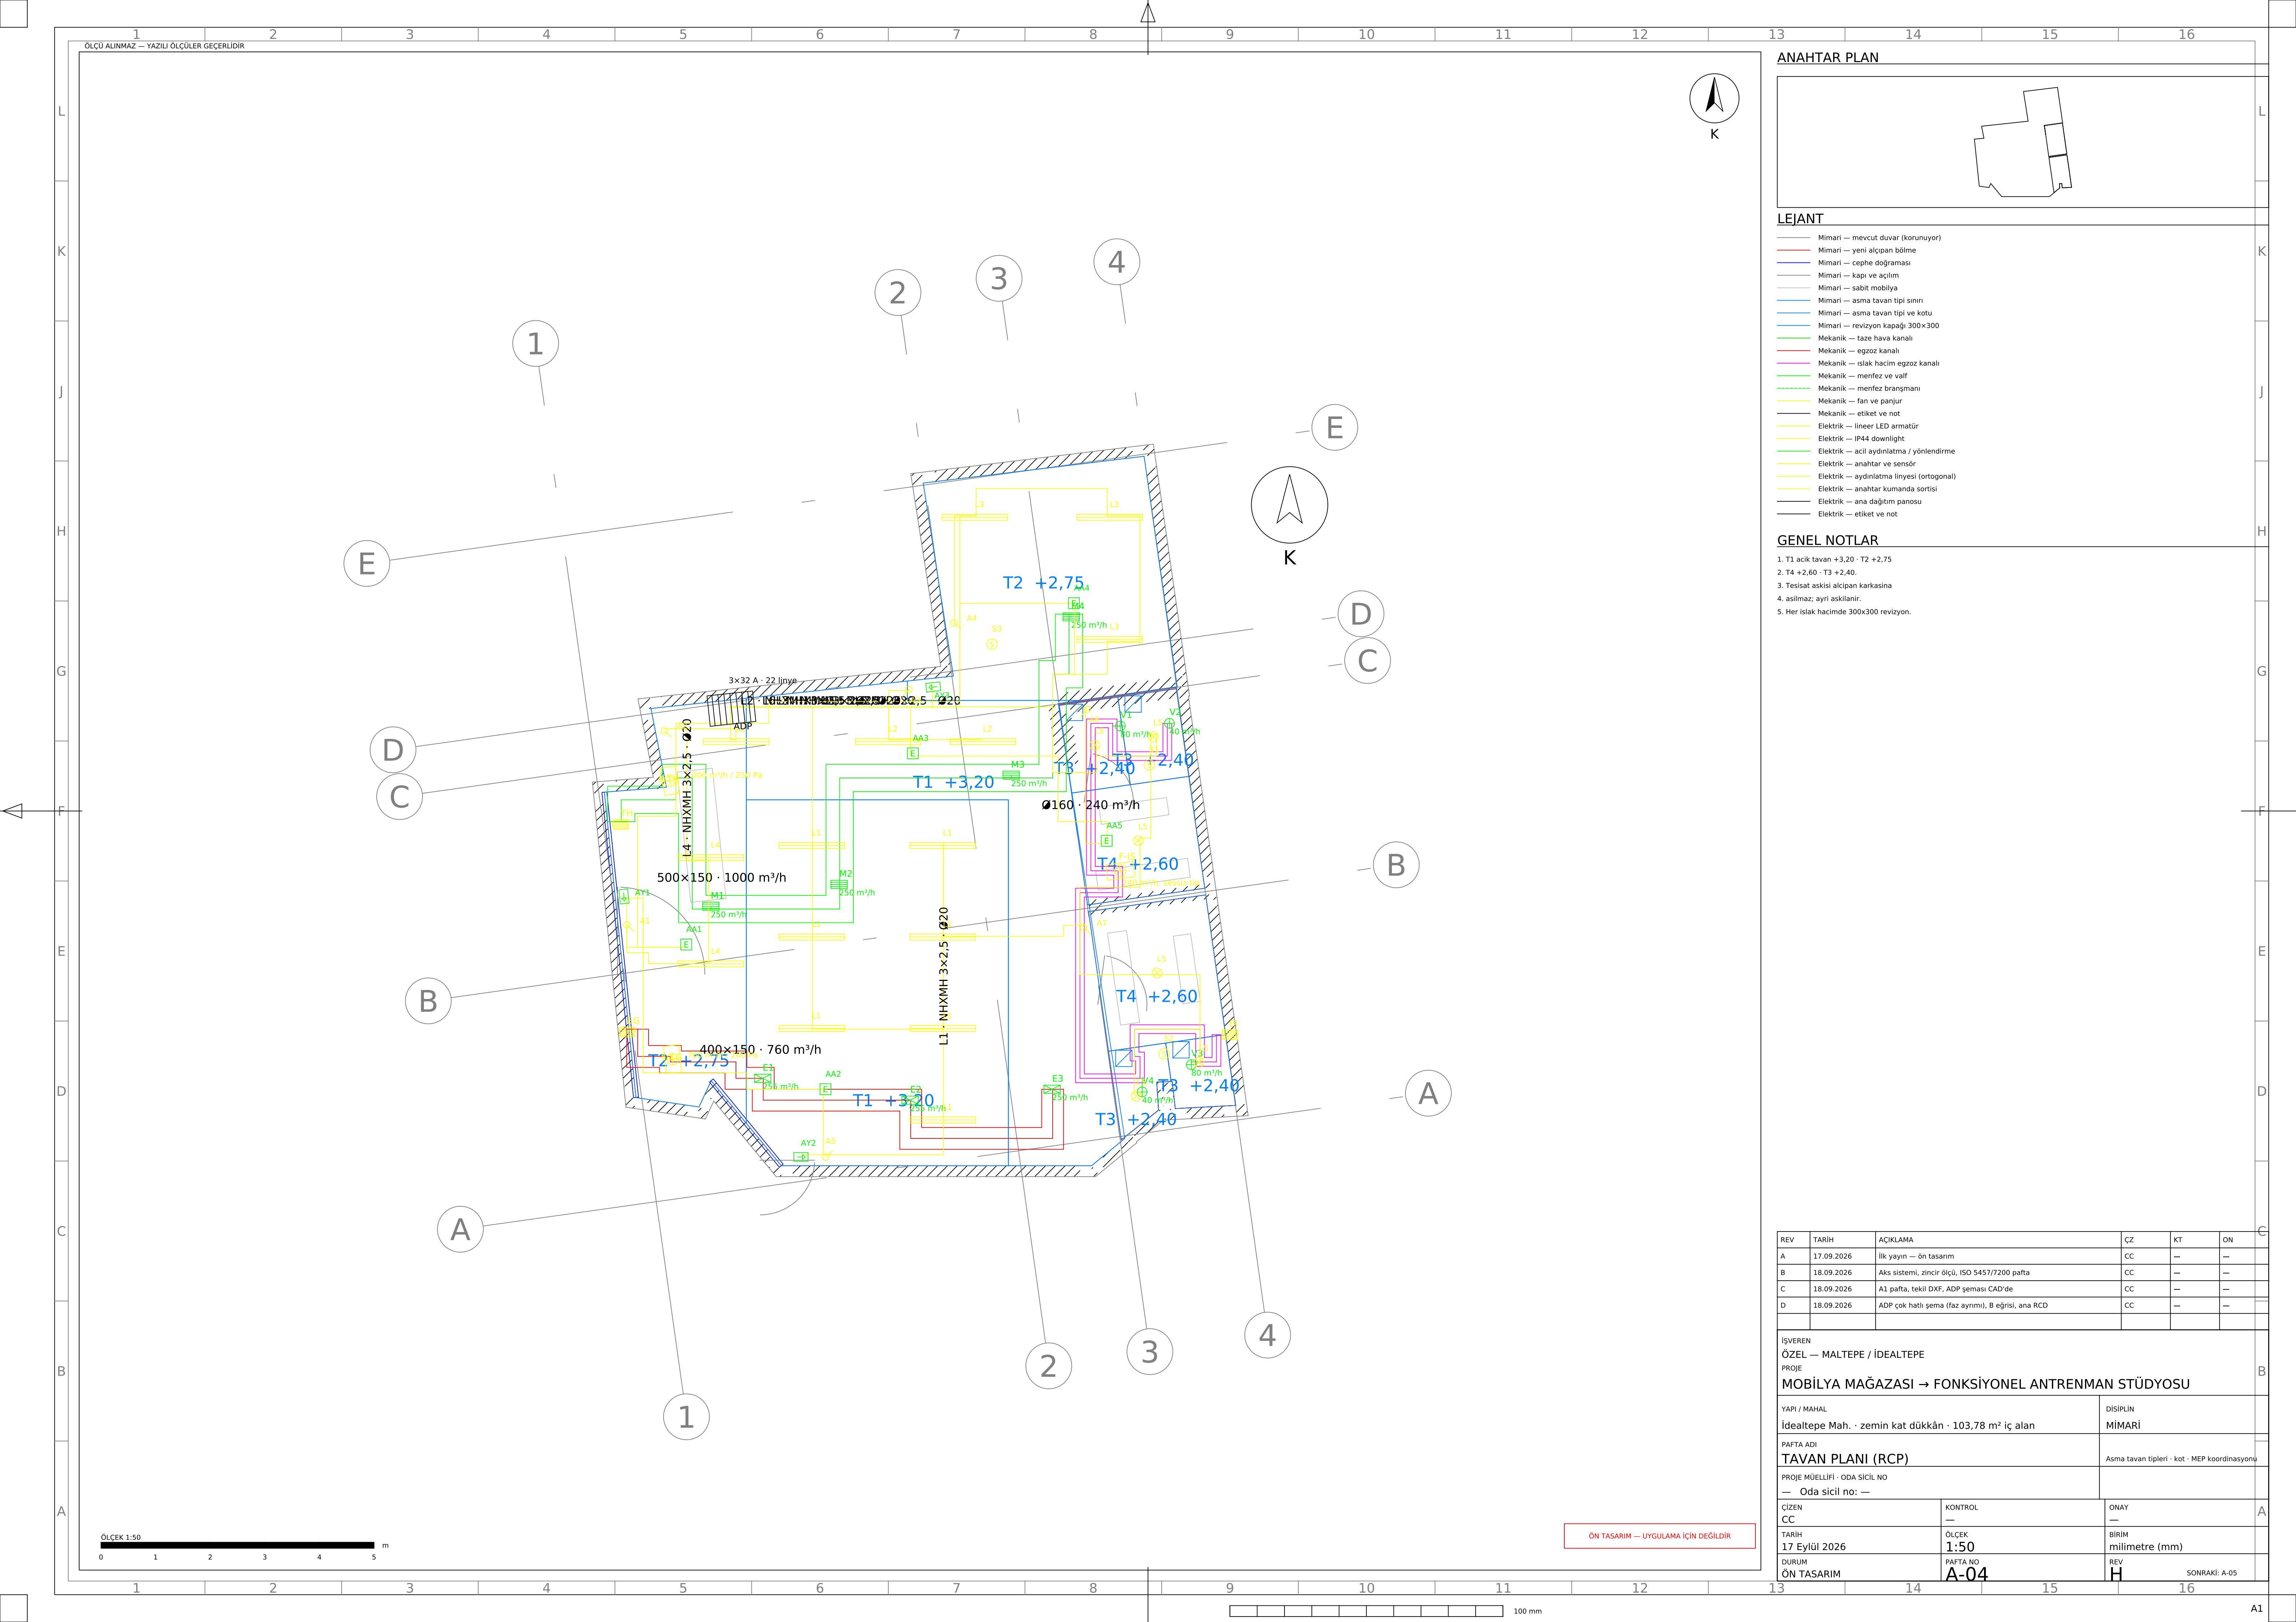

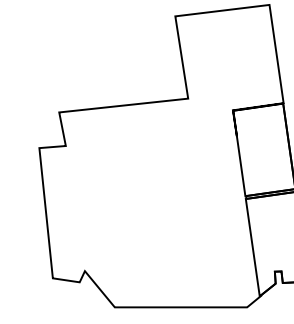


LEJANT

- Mimari — mevcut duvar (korunuyor)
- Mimari — yeni açılan bölme
- Mimari — cephe doğraması
- Mimari — kapı ve açılım
- Mimari — sabit mobilya
- Mimari — mahal adı ve alan
- Mimari — kaçış yolu ve çıkış
- Mimari — söndürücü, dolap, ihbar

GENEL NOTLAR

- İki bağımsız çıkış: Ç1 1,60 m, Ç2 1,00 m.
- En uzun kaçış yolu 13,4 m.
- Kaçış kapıları kaçış yönünde açılır.
- panik donanımlı, kilitli.

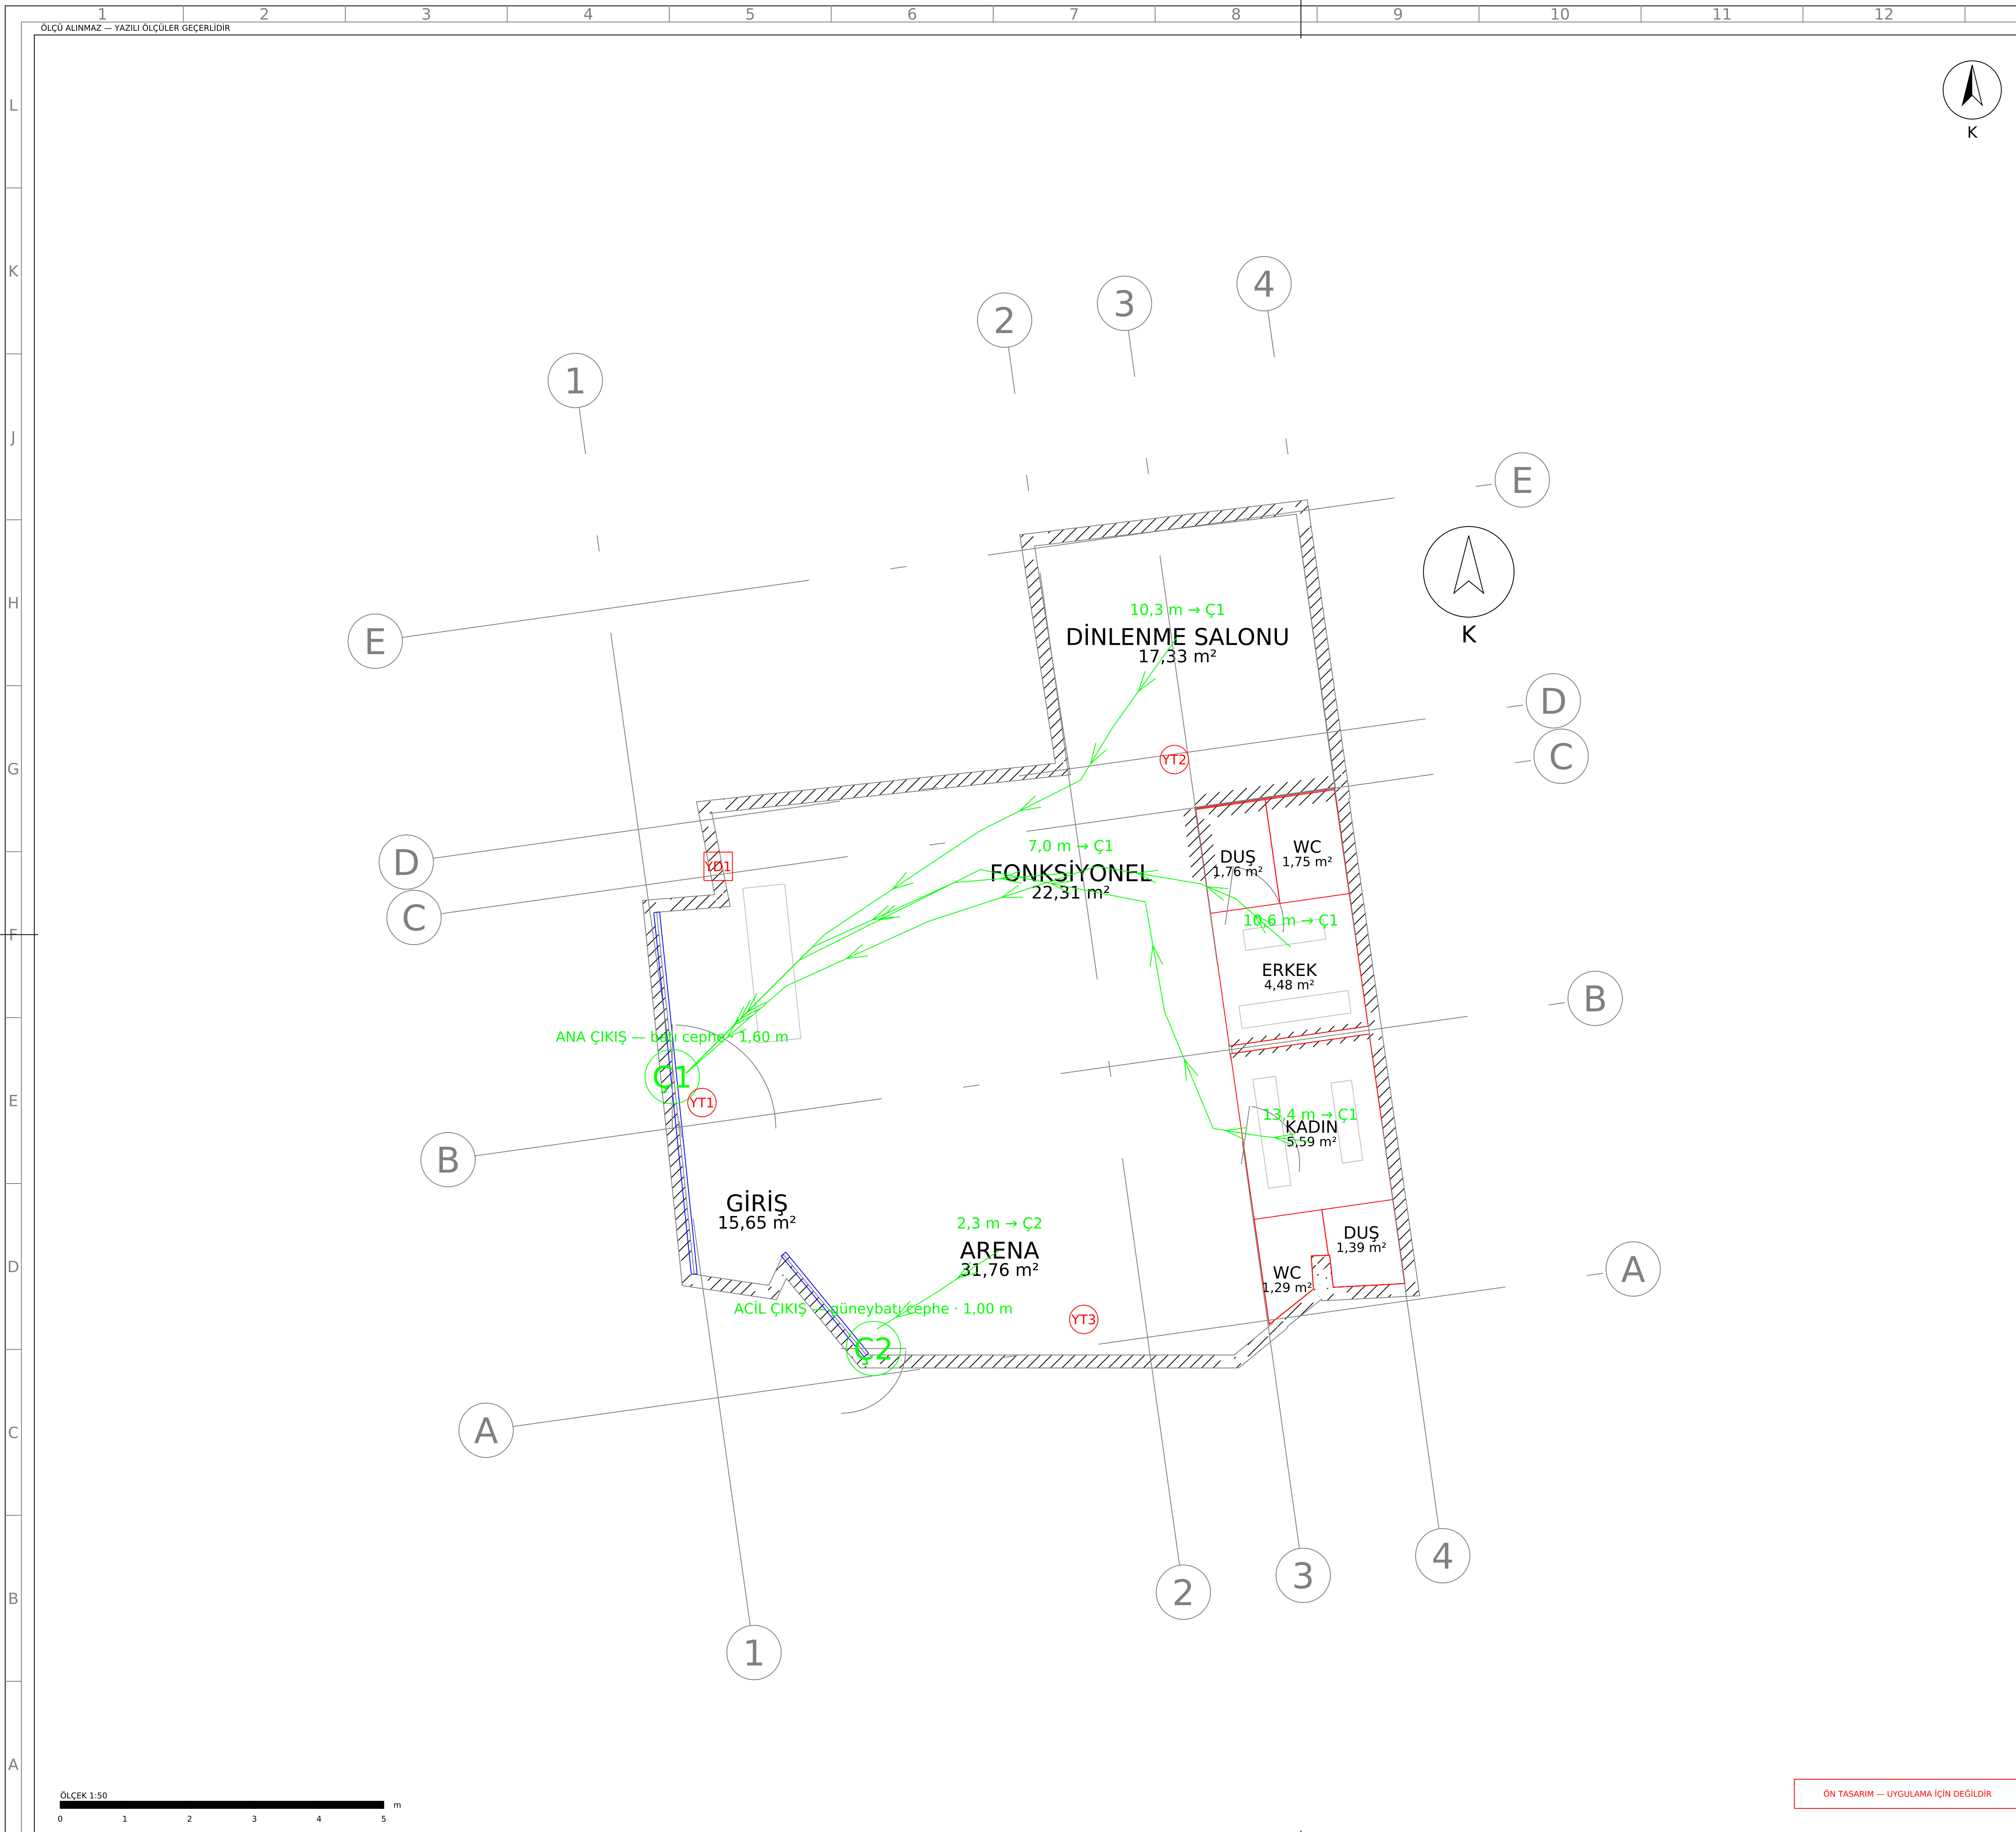

ÖN TASARIM — UYGULAMA İÇİN DEĞİLDİR

REV	TARİH	AÇIKLAMA	ÇZ	KT	ON
A	17.09.2026	İlk yayın — ön tasarım	CC	—	—
B	18.09.2026	Aks sistemi, zincir ölçü, ISO 5457/7200 pafta	CC	—	—
C	18.09.2026	A1 pafta, tekil DXF, ADP şeması CAD'de	CC	—	—
D	18.09.2026	ADP çok hatlı şema (faz ayrımı), B eğrisi, ana RCD	CC	—	—
İŞVEREN					
ÖZEL — MALTEPE / İDEALTEPE					
PROJE					
MOBİLYA MAĞAZASI → FONKSİYONEL ANTRENMAN STÜDYOSU					
YAPI / MAHAL			DİSİPLİN		
İdealtepe Mah. · zemin kat dükkân · 103,78 m² iç alan			MİMARİ		
PAFTA ADI			Kaçış yolları · çıkışlar · söndürücü		
YANGIN VE TAHLİYE PLANI					
PROJE MÜELLİFİ · ODA SİCİL NO					
— Oda sicil no: —					
ÇİZEN	KONTROL		ONAY		
CC	—		—		
TARİH	ÖLÇEK		BİRİM		
17 Eylül 2026	1:50		milimetre (mm)		
DURUM	PAFTA NO		REV		
ÖN TASARIM	A-05		H		
			SONRAKİ: M-01		

ÖLÇEK 1:50
0 1 2 3 4 5 m

LEJANT

- Mimari — mevcut duvar (korunuyor)
- Mimari — yeni alçıpan bölme
- Mimari — cephe doğraması
- Mimari — kapı ve açılım
- Mimari — spor ekipmanı (işverence temini)
- Mimari — sabit mobilya
- Mimari — mahal adı ve alan
- Mekanik — taze hava kanalı
- Mekanik — egzoz kanalı
- Mekanik — ıslak hacim egzoz kanalı
- Mekanik — menfez ve valf
- Mekanik — menfez bransmanı
- Mekanik — fan ve panjur
- Mekanik — etiket ve not

GENEL NOTLAR

- Kanallar galvaniz sac, TS EN 1507 sınıf B.
- Besleme ve egzoz hattı 19 mm izoleli.
- Her bransman bası debi ayar damperli.
- Devreye almada balanslama ve ölçüm raporu.

LEJANT

- Mimari — mevcut duvar (korunuyor)
- Mimari — yeni alçıpan bölme
- Mimari — cephe doğraması
- Mimari — kapı ve açılım
- Mimari — spor ekipmanı (işverence temin)
- Mimari — sabit mobilya
- Mimari — mahal adı ve alan
- Mekanik — klima iç ünite
- Mekanik — klima dış ünite platformu
- Mekanik — soğutucu akışkan bakır hattı
- Mekanik — klima drenaj hattı

GENEL NOTLAR


- İç ünite montaj kotu 2,40 m (altı kot).
- Bakır hat izoleli, dış ünite konsolu
- titresim takozlu.
- Drenaj %1 eğimli.

ÖLÇEK 1:50
0 1 2 3 4 5 m

ÖN TASARIM — UYGULAMA İÇİN DEĞİLDİR

REV	TARİH	AÇIKLAMA	CZ	KT	ON
A	17.09.2026	İlk yayın — ön tasarım	CC	—	—
B	18.09.2026	Aks sistemi, zincir ölçü, ISO 5457/7200 pafta	CC	—	—
C	18.09.2026	A1 pafta, tekil DXF, ADP şeması CAD'de	CC	—	—
D	18.09.2026	ADP çok hatlı şema (faz ayrımı), B eğrisi, ana RCD	CC	—	—

İŞVEREN ÖZEL — MALTEPE / IDEALTEPE PROJE MOBİLYA MAĞAZASI → FONKSİYONEL ANTRENMAN STÜDYOSU			DISIPLIN MEKANİK TESİSAT	
YAPI / MAHAL İdealtepe Mah. · zemin kat dükkân · 103,78 m² iç alan			Split küme · bakır hat · drenaj	
PAFTA ADI İKLİMLENDİRME PLANI			PROJE MÜELLİFİ · ODA SİCİL NO — Oda sicil no: —	
ÇİZEN CC		KONTROL —	ONAY —	
TARİH 17 Eylül 2026		ÖLÇEK 1:50	BİRİM milimetre (mm)	
DURUM ÖN TASARIM		PAFTA NO M-02	REV H	
			SONRAKİ: M-03	

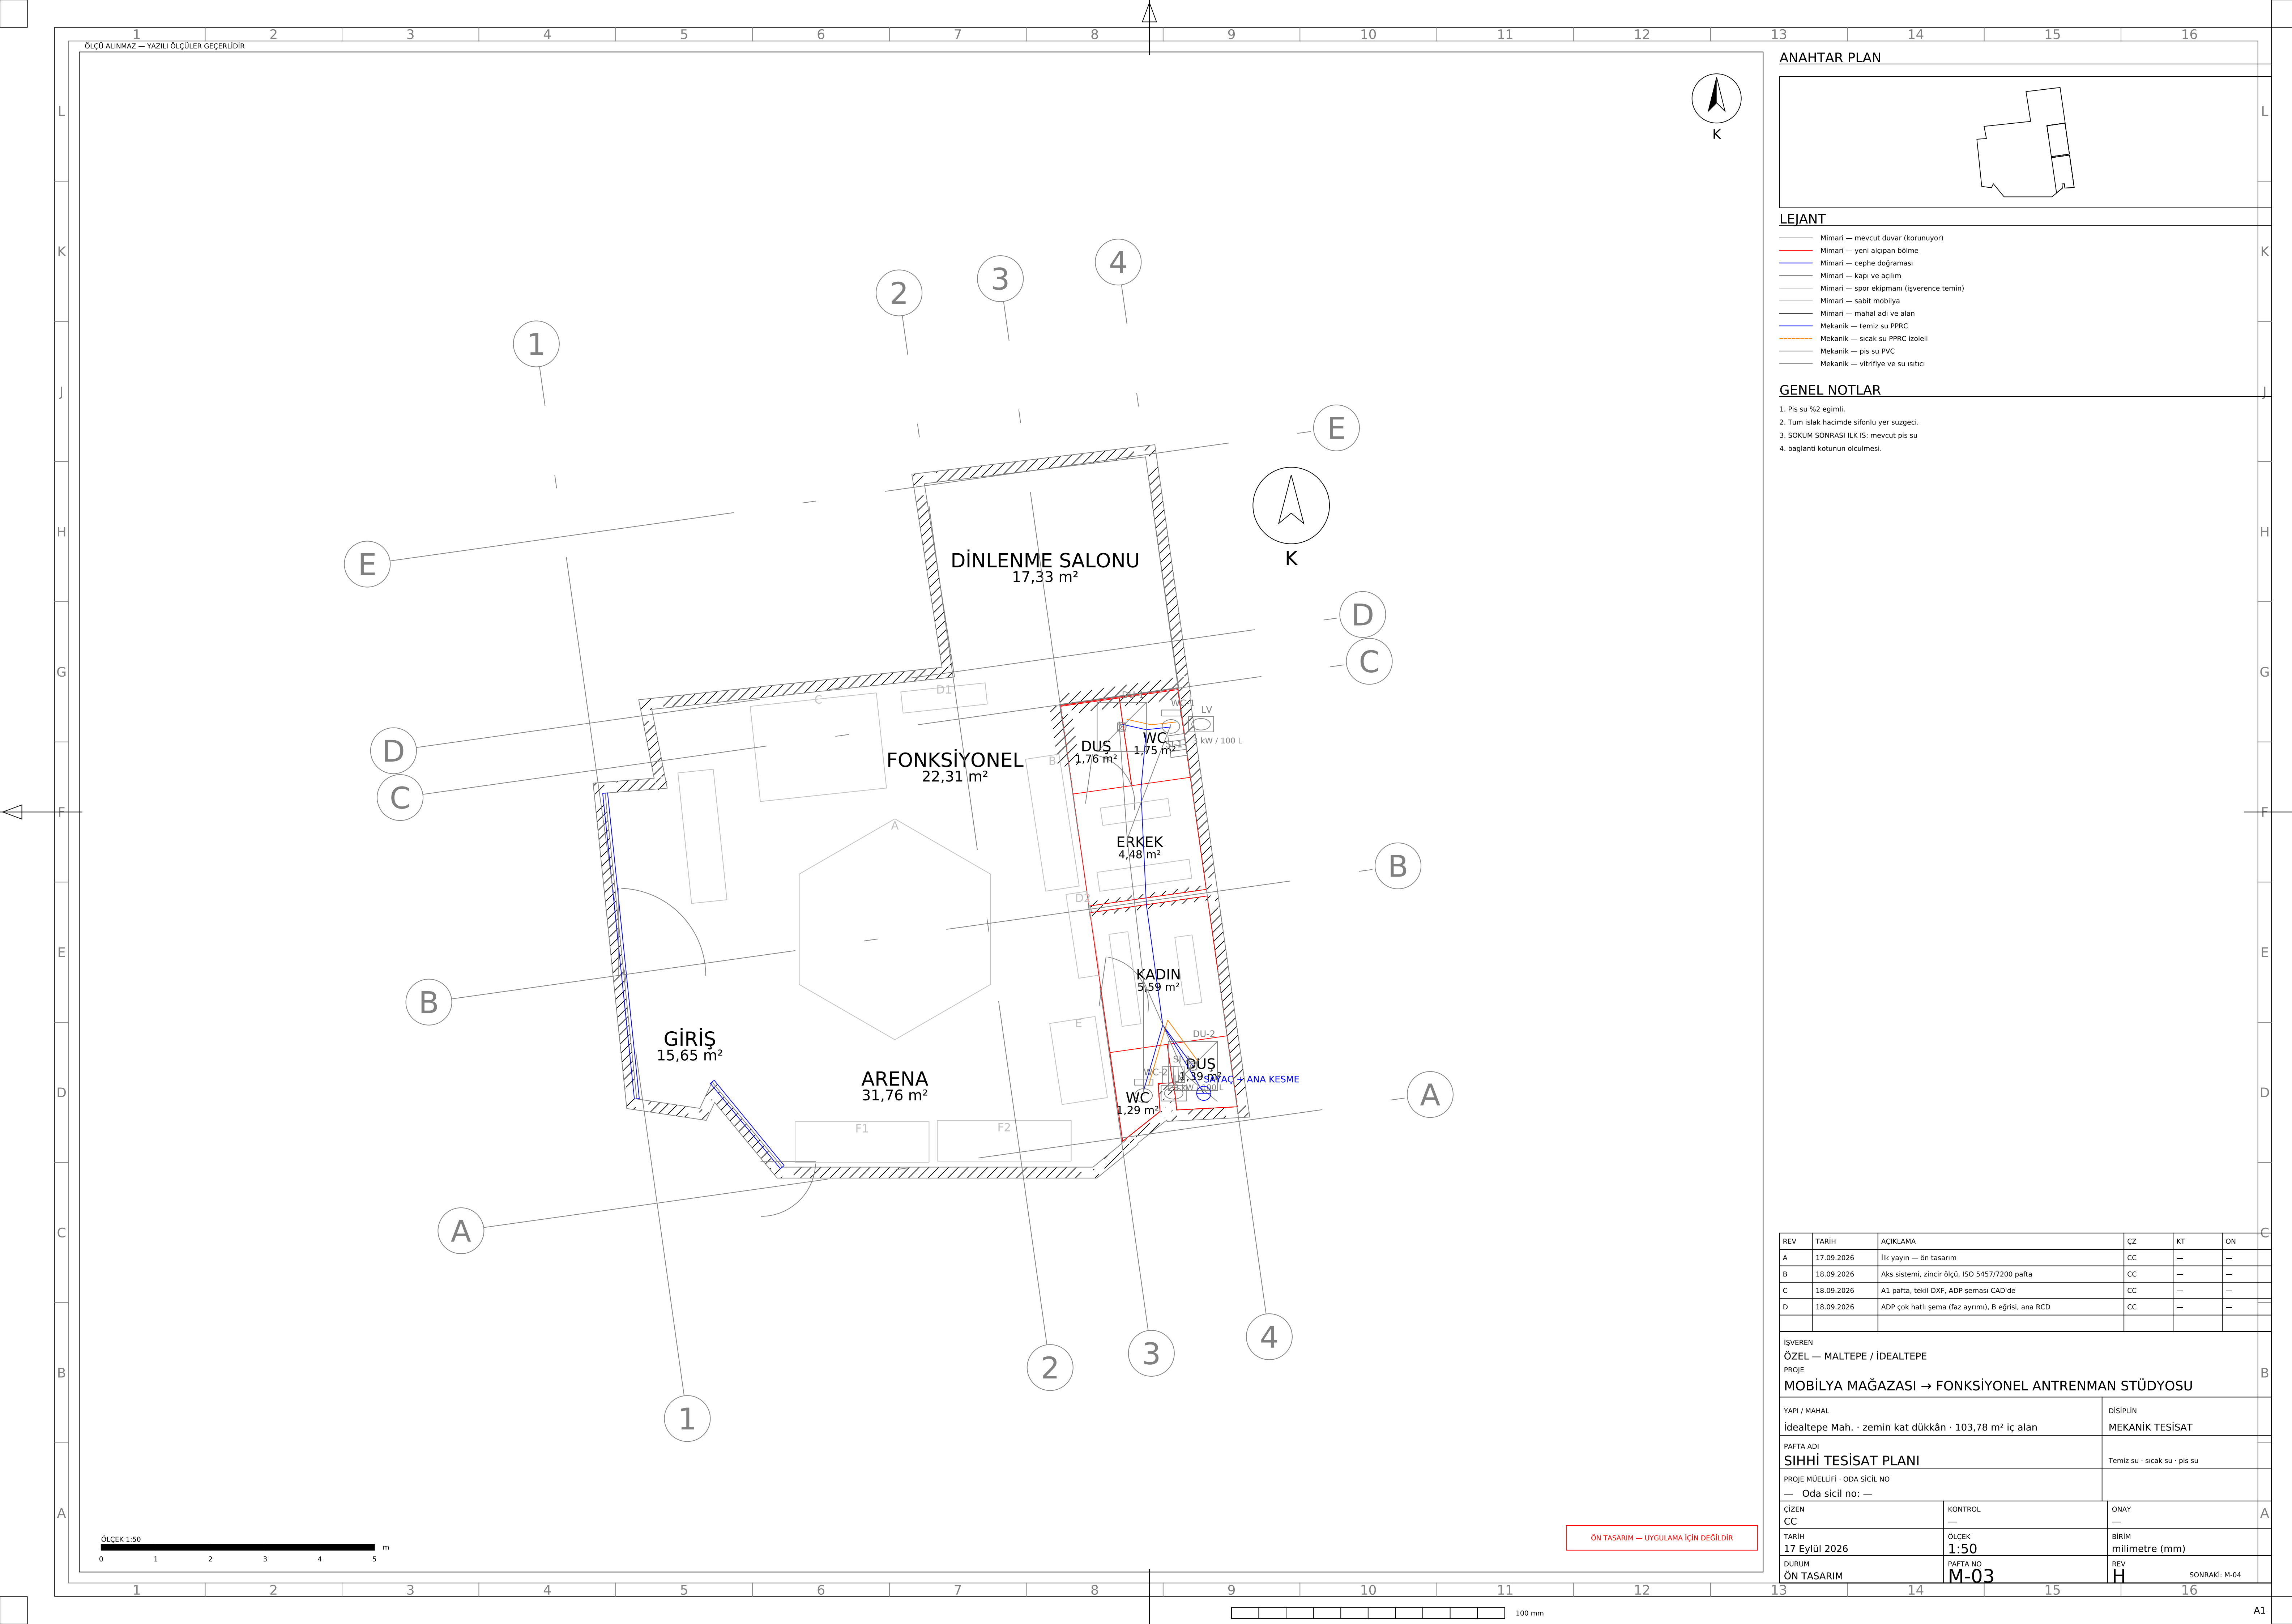

LEJANT

- Mimari — mevcut duvar (korunuyor)
- Mimari — yeni alçıpan bölme
- Mimari — cephe doğraması
- Mimari — kapı ve açılım
- Mimari — spor ekipmanı (işverence temini)
- Mimari — sabit mobilya
- Mimari — mahal adı ve alan
- Mekanik — taze hava kanalı
- Mekanik — egzoz kanalı
- Mekanik — ıslak hacim egzoz kanalı
- Mekanik — menfez ve valf
- Mekanik — menfez bransmanı
- Mekanik — fan ve panjur
- Mekanik — klima iç ünite
- Mekanik — klima dış ünite platformu
- Mekanik — soğutucu akışkan bakır hattı
- Mekanik — klima drenaj hattı
- Mekanik — temiz su PPRC
- Mekanik — sıcak su PPRC izoleli
- Mekanik — pis su PVC
- Mekanik — vitrifiye ve su ısıtıcı
- Mekanik — etiket ve not

GENEL NOTLAR

- Mekanik disiplin genel yerleşimi.
- Ayrıntı için M-01, M-02, M-03 paftaları.

REV	TARİH	AÇIKLAMA	CZ	KT	ON
A	17.09.2026	İlk yayın — ön tasarım	CC	—	—
B	18.09.2026	Aks sistemi, zincir ölçü, ISO 5457/7200 pafta	CC	—	—
C	18.09.2026	A1 pafta, tekil DXF, ADP şeması CAD'de	CC	—	—
D	18.09.2026	ADP çok hatlı şema (faz ayrımı), B eğrisi, ana RCD	CC	—	—

İŞVEREN	ÖZEL — MALTEPE / IDEALTEPE
PROJE	MOBİLYA MAĞAZASI → FONKSİYONEL ANTRENMAN STÜDYOSU
YAPI / MAHAL	İdealtepe Mah. · zemin kat dükkân · 103,78 m ² iç alan
PAFTA ADI	MEKANİK GENEL YERLEŞİM
PROJE MÜELLİFİ · ODA SİCİL NO	— Oda sicil no: —
ÇİZEN	CC
TARİH	17 Eylül 2026
DURUM	ÖN TASARIM
KONTROL	—
ÖLÇEK	1:50
PAFTA NO	M-04
ONAY	—
BİRİM	milimetre (mm)
REV	H
SONRAKİ:	E-01

LEJANT

- Mimari — mevcut duvar (korunuyor)
- Mimari — yeni açılan bölme
- Mimari — cephe doğraması
- Mimari — kapı ve açılım
- Mimari — spor ekipmanı (işverence temini)
- Mimari — sabit mobilya
- Mimari — mahal adı ve alan
- Elektrik — lineer LED armatür
- Elektrik — IP44 downlight
- Elektrik — acil aydınlatma / yönlendirme
- Elektrik — anahtar ve sensör
- Elektrik — aydınlatma linyesi (ortogonal)
- Elektrik — anahtar kumanda sortisi
- Elektrik — ana dağıtım panosu
- Elektrik — etiket ve not

GENEL NOTLAR

- Tesisat siva altı spiral boru içinde,
- NHXMH halojeniz kablo.
- Acil aydınlatma 3 saat bataryalı.

REV	TARİH	AÇIKLAMA	CZ	KT	ON
A	17.09.2026	İlk yayın — ön tasarım	CC	—	—
B	18.09.2026	Aks sistemi, zincir ölçü, ISO 5457/7200 pafta	CC	—	—
C	18.09.2026	A1 pafta, tekil DXF, ADP şeması CAD'de	CC	—	—
D	18.09.2026	ADP çok hatlı şema (faz ayrımı), B eğrisi, ana RCD	CC	—	—

İŞVEREN ÖZEL — MALTEPE / IDEALTEPE		
PROJE MOBİLYA MAĞAZASI → FONKSİYONEL ANTRENMAN STÜDYOSU		
YAPI / MAHAL İdealtepe Mah. · zemin kat dükkân · 103,78 m ² iç alan		DİSİPLİN ELEKTRİK
PAFTA ADI AYDINLATMA PLANI		Armatür · anahtar · aydınlatma linyeleri
PROJE MÜELLİFİ · ODA SİCİL NO — Oda sicil no: —		
ÇİZEN CC	KONTROL —	ONAY —
TARİH 17 Eylül 2026	ÖLÇEK 1:50	BİRİM milimetre (mm)
DURUM ÖN TASARIM	PAFTA NO E-01	REV H
SONRAKİ: E-02		

ÖLÇEK 1:50
0 1 2 3 4 5 m

ÖN TASARIM — UYGULAMA İÇİN DEĞİLDİR

LEJANT

- Mimari — mevcut duvar (korunuyor)
- Mimari — yeni alçıpan bölme
- Mimari — cephe doğraması
- Mimari — kapı ve açılım
- Mimari — spor ekipmanı (işverence temin)
- Mimari — sabit mobilya
- Mimari — mahal adı ve alan
- Elektrik — priz
- Elektrik — klima/sıtıcıfan beslemesi
- Elektrik — priz ve kuvvet linyesi
- Elektrik — ana dağıtım panosu
- Elektrik — etiket ve not

GENEL NOTLAR


- Islak hacim linyeleri ayrı 30 mA
- kacak akım rolesinden beslenir.
- Kardiyo ekipmanı ayrı linyede (P4).

ÖLÇEK 1:50
0 1 2 3 4 5 m

ÖN TASARIM — UYGULAMA İÇİN DEĞİLDİR

REV	TARİH	AÇIKLAMA	CZ	KT	ON
A	17.09.2026	İlk yayın — ön tasarım	CC	—	—
B	18.09.2026	Aks sistemi, zincir ölçü, ISO 5457/7200 pafta	CC	—	—
C	18.09.2026	A1 pafta, tekil DXF, ADP şeması CAD'de	CC	—	—
D	18.09.2026	ADP çok hatlı şema (faz ayrımı), B eğrisi, ana RCD	CC	—	—

İŞVEREN ÖZEL — MALTEPE / İDEALTEPE		B	
PROJE MOBİLYA MAĞAZASI → FONKSİYONEL ANTRENMAN STÜDYOSU			
YAPI / MAHAL İdealtepe Mah. · zemin kat dükkân · 103,78 m ² iç alan		DİSİPLİN ELEKTRİK	
PAFTA ADI PRİZ VE KUVVET PLANI			
PROJE MÜELLİFİ · ODA SİCİL NO — Oda sicil no: —		Priz · kuvvet linyeleri · cihaz beslemeleri	
ÇİZEN CC		KONTROL —	
TARİH 17 Eylül 2026		ONAY —	
DURUM ÖN TASARIM		A	
PAFTA NO E-02		BİRİM milimetre (mm)	
REV H		SONRAKİ: E-03	

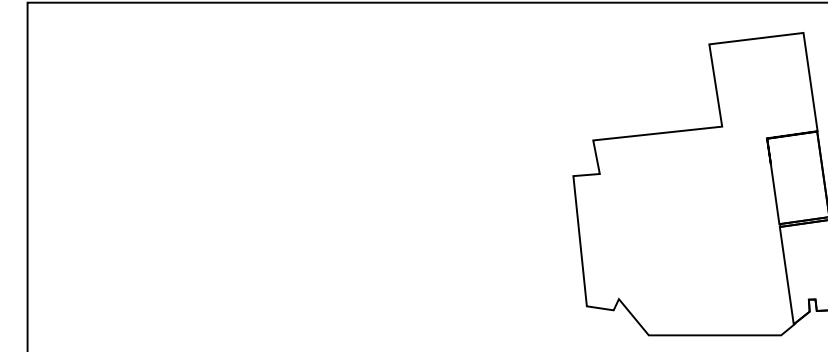

LEJANT

- Mimari — mevcut duvar (korunuyor)
- Mimari — yeni alçıpan bölme
- Mimari — cephe doğraması
- Mimari — kapı ve açılım
- Mimari — spor ekipmanı (işverence temin)
- Mimari — sabit mobilya
- Mimari — mahal adı ve alan
- Elektrik — IP kamera
- Elektrik — tavan hoparlörü
- Elektrik — veri prizi ve rack
- Elektrik — dedektör, buton, siren
- Elektrik — yangın algılama çevrimi
- Elektrik — zayıf akım kablo kanalı
- Elektrik — ana dağıtım panosu
- Elektrik — etiket ve not

GENEL NOTLAR

- SOYUNMA VE WC İÇİNE KAMERA KONULMAZ.
- Yangın algılama panosu kesintisiz beslenir.
- Topraklama direnci ≤ 10 ohm.

ÖLÇEK 1:50
0 1 2 3 4 5 m

ÖN TASARIM — UYGULAMA İÇİN DEĞİLDİR

100 mm

A1

LEJANT

- Mimari — mevcut duvar (korunuyor)
- Mimari — yeni açılan bölme
- Mimari — cephe doğraması
- Mimari — kapı ve açılım
- Mimari — spor ekipmanı (işverence temini)
- Mimari — sabit mobilya
- Mimari — mahal adı ve alan
- Elektrik — lineer LED armatür
- Elektrik — IP44 downlight
- Elektrik — acil aydınlatma / yönlendirme
- Elektrik — anahtar ve sensör
- Elektrik — priz
- Elektrik — klima/sıtıcı/fan beslemesi
- Elektrik — IP kamera
- Elektrik — tavan hoparlörü
- Elektrik — veri prizi ve rack
- Elektrik — dedektör, buton, siren
- Elektrik — yangın algılama çevrimi
- Elektrik — aydınlatma lineyesi (ortogonal)
- Elektrik — anahtar kumanda sortisi
- Elektrik — priz ve kuvvet lineyesi
- Elektrik — zayıf akım kablo kanalı
- Elektrik — ana dağıtım panosu
- Elektrik — etiket ve not

GENEL NOTLAR

- Elektrik disiplin genel yerleşimi.
- Ayrıntı için E-01, E-02, E-03 paftaları.

REV	TARİH	AÇIKLAMA	CZ	KT	ON
A	17.09.2026	İlk yayın — ön tasarım	CC	—	—
B	18.09.2026	Aks sistemi, zincir ölçü, ISO 5457/7200 pafta	CC	—	—
C	18.09.2026	A1 pafta, tekil DXF, ADP şeması CAD'de	CC	—	—
D	18.09.2026	ADP çok hatlı şema (faz ayrımı), B eğrisi, ana RCD	CC	—	—

İŞVEREN ÖZEL — MALTEPE / İDEALTEPE					
PROJE MOBİLYA MAĞAZASI → FONKSİYONEL ANTRENMAN STÜDYOSU			B		
YAPI / MAHAL İdealtepe Mah. · zemin kat dükkân · 103,78 m² iç alan			DISIPLİN ELEKTRİK		
PAFTA ADI ELEKTRİK GENEL YERLEŞİM			Elektrik disiplin genel yerleşimi		
PROJE MÜELLİFİ · ODA SİCİL NO — Oda sicil no: —					
ÇİZEN CC		KONTROL —	ONAY —		A
TARİH 17 Eylül 2026		ÖLÇEK 1:50	BİRİM milimetre (mm)		
DURUM ÖN TASARIM		PAFTA NO E-04	REV H		SONRAKİ: E-05

ÖN TASARIM — UYGULAMA İÇİN DEĞİLDİR

LEJANT

- Mimari — mevcut duvar (korunuyor)
- Mimari — yeni açılan bölme
- Mimari — cephe doğraması
- Mimari — kapı ve açılım
- Mimari — spor ekipmanı (işverence temin)
- Mimari — sabit mobilya
- Mimari — mahal adı ve alan
- Elektrik — çubuk elektrot
- Elektrik — elektrot bağlantı şeridi
- Elektrik — topraklama iletkeni
- Elektrik — ATB / EPDB barası
- Elektrik — topraklama etiketi
- Elektrik — ana dağıtım panosu

GENEL NOTLAR

- Topraklama ve potansiyel dengeleme.
- Elektrot grubu yapı dışında, 4 adet 2 m Cu kaplı
- çelik çubuk, 3 m aralık. Ra hesap 15,5 ohm <= 20 ohm.
- ATB pano altında; her ıslak blokta EPDB bulunur.

ÖLÇEK 1:50
0 1 2 3 4 5 m

ÖN TASARIM — UYGULAMA İÇİN DEĞİLDİR

REV	TARİH	AÇIKLAMA	CZ	KT	ON
A	17.09.2026	İlk yayın — ön tasarım	CC	—	—
B	18.09.2026	Aks sistemi, zincir ölçü, ISO 5457/7200 pafta	CC	—	—
C	18.09.2026	A1 pafta, tekil DXF, ADP şeması CAD'de	CC	—	—
D	18.09.2026	ADP çok hatlı şema (faz ayrımı), B eğrisi, ana RCD	CC	—	—

İŞVEREN ÖZEL — MALTEPE / İDEALTEPE					
PROJE MOBİLYA MAĞAZASI → FONKSİYONEL ANTRENMAN STÜDYOSU					
YAPI / MAHAL İdealtepe Mah. - zemin kat dükkân - 103,78 m ² iç alan		DİSİPLİN ELEKTRİK			
PAFTA ADI TOPRAKLAMA VE POTANSİYEL DENGELEME PLANI		Elektrot grubu - ATB - EPDB			
PROJE MÜELLİFİ - ODA SİCİL NO — Oda sicil no: —					
ÇİZEN CC		KONTROL —		ONAY —	
TARİH 17 Eylül 2026		ÖLÇEK 1:50		BİRİM milimetre (mm)	
DURUM ÖN TASARIM		PAFTA NO E-05		REV H	
			SONRAKİ: ADP-01		