

0

1

2

3

4

5

6

7

A

ADP — ANA DAĞITIM PANOSU

ÇOK HATLI ŞEMATİK DİYAGRAM SETİ / MULTI-LINE SCHEMATIC SET

Müşteri / Customer

Proje / Project

Pano / Panel

Proje No / Project No

Tarih / Date

Revizyon / Revision

Standartlar / Standards

ÖZEL — MALTEPE / İDEALTEPE

MOBİLYA MAĞAZASI → FONKSİYONEL ANTRENMAN STÜDYOSU

ADP

GYM-25-001-001

17 Eylül 2026

Rev H

IEC 61439-1&2 · IEC 60617 · IEC 81346-2 · TS HD 60364 · Elektrik İç Tesisleri Yönetmeliği

SAYFA İÇERİĞİ / SHEET INDEX

01

Cover Sheet / Kapak

02

Panel Characteristics / Pano Karakteristiği

03

Symbol List / Sembol Listesi

04

Incoming Supply / Ana Besleme

05

Schematic Diagram / Şematik Diyagram

06

Schematic Diagram / Şematik Diyagram

07

Schematic Diagram / Şematik Diyagram

08

Schematic Diagram / Şematik Diyagram

09

Terminal Diagram / Klemens Planı

10

Panel Overview / Pano Önden Görünüş

11

Load Schedule / Yükleme Cetveli

12

Parts List / Malzeme Listesi

E

F

Drawn By / Çizen

CC

Customer Name / Müşteri Adı

ÖZEL — MALTEPE / İDEALTEPE

Project Number / Proje Numarası

GYM-25-001-001

Sheet: / Sayfa

1

Checked By / Kontrol Eden

—

Project Description / Proje Açıklaması

MOBİLYA MAĞAZASI → FONKSİYONEL ANTRENMAN STÜDYOSU

Revision / Revizyon

Rev H

Total sheets: / Toplam

12

Approved By / Onaylayan

—

Panel Name / Pano Adı

ADP

Standards / Standartlar

IEC 61439-1&2 · IEC 60617

Sheet size / Kâğıt

A3



Project Date / Proje Tarihi


17 Eylül 2026

Page Description / Sayfa Açıklaması


Cover Sheet / Kapak


|                             |   |               |                                        |   |                                                   |   |   |                                 |                           |                        |    |
|-----------------------------|---|---------------|----------------------------------------|---|---------------------------------------------------|---|---|---------------------------------|---------------------------|------------------------|----|
|                             | 0   | 1             | 2                                      | 3 | 4                                                 | 5 | 6 | 7                               |                           |                        |    |
| A                           | <div><div>PANO KARAKTERİSTİK TABLOSU / PANEL CHARACTERISTICS</div><div><div>STANDARTLAR / STANDARDS</div><div><div>Tip testli pano / Type tested assembly</div><div>IEC 61439-1 &amp; IEC 61439-2</div></div><div><div>Semboller / Symbols</div><div>IEC 60617</div></div><div><div>Referans işaretleri / Designations</div><div>IEC 81346-2</div></div><div><div>Tesisat / Installation</div><div>TS HD 60364 · Elektrik İç Tes. Yön.</div></div></div><div><div>BESLEME / POWER SUPPLY</div><div><div>Anma işletme gerilimi / Rated voltage</div><div>400/230 V 50 Hz</div></div><div><div>Faz sayısı / Number of phases</div><div>3F + N + PE</div></div><div><div>Nötr işletmesi / Neutral operation</div><div>TN-S</div></div><div><div>Anma akımı / Rated current</div><div>32 A</div></div><div><div>Kısa devre dayanımı / Icw</div><div>6 kA 1 s</div></div><div><div>Ana besleme kablosu / Main cable</div><div>NYY 5×10 mm² · 25 m</div></div></div><div><div>KORUMA / PROTECTION</div><div><div>Ana şalter / Main switch</div><div>4×32 A</div></div><div><div>Ana kaçak akım / Main RCD</div><div>4×40 A / 300 mA S tipi</div></div><div><div>Son devre kaçak akım / Final RCD</div><div>30 mA A tipi</div></div><div><div>Aşırı gerilim / SPD</div><div>Tip 2 · Up 1,4 kV · In 20 kA</div></div><div><div>Kesici eğrisi / MCB curve</div><div>Aydınlatma B · Priz ve motor C · tümü 6 kA</div></div></div></div> |               |                                        |   |                                                   |   |   |                                 |                           |                        |    |
| B                           | <div><div>GÖVDE / ENCLOSURE</div><div><div>Koruma sınıfı / Degree of protection</div><div>IP 54</div></div><div><div>Ayrıştırma / Segregation</div><div>Form 2b</div></div><div><div>Gövde / Enclosure</div><div>Sac · RAL 7035</div></div><div><div>Bara / Busbar</div><div>Bakır · nötr tam kesit</div></div><div><div>Montaj / Mounting</div><div>Sabit · kapı arkası kumanda</div></div><div><div>Etiketleme / Labelling</div><div>PVC · Türkçe · vidalı</div></div></div> <div><div>ÖZET / SUMMARY</div><div><div>Linye sayısı / Number of circuits</div><div>22 + 4 yedek</div></div><div><div>Bağlı güç / Connected load</div><div>20,59 kW</div></div><div><div>Talep gücü / Demand</div><div>14,63 kW</div></div><div><div>Faz dengesizliği / Imbalance</div><div>%1,0</div></div><div><div>Toplam ΔU / Total voltage drop</div><div>%2,49</div></div></div>   |               |                                        |   |                                                   |   |   |                                 |                           |                        |    |
| C                           |   |               |                                        |   |                                                   |   |   |                                 |                           |                        |    |
| D                           |   |               |                                        |   |                                                   |   |   |                                 |                           |                        |    |
| E                           |   |               |                                        |   |                                                   |   |   |                                 |                           |                        |    |
| F                           |   |               |                                        |   |                                                   |   |   |                                 |                           |                        |    |
| Drawn By / Çizen            |   | CC            | Customer Name / Müşteri Adı            |   | ÖZEL — MALTEPE / İDEALTEPE                        |   |   | Project Number / Proje Numarası | GYM-25-001-001            | Sheet: / Sayfa         | 2  |
| Checked By / Kontrol Eden   |   | —             | Project Description / Proje Açıklaması |   | MOBİLYA MAĞAZASI → FONKSİYONEL ANTRENMAN STÜDYOSU |   |   |                                 |                           | Next sheet: / Sonraki  | 3  |
| Approved By / Onaylayan     |   | —             | Panel Name / Pano Adı                  |   | ADP                                               |   |   | Revision / Revizyon             | Rev H                     | Total sheets: / Toplam | 12 |
| Project Date / Proje Tarihi |   | 17 Eylül 2026 | Page Description / Sayfa Açıklaması    |   | Panel Characteristics / Pano Karakteristiği       |   |   | Standards / Standartlar         | IEC 61439-1&2 · IEC 60617 | Sheet size / Kağıt     | A3 |
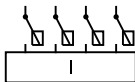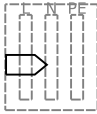
|                             |                                                                                     |               |                                                |                                                   |   |   |                                 |                           |                        |    |
|-----------------------------|-------------------------------------------------------------------------------------|---------------|------------------------------------------------|---------------------------------------------------|---|---|---------------------------------|---------------------------|------------------------|----|
|                             | 0                                                                                   | 1             | 2                                              | 3                                                 | 4 | 5 | 6                               | 7                         |                        |    |
| A                           | SEMBOL LİSTESİ / SYMBOL LIST — IEC 60617                                            |               |                                                |                                                   |   |   |                                 |                           |                        |    |
|                             |    | -F            | Otomatik sigorta, 1 kutup / MCB 1P             |                                                   |   |   |                                 |                           |                        |    |
|                             |    | -F            | Otomatik sigorta, 1F+N / MCB 1P+N              |                                                   |   |   |                                 |                           |                        |    |
| B                           |    | -ID           | Kaçak akım rölesi 2 kutup / RCD 2P             |                                                   |   |   |                                 |                           |                        |    |
|                             |    | -ID           | Kaçak akım rölesi 4 kutup / RCD 4P             |                                                   |   |   |                                 |                           |                        |    |
|                             |    | -F0           | Aşırı gerilim koruma Tip 2 / SPD Type 2        |                                                   |   |   |                                 |                           |                        |    |
| C                           |    | -X            | Klemens / Terminal                             |                                                   |   |   |                                 |                           |                        |    |
|                             |    | PE            | Koruma topraklaması / Protective earth         |                                                   |   |   |                                 |                           |                        |    |
|                             |    |               | Bağlantı noktası / Junction                    |                                                   |   |   |                                 |                           |                        |    |
| D                           |  | P             | Saha cihazı ve kablo / Field device and cable  |                                                   |   |   |                                 |                           |                        |    |
|                             |  |               | L1 L2 L3 N Potansiyel rayı / Potential rail    |                                                   |   |   |                                 |                           |                        |    |
|                             |  |               | Sayfalar arası referans / Cross-page reference |                                                   |   |   |                                 |                           |                        |    |
| E                           |                                                                                     |               |                                                |                                                   |   |   |                                 |                           |                        |    |
| F                           |                                                                                     |               |                                                |                                                   |   |   |                                 |                           |                        |    |
| Drawn By / Çizen            |                                                                                     | CC            | Customer Name / Müşteri Adı                    | ÖZEL — MALTEPE / İDEALTEPE                        |   |   | Project Number / Proje Numarası | GYM-25-001-001            | Sheet: / Sayfa         | 3  |
| Checked By / Kontrol Eden   |                                                                                     | —             | Project Description / Proje Açıklaması         | MOBİLYA MAĞAZASI → FONKSİYONEL ANTRENMAN STÜDYOSU |   |   |                                 |                           | Next sheet: / Sonraki  | 4  |
| Approved By / Onaylayan     |                                                                                     | —             | Panel Name / Pano Adı                          | ADP                                               |   |   | Revision / Revizyon             | Rev H                     | Total sheets: / Toplam | 12 |
| Project Date / Proje Tarihi |                                                                                     | 17 Eylül 2026 | Page Description / Sayfa Açıklaması            | Symbol List / Sembol Listesi                      |   |   | Standards / Standartlar         | IEC 61439-1&2 · IEC 60617 | Sheet size / Kâğıt     | A3 |

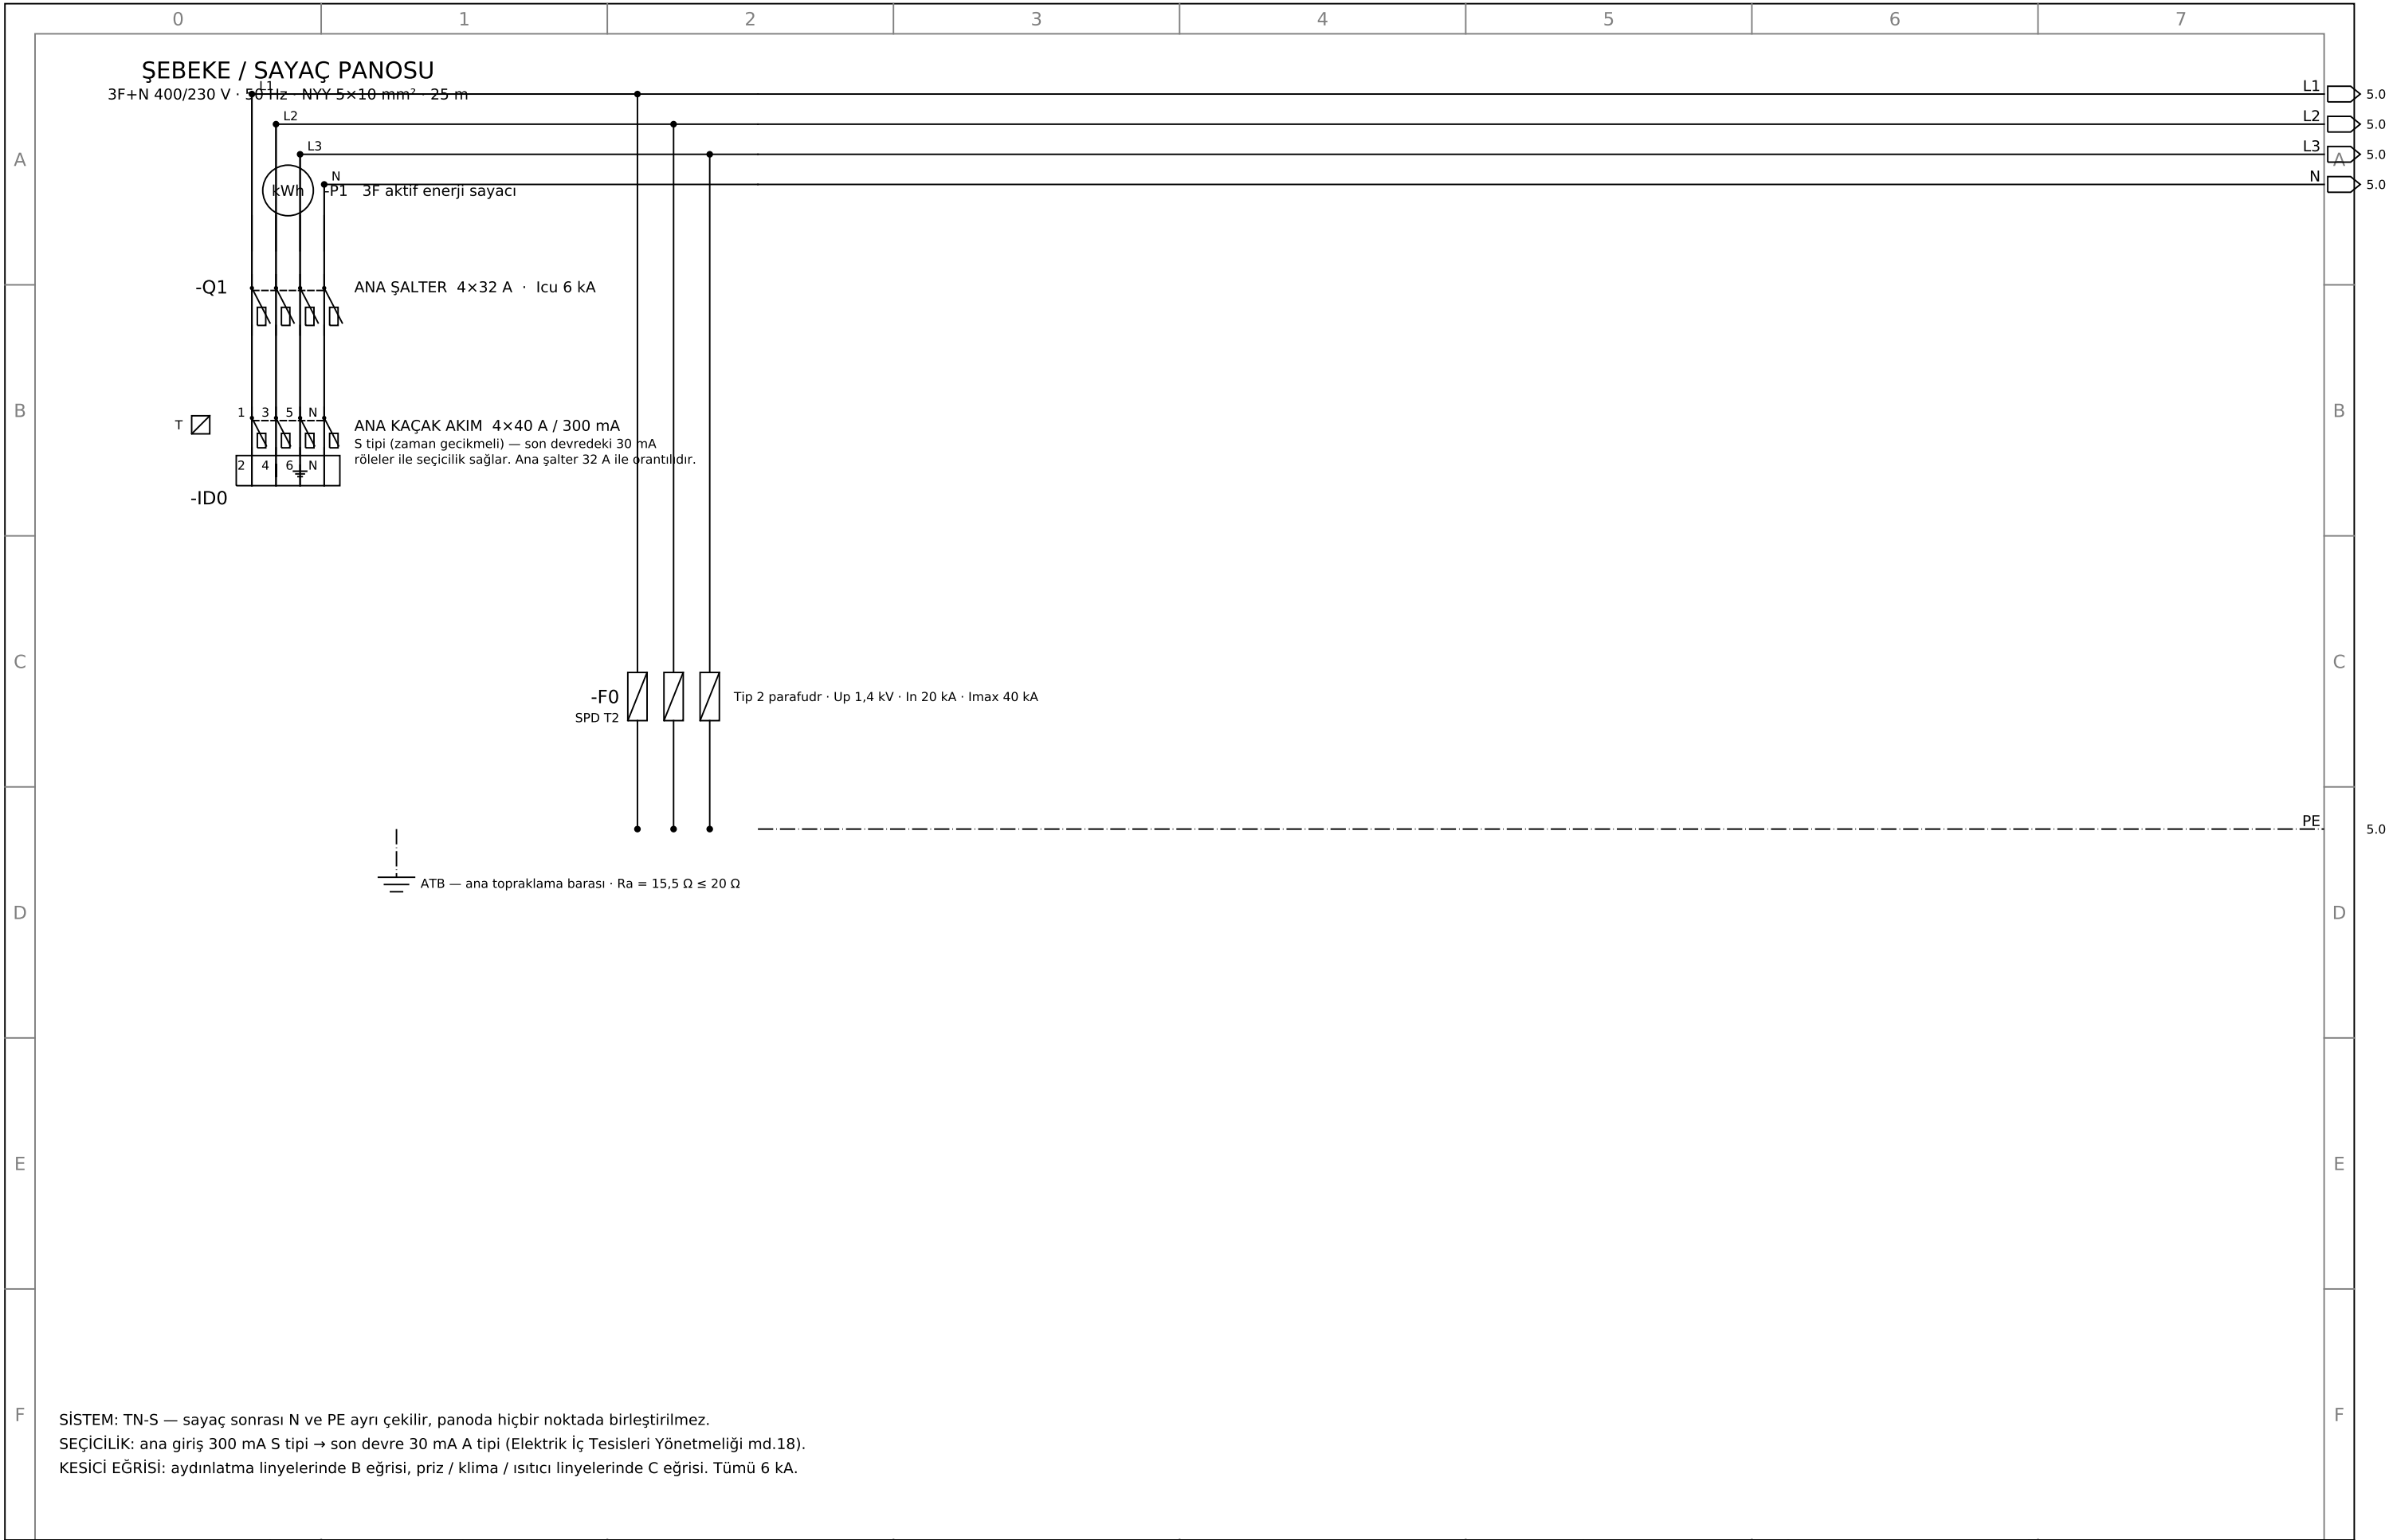


|                             |               |                                        |                                                   |                                 |                           |                        |    |
|-----------------------------|---------------|----------------------------------------|---------------------------------------------------|---------------------------------|---------------------------|------------------------|----|
| Drawn By / Çizen            | CC            | Customer Name / Müşteri Adı            | ÖZEL — MALTEPE / İDEALTEPE                        | Project Number / Proje Numarası | GYM-25-001-001            | Sheet: / Sayfa         | 4  |
| Checked By / Kontrol Eden   | —             | Project Description / Proje Açıklaması | MOBİLYA MAĞAZASI → FONKSİYONEL ANTRENMAN STÜDYOSU |                                 |                           | Next sheet: / Sonraki  | 5  |
| Approved By / Onaylayan     | —             | Panel Name / Pano Adı                  | ADP                                               | Revision / Revizyon             | Rev H                     | Total sheets: / Toplam | 12 |
| Project Date / Proje Tarihi | 17 Eylül 2026 | Page Description / Sayfa Açıklaması    | Incoming Supply / Ana Besleme                     | Standards / Standartlar         | IEC 61439-1&2 · IEC 60617 | Sheet size / Kâğıt     | A3 |

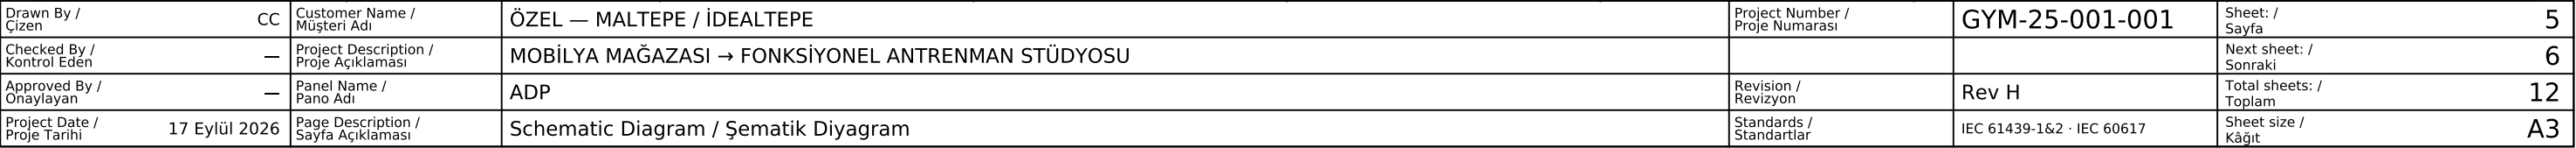

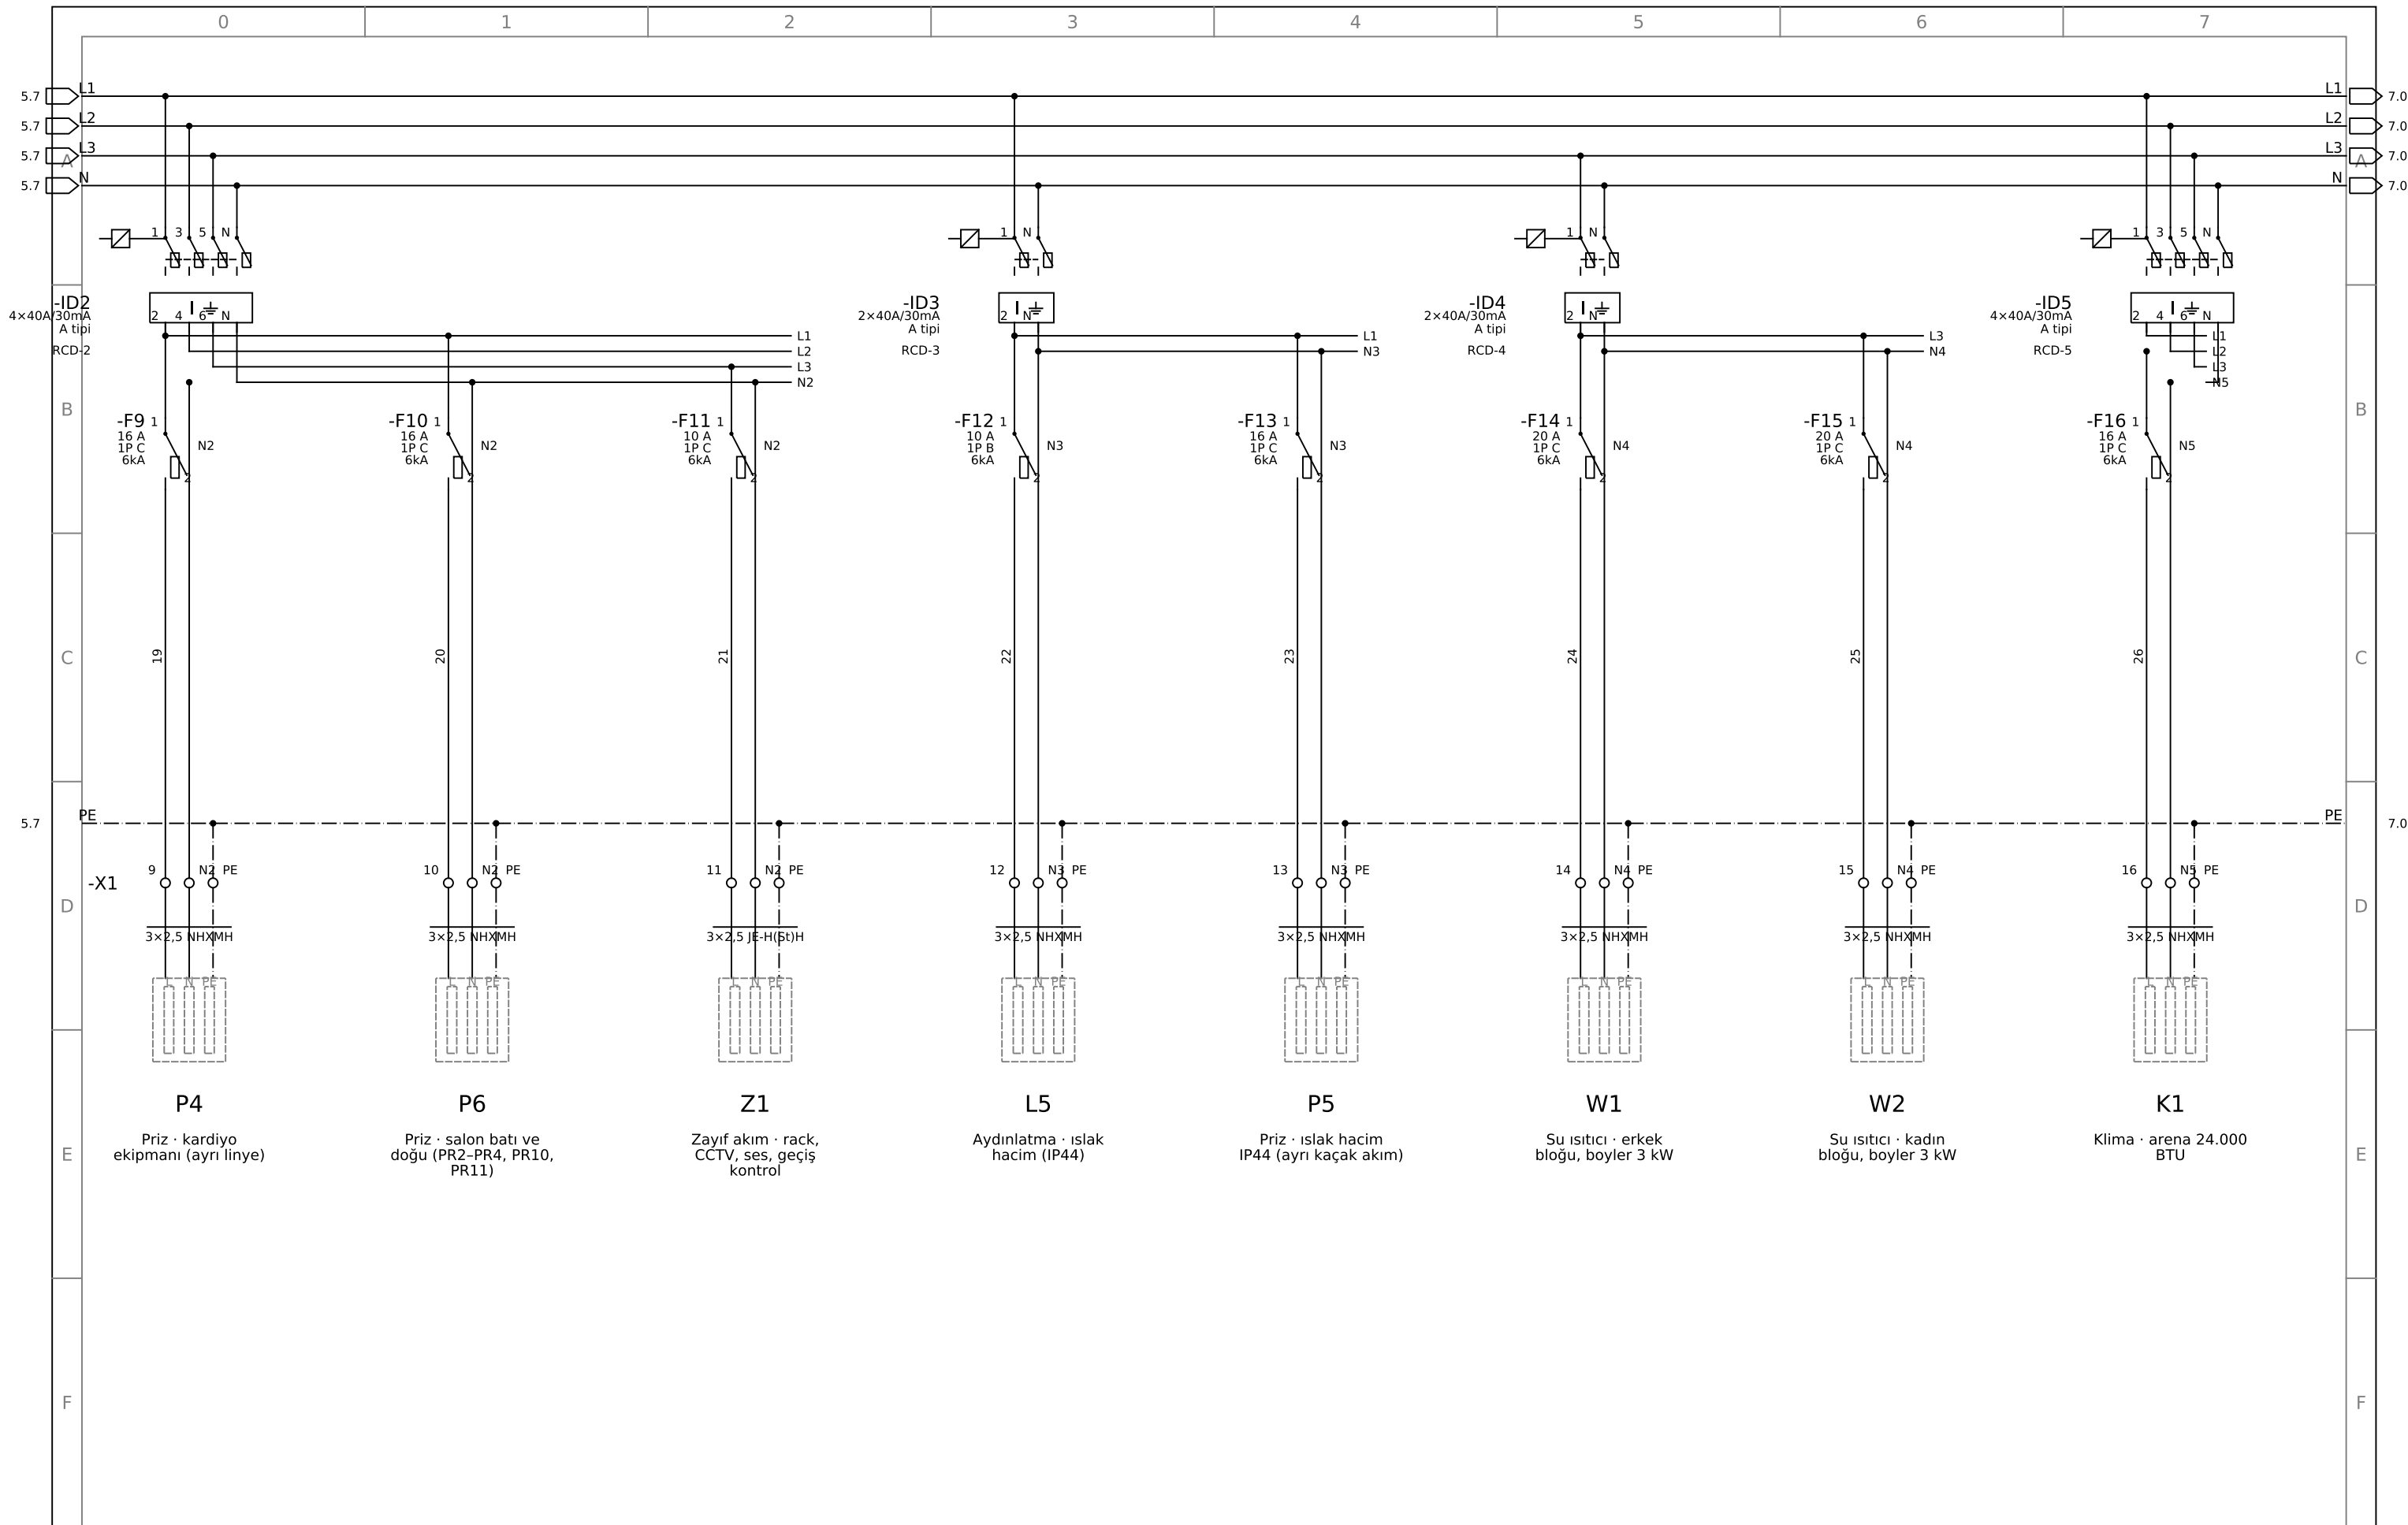

|                             |               |                                        |                                                   |                                 |                           |                        |    |
|-----------------------------|---------------|----------------------------------------|---------------------------------------------------|---------------------------------|---------------------------|------------------------|----|
| Drawn By / Çizen            | CC            | Customer Name / Müşteri Adı            | ÖZEL — MALTEPE / İDEALTEPE                        | Project Number / Proje Numarası | GYM-25-001-001            | Sheet: / Sayfa         | 6  |
| Checked By / Kontrol Eden   | —             | Project Description / Proje Açıklaması | MOBİLYA MAĞAZASI → FONKSİYONEL ANTRENMAN STÜDYOSU |                                 |                           | Next sheet: / Sonraki  | 7  |
| Approved By / Onaylayan     | —             | Panel Name / Pano Adı                  | ADP                                               | Revision / Revizyon             | Rev H                     | Total sheets: / Toplam | 12 |
| Project Date / Proje Tarihi | 17 Eylül 2026 | Page Description / Sayfa Açıklaması    | Schematic Diagram / Şematik Diyagram              | Standards / Standartlar         | IEC 61439-1&2 · IEC 60617 | Sheet size / Kâğıt     | A3 |

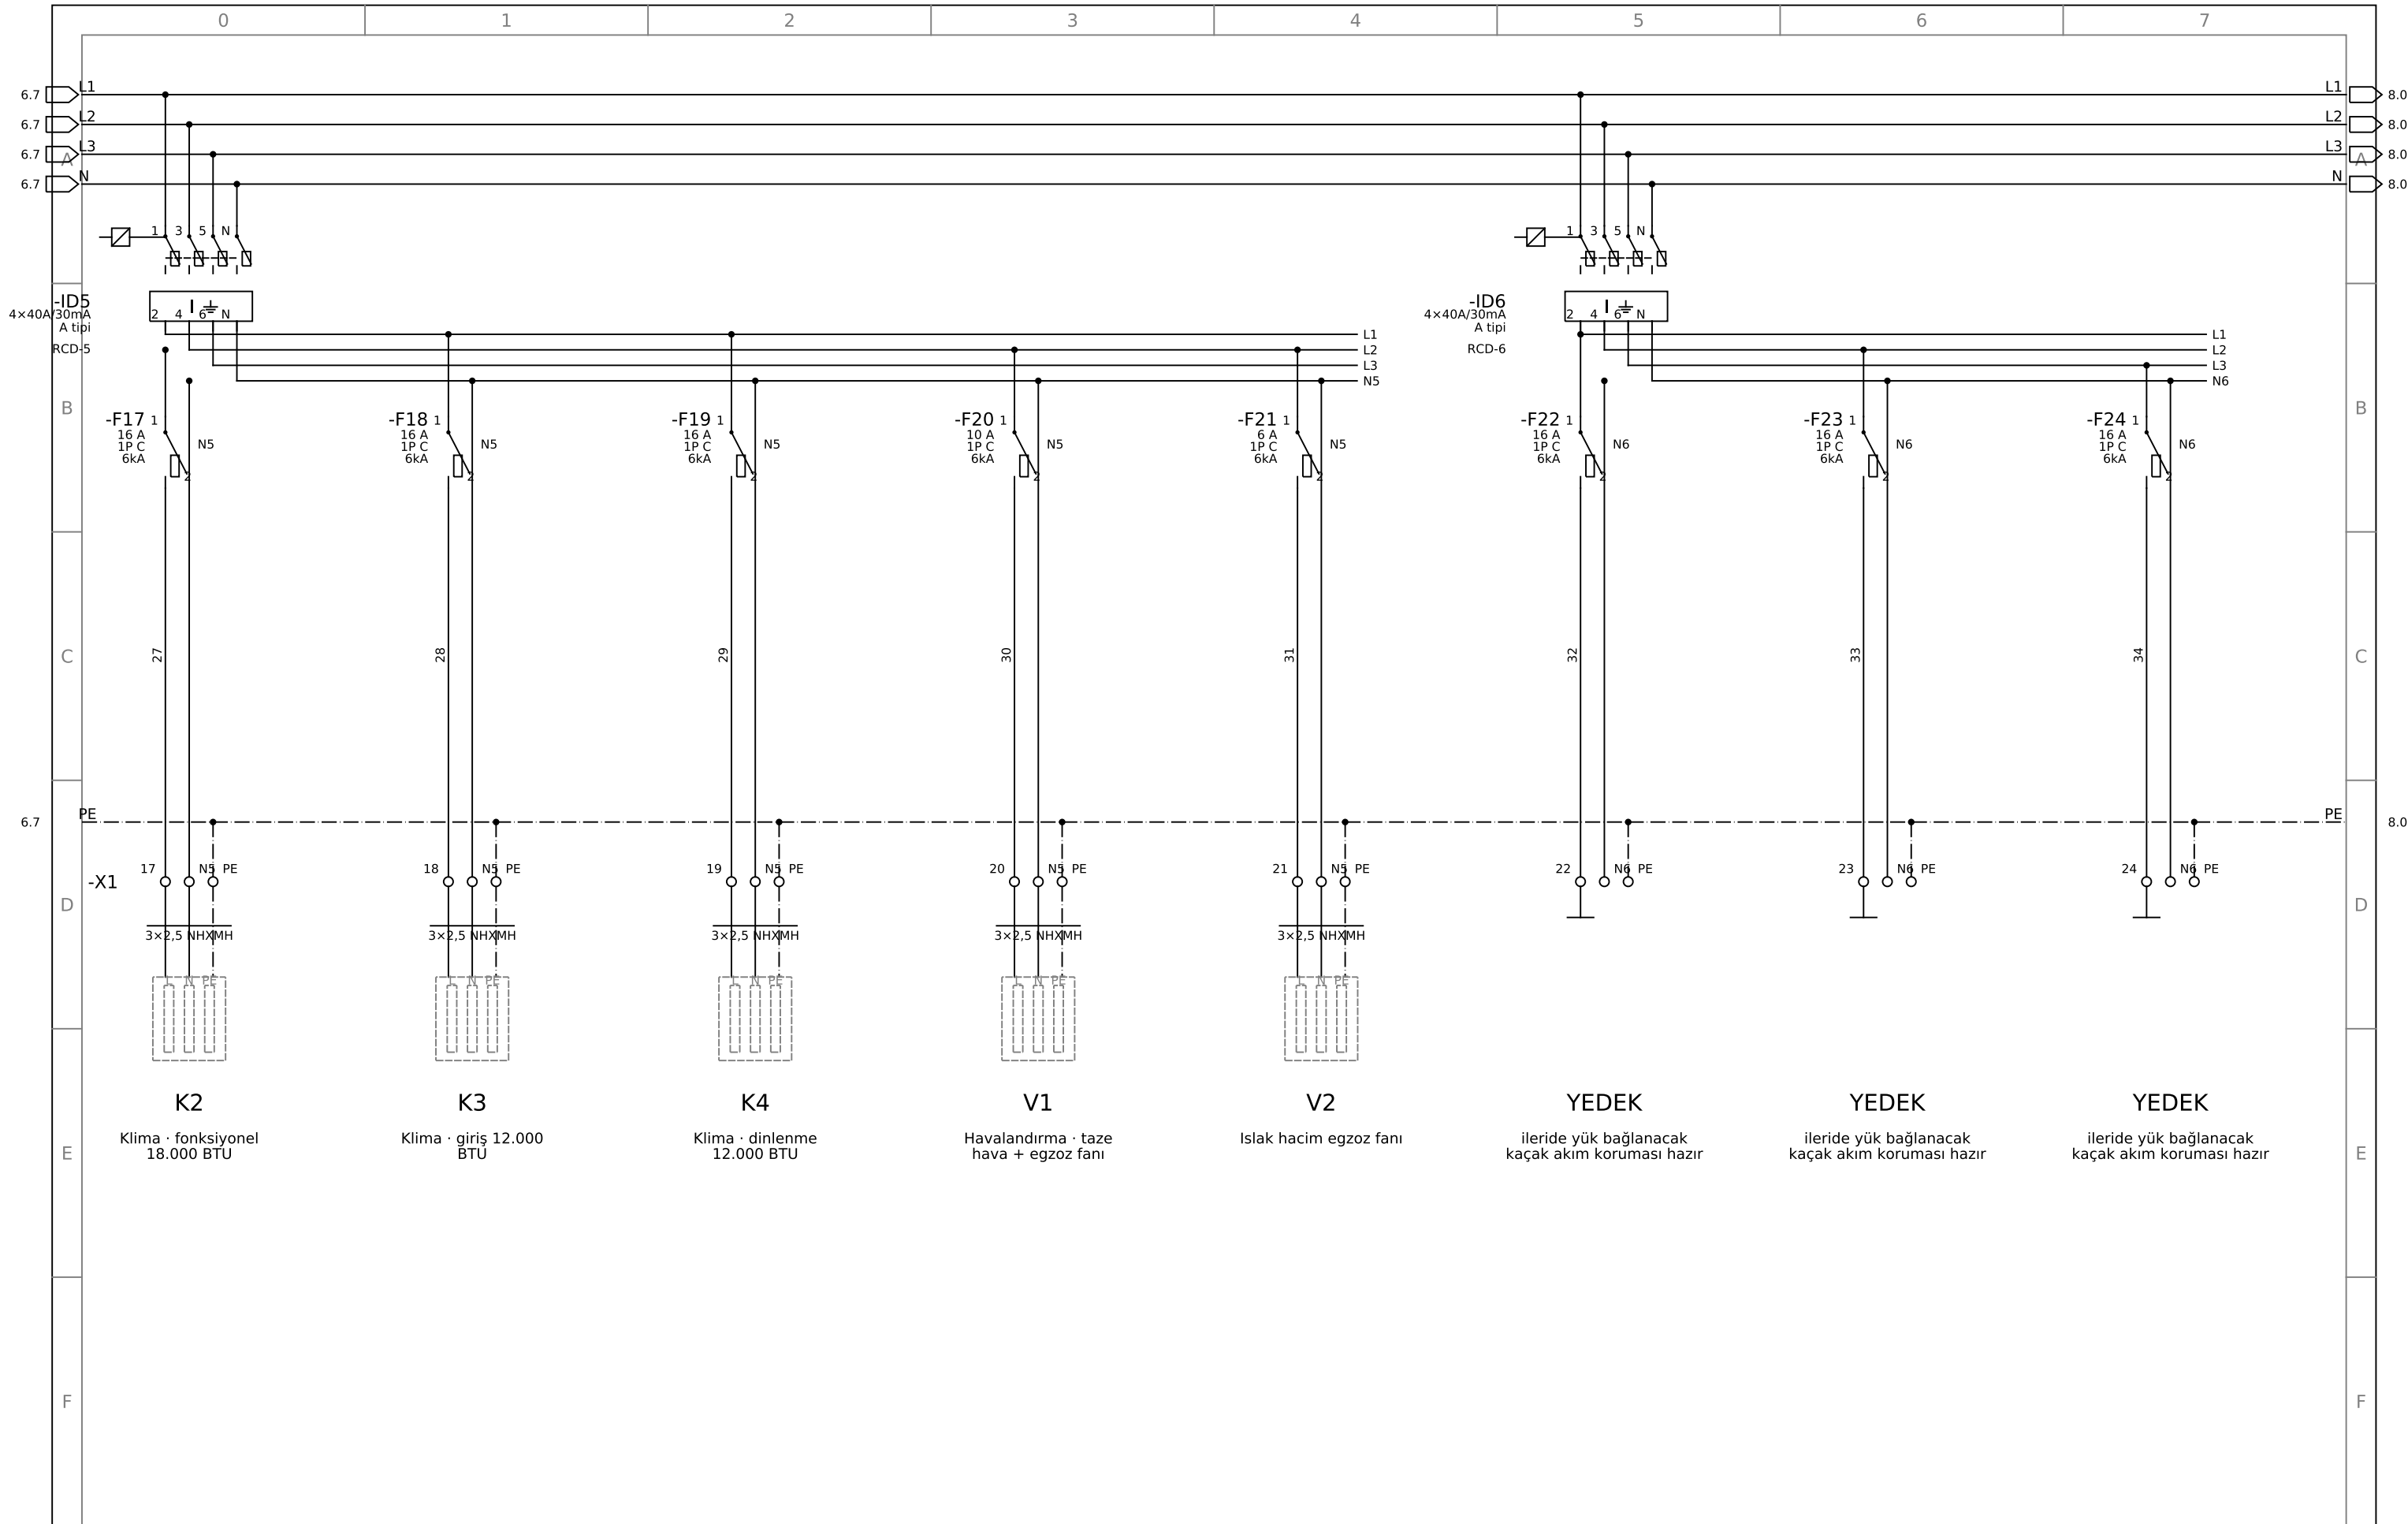

|                             |               |                                        |                                                   |                                 |                           |                        |    |
|-----------------------------|---------------|----------------------------------------|---------------------------------------------------|---------------------------------|---------------------------|------------------------|----|
| Drawn By / Çizen            | CC            | Customer Name / Müşteri Adı            | ÖZEL — MALTEPE / İDEALTEPE                        | Project Number / Proje Numarası | GYM-25-001-001            | Sheet: / Sayfa         | 7  |
| Checked By / Kontrol Eden   | —             | Project Description / Proje Açıklaması | MOBİLYA MAĞAZASI → FONKSİYONEL ANTRENMAN STÜDYOSU |                                 |                           | Next sheet: / Sonraki  | 8  |
| Approved By / Onaylayan     | —             | Panel Name / Pano Adı                  | ADP                                               | Revision / Revizyon             | Rev H                     | Total sheets: / Toplam | 12 |
| Project Date / Proje Tarihi | 17 Eylül 2026 | Page Description / Sayfa Açıklaması    | Schematic Diagram / Şematik Diyagram              | Standards / Standartlar         | IEC 61439-1&2 · IEC 60617 | Sheet size / Kâğıt     | A3 |



## KLEMENS PLANI / TERMINAL DIAGRAM — -X1

|                                |               |                                        |                                           |                                                    |                                  |                                              |                                             |       |            |                            |                                    |                       |                           |    |
|--------------------------------|---------------|----------------------------------------|-------------------------------------------|----------------------------------------------------|----------------------------------|----------------------------------------------|---------------------------------------------|-------|------------|----------------------------|------------------------------------|-----------------------|---------------------------|----|
| A                              |               | KLEMENS                                | LİNYE                                     | İLETKEN                                            | TEL NO                           | KABLO                                        | HEDEF / DESTINATION                         | SAYFA | KAÇAK AKIM | A                          |                                    |                       |                           |    |
|                                |               | 1                                      | L1                                        | L                                                  | 11                               | NHXXMH 3×2,5                                 | Aydınlatma — arena / serbest ağırlık        | 5     | RCD-1      |                            |                                    |                       |                           |    |
|                                |               | L1                                     | N                                         | N1                                                 | NHXXMH 3×2,5                     | Aydınlatma — arena / serbest ağırlık         | 5                                           | RCD-1 |            |                            |                                    |                       |                           |    |
|                                |               | L1                                     | PE                                        | PE                                                 | NHXXMH 3×2,5                     | Aydınlatma — arena / serbest ağırlık         | 5                                           | RCD-1 |            |                            |                                    |                       |                           |    |
| 2                              |               | L2                                     | L                                         | 12                                                 | NHXXMH 3×2,5                     | Aydınlatma — fonksiyonel / kardiyo           | 5                                           | RCD-1 |            |                            |                                    |                       |                           |    |
| B                              |               |                                        | L2                                        | N                                                  | N1                               | NHXXMH 3×2,5                                 | Aydınlatma — fonksiyonel / kardiyo          | 5     | RCD-1      | B                          |                                    |                       |                           |    |
|                                |               |                                        | L2                                        | PE                                                 | PE                               | NHXXMH 3×2,5                                 | Aydınlatma — fonksiyonel / kardiyo          | 5     | RCD-1      |                            |                                    |                       |                           |    |
|                                | 3             | L3                                     | L                                         | 13                                                 | NHXXMH 3×2,5                     | Aydınlatma — dinlenme salonu                 | 5                                           | RCD-1 |            |                            |                                    |                       |                           |    |
|                                |               | L3                                     | N                                         | N1                                                 | NHXXMH 3×2,5                     | Aydınlatma — dinlenme salonu                 | 5                                           | RCD-1 |            |                            |                                    |                       |                           |    |
|                                |               | L3                                     | PE                                        | PE                                                 | NHXXMH 3×2,5                     | Aydınlatma — dinlenme salonu                 | 5                                           | RCD-1 |            |                            |                                    |                       |                           |    |
|                                | 4             | L4                                     | L                                         | 14                                                 | NHXXMH 3×2,5                     | Aydınlatma — giriş / banko                   | 5                                           | RCD-1 |            |                            |                                    |                       |                           |    |
|                                |               | L4                                     | N                                         | N1                                                 | NHXXMH 3×2,5                     | Aydınlatma — giriş / banko                   | 5                                           | RCD-1 |            |                            |                                    |                       |                           |    |
|                                |               | L4                                     | PE                                        | PE                                                 | NHXXMH 3×2,5                     | Aydınlatma — giriş / banko                   | 5                                           | RCD-1 |            |                            |                                    |                       |                           |    |
|                                | 5             | L6                                     | L                                         | 15                                                 | NHXXMH 3×2,5                     | Acil aydınlatma ve yönlendirme               | 5                                           | RCD-1 |            |                            |                                    |                       |                           |    |
|                                |               |                                        | L6                                        | N                                                  | N1                               | NHXXMH 3×2,5                                 | Acil aydınlatma ve yönlendirme              | 5     | RCD-1      |                            |                                    |                       |                           |    |
| C                              |               |                                        | L6                                        | PE                                                 | PE                               | NHXXMH 3×2,5                                 | Acil aydınlatma ve yönlendirme              | 5     | RCD-1      | C                          |                                    |                       |                           |    |
|                                | 6             | P1                                     | L                                         | 16                                                 | NHXXMH 3×2,5                     | Priz — salon kuzey (PR12-PR16, PR1)          | 5                                           | RCD-2 |            |                            |                                    |                       |                           |    |
|                                |               | P1                                     | N                                         | N2                                                 | NHXXMH 3×2,5                     | Priz — salon kuzey (PR12-PR16, PR1)          | 5                                           | RCD-2 |            |                            |                                    |                       |                           |    |
|                                |               | P1                                     | PE                                        | PE                                                 | NHXXMH 3×2,5                     | Priz — salon kuzey (PR12-PR16, PR1)          | 5                                           | RCD-2 |            |                            |                                    |                       |                           |    |
|                                | 7             | P2                                     | L                                         | 17                                                 | NHXXMH 3×2,5                     | Priz — salon güney (PR5-PR9)                 | 5                                           | RCD-2 |            |                            |                                    |                       |                           |    |
|                                |               | P2                                     | N                                         | N2                                                 | NHXXMH 3×2,5                     | Priz — salon güney (PR5-PR9)                 | 5                                           | RCD-2 |            |                            |                                    |                       |                           |    |
|                                |               | P2                                     | PE                                        | PE                                                 | NHXXMH 3×2,5                     | Priz — salon güney (PR5-PR9)                 | 5                                           | RCD-2 |            |                            |                                    |                       |                           |    |
|                                | 8             | P3                                     | L                                         | 18                                                 | NHXXMH 3×2,5                     | Priz — banko, POS, veri                      | 5                                           | RCD-2 |            |                            |                                    |                       |                           |    |
|                                |               |                                        | P3                                        | N                                                  | N2                               | NHXXMH 3×2,5                                 | Priz — banko, POS, veri                     | 5     | RCD-2      |                            |                                    |                       |                           |    |
|                                |               |                                        | P3                                        | PE                                                 | PE                               | NHXXMH 3×2,5                                 | Priz — banko, POS, veri                     | 5     | RCD-2      |                            |                                    |                       |                           |    |
| D                              | 9             | P4                                     | L                                         | 19                                                 | NHXXMH 3×2,5                     | Priz — kardiyo ekipmanı (ayrı linye)         | 6                                           | RCD-2 | D          |                            |                                    |                       |                           |    |
|                                |               | P4                                     | N                                         | N2                                                 | NHXXMH 3×2,5                     | Priz — kardiyo ekipmanı (ayrı linye)         | 6                                           | RCD-2 |            |                            |                                    |                       |                           |    |
|                                |               | P4                                     | PE                                        | PE                                                 | NHXXMH 3×2,5                     | Priz — kardiyo ekipmanı (ayrı linye)         | 6                                           | RCD-2 |            |                            |                                    |                       |                           |    |
|                                | 10            | P6                                     | L                                         | 20                                                 | NHXXMH 3×2,5                     | Priz — salon batı ve doğu (PR2-PR4, PR10, PR | 6                                           | RCD-2 |            |                            |                                    |                       |                           |    |
|                                |               | P6                                     | N                                         | N2                                                 | NHXXMH 3×2,5                     | Priz — salon batı ve doğu (PR2-PR4, PR10, PR | 6                                           | RCD-2 |            |                            |                                    |                       |                           |    |
|                                |               | P6                                     | PE                                        | PE                                                 | NHXXMH 3×2,5                     | Priz — salon batı ve doğu (PR2-PR4, PR10, PR | 6                                           | RCD-2 |            |                            |                                    |                       |                           |    |
|                                | 11            | Z1                                     | L                                         | 21                                                 | JE-H(St)H 3×2,5                  | Zayıf akım — rack, CCTV, ses, geçiş kontrol  | 6                                           | RCD-2 |            |                            |                                    |                       |                           |    |
|                                |               |                                        | Z1                                        | N                                                  | N2                               | JE-H(St)H 3×2,5                              | Zayıf akım — rack, CCTV, ses, geçiş kontrol | 6     |            | RCD-2                      |                                    |                       |                           |    |
|                                |               |                                        | Z1                                        | PE                                                 | PE                               | JE-H(St)H 3×2,5                              | Zayıf akım — rack, CCTV, ses, geçiş kontrol | 6     |            | RCD-2                      |                                    |                       |                           |    |
|                                | 12            | L5                                     | L                                         | 22                                                 | NHXXMH 3×2,5                     | Aydınlatma — ıslak hacim (IP44)              | 6                                           | RCD-3 |            |                            |                                    |                       |                           |    |
| E                              |               |                                        | L5                                        | N                                                  | N3                               | NHXXMH 3×2,5                                 | Aydınlatma — ıslak hacim (IP44)             | 6     | RCD-3      | E                          |                                    |                       |                           |    |
|                                |               |                                        | L5                                        | PE                                                 | PE                               | NHXXMH 3×2,5                                 | Aydınlatma — ıslak hacim (IP44)             | 6     | RCD-3      |                            |                                    |                       |                           |    |
|                                | 13            | P5                                     | L                                         | 23                                                 | NHXXMH 3×2,5                     | Priz — ıslak hacim IP44 (ayrı kaçak akım)    | 6                                           | RCD-3 |            |                            |                                    |                       |                           |    |
|                                |               | P5                                     | N                                         | N3                                                 | NHXXMH 3×2,5                     | Priz — ıslak hacim IP44 (ayrı kaçak akım)    | 6                                           | RCD-3 |            |                            |                                    |                       |                           |    |
|                                |               | P5                                     | PE                                        | PE                                                 | NHXXMH 3×2,5                     | Priz — ıslak hacim IP44 (ayrı kaçak akım)    | 6                                           | RCD-3 |            |                            |                                    |                       |                           |    |
|                                | 14            | W1                                     | L                                         | 24                                                 | NHXXMH 3×2,5                     | Su ısıtıcı — erkek bloğu, boyler 3 kW        | 6                                           | RCD-4 |            |                            |                                    |                       |                           |    |
|                                |               |                                        | W1                                        | N                                                  | N4                               | NHXXMH 3×2,5                                 | Su ısıtıcı — erkek bloğu, boyler 3 kW       | 6     | RCD-4      |                            |                                    |                       |                           |    |
|                                |               |                                        | W1                                        | PE                                                 | PE                               | NHXXMH 3×2,5                                 | Su ısıtıcı — erkek bloğu, boyler 3 kW       | 6     | RCD-4      |                            |                                    |                       |                           |    |
|                                | 15            | W2                                     | L                                         | 25                                                 | NHXXMH 3×2,5                     | Su ısıtıcı — kadın bloğu, boyler 3 kW        | 6                                           | RCD-4 |            |                            |                                    |                       |                           |    |
|                                |               |                                        | W2                                        | N                                                  | N4                               | NHXXMH 3×2,5                                 | Su ısıtıcı — kadın bloğu, boyler 3 kW       | 6     | RCD-4      |                            |                                    |                       |                           |    |
| F                              |               |                                        | W2                                        | PE                                                 | PE                               | NHXXMH 3×2,5                                 | Su ısıtıcı — kadın bloğu, boyler 3 kW       | 6     | RCD-4      | F                          |                                    |                       |                           |    |
|                                | 16            | K1                                     | L                                         | 26                                                 | NHXXMH 3×2,5                     | Klima — arena 24.000 BTU                     | 6                                           | RCD-5 |            |                            |                                    |                       |                           |    |
|                                |               | K1                                     | N                                         | N5                                                 | NHXXMH 3×2,5                     | Klima — arena 24.000 BTU                     | 6                                           | RCD-5 |            |                            |                                    |                       |                           |    |
|                                |               | K1                                     | PE                                        | PE                                                 | NHXXMH 3×2,5                     | Klima — arena 24.000 BTU                     | 6                                           | RCD-5 |            |                            |                                    |                       |                           |    |
|                                | 17            | K2                                     | L                                         | 27                                                 | NHXXMH 3×2,5                     | Klima — fonksiyonel 18.000 BTU               | 7                                           | RCD-5 |            |                            |                                    |                       |                           |    |
|                                |               |                                        | K2                                        | N                                                  | N5                               | NHXXMH 3×2,5                                 | Klima — fonksiyonel 18.000 BTU              | 7     | RCD-5      |                            |                                    |                       |                           |    |
|                                |               |                                        | K2                                        | PE                                                 | PE                               | NHXXMH 3×2,5                                 | Klima — fonksiyonel 18.000 BTU              | 7     | RCD-5      |                            |                                    |                       |                           |    |
|                                | 18            | K3                                     | L                                         | 28                                                 | NHXXMH 3×2,5                     | Klima — giriş 12.000 BTU                     | 7                                           | RCD-5 |            |                            |                                    |                       |                           |    |
|                                |               |                                        | K3                                        | N                                                  | N5                               | NHXXMH 3×2,5                                 | Klima — giriş 12.000 BTU                    | 7     | RCD-5      |                            |                                    |                       |                           |    |
|                                |               |                                        | K3                                        | PE                                                 | PE                               | NHXXMH 3×2,5                                 | Klima — giriş 12.000 BTU                    | 7     | RCD-5      |                            |                                    |                       |                           |    |
| F                              |               |                                        | K3                                        | PE                                                 | PE                               | NHXXMH 3×2,5                                 | Klima — giriş 12.000 BTU                    | 7     | RCD-5      | F                          |                                    |                       |                           |    |
|                                | 19            | K4                                     | L                                         | 29                                                 | NHXXMH 3×2,5                     | Klima — dinlenme 12.000 BTU                  | 7                                           | RCD-5 |            |                            |                                    |                       |                           |    |
|                                |               |                                        | K4                                        | N                                                  | N5                               | NHXXMH 3×2,5                                 | Klima — dinlenme 12.000 BTU                 | 7     | RCD-5      |                            |                                    |                       |                           |    |
|                                |               |                                        | K4                                        | PE                                                 | PE                               | NHXXMH 3×2,5                                 | Klima — dinlenme 12.000 BTU                 | 7     | RCD-5      |                            |                                    |                       |                           |    |
|                                | 20            | V1                                     | L                                         | 30                                                 | NHXXMH 3×2,5                     | Havalandırma — taze hava + egzoz fanı        | 7                                           | RCD-5 |            |                            |                                    |                       |                           |    |
|                                |               |                                        | V1                                        | N5                                                 | NHXXMH 3×2,5                     | Havalandırma — taze hava + egzoz fanı        | 7                                           | RCD-5 |            |                            |                                    |                       |                           |    |
|                                |               |                                        | V1                                        | PE                                                 | PE                               | NHXXMH 3×2,5                                 | Havalandırma — taze hava + egzoz fanı       | 7     | RCD-5      |                            |                                    |                       |                           |    |
|                                | 21            | V2                                     | L                                         | 31                                                 | NHXXMH 3×2,5                     | Islak hacim egzoz fanı                       | 7                                           | RCD-5 |            |                            |                                    |                       |                           |    |
|                                |               |                                        | V2                                        | N5                                                 | NHXXMH 3×2,5                     | Islak hacim egzoz fanı                       | 7                                           | RCD-5 |            |                            |                                    |                       |                           |    |
|                                |               |                                        | V2                                        | PE                                                 | PE                               | NHXXMH 3×2,5                                 | Islak hacim egzoz fanı                      | 7     | RCD-5      |                            |                                    |                       |                           |    |
| Project Date /<br>Proje Tarihi | 17 Eylül 2026 | Page Description /<br>Sayfa Açıklaması |                                           |                                                    | Terminal Diagram / Klemens Planı | Islak hacim egzoz fanı                       | 7                                           | RCD-5 |            | Standards /<br>Standartlar | IEC 61439-1&2 · IEC 60617          | Sheet size /<br>Kâğıt | A3                        |    |
| Drawn By /<br>Çizen            |               | CC                                     | Customer Name /<br>Müşteri Adı            | ÖZEL — MALTEPE / IDEALTEPE                         |                                  |                                              |                                             |       |            |                            | Project Number /<br>Proje Numarası | GYM-25-001-001        | Sheet: /<br>Sayfa         | 9  |
| Checked By /<br>Kontrol Eden   |               |                                        | Project Description /<br>Proje Açıklaması | EMOBİLYA MAĞAZASI → FONKSİYONEL ANTRENMAN STÜDYOSU |                                  |                                              |                                             |       |            |                            |                                    |                       | Next sheet: /<br>Sonraki  | 10 |
| Approved By /<br>Onaylayan     |               |                                        | Panel Name /<br>Pano Adı                  | ADP                                                |                                  |                                              |                                             |       |            |                            |                                    |                       | Total sheets: /<br>Toplam | 12 |
|                                |               |                                        |                                           |                                                    |                                  |                                              |                                             |       |            |                            |                                    |                       |                           |    |

| |
|---|
|                             | 0                                                           | 1   | 2          | 3                                      | 4    | 5                                                 | 6         | 7         |      |                                 
| A                           | PANO ÖNDEN GÖRÜNÜŞ / PANEL FRONT VIEW — ölçek 1:5           |   |            |                                        |      |                                                   |           |           | A    |                                 |      
| B                           |                                                             |   |            |                                        |      |                                                   |           |           | B    |                                 |      
| C                           | ADP · 800×1000×250 mm · IP54 · Form 2b · sac gövde RAL 7035 |   |            |                                        |      |                                                   |           |           | C    |                                 |      
| D                           | R1                                                          | <table><tr><td>-Q1</td><td>-ID0</td><td>-F0</td><td colspan="4">BOŞ 12 MOD</td></tr><tr><td>4</td><td>4</td><td>4</td><td colspan="4"></td></tr></table>   |            |                                        |      |                                                   |           |           | -Q1  | -ID0                            | -F0  | BOŞ 12 MOD                |      |                        |      | 4         | 4         | 4    |      |      |      |      | D    |      |      |   |   |   |   |   |   |   |   |   |   |   |   |   |   |   |   |   |  |
| -Q1                         | -ID0                                                        | -F0   | BOŞ 12 MOD | |
| 4                           | 4                                                           | 4   | |
| E                           | R2                                                          | <table><tr><td>-ID1</td><td>-F1</td><td>-F2</td><td>-F3</td><td>-F4</td><td>-F5</td><td>-ID2</td><td>BOŞ 1 MOD</td></tr><tr><td>4</td><td>3</td><td>3</td><td>3</td><td>3</td><td>3</td><td>4</td><td></td></tr></table>   |            |                                        |      |                                                   |           |           | -ID1 | -F1                             | -F2  | -F3                       | -F4  | -F5                    | -ID2 | BOŞ 1 MOD | 4         | 3    | 3    | 3    | 3    | 3    | 4    |      | E    |   |   |   |   |   |   |   |   |   |   |   |   |   |   |   |   |   |  |
| -ID1                        | -F1                                                         | -F2   | -F3        | -F4                                    | -F5  | -ID2                                              | BOŞ 1 MOD |           |      
| 4                           | 3                                                           | 3   | 3          | 3                                      | 3    | 4                                                 |           |           
| F                           | R3                                                          | <table><tr><td>-F6</td><td>-F7</td><td>-F8</td><td>-F9</td><td>-F10</td><td>-F11</td><td>-ID3</td><td>-F12</td><td>BOŞ 1 MOD</td></tr><tr><td>3</td><td>3</td><td>3</td><td>3</td><td>3</td><td>3</td><td>2</td><td>3</td><td></td></tr></table>   |            |                                        |      |                                                   |           |           | -F6  | -F7                             | -F8  | -F9                       | -F10 | -F11                   | -ID3 | -F12      | BOŞ 1 MOD | 3    | 3    | 3    | 3    | 3    | 3    | 2    | 3    |   | F |   |   |   |   |   |   |   |   |   |   |   |   |   |   |   |  |
| -F6                         | -F7                                                         | -F8   | -F9        | -F10                                   | -F11 | -ID3                                              | -F12      | BOŞ 1 MOD |      |                                 
| 3                           | 3                                                           | 3   | 3          | 3                                      | 3    | 2                                                 | 3         |           |      
|                             | R4                                                          | <table><tr><td>-F13</td><td>-ID4</td><td>-F14</td><td>-F15</td><td>-ID5</td><td>-F16</td><td>-F17</td><td>-F18</td><td>-F19</td><td>-F20</td><td>-F21</td><td>-ID6</td><td>-F22</td><td>-F23</td><td>-F24</td><td>-F25</td><td>-F26</td></tr><tr><td>3</td><td>2</td><td>3</td><td>3</td><td>4</td><td>3</td><td>3</td><td>3</td><td>3</td><td>3</td><td>3</td><td>4</td><td>1</td><td>1</td><td>1</td><td>1</td><td>3</td></tr></table> |            |                                        |      |                                                   |           |           | -F13 | -ID4                            | -F14 | -F15                      | -ID5 | -F16                   | -F17 | -F18      | -F19      | -F20 | -F21 | -ID6 | -F22 | -F23 | -F24 | -F25 | -F26 | 3 | 2 | 3 | 3 | 4 | 3 | 3 | 3 | 3 | 3 | 3 | 4 | 1 | 1 | 1 | 1 | 3 |  |
| -F13                        | -ID4                                                        | -F14   | -F15       | -ID5                                   | -F16 | -F17                                              | -F18      | -F19      | -F20 | -F21                            | -ID6 | -F22                      | -F23 | -F24                   | -F25 | -F26      |           |      
| 3                           | 2                                                           | 3   | 3          | 4                                      | 3    | 3                                                 | 3         | 3         | 3    | 3                               | 4    | 1                         | 1    | 1                      | 1    | 3         |           |      
| SIRA                        |                                                             | CİHAZ   |            | MODÜL                                  |      | AÇIKLAMA                                          |           |           
| R1                          |                                                             | -Q1   |            | 4                                      |      | ANA ŞALTER 4×32 A                                 |           |           
| R1                          |                                                             | -ID0   |            | 4                                      |      | ANA KAÇAK AKIM 4×40 A/300 mA                      |           |           
| R1                          |                                                             | -F0   |            | 4                                      |      | SPD Tip 2                                         |           |           
| R2                          |                                                             | -ID1   |            | 4                                      |      | 4×40 A / 30 mA, A tipi                            |           |           
| R2                          |                                                             | -F1   |            | 3                                      |      | L1 10A B                                          |           |           
| R2                          |                                                             | -F2   |            | 3                                      |      | L2 10A B                                          |           |           
| R2                          |                                                             | -F3   |            | 3                                      |      | L3 10A B                                          |           |           
| R2                          |                                                             | -F4   |            | 3                                      |      | L4 10A B                                          |           |           
| R2                          |                                                             | -F5   |            | 3                                      |      | L6 6A B                                           |           |           
| R2                          |                                                             | -ID2   |            | 4                                      |      | 4×40 A / 30 mA, A tipi                            |           |           
| R3                          |                                                             | -F6   |            | 3                                      |      | P1 16A C                                          |           |           
| R3                          |                                                             | -F7   |            | 3                                      |      | P2 16A C                                          |           |           
| R3                          |                                                             | -F8   |            | 3                                      |      | P3 16A C                                          |           |           
| R3                          |                                                             | -F9   |            | 3                                      |      | P4 16A C                                          |           |           
| R3                          |                                                             | -F10   |            | 3                                      |      | P6 16A C                                          |           |           
| R3                          |                                                             | -F11   |            | 3                                      |      | Z1 10A C                                          |           |           
| R3                          |                                                             | -ID3   |            | 2                                      |      | 2×40 A / 30 mA, A tipi                            |           |           
| R3                          |                                                             | -F12   |            | 3                                      |      | L5 10A B                                          |           |           
| R4                          |                                                             | -F13   |            | 3                                      |      | P5 16A C                                          |           |           
| R4                          |                                                             | -ID4   |            | 2                                      |      | 2×40 A / 30 mA, A tipi                            |           |           
| R4                          |                                                             | -F14   |            | 3                                      |      | W1 20A C                                          |           |           
| R4                          |                                                             | -F15   |            | 3                                      |      | W2 20A C                                          |           |           
| R4                          |                                                             | -ID5   |            | 4                                      |      | 4×40 A / 30 mA, A tipi                            |           |           
| R4                          |                                                             | -F16   |            | 3                                      |      | K1 16A C                                          |           |           
| R4                          |                                                             | -F17   |            | 3                                      |      | K2 16A C                                          |           |           
| R4                          |                                                             | -F18   |            | 3                                      |      | K3 16A C                                          |           |           
| R4                          |                                                             | -F19   |            | 3                                      |      | K4 16A C                                          |           |           
| R4                          |                                                             | -F20   |            | 3                                      |      | V1 10A C                                          |           |           
| R4                          |                                                             | -F21   |            | 3                                      |      | V2 6A C                                           |           |           
| R4                          |                                                             | -ID6   |            | 4                                      |      | 4×40 A / 30 mA, A tipi                            |           |           
| R4                          |                                                             | -F22   |            | 1                                      |      | Y1 16A C                                          |           |           
| R4                          |                                                             | -F23   |            | 1                                      |      | Y2 16A C                                          |           |           
| R4                          |                                                             | -F24   |            | 1                                      |      | Y3 16A C                                          |           |           
| R4                          |                                                             | -F25   |            | 1                                      |      | Y4 16A C                                          |           |           
| R4                          |                                                             | -F26   |            | 3                                      |      | Z2 6A C                                           |           |           
| Drawn By / Çizen            |                                                             | CC   |            | Customer Name / Müşteri Adı            |      | ÖZEL — MALTEPE / İDEALTEPE                        |           |           |      | Project Number / Proje Numarası |      | GYM-25-001-001            |      | Sheet: / Sayfa         |      | 10        |           |      
| Checked By / Kontrol Eden   |                                                             | —   |            | Project Description / Proje Açıklaması |      | MOBİLYA MAĞAZASI → FONKSİYONEL ANTRENMAN STÜDYOSU |           |           |      |                                 |      |                           |      | Next sheet: / Sonraki  |      | 11        |           |      
| Approved By / Onaylayan     |                                                             | —   |            | Panel Name / Pano Adı                  |      | ADP                                               |           |           |      | Revision / Revizyon             |      | Rev H                     |      | Total sheets: / Toplam |      | 12        |           |      
| Project Date / Proje Tarihi |                                                             | 17 Eylül 2026   |            | Page Description / Sayfa Açıklaması    |      | Panel Overview / Pano Önden Görünüş               |           |           |      | Standards / Standartlar         |      | IEC 61439-1&2 · IEC 60617 |      | Sheet size / Kâğıt     |      | A3        |           |      

| SIRA | CİHAZ | MODÜL | AÇIKLAMA                     |
|------|-------|-------|------------------------------|
| R1   | -Q1   | 4     | ANA ŞALTER 4×32 A            |
| R1   | -ID0  | 4     | ANA KAÇAK AKIM 4×40 A/300 mA |
| R1   | -F0   | 4     | SPD Tip 2                    |
| R2   | -ID1  | 4     | 4×40 A / 30 mA, A tipi       |
| R2   | -F1   | 3     | L1 10A B                     |
| R2   | -F2   | 3     | L2 10A B                     |
| R2   | -F3   | 3     | L3 10A B                     |
| R2   | -F4   | 3     | L4 10A B                     |
| R2   | -F5   | 3     | L6 6A B                      |
| R2   | -ID2  | 4     | 4×40 A / 30 mA, A tipi       |
| R3   | -F6   | 3     | P1 16A C                     |
| R3   | -F7   | 3     | P2 16A C                     |
| R3   | -F8   | 3     | P3 16A C                     |
| R3   | -F9   | 3     | P4 16A C                     |
| R3   | -F10  | 3     | P6 16A C                     |
| R3   | -F11  | 3     | Z1 10A C                     |
| R3   | -ID3  | 2     | 2×40 A / 30 mA, A tipi       |
| R3   | -F12  | 3     | L5 10A B                     |
| R4   | -F13  | 3     | P5 16A C                     |
| R4   | -ID4  | 2     | 2×40 A / 30 mA, A tipi       |
| R4   | -F14  | 3     | W1 20A C                     |
| R4   | -F15  | 3     | W2 20A C                     |
| R4   | -ID5  | 4     | 4×40 A / 30 mA, A tipi       |
| R4   | -F16  | 3     | K1 16A C                     |
| R4   | -F17  | 3     | K2 16A C                     |
| R4   | -F18  | 3     | K3 16A C                     |
| R4   | -F19  | 3     | K4 16A C                     |
| R4   | -F20  | 3     | V1 10A C                     |
| R4   | -F21  | 3     | V2 6A C                      |
| R4   | -ID6  | 4     | 4×40 A / 30 mA, A tipi       |
| R4   | -F22  | 1     | Y1 16A C                     |
| R4   | -F23  | 1     | Y2 16A C                     |
| R4   | -F24  | 1     | Y3 16A C                     |
| R4   | -F25  | 1     | Y4 16A C                     |
| R4   | -F26  | 3     | Z2 6A C                      |

|                             |                                                                                |               |                                        |                           |                                                   |                                      |                                     |      |                    |                                 |       |                           |        |                        |   |    |
|-----------------------------|--------------------------------------------------------------------------------|---------------|----------------------------------------|---------------------------|---------------------------------------------------|--------------------------------------|-------------------------------------|------|--------------------|---------------------------------|-------|---------------------------|--------|------------------------|---|----|
|                             | 0                                                                              | 1             | 2                                      | 3                         | 4                                                 | 5                                    | 6                                   | 7    |                    |                                 |       |                           |        |                        |   |    |
| A                           | ADP YÜKLEME CETVELİ / LOAD SCHEDULE                                            |               |                                        |                           |                                                   |                                      |                                     |      |                    |                                 |       |                           |        |                        | A |    |
|                             | Grup kaçak akım röleleri ve kapsadıkları linyeler ayrı sütunda gösterilmiştir. |               |                                        |                           |                                                   |                                      |                                     |      |                    |                                 |       |                           |        |                        |   |    |
|                             | NO                                                                             | LİNYE         | MAHAL / YÜK                            | FAZ                       | KESİCİ                                            | KAÇAK AKIM (GRUP)                    | KABLO                               | BORU | UZUNLUK            | Pb (kW)                         | cos φ | Ib (A)                    | ΔU (%) | SONUÇ                  |   |    |
|                             | 1                                                                              | L1            | Aydınlatma — arena / serbest ağırlık   | L2                        | 10 A · 1P B · 6 kA                                | RCD-1 · 4×40 A / 30 mA A tipi        | NHXMH 3×2,5                         | Ø20  | 14 m               | 0,28                            | 0,95  | 1,3                       | 0,13   | UYGUN                  |   |    |
|                             | 2                                                                              | L2            | Aydınlatma — fonksiyonel / kardiyo     | L3                        | 10 A · 1P B · 6 kA                                | ↑ aynı grup                          | NHXMH 3×2,5                         | Ø20  | 11 m               | 0,12                            | 0,95  | 0,5                       | 0,05   | UYGUN                  |   |    |
|                             | 3                                                                              | L3            | Aydınlatma — dinlenme salonu           | L1                        | 10 A · 1P B · 6 kA                                | ↑ aynı grup                          | NHXMH 3×2,5                         | Ø20  | 14 m               | 0,12                            | 0,95  | 0,5                       | 0,06   | UYGUN                  |   |    |
|                             | 4                                                                              | L4            | Aydınlatma — giriş / banko             | L3                        | 10 A · 1P B · 6 kA                                | ↑ aynı grup                          | NHXMH 3×2,5                         | Ø20  | 12 m               | 0,08                            | 0,95  | 0,4                       | 0,03   | UYGUN                  |   |    |
|                             | 5                                                                              | L6            | Acil aydınlatma ve yönlendirme         | L2                        | 6 A · 1P B · 6 kA                                 | ↑ aynı grup                          | NHXMH 3×2,5                         | Ø20  | 10 m               | 0,06                            | 0,95  | 0,3                       | 0,02   | UYGUN                  |   |    |
| B                           | 6                                                                              | P1            | Priz — salon kuzey (PR12-PR16, PR1)    | L1                        | 16 A · 1P C · 6 kA                                | RCD-2 · 4×40 A / 30 mA A tipi        | NHXMH 3×2,5                         | Ø20  | 8 m                | 0,90                            | 0,90  | 4,3                       | 0,24   | UYGUN                  | B |    |
|                             | 7                                                                              | P2            | Priz — salon güney (PR5-PR9)           | L3                        | 16 A · 1P C · 6 kA                                | ↑ aynı grup                          | NHXMH 3×2,5                         | Ø20  | 16 m               | 0,75                            | 0,90  | 3,6                       | 0,42   | UYGUN                  |   |    |
|                             | 8                                                                              | P3            | Priz — banko, POS, veri                | L2                        | 16 A · 1P C · 6 kA                                | ↑ aynı grup                          | NHXMH 3×2,5                         | Ø20  | 9 m                | 1,00                            | 0,90  | 4,8                       | 0,30   | UYGUN                  |   |    |
|                             | 9                                                                              | P4            | Priz — kardiyo ekipmanı (ayrı linye)   | L1                        | 16 A · 1P C · 6 kA                                | ↑ aynı grup                          | NHXMH 3×2,5                         | Ø20  | 17 m               | 2,40                            | 0,90  | 11,6                      | 1,40   | UYGUN                  |   |    |
|                             | 10                                                                             | P6            | Priz — salon batı ve doğu (PR2-PR4, PR | L1                        | 16 A · 1P C · 6 kA                                | ↑ aynı grup                          | NHXMH 3×2,5                         | Ø20  | 10 m               | 0,75                            | 0,90  | 3,6                       | 0,27   | UYGUN                  |   |    |
|                             | 11                                                                             | Z1            | Zayıf akım — rack, CCTV, ses, geçiş ko | L3                        | 10 A · 1P C · 6 kA                                | ↑ aynı grup                          | JE-H(St)H 3×2,5                     | Ø20  | 9 m                | 0,60                            | 0,90  | 2,9                       | 0,18   | UYGUN                  |   |    |
|                             | 12                                                                             | L5            | Aydınlatma — ıslak hacim (IP44)        | L1                        | 10 A · 1P B · 6 kA                                | RCD-3 · 2×40 A / 30 mA A tipi        | NHXMH 3×2,5                         | Ø20  | 16 m               | 0,11                            | 0,95  | 0,5                       | 0,06   | UYGUN                  |   |    |
|                             | 13                                                                             | P5            | Priz — ıslak hacim IP44 (ayrı kaçak ak | L3                        | 16 A · 1P C · 6 kA                                | ↑ aynı grup                          | NHXMH 3×2,5                         | Ø20  | 16 m               | 0,50                            | 0,90  | 2,4                       | 0,27   | UYGUN                  |   |    |
| C                           | 14                                                                             | W1            | Su ısıtıcı — erkek bloğu, boyler 3 kW  | L3                        | 20 A · 1P C · 6 kA                                | RCD-4 · 2×40 A / 30 mA A tipi        | NHXMH 3×2,5                         | Ø20  | 16 m               | 3,00                            | 1,00  | 13,0                      | 1,65   | UYGUN                  | C |    |
|                             | 15                                                                             | W2            | Su ısıtıcı — kadın bloğu, boyler 3 kW  | L3                        | 20 A · 1P C · 6 kA                                | ↑ aynı grup                          | NHXMH 3×2,5                         | Ø20  | 19 m               | 3,00                            | 1,00  | 13,0                      | 1,97   | UYGUN                  |   |    |
|                             | 16                                                                             | K1            | Klima — arena 24.000 BTU               | L2                        | 16 A · 1P C · 6 kA                                | RCD-5 · 4×40 A / 30 mA A tipi        | NHXMH 3×2,5                         | Ø20  | 18 m               | 2,20                            | 0,85  | 11,3                      | 1,32   | UYGUN                  |   |    |
|                             | 17                                                                             | K2            | Klima — fonksiyonel 18.000 BTU         | L2                        | 16 A · 1P C · 6 kA                                | ↑ aynı grup                          | NHXMH 3×2,5                         | Ø20  | 13 m               | 1,70                            | 0,85  | 8,7                       | 0,73   | UYGUN                  |   |    |
|                             | 18                                                                             | K3            | Klima — giriş 12.000 BTU               | L1                        | 16 A · 1P C · 6 kA                                | ↑ aynı grup                          | NHXMH 3×2,5                         | Ø20  | 12 m               | 1,15                            | 0,85  | 5,9                       | 0,48   | UYGUN                  |   |    |
|                             | 19                                                                             | K4            | Klima — dinlenme 12.000 BTU            | L1                        | 16 A · 1P C · 6 kA                                | ↑ aynı grup                          | NHXMH 3×2,5                         | Ø20  | 15 m               | 1,15                            | 0,85  | 5,9                       | 0,58   | UYGUN                  |   |    |
|                             | 20                                                                             | V1            | Havalandırma — taze hava + egzoz fanı  | L2                        | 10 A · 1P C · 6 kA                                | ↑ aynı grup                          | NHXMH 3×2,5                         | Ø20  | 14 m               | 0,45                            | 0,85  | 2,3                       | 0,21   | UYGUN                  |   |    |
|                             | 21                                                                             | V2            | Islak hacim egzoz fanı                 | L2                        | 6 A · 1P C · 6 kA                                 | ↑ aynı grup                          | NHXMH 3×2,5                         | Ø20  | 16 m               | 0,12                            | 0,85  | 0,6                       | 0,07   | UYGUN                  |   |    |
| D                           | 22                                                                             | Y1            | YEDEK — ileride yük bağlanacak         | L1                        | 16 A · 1P C · 6 kA                                | RCD-6 · 4×40 A / 30 mA A tipi        | —                                   | —    | —                  | —                               | —     | —                         | —      | YEDEK                  | D |    |
|                             | 23                                                                             | Y2            | YEDEK — ileride yük bağlanacak         | L2                        | 16 A · 1P C · 6 kA                                | ↑ aynı grup                          | —                                   | —    | —                  | —                               | —     | —                         | —      | YEDEK                  |   |    |
|                             | 24                                                                             | Y3            | YEDEK — ileride yük bağlanacak         | L3                        | 16 A · 1P C · 6 kA                                | ↑ aynı grup                          | —                                   | —    | —                  | —                               | —     | —                         | —      | YEDEK                  |   |    |
|                             | 25                                                                             | Y4            | YEDEK — ileride yük bağlanacak         | L1                        | 16 A · 1P C · 6 kA                                | ↑ aynı grup                          | —                                   | —    | —                  | —                               | —     | —                         | —      | YEDEK                  |   |    |
|                             | 26                                                                             | Z2            | Yangın algılama paneli (kesintisiz)    | L1                        | 6 A · 1P C · 6 kA                                 | — kaçak akım rölesi yok (kesintisiz) | JE-H(St)H 3×2,5                     | Ø20  | 10 m               | 0,15                            | 0,90  | 0,7                       | 0,05   | UYGUN                  |   |    |
| E                           | ÖZET / SUMMARY                                                                 |               |                                        |                           |                                                   |                                      |                                     |      |                    |                                 |       |                           |        |                        | E |    |
|                             | Bağlı güç / Connected                                                          |               | 20,59 kW                               | Talep gücü / Demand       |                                                   | 14,63 kW                             | L1 / L2 / L3 (kW)                   |      | 4,86 / 4,91 / 4,87 | Faz dengesizliği / Imbalance    |       | %1,0                      |        |                        |   |    |
|                             | Ana şalter / Main switch                                                       |               | 4×32 A                                 | Ana kaçak akım / Main RCD |                                                   | 4×40 A / 300 mA S tipi               | Grup kaçak akım sayısı / RCD groups |      | 7 adet             | Toplam ΔU / Total               |       | %2,49                     |        |                        |   |    |
| F                           |                                                                                |               |                                        |                           |                                                   |                                      |                                     |      |                    |                                 |       |                           |        |                        | F |    |
| Drawn By / Çizen            |                                                                                | CC            | Customer Name / Müşteri Adı            |                           | ÖZEL — MALTEPE / İDEALTEPE                        |                                      |                                     |      |                    | Project Number / Proje Numarası |       | GYM-25-001-001            |        | Sheet: / Sayfa         |   | 11 |
| Checked By / Kontrol Eden   |                                                                                | —             | Project Description / Proje Açıklaması |                           | MOBİLYA MAĞAZASI → FONKSİYONEL ANTRENMAN STÜDYOSU |                                      |                                     |      |                    |                                 |       |                           |        | Next sheet: / Sonraki  |   | 12 |
| Approved By / Onaylayan     |                                                                                | —             | Panel Name / Pano Adı                  |                           | ADP                                               |                                      |                                     |      |                    | Revision / Revizyon             |       | Rev H                     |        | Total sheets: / Toplam |   | 12 |
| Project Date / Proje Tarihi |                                                                                | 17 Eylül 2026 | Page Description / Sayfa Açıklaması    |                           | Load Schedule / Yükleme Cetveli                   |                                      |                                     |      |                    | Standards / Standartlar         |       | IEC 61439-1&2 · IEC 60617 |        | Sheet size / Kâğıt     |   | A3 |

0

1

2

3

4

5

6

7

A

B

C

D

E

F

MALZEME LİSTESİ / PARTS LIST

| S.NO | MALZEME / MATERIAL                           | BİRİM | MİKTAR |
|------|----------------------------------------------|-------|--------|
| 1    | Otomatik sigorta 2×16 A C eğrisi · 6 kA      | adet  | 10     |
| 2    | Otomatik sigorta 2×10 A B eğrisi · 6 kA      | adet  | 5      |
| 3    | Otomatik sigorta 1×16 A C eğrisi · 6 kA      | adet  | 4      |
| 4    | Kaçak akım rölesi 4×40 A / 30 mA, A tipi     | adet  | 4      |
| 5    | Otomatik sigorta 2×10 A C eğrisi · 6 kA      | adet  | 2      |
| 6    | Otomatik sigorta 2×20 A C eğrisi · 6 kA      | adet  | 2      |
| 7    | Otomatik sigorta 2×6 A C eğrisi · 6 kA       | adet  | 2      |
| 8    | Kaçak akım rölesi 2×40 A / 30 mA, A tipi     | adet  | 2      |
| 9    | Otomatik sigorta 2×6 A B eğrisi · 6 kA       | adet  | 1      |
| 10   | Ana şalter 4×32 A yük ayırıcı                | adet  | 1      |
| 11   | Ana kaçak akım rölesi 4×40 A / 300 mA S tipi | adet  | 1      |
| 12   | Parafudr Tip 2 · Up 1,4 kV · In 20 kA (3F+N) | adet  | 1      |
| 13   | Pano gövdesi 800×1000×250 mm IP54 Form 2b    | adet  | 1      |
| 14   | Bakır bara seti 3F+N+PE                      | adet  | 1      |
| 15   | Klemens sırası -X1 (vidalı, 4 mm²)           | adet  | 66     |
| 16   | Etiket seti (PVC, Türkçe, vidalı)            | adet  | 1      |

|                             |               |                                        |                                                   |                                 |                           |                        |    |
|-----------------------------|---------------|----------------------------------------|---------------------------------------------------|---------------------------------|---------------------------|------------------------|----|
| Drawn By / Çizen            | CC            | Customer Name / Müşteri Adı            | ÖZEL — MALTEPE / İDEALTEPE                        | Project Number / Proje Numarası | GYM-25-001-001            | Sheet: / Sayfa         | 12 |
| Checked By / Kontrol Eden   | —             | Project Description / Proje Açıklaması | MOBİLYA MAĞAZASI → FONKSİYONEL ANTRENMAN STÜDYOSU |                                 |                           | Next sheet: / Sonraki  | —  |
| Approved By / Onaylayan     | —             | Panel Name / Pano Adı                  | ADP                                               | Revision / Revizyon             | Rev H                     | Total sheets: / Toplam | 12 |
| Project Date / Proje Tarihi | 17 Eylül 2026 | Page Description / Sayfa Açıklaması    | Parts List / Malzeme Listesi                      | Standards / Standartlar         | IEC 61439-1&2 · IEC 60617 | Sheet size / Kâğıt     | A3 |