

MALTEPE / İDEALTEPE

MOBİLYA MAĞAZASI → FONKSİYONEL ANTRENMAN STÜDYOSU

UYGULAMA PROJESİ — MİMARİ · MEKANİK · ELEKTRİK

Proje no	GYM-25-001
Yapı	İdealtepe Mah. · zemin kat dükkân · 103,78 m² iç alan
İç alan	103,78 m²
Tarih	17 Eylül 2026
Revizyon	Rev H
Pafta boyutu	A1 (841×594) planlar · A3 (420×297) şemalar
Ölçek	Planlar 1:50 · şemalar ölçeksiz
Standartlar	TS EN ISO 5457 · TS EN ISO 7200 · ISO 128 · ISO 3098 · IEC 60617 · IEC 61439 · IEC 81346-2

PAFTA İNDEKSİ

BÖLÜM 1 — MİMARİ

A-01	MİMARİ ALTLIK	Mevcut durum · ölçü ve aks sistemi · 1:50
A-02	MİMARİ UYGULAMA PLANI	Bölme duvarlar · kapılar · mahal no · 1:50
A-03	ZEMİN KAPLAMA PLANI	Kaplama tipleri · kot · derz yönü · 1:50
A-04	TAVAN PLANI (RCP)	Tavan tipleri · kot · MEP koordinasyonu · 1:50
A-05	YANGIN VE TAHLİYE PLANI	Kaçış yolları · çıkışlar · söndürücü · 1:50

BÖLÜM 2 — MEKANİK TESİSAT

M-01	HAVALANDIRMA PLANI	Kanal güzergâhı · menfez debileri · 1:50
M-02	İKLİMLENDİRME PLANI	Split küme · bakır hat · drenaj · 1:50
M-03	SIHHİ TESİSAT PLANI	Temiz su · sıcak su · pis su · 1:50
M-04	MEKANİK GENEL YERLEŞİM	Disiplin genel yerleşimi · 1:50

BÖLÜM 3 — ELEKTRİK

E-01	AYDINLATMA PLANI	Armatür · anahtar · aydınlatma linyeleri · 1:50
E-02	PRİZ VE KUVVET PLANI	Priz · kuvvet linyeleri · cihazlar · 1:50
E-03	ZAYIF AKIM PLANI	Veri · CCTV · ses · yangın algılama · 1:50
E-04	ELEKTRİK GENEL YERLEŞİM	Disiplin genel yerleşimi · 1:50
E-05	TOPRAKLAMA PLANI	Elektrot grubu · ATB · EPDB · 1:50


BÖLÜM 4 — ADP ÇOK HATLI ŞEMA SETİ (A3)

ADP-01	Cover Sheet / Kapak
ADP-02	Panel Characteristics / Pano Karakteristiği
ADP-03	Symbol List / Sembol Listesi
ADP-04	Incoming Supply / Ana Besleme
ADP-05	Schematic Diagram / Şematik Diyagram
ADP-06	Schematic Diagram / Şematik Diyagram
ADP-07	Schematic Diagram / Şematik Diyagram
ADP-08	Schematic Diagram / Şematik Diyagram
ADP-09	Terminal Diagram / Klemens Planı
ADP-10	Panel Overview / Pano Önden Görünüş
ADP-11	Load Schedule / Yükleme Cetveli
ADP-12	Parts List / Malzeme Listesi

OKUMA NOTLARI

- Bu set ön tasarım aşamasındadır; yerinde röleve alınmadan ve ruhsat alınmadan uygulama yapılamaz.
- Ölçü alınmaz — yazılı ölçüler geçerlidir. Tüm ölçüler milimetredir.
- Aks sistemi yapının kendi doğrultusuna kurulmuştur (kuzeye göre 8,0°).
- Elektrik linye güzergâhları ortogonaldır; çapraz hat yoktur.
- Aydınlatma linyelerinde B eğrili, priz ve motor linyelerinde C eğrili kesici kullanılır.
- Ana kaçak akım rölesi ana şalterle orantılıdır (4×32 A → 4×40 A 300 mA S tipi).
- Yedek linyeler dâhil tüm son devreler 30 mA kaçak akım rölesi arkasındadır; yangın algılama paneli hariç.
- Mimari altlık tüm disiplin paftalarında ortaktır ve değiştirilmez.

REV	TARİH	AÇIKLAMA	ÇZ	KT	ON
A	17.09.2026	İlk yayın — ön tasarım	CC	—	—
B	18.09.2026	Aks sistemi, zincir ölçü, ISO 5457/7200 pafta	CC	—	—
C	18.09.2026	A1 pafta, tekil DXF, ADP şeması CAD'de	CC	—	—
D	18.09.2026	ADP çok hatlı şema (faz ayrımı), B eğrisi, ana RCD	CC	—	—
İŞVEREN					
ÖZEL — MALTEPE / İDEALTEPE					
PROJE					
MOBİLYA MAĞAZASI → FONKSİYONEL ANTRENMAN STÜDYOSU					
YAPI / MAHAL			DİSİPLİN		
İdealtepe Mah. · zemin kat dükkân · 103,78 m² iç alan			GENEL		
PAFTA ADI					
PAFTA İNDEKSİ			Proje kapağı ve pafta listesi		
PROJE MÜELLİFİ · ODA SİCİL NO					
— Oda sicil no: —					
ÇİZEN		KONTROL	ONAY		A
CC		—	—		
TARİH		ÖLÇEK	BİRİM		
17 Eylül 2026		—	milimetre (mm)		
DURUM		PAFTA NO	REV		
ÖN TASARIM		00	H		SONRAKİ: A-01

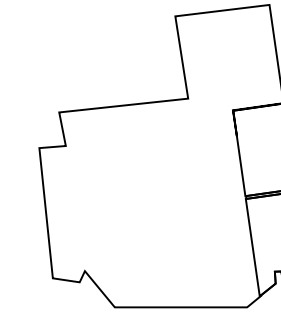

LEJANT

- Mimari — mevcut duvar (korunuyor)
— Mimari — yeni alçıpan bölme
— Mimari — cephe doğraması
— Mimari — kapı ve açılım
— Mimari — spor ekipmanı (işverence temin)
— Mimari — sabit mobilya
— Mimari — mahal adı ve alan

GENEL NOTLAR

1. Mimari altlık — mevcut duvar korunur.
2. Kırmızı: yeni alçıpan bölme.
3. Ölçüler raster paftadan (+/-%3).

ÖLÇEK 1:50
0 1 2 3 4 5 m

ÖN TASARIM — UYGULAMA İÇİN DEĞİLDİR

REV	TARİH	AÇIKLAMA	CZ	KT	ON
A	17.09.2026	İlk yayın — ön tasarım	CC	—	—
B	18.09.2026	Aks sistemi, zincir ölçü, ISO 5457/7200 pafta	CC	—	—
C	18.09.2026	A1 pafta, tekil DXF, ADP şeması CAD'de	CC	—	—
D	18.09.2026	ADP çok hatlı şema (faz ayrımı), B eğrisi, ana RCD	CC	—	—

İŞVEREN ÖZEL — MALTEPE / IDEALTEPE PROJE MOBİLYA MAĞAZASI → FONKSİYONEL ANTRENMAN STÜDYOSU		
YAPI / MAHAL İdealtepe Mah. · zemin kat dükkân · 103,78 m² iç alan		DISİPLİN MİMARİ
PAFTA ADI MİMARİ ALTLIK		Mevcut durum · ölçü ve aks sistemi
PROJE MÜELLİFİ · ODA SİCİL NO — Oda sicil no: —		
ÇİZEN CC	KONTROL —	ONAY —
TARİH 17 Eylül 2026	ÖLÇEK 1:50	BİRİM milimetre (mm)
DURUM ÖN TASARIM	PAFTA NO A-01	REV H SONRAKİ: A-02


LEJANT

- Mimari — mevcut duvar (korunuyor)
— Mimari — yeni alçıpan bölme
— Mimari — cephe doğraması
— Mimari — kapı ve açılım
— Mimari — spor ekipmanı (işverence temin)
— Mimari — sabit mobilya
— Mimari — mahal adı ve alan
— Mimari — mahal numarası ve kapı kodu balonu
- - - Mimari — kesit ve görünüş hattı


GENEL NOTLAR

1. Mahal no, kapı kodu, duvar tipi ve
2. kesit hattı gösterilmiştir.
3. Tüm alçıpan bölmeler yapısal döşeme
4. altına (+3.20) kadar yükselir.

ÖLÇÜ ALINMAZ — YAZILI ÖLÇÜLER GEÇERLİDİR

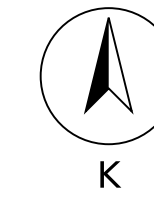

ANAHTAR PLAN

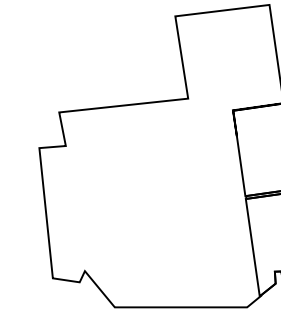

LEJANT

- Mimari — mevcut duvar (korunuyor)
- Mimari — yeni açılan bölme
- Mimari — cephe doğraması
- Mimari — kapı ve açılım
- Mimari — mahal numarası ve kapı kodu balonu
- Mimari — zemin kaplama tipi sınırı
- Mimari — zemin kaplama tipi ve kotu
- Mimari — kauçuk karo derz ızgarası

GENEL NOTLAR

- Bitmiş zemin kotu tüm kuru hacimde
- +/-0,00; dus ve WC -0,02.
- Tesviye sapı kalınlıkları farklıdır
- (Z1:3 Z2:30 Z3:42 Z5:38 mm).
- Kaucuk karo derz 1000x1000 mm.


ÖLÇEK 1:50
0 1 2 3 4 5 m


ÖN TASARIM — UYGULAMA İÇİN DEĞİLDİR

REV	TARİH	AÇIKLAMA	CZ	KT	ON
A	17.09.2026	İlk yayın — ön tasarım	CC	—	—
B	18.09.2026	Aks sistemi, zincir ölçü, ISO 5457/7200 pafta	CC	—	—
C	18.09.2026	A1 pafta, tekil DXF, ADP şeması CAD'de	CC	—	—
D	18.09.2026	ADP çok hatlı şema (faz ayrımı), B eğrisi, ana RCD	CC	—	—

İŞVEREN ÖZEL — MALTEPE / IDEALTEPE			B			
PROJE MOBİLYA MAĞAZASI → FONKSİYONEL ANTRENMAN STÜDYOSU						
YAPI / MAHAL İdealtepe Mah. · zemin kat dükkân · 103,78 m ² iç alan		DISIPLİN MİMARİ				
PAFTA ADI ZEMİN KAPLAMA PLANI		Kaplama tipleri · kot · derz yönü				
PROJE MÜELLİFİ · ODA SİCİL NO — Oda sicil no: —						
ÇİZEN CC		KONTROL —		ONAY —		
TARİH 17 Eylül 2026		ÖLÇEK 1:50		BİRİM milimetre (mm)		
DURUM ÖN TASARIM		PAFTA NO A-03		REV H		
				SONRAKİ: A-04		

100 mm

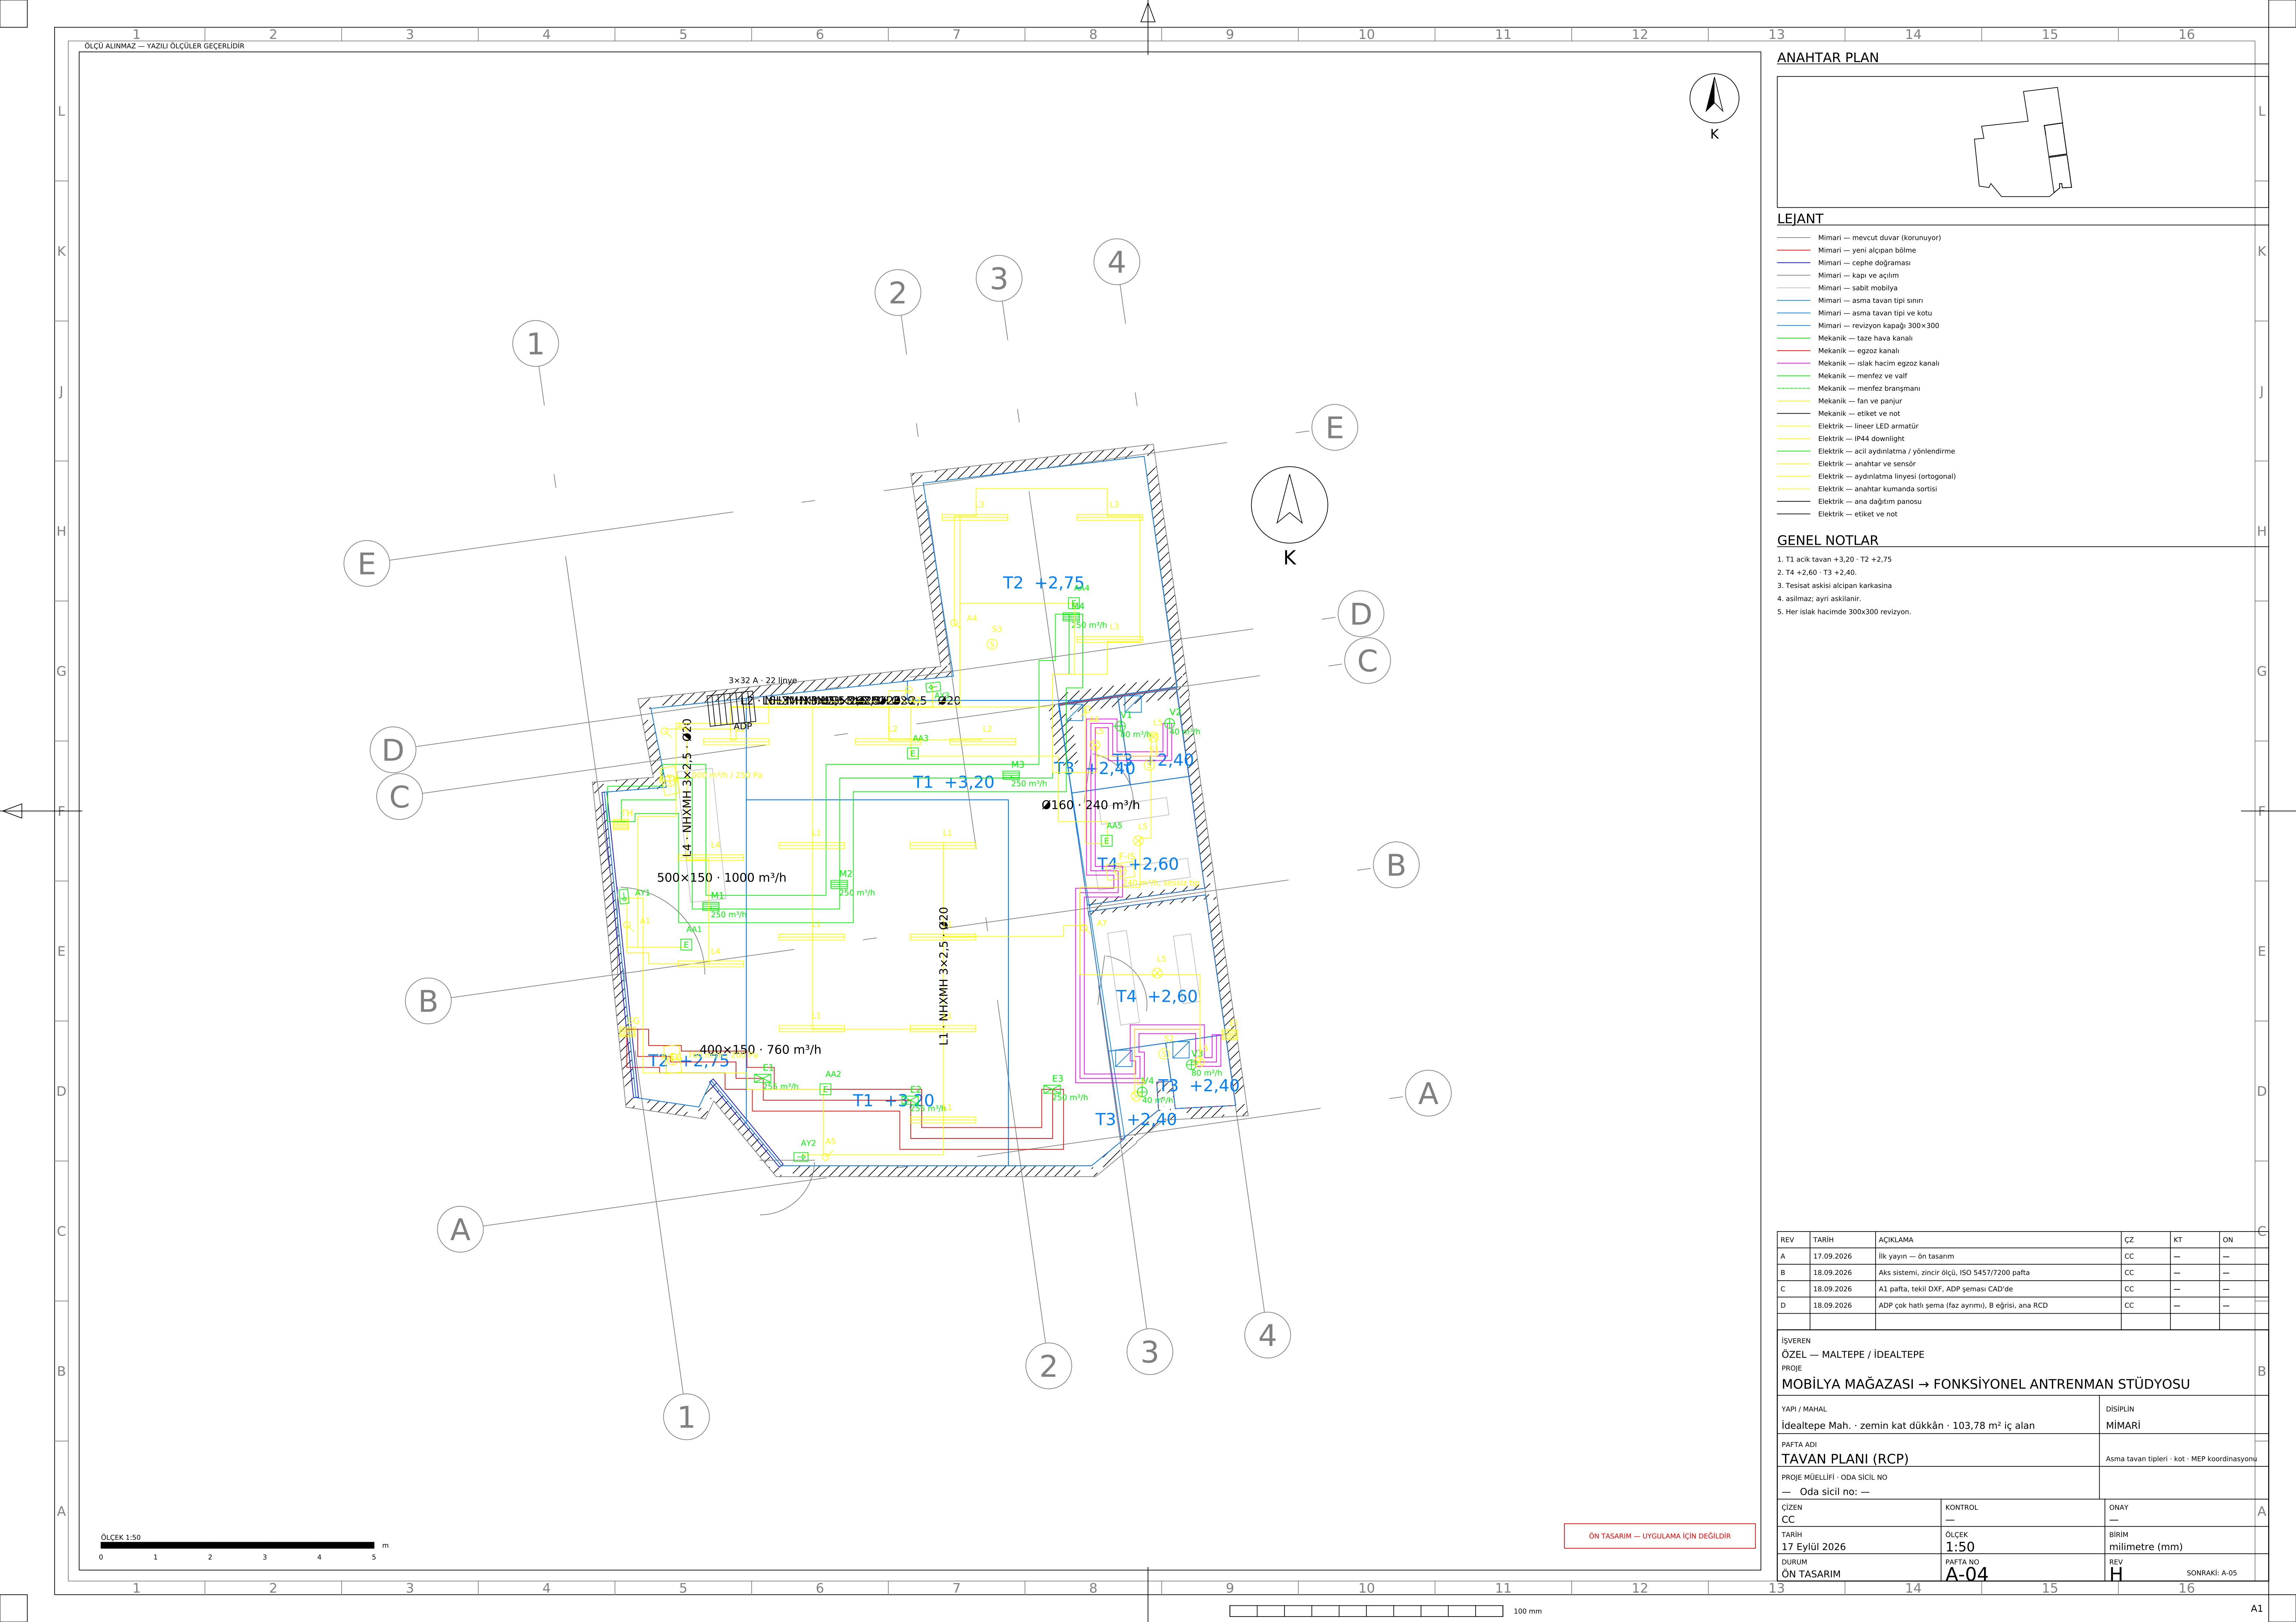

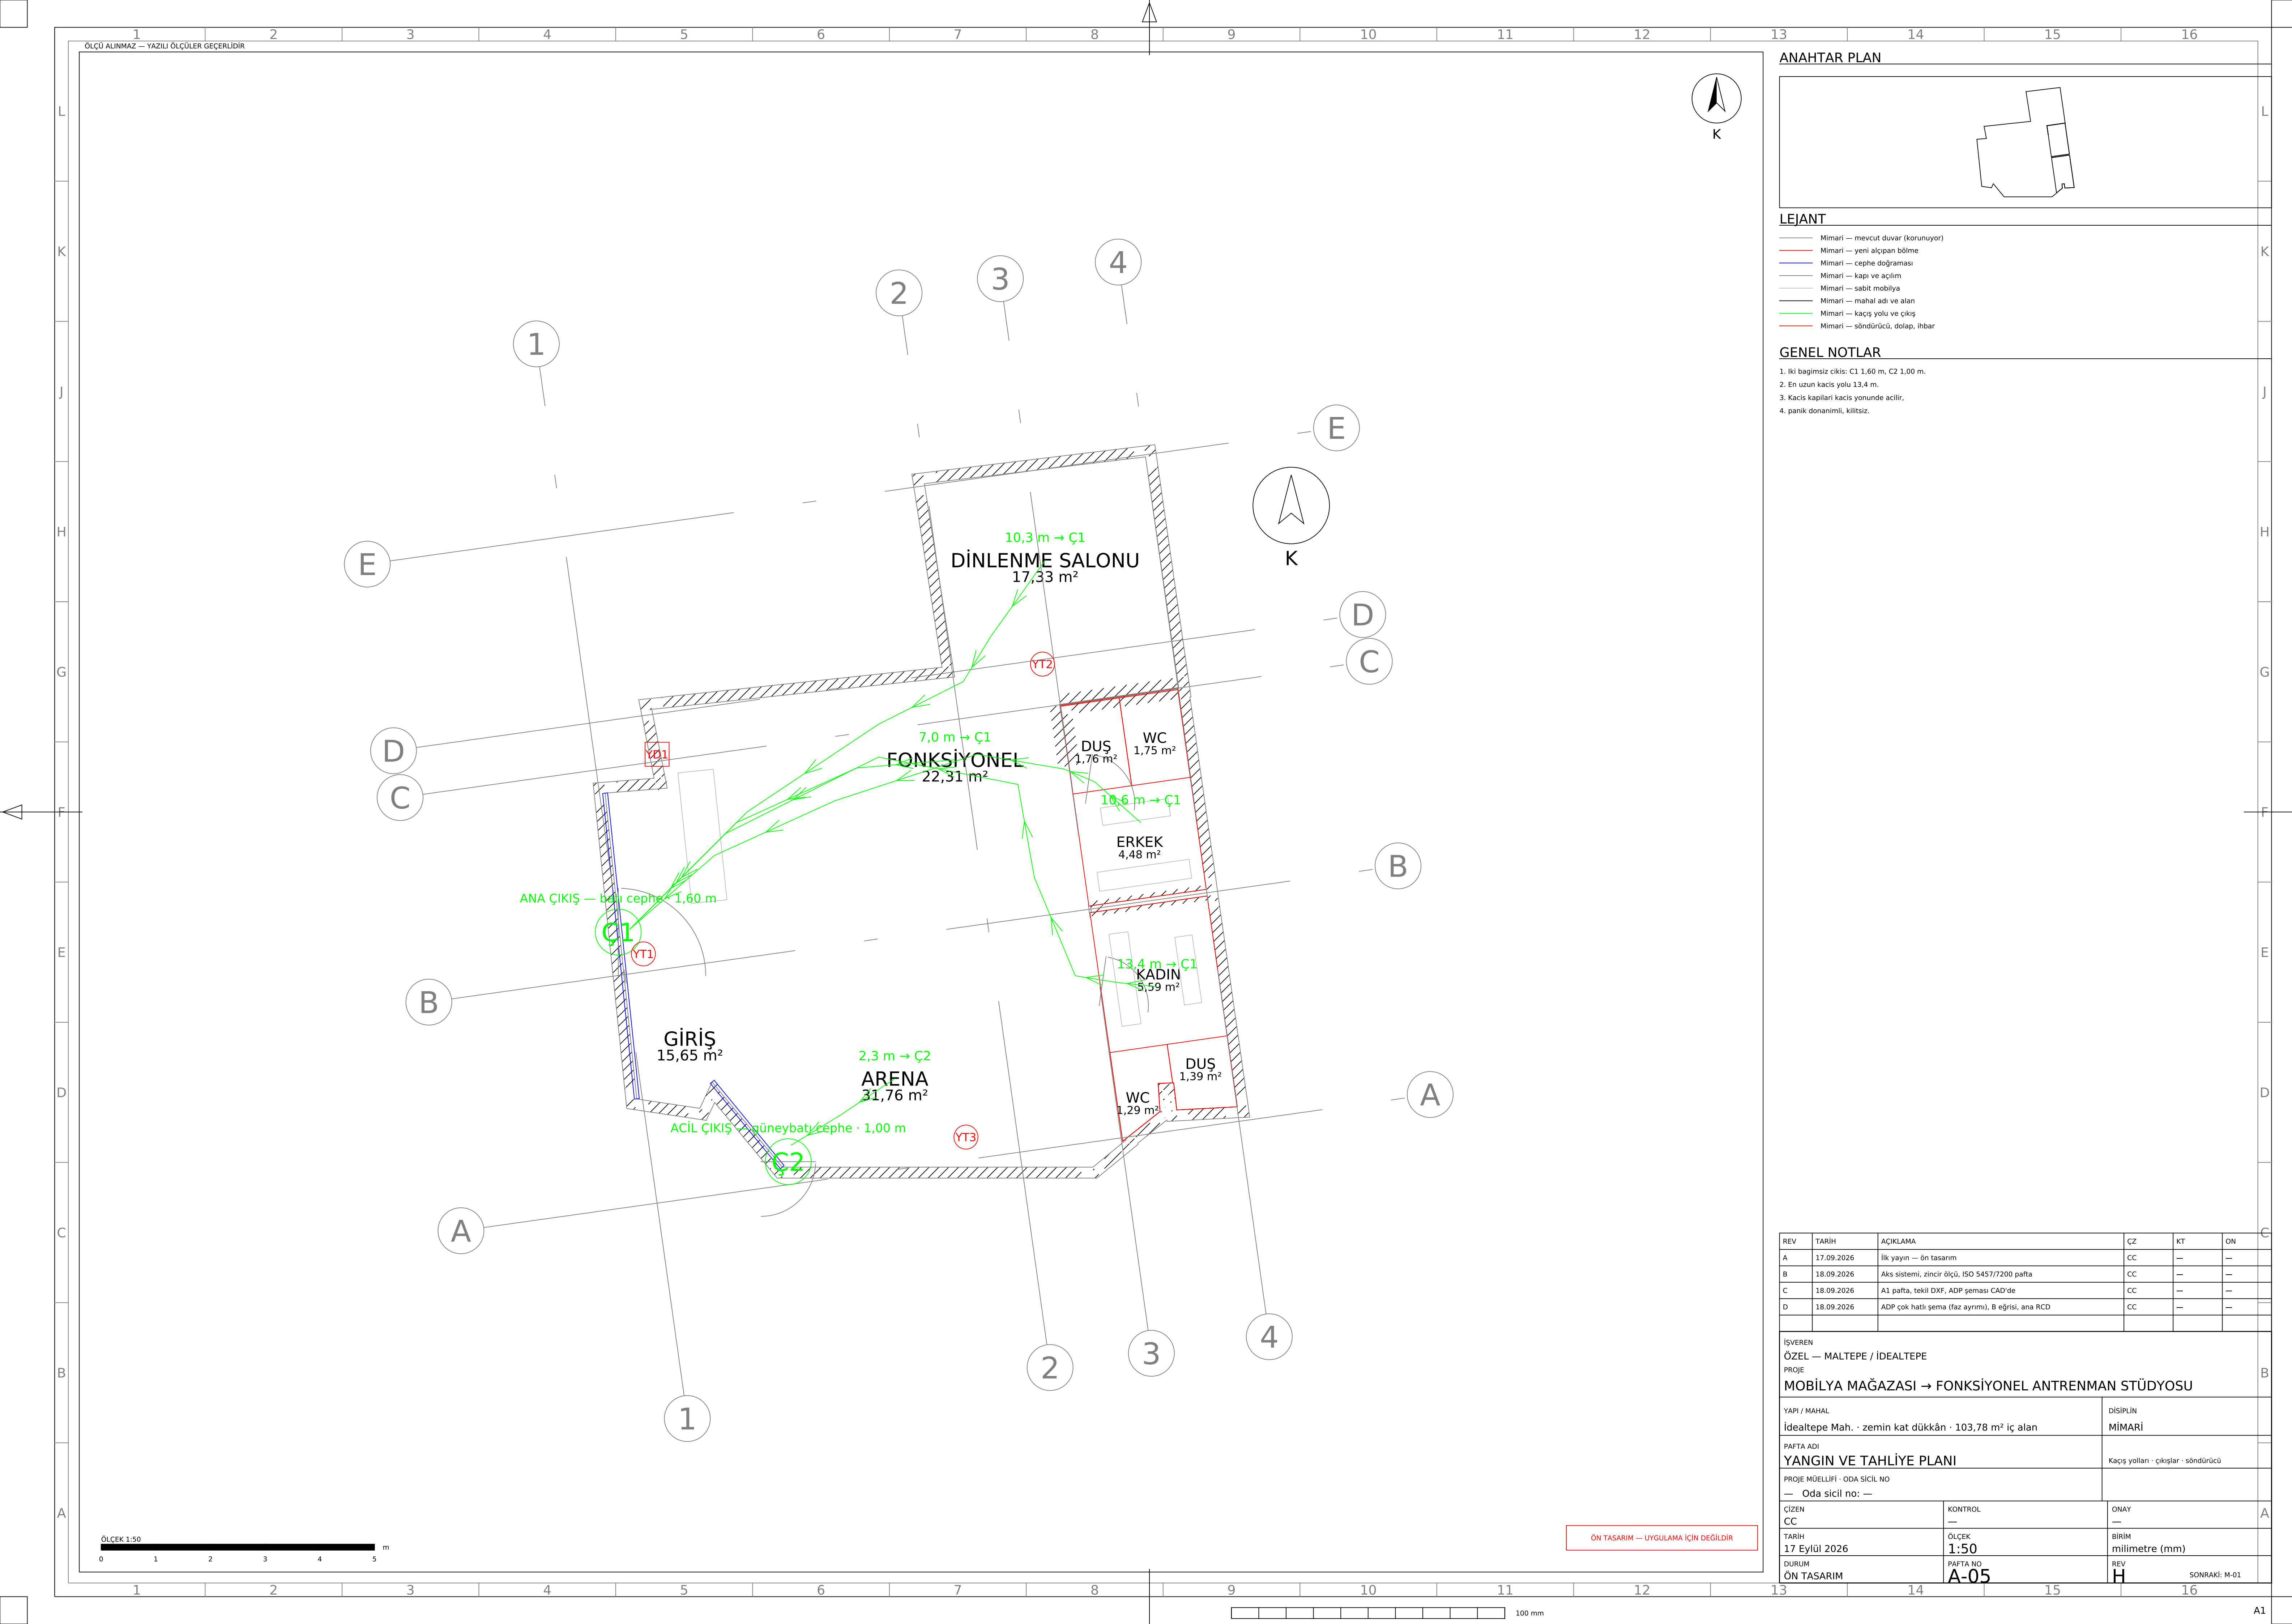

LEJANT

- Mimari — mevcut duvar (korunuyor)
— Mimari — yeni alçıpan bölme
— Mimari — cephe doğraması
— Mimari — kapı ve açılım
— Mimari — spor ekipmanı (işverence temin)
— Mimari — sabit mobilya
— Mimari — mahal adı ve alan
— Mekanik — taze hava kanalı
— Mekanik — egzoz kanalı
— Mekanik — ıslak hacim egzoz kanalı
— Mekanik — menfez ve valf
— Mekanik — menfez bransmanı
— Mekanik — fan ve panjur
— Mekanik — etiket ve not

GENEL NOTLAR

1. Kanallar galvaniz sac, TS EN 1507 sınıf B.
2. Besleme ve egzoz hattı 19 mm izoleli.
3. Her bransman bası debi ayar damperli.
4. Devreye almada balanslama ve ölçüm raporu.

DİNLENME SALONU
17,33 m²

FONKSİYONEL
22,31 m²

DÜŞ
1,76 m²

WC
1,75 m²

ERKEK
4,48 m²

KADIN
5,59 m²

GİRİŞ
15,65 m²

ARENA
31,76 m²

WC
1,29 m²

DÜŞ
1,39 m²

ÖLÇEK 1:50
0 1 2 3 4 5 m

ÖN TASARIM — UYGULAMA İÇİN DEĞİLDİR

REV	TARİH	AÇIKLAMA	ÇZ	KT	ON
A	17.09.2026	İlk yayın — ön tasarım	CC	—	—
B	18.09.2026	Aks sistemi, zincir ölçü, ISO 5457/7200 pafta	CC	—	—
C	18.09.2026	A1 pafta, tekil DXF, ADP şeması CAD'de	CC	—	—
D	18.09.2026	ADP çok hatlı şema (faz ayrımı), B eğrisi, ana RCD	CC	—	—

İŞVEREN ÖZEL — MALTEPE / İDEALTEPE			
PROJE MOBİLYA MAĞAZASI → FONKSİYONEL ANTRENMAN STÜDYOSU			
YAPI / MAHAL İdealtepe Mah. · zemin kat dükkân · 103,78 m ² iç alan		DİSİPLİN MEKANİK TESİSAT	
PAFTA ADI HAVALANDIRMA PLANI		Kanal güzergâhı · menfez debileri	
PROJE MÜELLİFİ · ODA SİCİL NO — Oda sicil no: —			
ÇİZEN CC	KONTROL —	ONAY —	
TARİH 17 Eylül 2026	ÖLÇEK 1:50	BİRİM milimetre (mm)	
DURUM ÖN TASARIM	PAFTA NO M-01	REV H	SONRAKİ: M-02

LEJANT

- Mimari — mevcut duvar (korunuyor)
- Mimari — yeni alçıpan bölme
- Mimari — cephe doğraması
- Mimari — kapı ve açılım
- Mimari — spor ekipmanı (işverence temin)
- Mimari — sabit mobilya
- Mimari — mahal adı ve alan
- Mekanik — klima iç ünite
- Mekanik — klima dış ünite platformu
- Mekanik — soğutucu akışkan bakır hattı
- Mekanik — klima drenaj hattı

GENEL NOTLAR

- İç ünite montaj kotu 2,40 m (altı kot).
- Bakır hat izoleli, dış ünite konsolu
- titresim takozlu.
- Drenaj %1 eğimli.

ÖLÇEK 1:50
0 1 2 3 4 5 m

ÖN TASARIM — UYGULAMA İÇİN DEĞİLDİR

REV	TARİH	AÇIKLAMA	CZ	KT	ON
A	17.09.2026	İlk yayın — ön tasarım	CC	—	—
B	18.09.2026	Aks sistemi, zincir ölçü, ISO 5457/7200 pafta	CC	—	—
C	18.09.2026	A1 pafta, tekil DXF, ADP şeması CAD'de	CC	—	—
D	18.09.2026	ADP çok hatlı şema (faz ayrımı), B eğrisi, ana RCD	CC	—	—

İŞVEREN ÖZEL — MALTEPE / IDEALTEPE PROJE MOBİLYA MAĞAZASI → FONKSİYONEL ANTRENMAN STÜDYOSU			YAPI / MAHAL İdealtepe Mah. · zemin kat dükkân · 103,78 m ² iç alan		DISIPLIN MEKANİK TESİSAT
PAFTA ADI İKLİMLENDİRME PLANI			PROJE MÜELLİFİ · ODA SİCİL NO — Oda sicil no: —		Split küme · bakır hat · drenaj
ÇİZEN CC			KONTROL —		ONAY —
TARİH 17 Eylül 2026			ÖLÇEK 1:50		BİRİM milimetre (mm)
DURUM ÖN TASARIM			PAFTA NO M-02		REV H
					SONRAKİ: M-03

LEJANT

- Mimari — mevcut duvar (korunuyor)
- Mimari — yeni alçıpan bölme
- Mimari — cephe doğraması
- Mimari — kapı ve açılım
- Mimari — spor ekipmanı (işverence temin)
- Mimari — sabit mobilya
- Mimari — mahal adı ve alan
- Mekanik — temiz su PPRC
- Mekanik — sıcak su PPRC İzoleli
- Mekanik — pis su PVC
- Mekanik — vitrifiye ve su ısıtıcı

GENEL NOTLAR

- Pis su %2 eğimli.
- Tüm ıslak hacimde sifonlu yer suzgeci.
- SOKUM SONRASI İLK İS: mevcut pis su
- bağlantı kotunun ölçülmesi.

REV	TARİH	AÇIKLAMA	CZ	KT	ON
A	17.09.2026	İlk yayın — ön tasarım	CC	—	—
B	18.09.2026	Aks sistemi, zincir ölçü, ISO 5457/7200 pafta	CC	—	—
C	18.09.2026	A1 pafta, tekil DXF, ADP şeması CAD'de	CC	—	—
D	18.09.2026	ADP çok hatlı şema (faz ayrımı), B eğrisi, ana RCD	CC	—	—

İŞVEREN ÖZEL — MALTEPE / İDEALTEPE			B			
PROJE MOBİLYA MAĞAZASI → FONKSİYONEL ANTRENMAN STÜDYOSU						
YAPI / MAHAL İdealtepe Mah. · zemin kat dükkân · 103,78 m² iç alan		DİSİPLİN MEKANİK TESİSAT				
PAFTA ADI SIHHİ TESİSAT PLANI		Temiz su · sıcak su · pis su				
PROJE MÜELLİFİ · ODA SİCİL NO — Oda sicil no: —						
ÇİZEN CC		KONTROL —		ONAY —		
TARİH 17 Eylül 2026		ÖLÇEK 1:50		BİRİM milimetre (mm)		
DURUM ÖN TASARIM		PAFTA NO M-03		REV H		
				SONRAKİ: M-04		

ÖLÇEK 1:50
0 1 2 3 4 5 m

ÖN TASARIM — UYGULAMA İÇİN DEĞİLDİR

LEJANT

- Mimari — mevcut duvar (korunuyor)
- Mimari — yeni alçıpan bölme
- Mimari — cephe doğraması
- Mimari — kapı ve açılım
- Mimari — spor ekipmanı (işverence temini)
- Mimari — sabit mobilya
- Mimari — mahal adı ve alan
- Mekanik — taze hava kanalı
- Mekanik — egzoz kanalı
- Mekanik — ıslak hacim egzoz kanalı
- Mekanik — menfez ve valf
- Mekanik — menfez bransmanı
- Mekanik — fan ve panjur
- Mekanik — klima iç ünite
- Mekanik — klima dış ünite platformu
- Mekanik — soğutucu akışkan bakır hattı
- Mekanik — klima drenaj hattı
- Mekanik — temiz su PPRC
- Mekanik — sıcak su PPRC izoleli
- Mekanik — pis su PVC
- Mekanik — vitrifiye ve su ısıtıcı
- Mekanik — etiket ve not

GENEL NOTLAR

- Mekanik disiplin genel yerleşimi.
- Ayrıntı için M-01, M-02, M-03 paftaları.

REV	TARİH	AÇIKLAMA	CZ	KT	ON
A	17.09.2026	İlk yayın — ön tasarım	CC	—	—
B	18.09.2026	Aks sistemi, zincir ölçü, ISO 5457/7200 pafta	CC	—	—
C	18.09.2026	A1 pafta, tekil DXF, ADP şeması CAD'de	CC	—	—
D	18.09.2026	ADP çok hatlı şema (faz ayrımı), B eğrisi, ana RCD	CC	—	—

İŞVEREN	ÖZEL — MALTEPE / IDEALTEPE
PROJE	MOBİLYA MAĞAZASI → FONKSİYONEL ANTRENMAN STÜDYOSU
YAPI / MAHAL	İdealtepe Mah. · zemin kat dükkân · 103,78 m ² iç alan
PAFTA ADI	MEKANİK GENEL YERLEŞİM
PROJE MÜELLİFİ · ODA SİCİL NO	— Oda sicil no: —
ÇİZEN	CC
TARİH	17 Eylül 2026
DURUM	ÖN TASARIM
KONTROL	—
ÖLÇEK	1:50
PAFTA NO	M-04
ONAY	—
BİRİM	milimetre (mm)
REV	H
SONRAKİ	E-01

LEJANT

- Mimari — mevcut duvar (korunuyor)
- Mimari — yeni açılan bölme
- Mimari — cephe doğraması
- Mimari — kapı ve açılım
- Mimari — spor ekipmanı (işverence temini)
- Mimari — sabit mobilya
- Mimari — mahal adı ve alan
- Elektrik — lineer LED armatür
- Elektrik — IP44 downlight
- Elektrik — acil aydınlatma / yönlendirme
- Elektrik — anahtar ve sensör
- Elektrik — aydınlatma lineyesi (ortogonal)
- Elektrik — anahtar kumanda sortisi
- Elektrik — ana dağıtım panosu
- Elektrik — etiket ve not

GENEL NOTLAR

- Tesisat siva altı spiral boru içinde,
- NHXMH halojeniz kablo.
- Acil aydınlatma 3 saat bataryalı.

REV	TARİH	AÇIKLAMA	CZ	KT	ON
A	17.09.2026	İlk yayın — ön tasarım	CC	—	—
B	18.09.2026	Aks sistemi, zincir ölçü, ISO 5457/7200 pafta	CC	—	—
C	18.09.2026	A1 pafta, tekil DXF, ADP şeması CAD'de	CC	—	—
D	18.09.2026	ADP çok hatlı şema (faz ayrımı), B eğrisi, ana RCD	CC	—	—

İŞVEREN ÖZEL — MALTEPE / IDEALTEPE			DISİPLİN ELEKTRİK		
PROJE MOBİLYA MAĞAZASI → FONKSİYONEL ANTRENMAN STÜDYOSU			YAPI / MAHAL İdealtepe Mah. · zemin kat dükkân · 103,78 m ² iç alan		
PAFTA ADI AYDINLATMA PLANI			ARMATÜR · ANAHTAR · AYDINLATMA LİNYELERİ		
PROJE MÜELLİFİ · ODA SİCİL NO — Oda sicil no: —			CİZEN CC		
TARİH 17 Eylül 2026			KONTROL —		
DURUM ÖN TASARIM			ONAY —		
ÖLÇEK 1:50			BİRİM milimetre (mm)		
PAFTA NO E-01			REV H		
SONRAKİ: E-02					


ÖN TASARIM — UYGULAMA İÇİN DEĞİLDİR

LEJANT

- Mimari — mevcut duvar (korunuyor)
- Mimari — yeni alçıpan bölme
- Mimari — cephe doğraması
- Mimari — kapı ve açılım
- Mimari — spor ekipmanı (işverence temin)
- Mimari — sabit mobilya
- Mimari — mahal adı ve alan
- Elektrik — priz
- Elektrik — klima/sıtıcıfan beslemesi
- Elektrik — priz ve kuvvet linyesi
- Elektrik — ana dağıtım panosu
- Elektrik — etiket ve not

GENEL NOTLAR

- Islak hacim linyeleri ayrı 30 mA
- kacak akım rolesinden beslenir.
- Kardiyo ekipmanı ayrı linyede (P4).

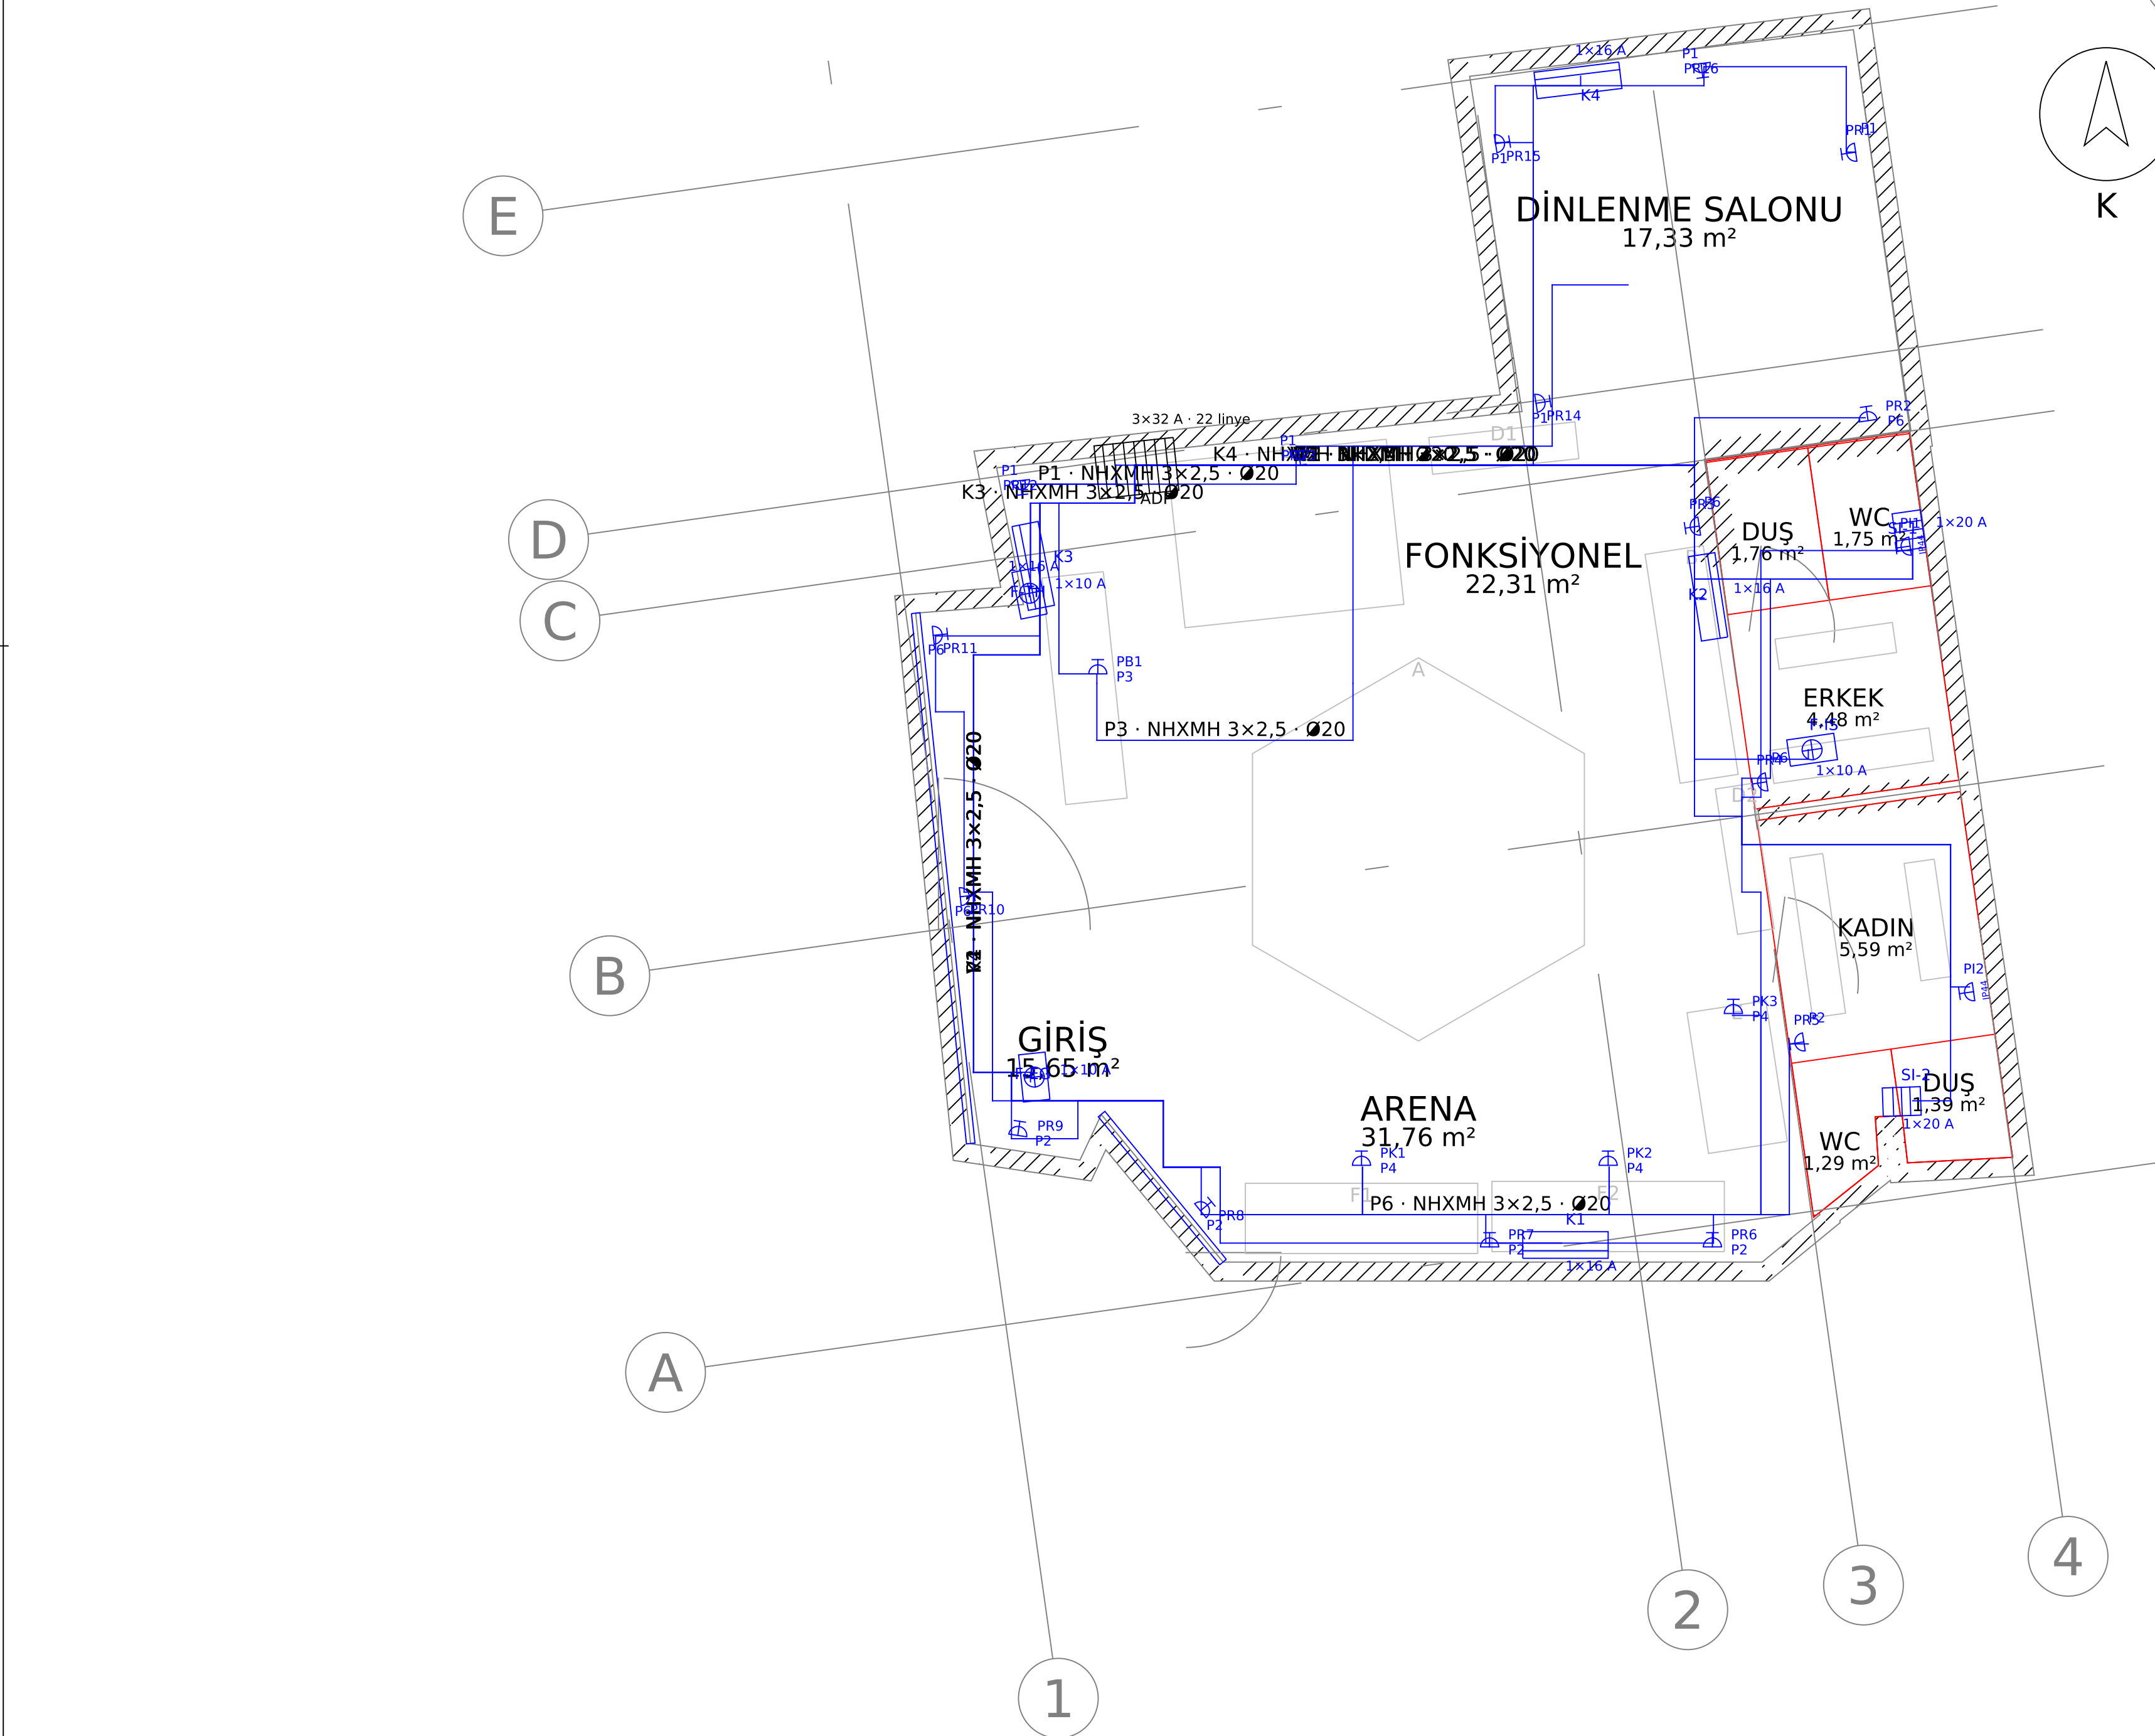

ÖN TASARIM — UYGULAMA İÇİN DEĞİLDİR

REV	TARİH	AÇIKLAMA	CZ	KT	ON
A	17.09.2026	İlk yayın — ön tasarım	CC	—	—
B	18.09.2026	Aks sistemi, zincir ölçü, ISO 5457/7200 pafta	CC	—	—
C	18.09.2026	A1 pafta, tekil DXF, ADP şeması CAD'de	CC	—	—
D	18.09.2026	ADP çok hatlı şema (faz ayrımı), B eğrisi, ana RCD	CC	—	—

İŞVEREN ÖZEL — MALTEPE / IDEALTEPE					
PROJE MOBİLYA MAĞAZASI → FONKSİYONEL ANTRENMAN STÜDYOSU					
YAPI / MAHAL İdealtepe Mah. · zemin kat dükkân · 103,78 m ² iç alan			DİSİPLİN ELEKTRİK		
PAFTA ADI PRİZ VE KUVVET PLANI			Priz - kuvvet linyeleri · cihaz beslemeleri		
PROJE MÜELLİFİ · ODA SİCİL NO — Oda sicil no: —					
ÇİZEN CC		KONTROL —	ONAY —		A
TARİH 17 Eylül 2026		ÖLÇEK 1:50	BİRİM milimetre (mm)		
DURUM ÖN TASARIM		PAFTA NO E-02	REV H		SONRAKİ: E-03

LEJANT

- Mimari — mevcut duvar (korunuyor)
- Mimari — yeni alçıpan bölme
- Mimari — cephe doğraması
- Mimari — kapı ve açılım
- Mimari — spor ekipmanı (işverence temin)
- Mimari — sabit mobilya
- Mimari — mahal adı ve alan
- Elektrik — IP kamera
- Elektrik — tavan hoparlörü
- Elektrik — veri prizi ve rack
- Elektrik — dedektör, buton, siren
- Elektrik — yangın algılama çevrimi
- Elektrik — zayıf akım kablo kanalı
- Elektrik — ana dağıtım panosu
- Elektrik — etiket ve not

GENEL NOTLAR

- SOYUNMA VE WC İÇİNE KAMERA KONULMAZ.
- Yangın algılama panosu kesintisiz beslenir.
- Topraklama direnci ≤ 10 ohm.

REV	TARİH	AÇIKLAMA	CZ	KT	ON
A	17.09.2026	İlk yayın — ön tasarım	CC	—	—
B	18.09.2026	Aks sistemi, zincir ölçü, ISO 5457/7200 pafta	CC	—	—
C	18.09.2026	A1 pafta, tekil DXF, ADP şeması CAD'de	CC	—	—
D	18.09.2026	ADP çok hatlı şema (faz ayrımı), B eğrisi, ana RCD	CC	—	—

İŞVEREN ÖZEL — MALTEPE / İDEALTEPE			B			
PROJE MOBİLYA MAĞAZASI → FONKSİYONEL ANTRENMAN STÜDYOSU						
YAPI / MAHAL İdealtepe Mah. · zemin kat dükkân · 103,78 m ² iç alan		DİSİPLİN ELEKTRİK				
PAFTA ADI ZAYIF AKIM PLANI		Veri · CCTV · ses · yangın algılama				
PROJE MÜELLİFİ · ODA SİCİL NO — Oda sicil no: —						
ÇİZEN CC		KONTROL —		ONAY —		
TARİH 17 Eylül 2026		ÖLÇEK 1:50		BİRİM milimetre (mm)		
DURUM ÖN TASARIM		PAFTA NO E-03		REV H		
				SONRAKİ: E-04		

ÖLÇEK 1:50
0 1 2 3 4 5 m

ÖN TASARIM — UYGULAMA İÇİN DEĞİLDİR

LEJANT

- Mimari — mevcut duvar (korunuyor)
- Mimari — yeni açılan bölme
- Mimari — cephe doğraması
- Mimari — kapı ve açılım
- Mimari — spor ekipmanı (işverence temini)
- Mimari — sabit mobilya
- Mimari — mahal adı ve alan
- Elektrik — lineer LED armatür
- Elektrik — IP44 downlight
- Elektrik — acil aydınlatma / yönlendirme
- Elektrik — anahtar ve sensör
- Elektrik — priz
- Elektrik — klima/sıtıcı/fan beslemesi
- Elektrik — IP kamera
- Elektrik — tavan hoparlörü
- Elektrik — veri prizi ve rack
- Elektrik — dedektör, buton, siren
- Elektrik — yangın algılama çevrimi
- Elektrik — aydınlatma lineyesi (ortogonal)
- Elektrik — anahtar kumanda sortisi
- Elektrik — priz ve kuvvet lineyesi
- Elektrik — zayıf akım kablo kanalı
- Elektrik — ana dağıtım panosu
- Elektrik — etiket ve not

GENEL NOTLAR

- Elektrik disiplin genel yerleşimi.
- Ayrıntı için E-01, E-02, E-03 paftaları.

REV	TARİH	AÇIKLAMA	CZ	KT	ON
A	17.09.2026	İlk yayın — ön tasarım	CC	—	—
B	18.09.2026	Aks sistemi, zincir ölçü, ISO 5457/7200 pafta	CC	—	—
C	18.09.2026	A1 pafta, tekil DXF, ADP şeması CAD'de	CC	—	—
D	18.09.2026	ADP çok hatlı şema (faz ayrımı), B eğrisi, ana RCD	CC	—	—

İŞVEREN ÖZEL — MALTEPE / İDEALTEPE					
PROJE MOBİLYA MAĞAZASI → FONKSİYONEL ANTRENMAN STÜDYOSU					
YAPI / MAHAL İdealtepe Mah. - zemin kat dükkân - 103,78 m ² iç alan			DISİPLİN ELEKTRİK		
PAFTA ADI ELEKTRİK GENEL YERLEŞİM			Elektrik disiplin genel yerleşimi		
PROJE MÜELLİFİ - ODA SİCİL NO — Oda sicil no: —					
ÇİZEN CC		KONTROL —		ONAY —	
TARİH 17 Eylül 2026		ÖLÇEK 1:50		BİRİM milimetre (mm)	
DURUM ÖN TASARIM		PAFTA NO E-04		REV H SONRAKİ: E-05	

ÖN TASARIM — UYGULAMA İÇİN DEĞİLDİR

LEJANT

- Mimari — mevcut duvar (korunuyor)
- Mimari — yeni açılan bölme
- Mimari — cephe doğraması
- Mimari — kapı ve açılım
- Mimari — spor ekipmanı (işverence temin)
- Mimari — sabit mobilya
- Mimari — mahal adı ve alan
- Elektrik — çubuk elektrot
- Elektrik — elektrot bağlantı şeridi
- Elektrik — topraklama iletkeni
- Elektrik — ATB / EPDB barası
- Elektrik — topraklama etiketi
- Elektrik — ana dağıtım panosu

GENEL NOTLAR

- Topraklama ve potansiyel dengeleme.
- Elektrot grubu yapı dışında, 4 adet 2 m Cu kaplı
- çelik çubuk, 3 m aralık. Ra hesap 15,5 ohm <= 20 ohm.
- ATB pano altında; her ıslak blokta EPDB bulunur.

ÖLÇEK 1:50
0 1 2 3 4 5 m

ÖN TASARIM — UYGULAMA İÇİN DEĞİLDİR

REV	TARİH	AÇIKLAMA	CZ	KT	ON
A	17.09.2026	İlk yayın — ön tasarım	CC	—	—
B	18.09.2026	Aks sistemi, zincir ölçü, ISO 5457/7200 pafta	CC	—	—
C	18.09.2026	A1 pafta, tekil DXF, ADP şeması CAD'de	CC	—	—
D	18.09.2026	ADP çok hatlı şema (faz ayrımı), B eğrisi, ana RCD	CC	—	—

İŞVEREN ÖZEL — MALTEPE / IDEALTEPE					
PROJE MOBİLYA MAĞAZASI → FONKSİYONEL ANTRENMAN STÜDYOSU					
YAPI / MAHAL İdealtepe Mah. · zemin kat dükkân · 103,78 m² iç alan		DİSİPLİN ELEKTRİK			
PAFTA ADI TOPRAKLAMA VE POTANSİYEL DENGELEME PLANI		Elektrot grubu · ATB · EPDB			
PROJE MÜELLİFİ · ODA SİCİL NO — Oda sicil no: —					
ÇİZEN CC		KONTROL —		ONAY —	
TARİH 17 Eylül 2026		ÖLÇEK 1:50		BİRİM milimetre (mm)	
DURUM ÖN TASARIM		PAFTA NO E-05		REV H	
			SONRAKİ: ADP-01		

0

1

2

3

4

5

6

7

A

ADP — ANA DAĞITIM PANOSU

ÇOK HATLI ŞEMATİK DİYAGRAM SETİ / MULTI-LINE SCHEMATIC SET

Müşteri / Customer

Proje / Project

Pano / Panel

Proje No / Project No

Tarih / Date

Revizyon / Revision

Standartlar / Standards

ÖZEL — MALTEPE / İDEALTEPE

MOBİLYA MAĞAZASI → FONKSİYONEL ANTRENMAN STÜDYOSU

ADP

GYM-25-001-001

17 Eylül 2026

Rev H

IEC 61439-1&2 · IEC 60617 · IEC 81346-2 · TS HD 60364 · Elektrik İç Tesisleri Yönetmeliği

SAYFA İÇERİĞİ / SHEET INDEX

01

Cover Sheet / Kapak

02

Panel Characteristics / Pano Karakteristiği

03

Symbol List / Sembol Listesi

04

Incoming Supply / Ana Besleme

05

Schematic Diagram / Şematik Diyagram

06

Schematic Diagram / Şematik Diyagram

07

Schematic Diagram / Şematik Diyagram

08

Schematic Diagram / Şematik Diyagram

09

Terminal Diagram / Klemens Planı

10

Panel Overview / Pano Önden Görünüş

11

Load Schedule / Yükleme Cetveli

12

Parts List / Malzeme Listesi

Drawn By / Çizen

CC

Customer Name / Müşteri Adı

ÖZEL — MALTEPE / İDEALTEPE

Project Number / Proje Numarası

GYM-25-001-001

Sheet: / Sayfa

1

Checked By / Kontrol Eden

—

Project Description / Proje Açıklaması

MOBİLYA MAĞAZASI → FONKSİYONEL ANTRENMAN STÜDYOSU

Revision / Revizyon

Rev H

Next sheet: / Sonraki

2

Approved By / Onaylayan

—

Panel Name / Pano Adı

ADP

Total sheets: / Toplam

12

Project Date / Proje Tarihi

17 Eylül 2026

Page Description / Sayfa Açıklaması

Cover Sheet / Kapak



Standards / Standartlar


IEC 61439-1&2 · IEC 60617

Sheet size / Kâğıt


A3

	0	1	2	3	4	5	6	7			
A	PANO KARAKTERİSTİK TABLOSU / PANEL CHARACTERISTICS STANDARTLAR / STANDARDS Tip testli pano / Type tested assembly IEC 61439-1 & IEC 61439-2 Semboller / Symbols IEC 60617 Referans işaretleri / Designations IEC 81346-2 Tesisat / Installation TS HD 60364 · Elektrik İç Tes. Yön. BESLEME / POWER SUPPLY Anma işletme gerilimi / Rated voltage 400/230 V 50 Hz Faz sayısı / Number of phases 3F + N + PE Nötr işletmesi / Neutral operation TN-S Anma akımı / Rated current 32 A Kısa devre dayanımı / Icw 6 kA 1 s Ana besleme kablosu / Main cable NYY 5×10 mm² · 25 m KORUMA / PROTECTION Ana şalter / Main switch 4×32 A Ana kaçak akım / Main RCD 4×40 A / 300 mA S tipi Son devre kaçak akım / Final RCD 30 mA A tipi Aşırı gerilim / SPD Tip 2 · Up 1,4 kV · In 20 kA Kesici eğrisi / MCB curve Aydınlatma B · Priz ve motor C · tümü 6 kA										
B	GÖVDE / ENCLOSURE Koruma sınıfı / Degree of protection IP 54 Ayrıştırma / Segregation Form 2b Gövde / Enclosure Sac · RAL 7035 Bara / Busbar Bakır · nötr tam kesit Montaj / Mounting Sabit · kapı arkası kumanda Etiketleme / Labelling PVC · Türkçe · vidalı ÖZET / SUMMARY Linye sayısı / Number of circuits 22 + 4 yedek Bağlı güç / Connected load 20,59 kW Talep gücü / Demand 14,63 kW Faz dengesizliği / Imbalance %1,0 Toplam ΔU / Total voltage drop %2,49										
C											
D											
E											
F											
Drawn By / Çizen		CC	Customer Name / Müşteri Adı		ÖZEL — MALTEPE / İDEALTEPE			Project Number / Proje Numarası	GYM-25-001-001	Sheet: / Sayfa	2
Checked By / Kontrol Eden		—	Project Description / Proje Açıklaması		MOBİLYA MAĞAZASI → FONKSİYONEL ANTRENMAN STÜDYOSU					Next sheet: / Sonraki	3
Approved By / Onaylayan		—	Panel Name / Pano Adı		ADP			Revision / Revizyon	Rev H	Total sheets: / Toplam	12
Project Date / Proje Tarihi		17 Eylül 2026	Page Description / Sayfa Açıklaması		Panel Characteristics / Pano Karakteristiği			Standards / Standartlar	IEC 61439-1&2 · IEC 60617	Sheet size / Kağıt	A3

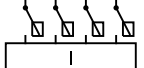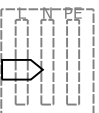
	0	1	2	3	4	5	6	7		
A	SEMBOL LİSTESİ / SYMBOL LIST — IEC 60617									
		-F	Otomatik sigorta, 1 kutup / MCB 1P							
		-F	Otomatik sigorta, 1F+N / MCB 1P+N							
B		-ID	Kaçak akım rölesi 2 kutup / RCD 2P							
		-ID	Kaçak akım rölesi 4 kutup / RCD 4P							
		-F0	Aşırı gerilim koruma Tip 2 / SPD Type 2							
C		-X	Klemens / Terminal							
		PE	Koruma topraklaması / Protective earth							
			Bağlantı noktası / Junction							
D		P	Saha cihazı ve kablo / Field device and cable							
			L1 L2 L3 NPotansiyel rayı / Potential rail							
			Sayfalar arası referans / Cross-page reference							
E										
F										
Drawn By / Çizen		CC	Customer Name / Müşteri Adı	ÖZEL — MALTEPE / İDEALTEPE			Project Number / Proje Numarası	GYM-25-001-001	Sheet: / Sayfa	3
Checked By / Kontrol Eden		—	Project Description / Proje Açıklaması	MOBİLYA MAĞAZASI → FONKSİYONEL ANTRENMAN STÜDYOSU					Next sheet: / Sonraki	4
Approved By / Onaylayan		—	Panel Name / Pano Adı	ADP			Revision / Revizyon	Rev H	Total sheets: / Toplam	12
Project Date / Proje Tarihi		17 Eylül 2026	Page Description / Sayfa Açıklaması	Symbol List / Sembol Listesi			Standards / Standartlar	IEC 61439-1&2 · IEC 60617	Sheet size / Kâğıt	A3

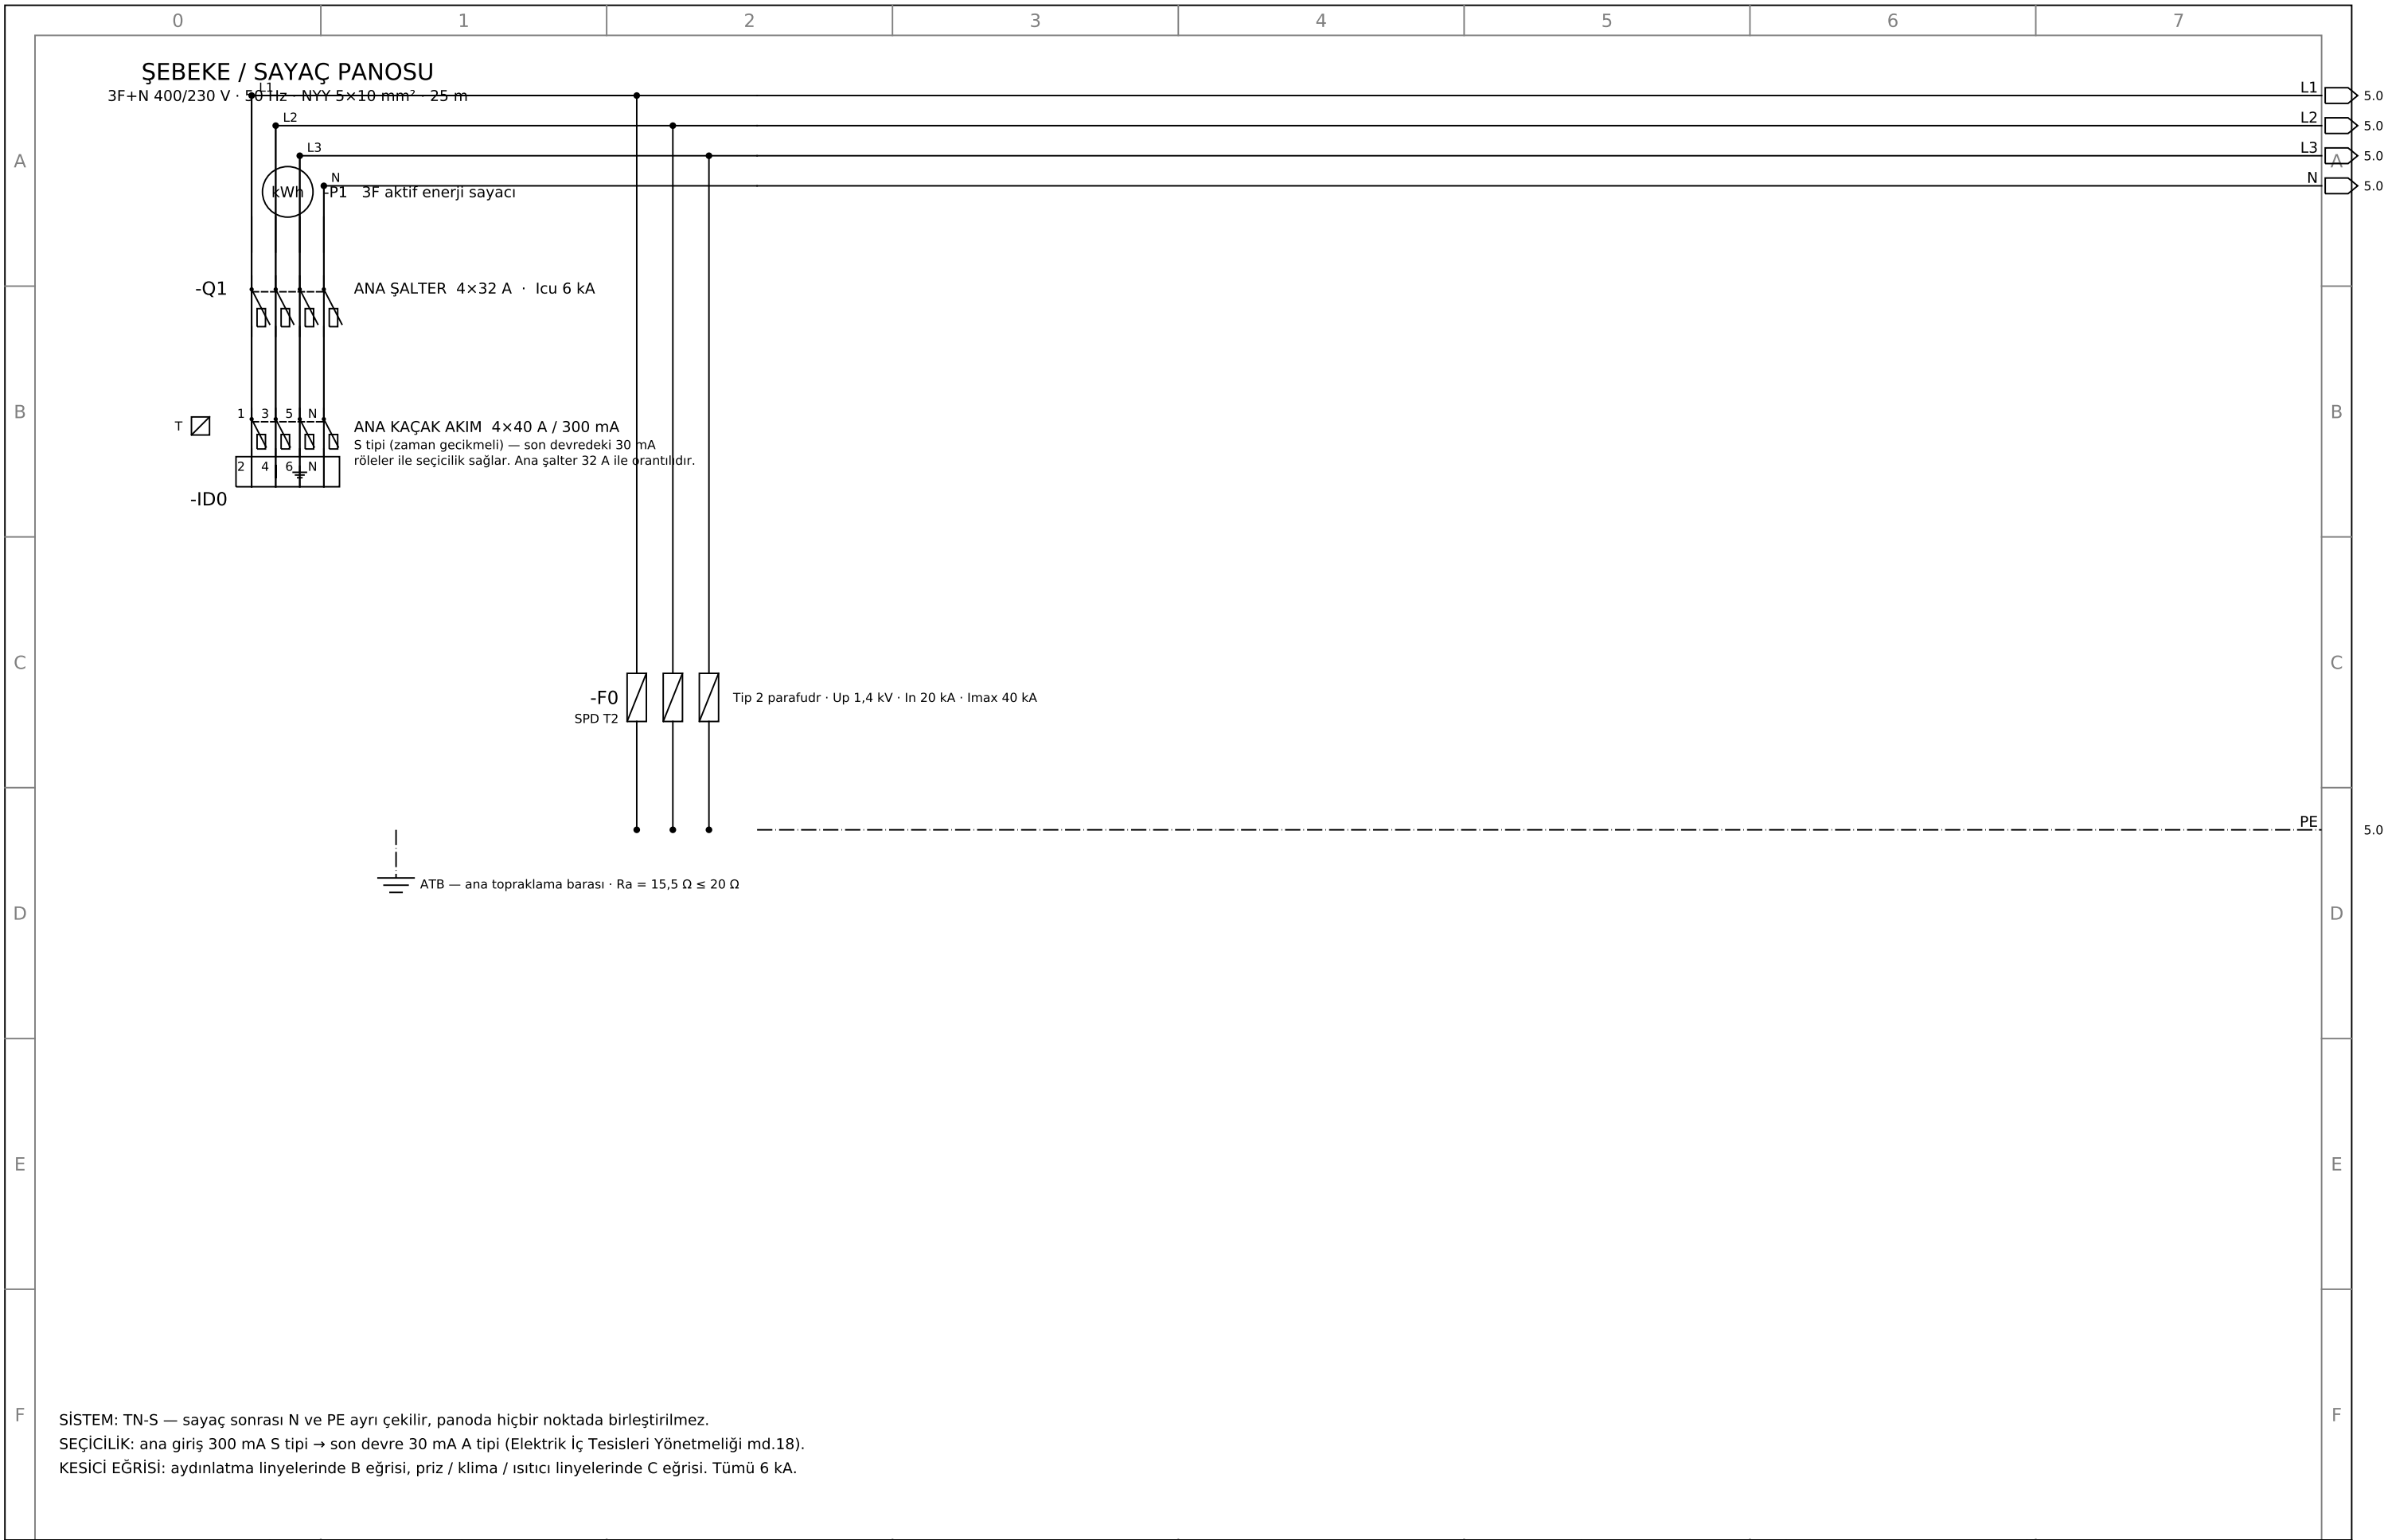


Drawn By / Çizen	CC	Customer Name / Müşteri Adı	ÖZEL — MALTEPE / İDEALTEPE	Project Number / Proje Numarası	GYM-25-001-001	Sheet: / Sayfa	4
Checked By / Kontrol Eden	—	Project Description / Proje Açıklaması	MOBİLYA MAĞAZASI → FONKSİYONEL ANTRENMAN STÜDYOSU			Next sheet: / Sonraki	5
Approved By / Onaylayan	—	Panel Name / Pano Adı	ADP	Revision / Revizyon	Rev H	Total sheets: / Toplam	12
Project Date / Proje Tarihi	17 Eylül 2026	Page Description / Sayfa Açıklaması	Incoming Supply / Ana Besleme	Standards / Standartlar	IEC 61439-1&2 · IEC 60617	Sheet size / Kâğıt	A3

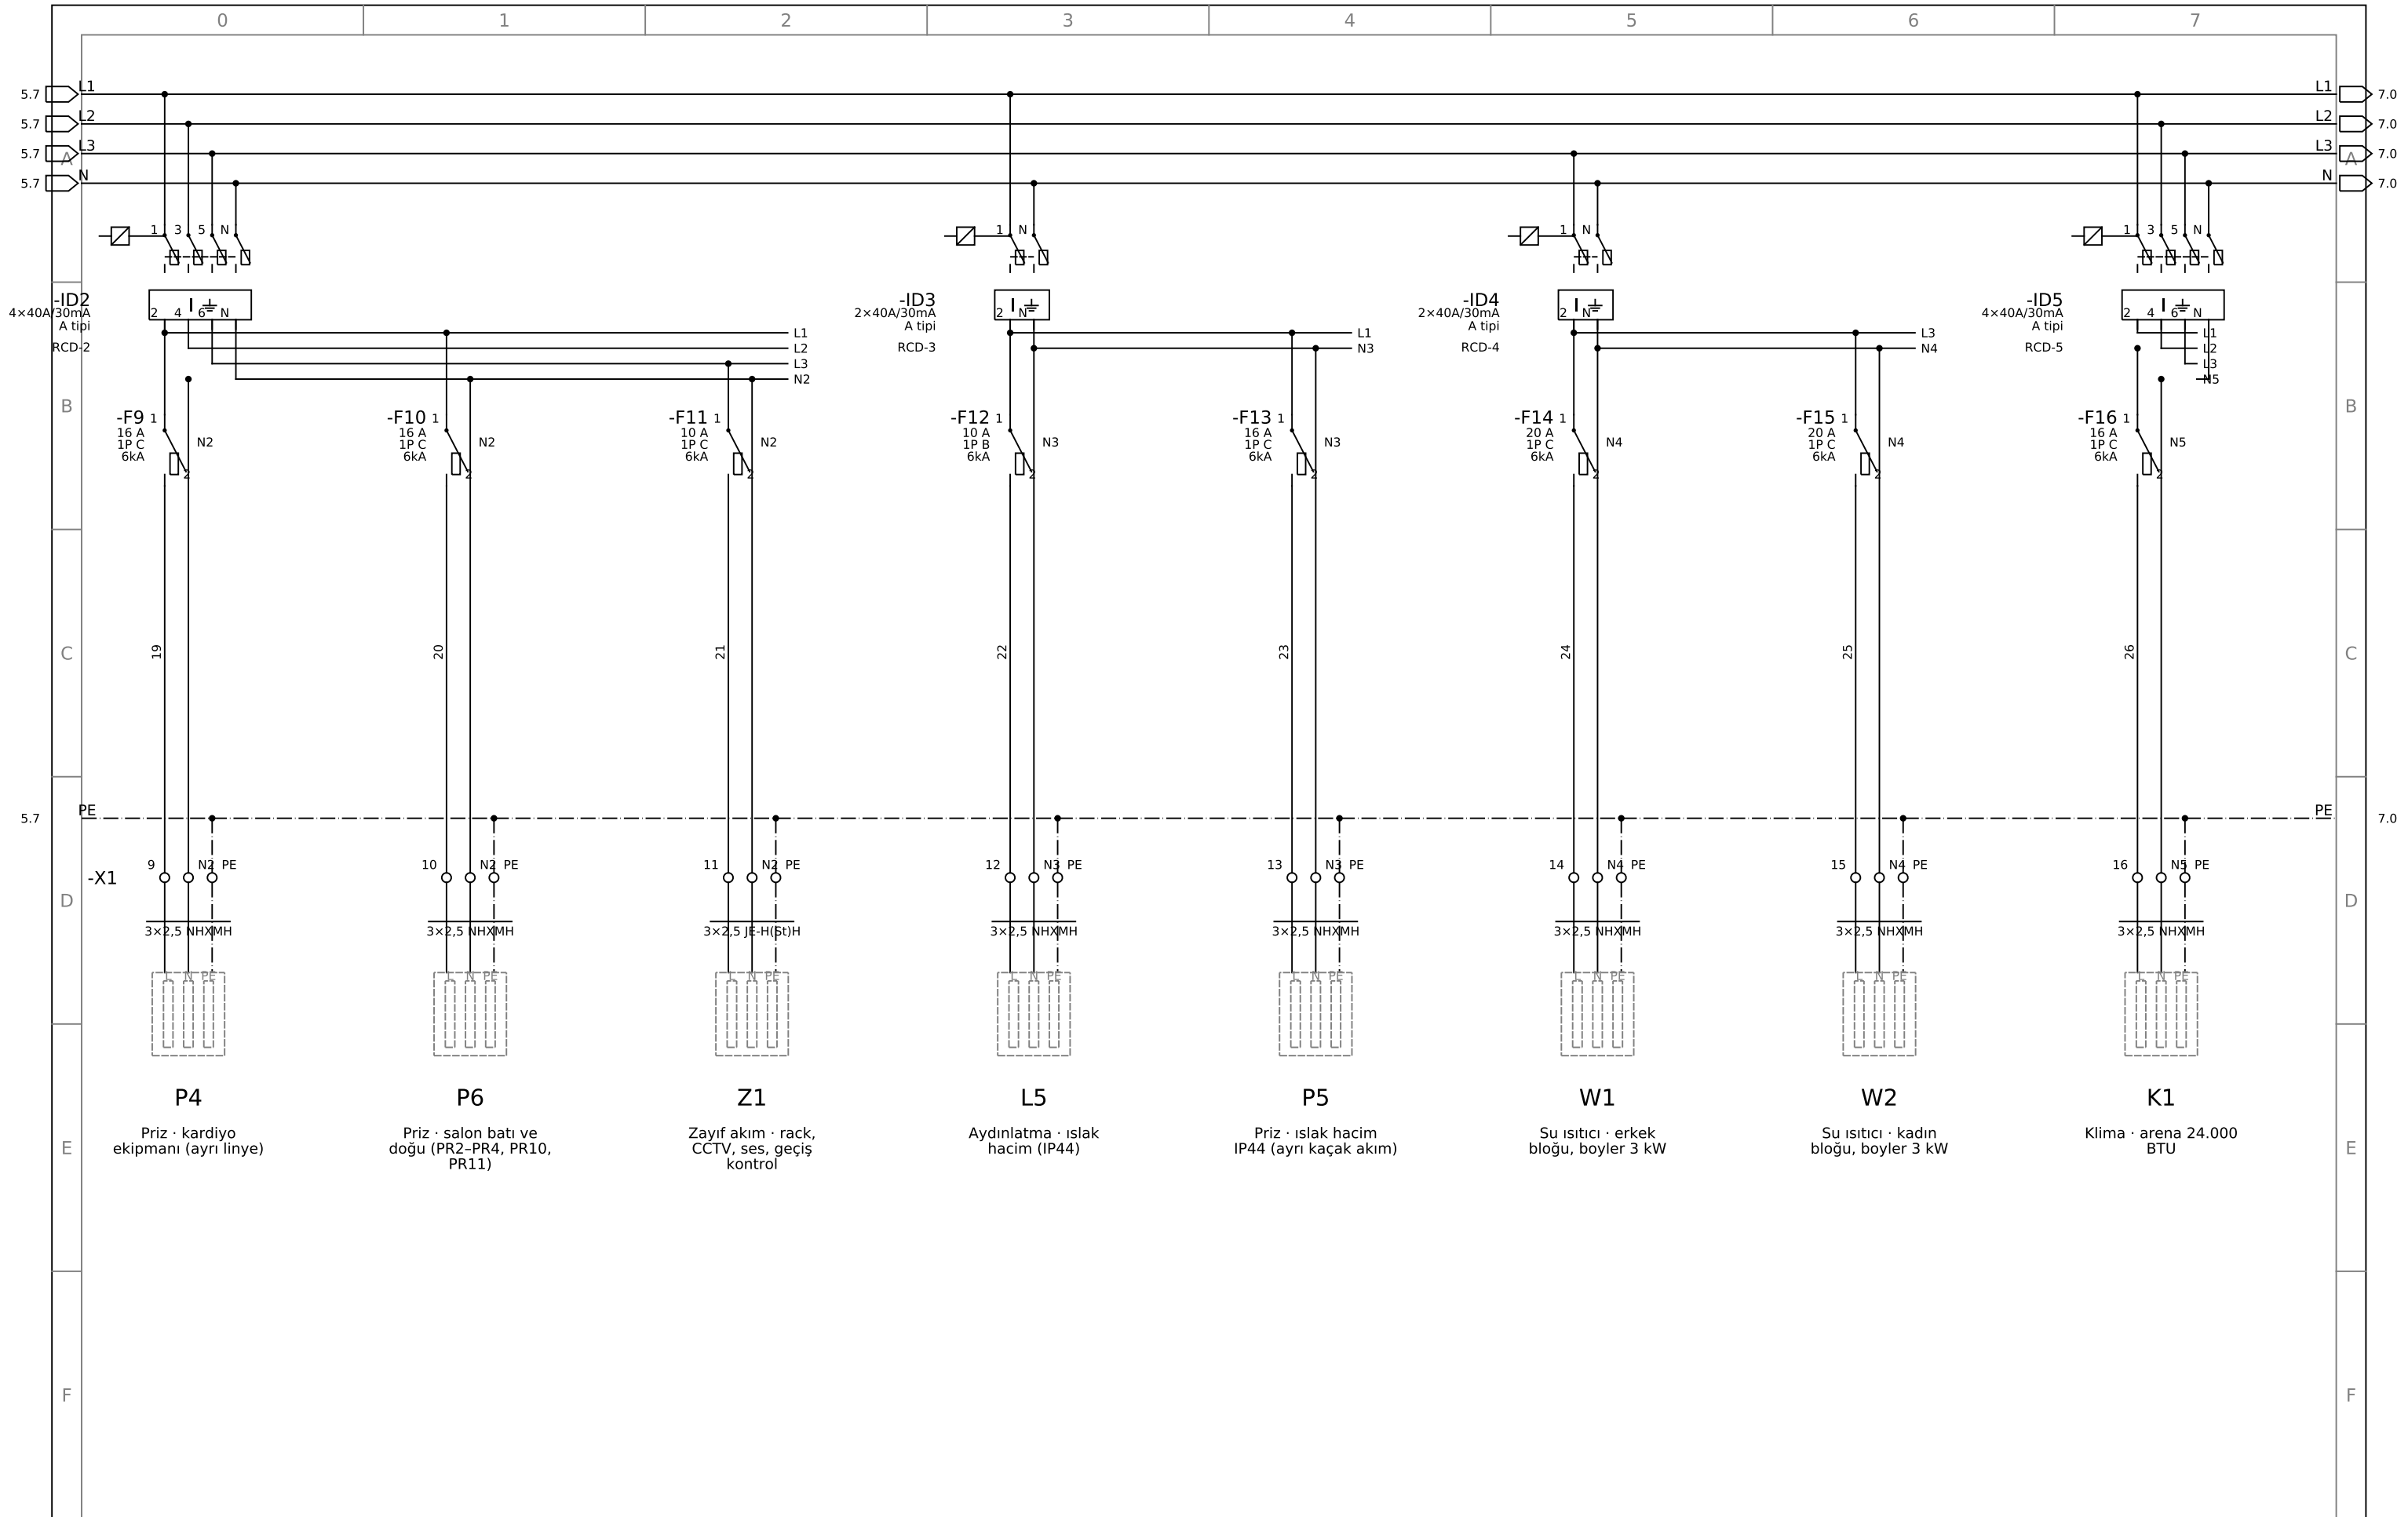

Drawn By / Çizen	CC	Customer Name / Müşteri Adı	ÖZEL — MALTEPE / İDEALTEPE		Project Number / Proje Numarası	GYM-25-001-001	Sheet: / Sayfa	6
Checked By / Kontrol Eden	—	Project Description / Proje Açıklaması	MOBİLYA MAĞAZASI → FONKSİYONEL ANTRENMAN STÜDYOSU				Next sheet: / Sonraki	7
Approved By / Onaylayan	—	Panel Name / Pano Adı	ADP		Revision / Revizyon	Rev H	Total sheets: / Toplam	12
Project Date / Proje Tarihi	17 Eylül 2026	Page Description / Sayfa Açıklaması	Schematic Diagram / Şematik Diyagram		Standards / Standartlar	IEC 61439-1&2 · IEC 60617	Sheet size / Kâğıt	A3

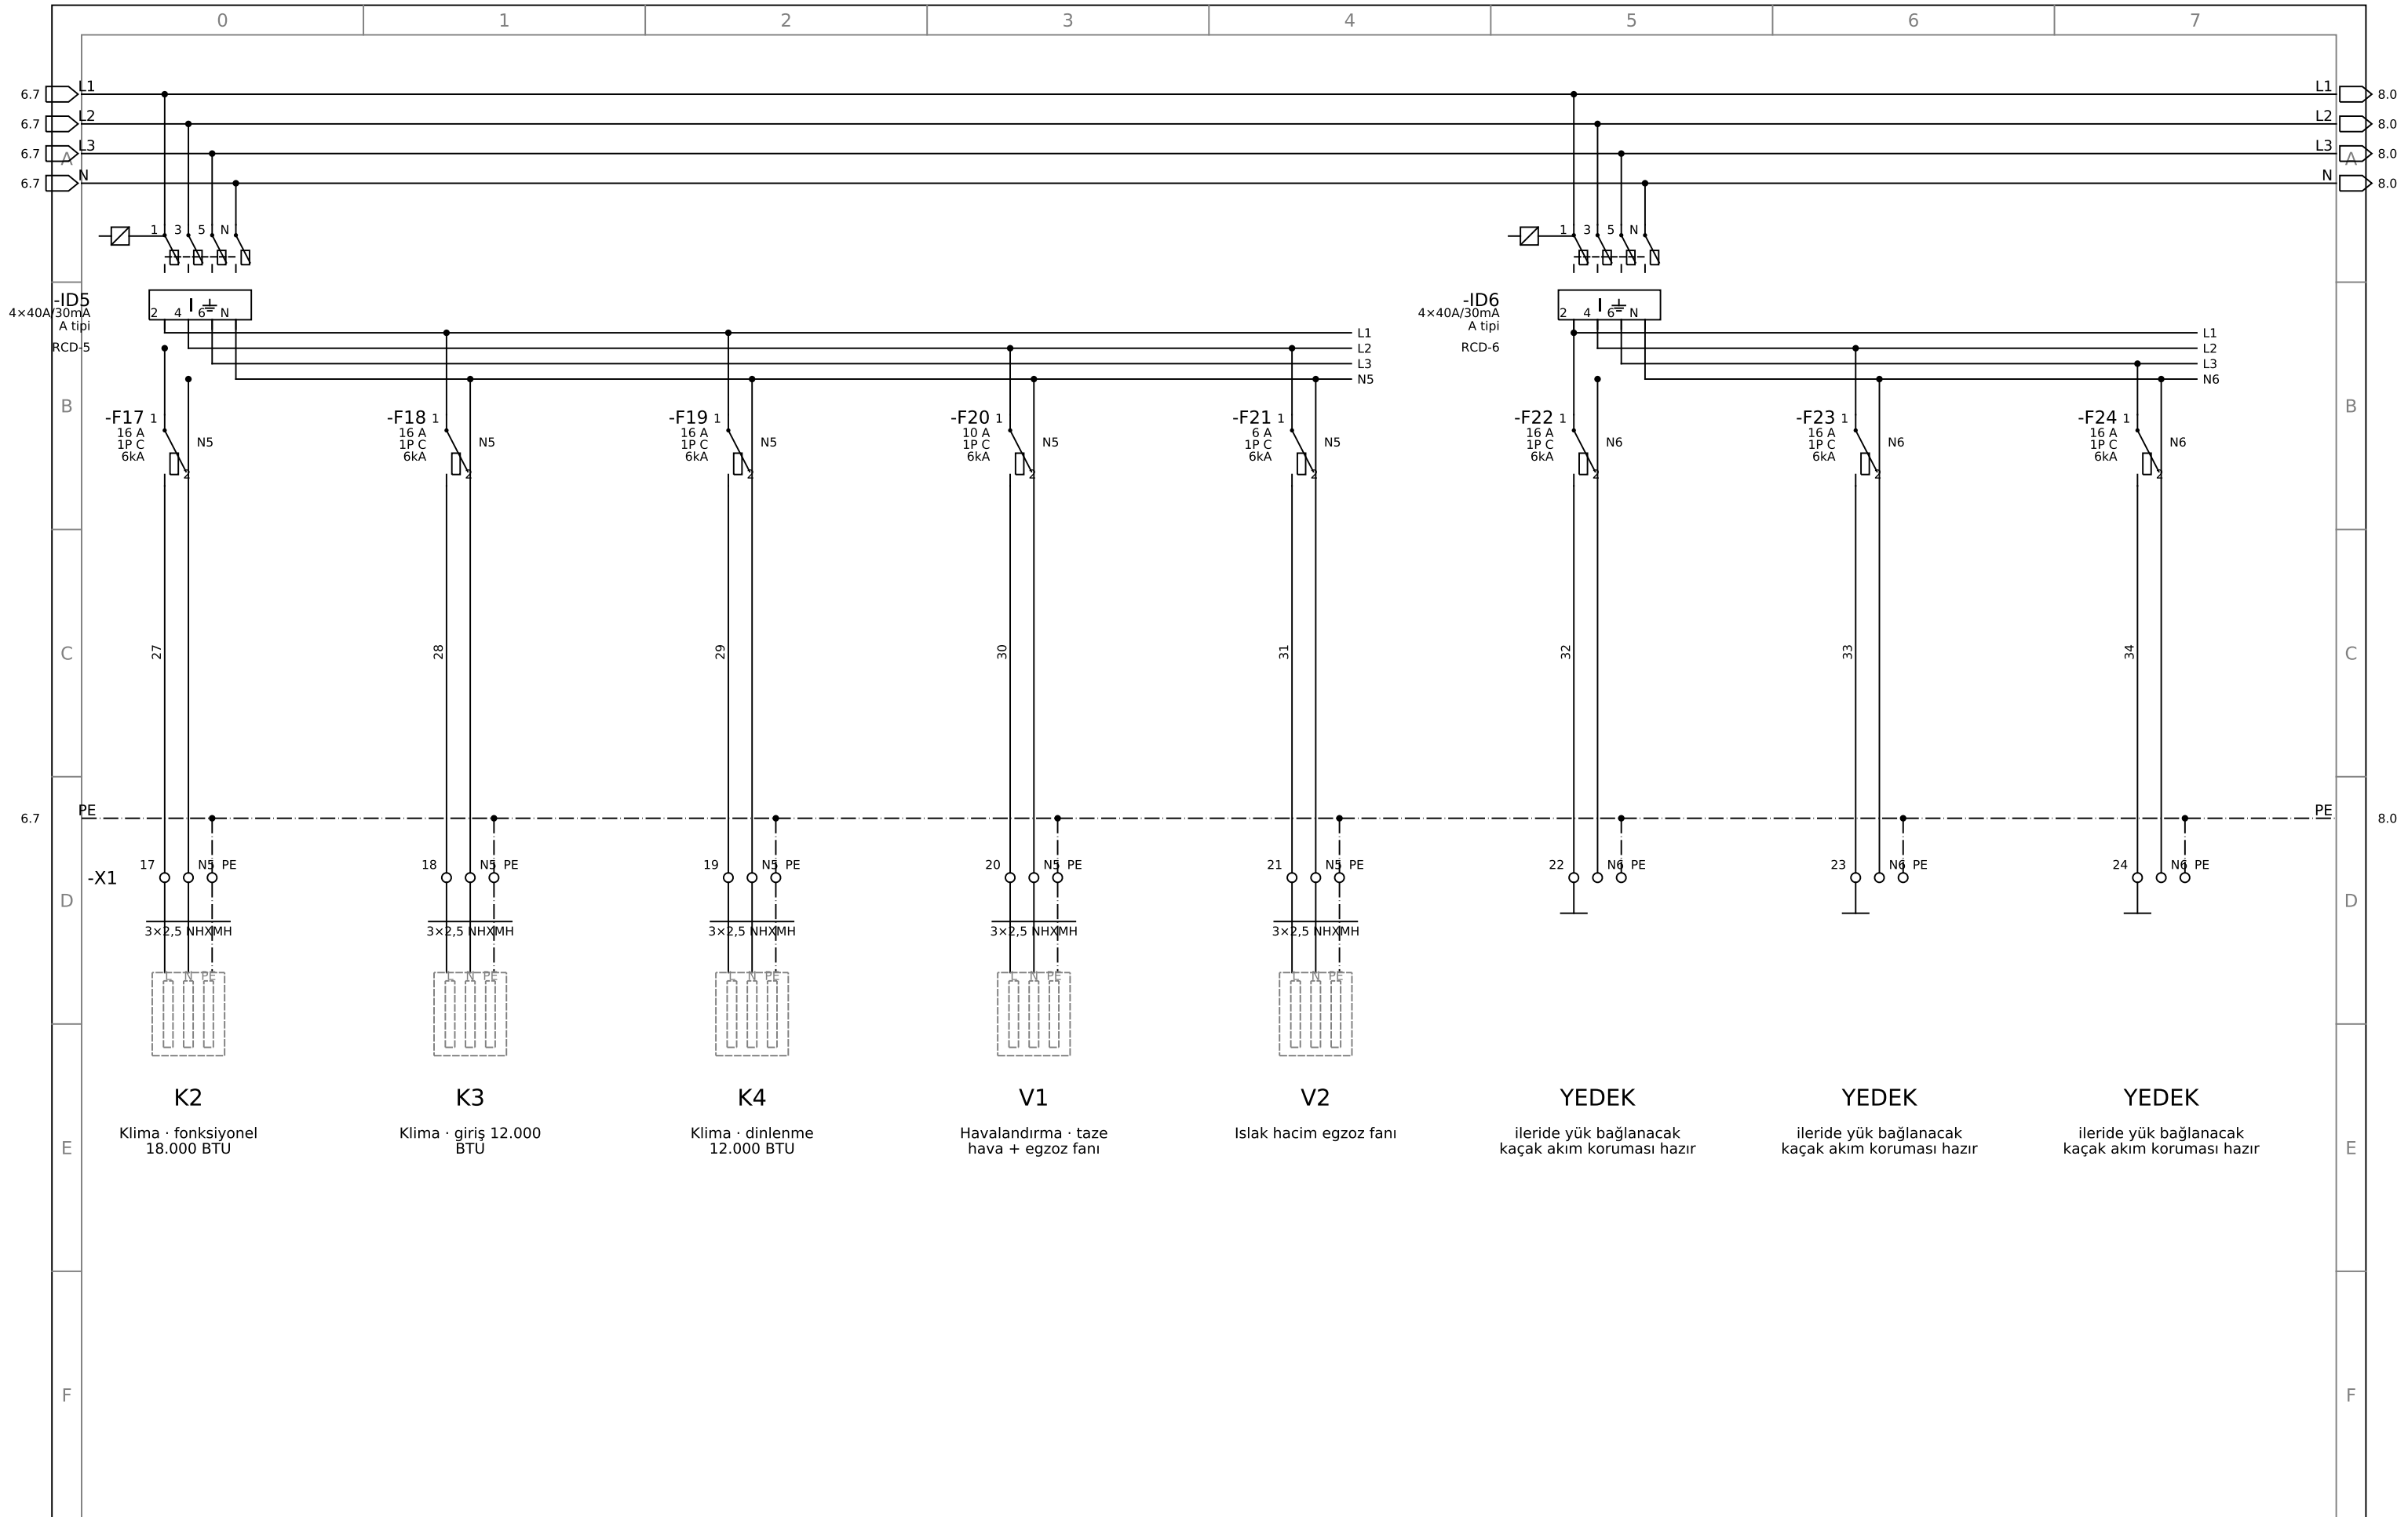

Drawn By / Çizen	CC	Customer Name / Müşteri Adı	ÖZEL — MALTEPE / İDEALTEPE	Project Number / Proje Numarası	GYM-25-001-001	Sheet: / Sayfa	7
Checked By / Kontrol Eden	—	Project Description / Proje Açıklaması	MOBİLYA MAĞAZASI → FONKSİYONEL ANTRENMAN STÜDYOSU			Next sheet: / Sonraki	8
Approved By / Onaylayan	—	Panel Name / Pano Adı	ADP	Revision / Revizyon	Rev H	Total sheets: / Toplam	12
Project Date / Proje Tarihi	17 Eylül 2026	Page Description / Sayfa Açıklaması	Schematic Diagram / Şematik Diyagram	Standards / Standartlar	IEC 61439-1&2 · IEC 60617	Sheet size / Kâğıt	A3

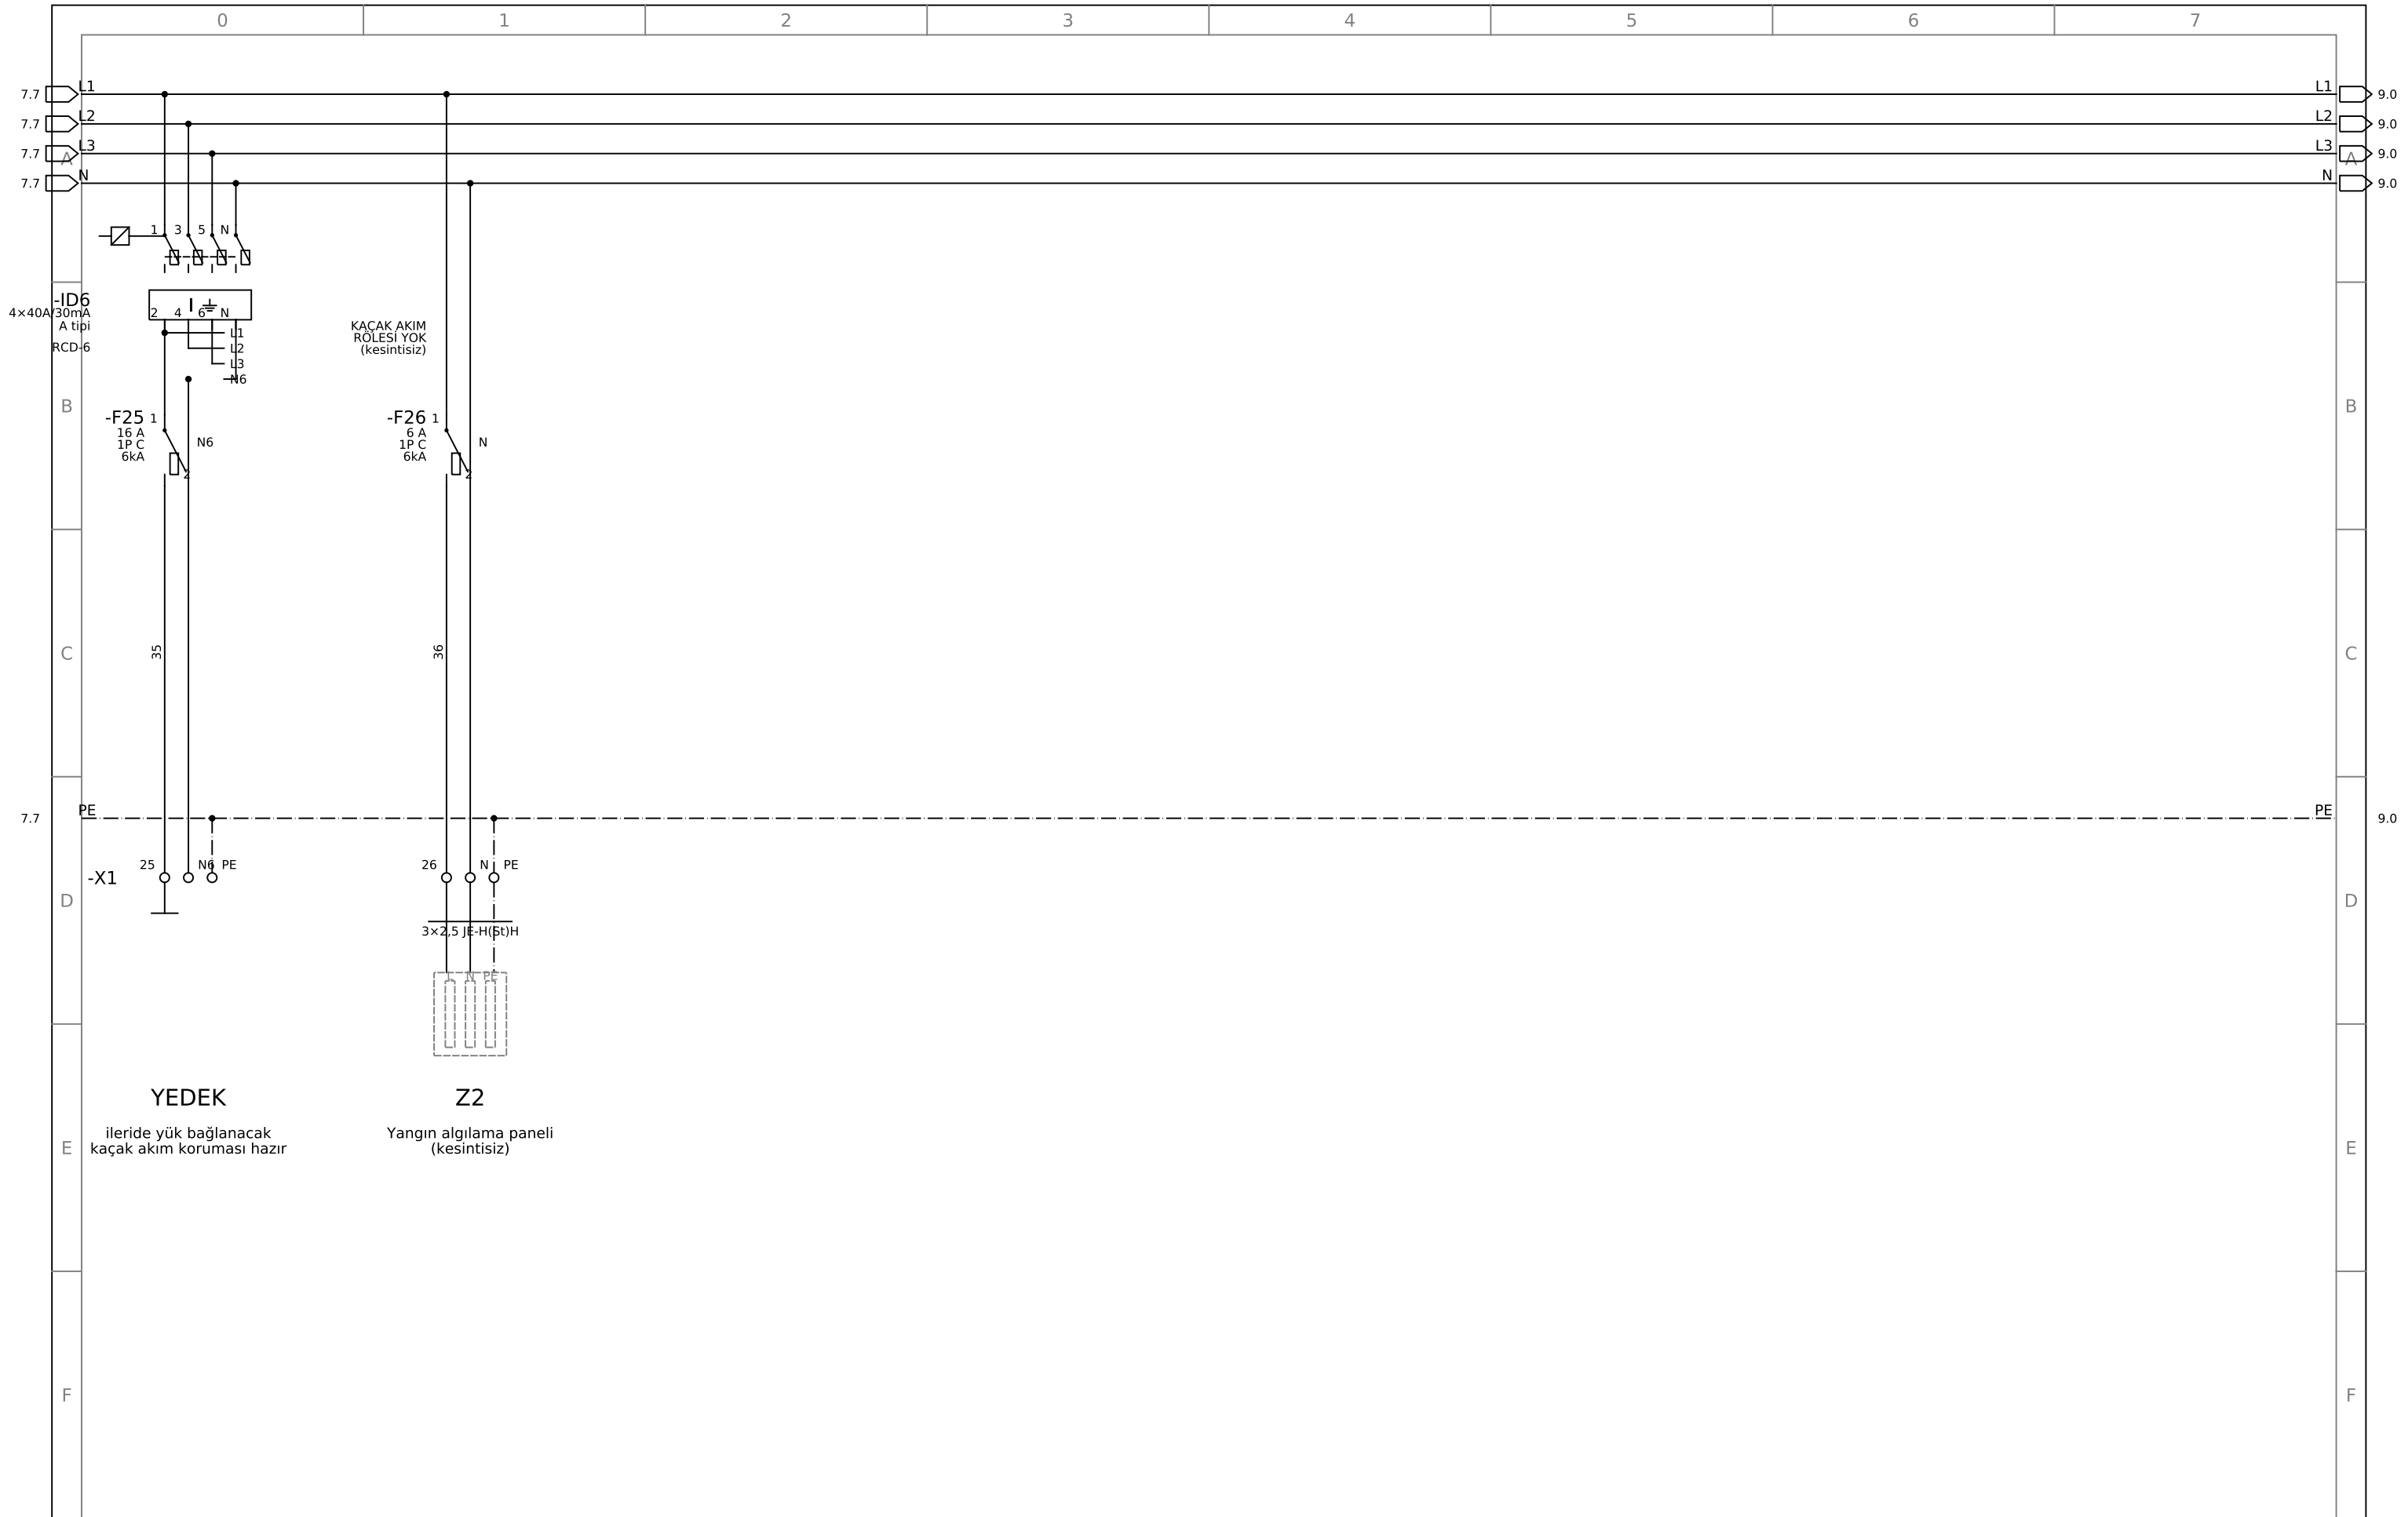

Drawn By / Çizen	CC	Customer Name / Müşteri Adı	ÖZEL — MALTEPE / İDEALTEPE	Project Number / Proje Numarası	GYM-25-001-001	Sheet: / Sayfa	8
Checked By / Kontrol Eden	—	Project Description / Proje Açıklaması	MOBİLYA MAĞAZASI → FONKSİYONEL ANTRENMAN STÜDYOSU			Next sheet: / Sonraki	9
Approved By / Onaylayan	—	Panel Name / Pano Adı	ADP	Revision / Revizyon	Rev H	Total sheets: / Toplam	12
Project Date / Proje Tarihi	17 Eylül 2026	Page Description / Sayfa Açıklaması	Schematic Diagram / Şematik Diyagram	Standards / Standartlar	IEC 61439-1&2 · IEC 60617	Sheet size / Kâğıt	A3

KLEMENS PLANI / TERMINAL DIAGRAM — -X1

A	KLEMENS	LİNYE	İLETKEN	TEL NO	KABLO	HEDEF / DESTINATION	SAYFA	KAÇAK AKIM	A																
		1	L1	L	11	NHXMH 3×2,5	Aydınlatma — arena / serbest ağırlık	5		RCD-1															
			L1	N	N1	NHXMH 3×2,5	Aydınlatma — arena / serbest ağırlık	5		RCD-1															
B			L1	PE	PE	NHXMH 3×2,5	Aydınlatma — arena / serbest ağırlık	5	RCD-1	B															
		2	L2	L	12	NHXMH 3×2,5	Aydınlatma — fonksiyonel / kardiyo	5	RCD-1																
			L2	N	N1	NHXMH 3×2,5	Aydınlatma — fonksiyonel / kardiyo	5	RCD-1																
			L2	PE	PE	NHXMH 3×2,5	Aydınlatma — fonksiyonel / kardiyo	5	RCD-1																
		3	L3	L	13	NHXMH 3×2,5	Aydınlatma — dinlenme salonu	5	RCD-1																
			L3	N	N1	NHXMH 3×2,5	Aydınlatma — dinlenme salonu	5	RCD-1																
			L3	PE	PE	NHXMH 3×2,5	Aydınlatma — dinlenme salonu	5	RCD-1																
		4	L4	L	14	NHXMH 3×2,5	Aydınlatma — giriş / banko	5	RCD-1																
			L4	N	N1	NHXMH 3×2,5	Aydınlatma — giriş / banko	5	RCD-1																
			L4	PE	PE	NHXMH 3×2,5	Aydınlatma — giriş / banko	5	RCD-1																
		5	L6	L	15	NHXMH 3×2,5	Acil aydınlatma ve yönlendirme	5	RCD-1																
			L6	N	N1	NHXMH 3×2,5	Acil aydınlatma ve yönlendirme	5	RCD-1																
			L6	PE	PE	NHXMH 3×2,5	Acil aydınlatma ve yönlendirme	5	RCD-1																
		6	P1	L	16	NHXMH 3×2,5	Priz — salon kuzey (PR12–PR16, PR1)	5	RCD-2																
			P1	N	N2	NHXMH 3×2,5	Priz — salon kuzey (PR12–PR16, PR1)	5	RCD-2																
			P1	PE	PE	NHXMH 3×2,5	Priz — salon kuzey (PR12–PR16, PR1)	5	RCD-2																
		7	P2	L	17	NHXMH 3×2,5	Priz — salon güney (PR5–PR9)	5	RCD-2																
			P2	N	N2	NHXMH 3×2,5	Priz — salon güney (PR5–PR9)	5	RCD-2																
			P2	PE	PE	NHXMH 3×2,5	Priz — salon güney (PR5–PR9)	5	RCD-2																
		8	P3	L	18	NHXMH 3×2,5	Priz — banko, POS, veri	5	RCD-2																
			P3	N	N2	NHXMH 3×2,5	Priz — banko, POS, veri	5	RCD-2																
			P3	PE	PE	NHXMH 3×2,5	Priz — banko, POS, veri	5	RCD-2																
		9	P4	L	19	NHXMH 3×2,5	Priz — kardiyo ekipmanı (ayrı linye)	6	RCD-2																
			P4	N	N2	NHXMH 3×2,5	Priz — kardiyo ekipmanı (ayrı linye)	6	RCD-2																
			P4	PE	PE	NHXMH 3×2,5	Priz — kardiyo ekipmanı (ayrı linye)	6	RCD-2																
		10	P6	L	20	NHXMH 3×2,5	Priz — salon batı ve doğu (PR2–PR4, PR10, PR	6	RCD-2																
			P6	N	N2	NHXMH 3×2,5	Priz — salon batı ve doğu (PR2–PR4, PR10, PR	6	RCD-2																
			P6	PE	PE	NHXMH 3×2,5	Priz — salon batı ve doğu (PR2–PR4, PR10, PR	6	RCD-2																
		11	Z1	L	21	JE-H(St)H 3×2,5	Zayıf akım — rack, CCTV, ses, geçiş kontrol	6	RCD-2																
			Z1	N	N2	JE-H(St)H 3×2,5	Zayıf akım — rack, CCTV, ses, geçiş kontrol	6	RCD-2																
			Z1	PE	PE	JE-H(St)H 3×2,5	Zayıf akım — rack, CCTV, ses, geçiş kontrol	6	RCD-2																
		12	L5	L	22	NHXMH 3×2,5	Aydınlatma — ıslak hacim (IP44)	6	RCD-3																
			L5	N	N3	NHXMH 3×2,5	Aydınlatma — ıslak hacim (IP44)	6	RCD-3																
			L5	PE	PE	NHXMH 3×2,5	Aydınlatma — ıslak hacim (IP44)	6	RCD-3																
		13	P5	L	23	NHXMH 3×2,5	Priz — ıslak hacim IP44 (ayrı kaçak akım)	6	RCD-3																
			P5	N	N3	NHXMH 3×2,5	Priz — ıslak hacim IP44 (ayrı kaçak akım)	6	RCD-3																
			P5	PE	PE	NHXMH 3×2,5	Priz — ıslak hacim IP44 (ayrı kaçak akım)	6	RCD-3																
		14	W1	L	24	NHXMH 3×2,5	Su ısıtıcı — erkek bloğu, boyler 3 kW	6	RCD-4																
			W1	N	N4	NHXMH 3×2,5	Su ısıtıcı — erkek bloğu, boyler 3 kW	6	RCD-4																
			W1	PE	PE	NHXMH 3×2,5	Su ısıtıcı — erkek bloğu, boyler 3 kW	6	RCD-4																
		15	W2	L	25	NHXMH 3×2,5	Su ısıtıcı — kadın bloğu, boyler 3 kW	6	RCD-4																
			W2	N	N4	NHXMH 3×2,5	Su ısıtıcı — kadın bloğu, boyler 3 kW	6	RCD-4																
			W2	PE	PE	NHXMH 3×2,5	Su ısıtıcı — kadın bloğu, boyler 3 kW	6	RCD-4																
		16	K1	L	26	NHXMH 3×2,5	Klima — arena 24.000 BTU	6	RCD-5																
			K1	N	N5	NHXMH 3×2,5	Klima — arena 24.000 BTU	6	RCD-5																
			K1	PE	PE	NHXMH 3×2,5	Klima — arena 24.000 BTU	6	RCD-5																
		17	K2	L	27	NHXMH 3×2,5	Klima — fonksiyonel 18.000 BTU	7	RCD-5																
			K2	N	N5	NHXMH 3×2,5	Klima — fonksiyonel 18.000 BTU	7	RCD-5																
			K2	PE	PE	NHXMH 3×2,5	Klima — fonksiyonel 18.000 BTU	7	RCD-5																
		18	K3	L	28	NHXMH 3×2,5	Klima — giriş 12.000 BTU	7	RCD-5																
			K3	N	N5	NHXMH 3×2,5	Klima — giriş 12.000 BTU	7	RCD-5																
			K3	PE	PE	NHXMH 3×2,5	Klima — giriş 12.000 BTU	7	RCD-5																
		19	K4	L	29	NHXMH 3×2,5	Klima — dinlenme 12.000 BTU	7	RCD-5																
			K4	N	N5	NHXMH 3×2,5	Klima — dinlenme 12.000 BTU	7	RCD-5																
			K4	PE	PE	NHXMH 3×2,5	Klima — dinlenme 12.000 BTU	7	RCD-5																
		20	V1	L	30	NHXMH 3×2,5	Havalandırma — taze hava + egzoz fanı	7	RCD-5																
			V1	N	N5	NHXMH 3×2,5	Havalandırma — taze hava + egzoz fanı	7	RCD-5																
D	Checked By / Kontrol Eden	CC	Customer Name / Müşteri Adı	ÖZEL — MALTEPE / IDEALTEPE	N	Havalandırma — taze hava + egzoz fanı	7	RCD-5		Project Number / Proje Numarası	GYM-25-001-001	Sheet: / Sayfa	9												
														F	By / Onaylayan	V1	Project Description / Proje Açıklaması	F	N	Havalandırma — taze hava + egzoz fanı	7	RCD-5		Next sheet: / Sonraki	10
Project Date / Proje Tarihi	17 Eylül 2026	Page Description / Sayfa Açıklaması	P	N	Islak hacim egzoz fanı	7	RCD-5		Sheet size / Kağıt	A3															

	0	1	2	3	4	5	6	7																																			
A	PANO ÖNDEN GÖRÜNÜŞ / PANEL FRONT VIEW — ölçek 1:5								A																																		
B									B																																		
C	ADP · 800×1000×250 mm · IP54 · Form 2b · sac gövde RAL 7035								C																																		
D	R1	<table><tr><td>-Q1</td><td>-ID0</td><td>-F0</td><td colspan="4">BOŞ 12 MOD</td></tr><tr><td>4</td><td>4</td><td>4</td><td colspan="4"></td></tr></table>							-Q1	-ID0	-F0	BOŞ 12 MOD				4	4	4					D																				
-Q1	-ID0	-F0	BOŞ 12 MOD	
4	4	4	
E	R2	<table><tr><td>-ID1</td><td>-F1</td><td>-F2</td><td>-F3</td><td>-F4</td><td>-F5</td><td>-ID2</td></tr><tr><td>4</td><td>3</td><td>3</td><td>3</td><td>3</td><td>3</td><td>4</td></tr></table> BOŞ 1 MOD							-ID1	-F1	-F2	-F3	-F4	-F5	-ID2	4	3	3	3	3	3	4	E																				
-ID1	-F1	-F2	-F3	-F4	-F5	-ID2																																					
4	3	3	3	3	3	4																																					
F	R3	<table><tr><td>-F6</td><td>-F7</td><td>-F8</td><td>-F9</td><td>-F10</td><td>-F11</td><td>-ID3</td><td>-F12</td></tr><tr><td>3</td><td>3</td><td>3</td><td>3</td><td>3</td><td>3</td><td>2</td><td>3</td></tr></table> BOŞ 1 MOD							-F6	-F7	-F8	-F9	-F10	-F11	-ID3	-F12	3	3	3	3	3	3	2	3	F																		
-F6	-F7	-F8	-F9	-F10	-F11	-ID3	-F12																																				
3	3	3	3	3	3	2	3																																				
	R4	<table><tr><td>-F13</td><td>-ID4</td><td>-F14</td><td>-F15</td><td>-ID5</td><td>-F16</td><td>-F17</td><td>-F18</td><td>-F19</td><td>-F20</td><td>-F21</td><td>-ID6</td><td>-F22</td><td>-F23</td><td>-F24</td><td>-F25</td><td>-F26</td></tr><tr><td>3</td><td>2</td><td>3</td><td>3</td><td>4</td><td>3</td><td>3</td><td>3</td><td>3</td><td>3</td><td>3</td><td>4</td><td>1</td><td>1</td><td>1</td><td>1</td><td>3</td></tr></table>							-F13	-ID4	-F14	-F15	-ID5	-F16	-F17	-F18	-F19	-F20	-F21	-ID6	-F22	-F23	-F24	-F25	-F26	3	2	3	3	4	3	3	3	3	3	3	4	1	1	1	1	3	
-F13	-ID4	-F14	-F15	-ID5	-F16	-F17	-F18	-F19	-F20	-F21	-ID6	-F22	-F23	-F24	-F25	-F26																											
3	2	3	3	4	3	3	3	3	3	3	4	1	1	1	1	3																											
Drawn By / Çizen		CC	Customer Name / Müşteri Adı		ÖZEL — MALTEPE / İDEALTEPE				Project Number / Proje Numarası		GYM-25-001-001		Sheet: / Sayfa		10																												
Checked By / Kontrol Eden		—	Project Description / Proje Açıklaması		MOBİLYA MAĞAZASI → FONKSİYONEL ANTRENMAN STÜDYOSU								Next sheet: / Sonraki		11																												
Approved By / Onaylayan		—	Panel Name / Pano Adı		ADP				Revision / Revizyon		Rev H		Total sheets: / Toplam		12																												
Project Date / Proje Tarihi		17 Eylül 2026		Page Description / Sayfa Açıklaması		Panel Overview / Pano Önden Görünüş				Standards / Standartlar		IEC 61439-1&2 · IEC 60617		Sheet size / Kâğıt		A3																											

SIRA	CİHAZ	MODÜL	AÇIKLAMA
R1	-Q1	4	ANA ŞALTER 4×32 A
R1	-ID0	4	ANA KAÇAK AKIM 4×40 A/300 mA
R1	-F0	4	SPD Tip 2
R2	-ID1	4	4×40 A / 30 mA, A tipi
R2	-F1	3	L1 10A B
R2	-F2	3	L2 10A B
R2	-F3	3	L3 10A B
R2	-F4	3	L4 10A B
R2	-F5	3	L6 6A B
R2	-ID2	4	4×40 A / 30 mA, A tipi
R3	-F6	3	P1 16A C
R3	-F7	3	P2 16A C
R3	-F8	3	P3 16A C
R3	-F9	3	P4 16A C
R3	-F10	3	P6 16A C
R3	-F11	3	Z1 10A C
R3	-ID3	2	2×40 A / 30 mA, A tipi
R3	-F12	3	L5 10A B
R4	-F13	3	P5 16A C
R4	-ID4	2	2×40 A / 30 mA, A tipi
R4	-F14	3	W1 20A C
R4	-F15	3	W2 20A C
R4	-ID5	4	4×40 A / 30 mA, A tipi
R4	-F16	3	K1 16A C
R4	-F17	3	K2 16A C
R4	-F18	3	K3 16A C
R4	-F19	3	K4 16A C
R4	-F20	3	V1 10A C
R4	-F21	3	V2 6A C
R4	-ID6	4	4×40 A / 30 mA, A tipi
R4	-F22	1	Y1 16A C
R4	-F23	1	Y2 16A C
R4	-F24	1	Y3 16A C
R4	-F25	1	Y4 16A C
R4	-F26	3	Z2 6A C

	0	1	2	3	4	5	6	7							
A	ADP YÜKLEME CETVELİ / LOAD SCHEDULE														A
	Grup kaçak akım röleleri ve kapsadıkları linyeler ayrı sütunda gösterilmiştir.														
	NO	LİNYE	MAHAL / YÜK	FAZ	KESİCİ	KAÇAK AKIM (GRUP)	KABLO	BORU	UZUNLUK	Pb (kW)	cos φ	Ib (A)	ΔU (%)	SONUÇ	
	1	L1	Aydınlatma — arena / serbest ağırlık	L2	10 A · 1P B · 6 kA	RCD-1 · 4×40 A / 30 mA A tipi	NHXMH 3×2,5	Ø20	14 m	0,28	0,95	1,3	0,13	UYGUN	
	2	L2	Aydınlatma — fonksiyonel / kardiyo	L3	10 A · 1P B · 6 kA	↑ aynı grup	NHXMH 3×2,5	Ø20	11 m	0,12	0,95	0,5	0,05	UYGUN	
	3	L3	Aydınlatma — dinlenme salonu	L1	10 A · 1P B · 6 kA	↑ aynı grup	NHXMH 3×2,5	Ø20	14 m	0,12	0,95	0,5	0,06	UYGUN	
	4	L4	Aydınlatma — giriş / banko	L3	10 A · 1P B · 6 kA	↑ aynı grup	NHXMH 3×2,5	Ø20	12 m	0,08	0,95	0,4	0,03	UYGUN	
	5	L6	Acil aydınlatma ve yönlendirme	L2	6 A · 1P B · 6 kA	↑ aynı grup	NHXMH 3×2,5	Ø20	10 m	0,06	0,95	0,3	0,02	UYGUN	
B	6	P1	Priz — salon kuzey (PR12-PR16, PR1)	L1	16 A · 1P C · 6 kA	RCD-2 · 4×40 A / 30 mA A tipi	NHXMH 3×2,5	Ø20	8 m	0,90	0,90	4,3	0,24	UYGUN	B
	7	P2	Priz — salon güney (PR5-PR9)	L3	16 A · 1P C · 6 kA	↑ aynı grup	NHXMH 3×2,5	Ø20	16 m	0,75	0,90	3,6	0,42	UYGUN	
	8	P3	Priz — banko, POS, veri	L2	16 A · 1P C · 6 kA	↑ aynı grup	NHXMH 3×2,5	Ø20	9 m	1,00	0,90	4,8	0,30	UYGUN	
	9	P4	Priz — kardiyo ekipmanı (ayrı linye)	L1	16 A · 1P C · 6 kA	↑ aynı grup	NHXMH 3×2,5	Ø20	17 m	2,40	0,90	11,6	1,40	UYGUN	
	10	P6	Priz — salon batı ve doğu (PR2-PR4, PR	L1	16 A · 1P C · 6 kA	↑ aynı grup	NHXMH 3×2,5	Ø20	10 m	0,75	0,90	3,6	0,27	UYGUN	
	11	Z1	Zayıf akım — rack, CCTV, ses, geçiş ko	L3	10 A · 1P C · 6 kA	↑ aynı grup	JE-H(St)H 3×2,5	Ø20	9 m	0,60	0,90	2,9	0,18	UYGUN	
	12	L5	Aydınlatma — ıslak hacim (IP44)	L1	10 A · 1P B · 6 kA	RCD-3 · 2×40 A / 30 mA A tipi	NHXMH 3×2,5	Ø20	16 m	0,11	0,95	0,5	0,06	UYGUN	
	13	P5	Priz — ıslak hacim IP44 (ayrı kaçak ak	L3	16 A · 1P C · 6 kA	↑ aynı grup	NHXMH 3×2,5	Ø20	16 m	0,50	0,90	2,4	0,27	UYGUN	
C	14	W1	Su ısıtıcı — erkek bloğu, boyler 3 kW	L3	20 A · 1P C · 6 kA	RCD-4 · 2×40 A / 30 mA A tipi	NHXMH 3×2,5	Ø20	16 m	3,00	1,00	13,0	1,65	UYGUN	C
	15	W2	Su ısıtıcı — kadın bloğu, boyler 3 kW	L3	20 A · 1P C · 6 kA	↑ aynı grup	NHXMH 3×2,5	Ø20	19 m	3,00	1,00	13,0	1,97	UYGUN	
	16	K1	Klima — arena 24.000 BTU	L2	16 A · 1P C · 6 kA	RCD-5 · 4×40 A / 30 mA A tipi	NHXMH 3×2,5	Ø20	18 m	2,20	0,85	11,3	1,32	UYGUN	
	17	K2	Klima — fonksiyonel 18.000 BTU	L2	16 A · 1P C · 6 kA	↑ aynı grup	NHXMH 3×2,5	Ø20	13 m	1,70	0,85	8,7	0,73	UYGUN	
	18	K3	Klima — giriş 12.000 BTU	L1	16 A · 1P C · 6 kA	↑ aynı grup	NHXMH 3×2,5	Ø20	12 m	1,15	0,85	5,9	0,48	UYGUN	
	19	K4	Klima — dinlenme 12.000 BTU	L1	16 A · 1P C · 6 kA	↑ aynı grup	NHXMH 3×2,5	Ø20	15 m	1,15	0,85	5,9	0,58	UYGUN	
	20	V1	Havalandırma — taze hava + egzoz fanı	L2	10 A · 1P C · 6 kA	↑ aynı grup	NHXMH 3×2,5	Ø20	14 m	0,45	0,85	2,3	0,21	UYGUN	
	21	V2	Islak hacim egzoz fanı	L2	6 A · 1P C · 6 kA	↑ aynı grup	NHXMH 3×2,5	Ø20	16 m	0,12	0,85	0,6	0,07	UYGUN	
D	22	Y1	YEDEK — ileride yük bağlanacak	L1	16 A · 1P C · 6 kA	RCD-6 · 4×40 A / 30 mA A tipi	—	—	—	—	—	—	—	YEDEK	D
	23	Y2	YEDEK — ileride yük bağlanacak	L2	16 A · 1P C · 6 kA	↑ aynı grup	—	—	—	—	—	—	—	YEDEK	
	24	Y3	YEDEK — ileride yük bağlanacak	L3	16 A · 1P C · 6 kA	↑ aynı grup	—	—	—	—	—	—	—	YEDEK	
	25	Y4	YEDEK — ileride yük bağlanacak	L1	16 A · 1P C · 6 kA	↑ aynı grup	—	—	—	—	—	—	—	YEDEK	
	26	Z2	Yangın algılama paneli (kesintisiz)	L1	6 A · 1P C · 6 kA	— kaçak akım rölesi yok (kesintisiz)	JE-H(St)H 3×2,5	Ø20	10 m	0,15	0,90	0,7	0,05	UYGUN	
E	ÖZET / SUMMARY														E
	Bağlı güç / Connected		20,59 kW	Talep gücü / Demand		14,63 kW	L1 / L2 / L3 (kW)		4,86 / 4,91 / 4,87	Faz dengesizliği / Imbalance		%1,0			
	Ana şalter / Main switch		4×32 A	Ana kaçak akım / Main RCD		4×40 A / 300 mA S tipi	Grup kaçak akım sayısı / RCD groups		7 adet	Toplam ΔU / Total		%2,49			
F															F
Drawn By / ÇizenCCCustomer Name / Müşteri AdıÖZEL — MALTEPE / İDEALTEPEProject Number / Proje NumarasıGYM-25-001-001Sheet: / Sayfa11															
Checked By / Kontrol Eden—Project Description / Proje AçıklamasıMOBİLYA MAĞAZASI → FONKSİYONEL ANTRENMAN STÜDYOSURevision / RevizyonRev HNext sheet: / Sonraki12															
Approved By / Onaylayan—Panel Name / Pano AdıADPTotal sheets: / Toplam12															
Project Date / Proje Tarihi17 Eylül 2026Page Description / Sayfa AçıklamasıLoad Schedule / Yükleme CetveliStandards / StandartlarIEC 61439-1&2 · IEC 60617Sheet size / KâğıtA3															

	0	1	2	3	4	5	6	7	
A	MALZEME LİSTESİ / PARTS LIST <table><tr><th>S.NO</th><th>MALZEME / MATERIAL</th><th>BİRİM</th><th>MİKTAR</th></tr><tr><td>1</td><td>Otomatik sigorta 2×16 A C eğrisi · 6 kA</td><td>adet</td><td>10</td></tr><tr><td>2</td><td>Otomatik sigorta 2×10 A B eğrisi · 6 kA</td><td>adet</td><td>5</td></tr><tr><td>3</td><td>Otomatik sigorta 1×16 A C eğrisi · 6 kA</td><td>adet</td><td>4</td></tr><tr><td>4</td><td>Kaçak akım rölesi 4×40 A / 30 mA, A tipi</td><td>adet</td><td>4</td></tr><tr><td>5</td><td>Otomatik sigorta 2×10 A C eğrisi · 6 kA</td><td>adet</td><td>2</td></tr><tr><td>6</td><td>Otomatik sigorta 2×20 A C eğrisi · 6 kA</td><td>adet</td><td>2</td></tr><tr><td>7</td><td>Otomatik sigorta 2×6 A C eğrisi · 6 kA</td><td>adet</td><td>2</td></tr><tr><td>8</td><td>Kaçak akım rölesi 2×40 A / 30 mA, A tipi</td><td>adet</td><td>2</td></tr><tr><td>9</td><td>Otomatik sigorta 2×6 A B eğrisi · 6 kA</td><td>adet</td><td>1</td></tr><tr><td>10</td><td>Ana şalter 4×32 A yük ayırıcı</td><td>adet</td><td>1</td></tr><tr><td>11</td><td>Ana kaçak akım rölesi 4×40 A / 300 mA S tipi</td><td>adet</td><td>1</td></tr><tr><td>12</td><td>Parafudr Tip 2 · Up 1,4 kV · In 20 kA (3F+N)</td><td>adet</td><td>1</td></tr><tr><td>13</td><td>Pano gövdesi 800×1000×250 mm IP54 Form 2b</td><td>adet</td><td>1</td></tr><tr><td>14</td><td>Bakır bara seti 3F+N+PE</td><td>adet</td><td>1</td></tr><tr><td>15</td><td>Klemens sırası -X1 (vidalı, 4 mm²)</td><td>adet</td><td>66</td></tr><tr><td>16</td><td>Etiket seti (PVC, Türkçe, vidalı)</td><td>adet</td><td>1</td></tr></table>								S.NO	MALZEME / MATERIAL	BİRİM	MİKTAR	1	Otomatik sigorta 2×16 A C eğrisi · 6 kA	adet	10	2	Otomatik sigorta 2×10 A B eğrisi · 6 kA	adet	5	3	Otomatik sigorta 1×16 A C eğrisi · 6 kA	adet	4	4	Kaçak akım rölesi 4×40 A / 30 mA, A tipi	adet	4	5	Otomatik sigorta 2×10 A C eğrisi · 6 kA	adet	2	6	Otomatik sigorta 2×20 A C eğrisi · 6 kA	adet	2	7	Otomatik sigorta 2×6 A C eğrisi · 6 kA	adet	2	8	Kaçak akım rölesi 2×40 A / 30 mA, A tipi	adet	2	9	Otomatik sigorta 2×6 A B eğrisi · 6 kA	adet	1	10	Ana şalter 4×32 A yük ayırıcı	adet	1	11	Ana kaçak akım rölesi 4×40 A / 300 mA S tipi	adet	1	12	Parafudr Tip 2 · Up 1,4 kV · In 20 kA (3F+N)	adet	1	13	Pano gövdesi 800×1000×250 mm IP54 Form 2b	adet	1	14	Bakır bara seti 3F+N+PE	adet	1	15	Klemens sırası -X1 (vidalı, 4 mm²)	adet	66	16	Etiket seti (PVC, Türkçe, vidalı)	adet	1	A
S.NO									MALZEME / MATERIAL	BİRİM	MİKTAR	
1									Otomatik sigorta 2×16 A C eğrisi · 6 kA	adet	10	
2									Otomatik sigorta 2×10 A B eğrisi · 6 kA	adet	5	
3									Otomatik sigorta 1×16 A C eğrisi · 6 kA	adet	4	
4									Kaçak akım rölesi 4×40 A / 30 mA, A tipi	adet	4	
5									Otomatik sigorta 2×10 A C eğrisi · 6 kA	adet	2	
6									Otomatik sigorta 2×20 A C eğrisi · 6 kA	adet	2	
7									Otomatik sigorta 2×6 A C eğrisi · 6 kA	adet	2	
8									Kaçak akım rölesi 2×40 A / 30 mA, A tipi	adet	2	
9									Otomatik sigorta 2×6 A B eğrisi · 6 kA	adet	1	
10									Ana şalter 4×32 A yük ayırıcı	adet	1	
11									Ana kaçak akım rölesi 4×40 A / 300 mA S tipi	adet	1	
12									Parafudr Tip 2 · Up 1,4 kV · In 20 kA (3F+N)	adet	1	
13									Pano gövdesi 800×1000×250 mm IP54 Form 2b	adet	1	
14									Bakır bara seti 3F+N+PE	adet	1	
15	Klemens sırası -X1 (vidalı, 4 mm²)	adet	66	
16	Etiket seti (PVC, Türkçe, vidalı)	adet	1	
B	B	
C	C	
D	D	
E	E	
F	F	
Drawn By / Çizen		CC	Customer Name / Müşteri Adı		ÖZEL — MALTEPE / İDEALTEPE		Project Number / Proje Numarası		GYM-25-001-001	Sheet: / Sayfa		12	
Checked By / Kontrol Eden		—	Project Description / Proje Açıklaması		MOBİLYA MAĞAZASI → FONKSİYONEL ANTRENMAN STÜDYOSU					Next sheet: / Sonraki		—	
Approved By / Onaylayan		—	Panel Name / Pano Adı		ADP		Revision / Revizyon		Rev H	Total sheets: / Toplam		12	
Project Date / Proje Tarihi		17 Eylül 2026		Page Description / Sayfa Açıklaması		Parts List / Malzeme Listesi		Standards / Standartlar		IEC 61439-1&2 · IEC 60617		Sheet size / Kâğıt	A3	