


LEJANT

- Mimari — mevcut duvar (korunuyor)
- Mimari — yeni alçıpan bölme
- Mimari — cephe doğraması
- Mimari — kapı ve açılım
- Mimari — spor ekipmanı (işverence temin)
- Mimari — sabit mobilya
- Mimari — mahal adı ve alan

GENEL NOTLAR

- Mimari altlık — mevcut duvar korunur.
- Kırmızı: yeni alçıpan bölme.
- Ölçüler raster paftadan (+/-%3).

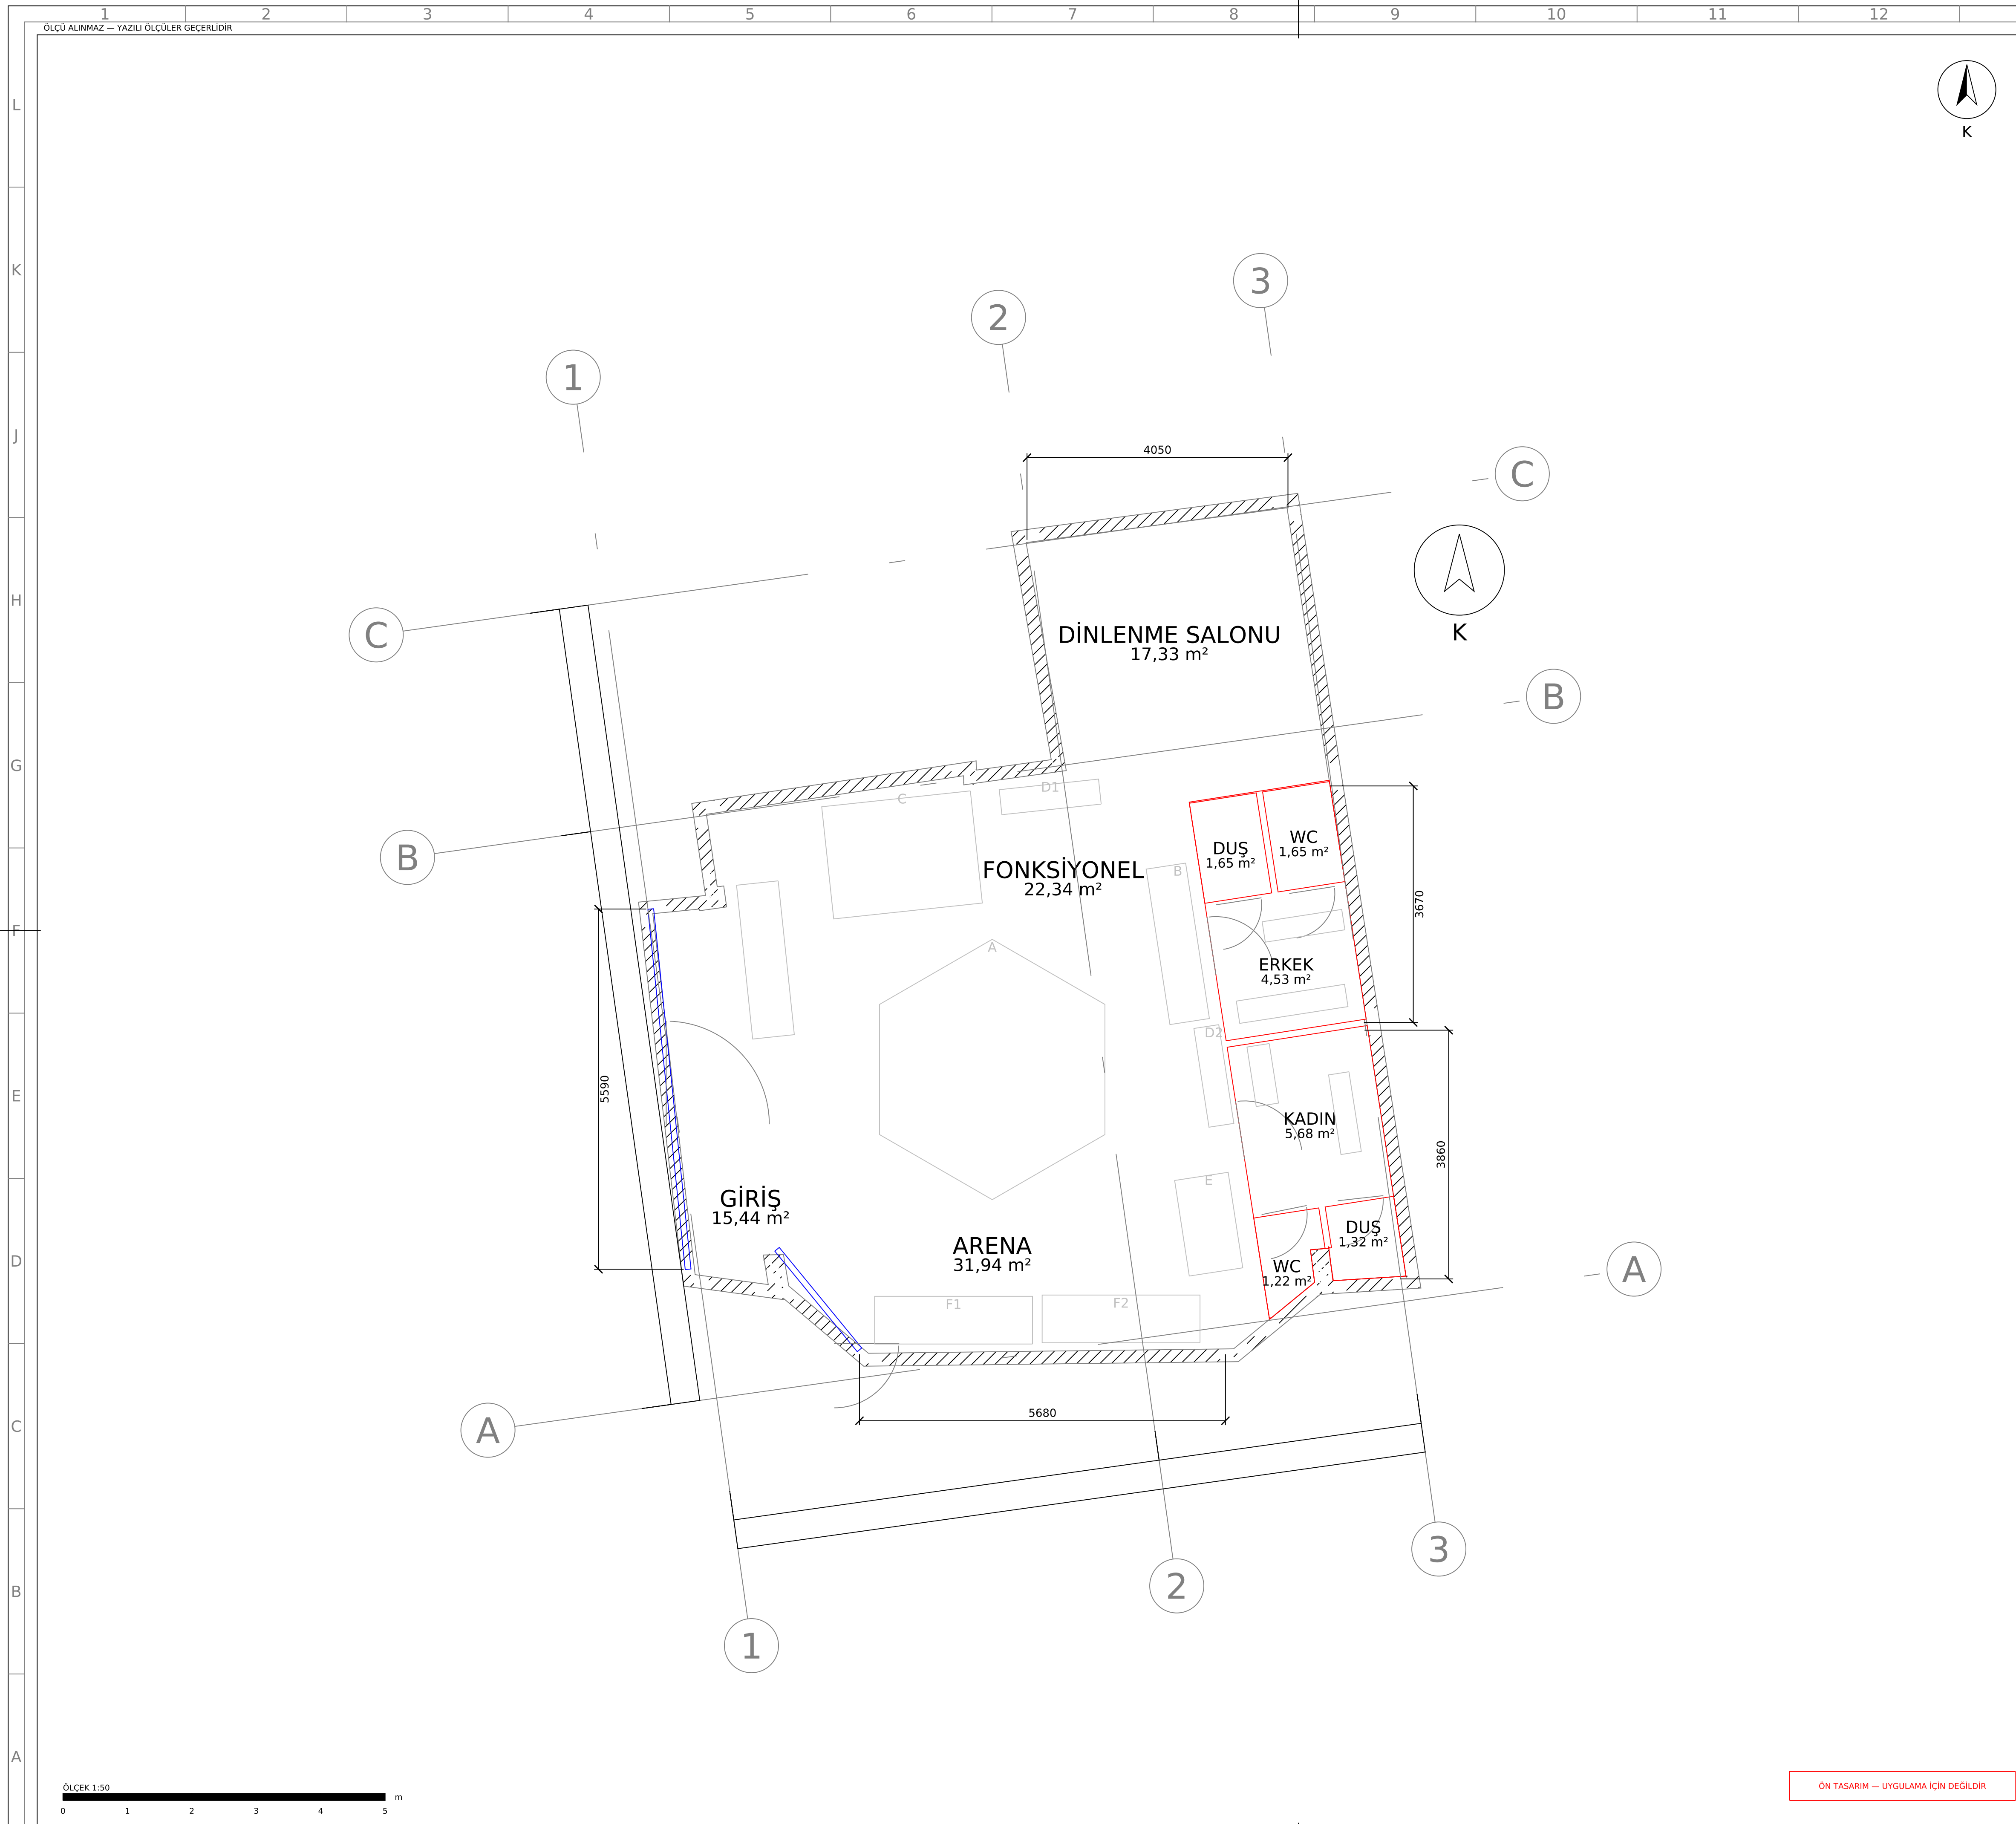

REV	TARİH	AÇIKLAMA	CZ	KT	ON
A	17.09.2026	İlk yayın — ön tasarım	CC	—	—
B	18.09.2026	Aks sistemi, zincir ölçü, ISO 5457/7200 pafta	CC	—	—
C	18.09.2026	A1 pafta, tekil DXF, ADP şeması CAD'de	CC	—	—
D	18.09.2026	ADP çok hatlı şema (faz ayrımı), B eğrisi, ana RCD	CC	—	—

İŞVEREN ÖZEL — MALTEPE / IDEALTEPE PROJE MOBİLYA MAĞAZASI → FONKSİYONEL ANTRENMAN STÜDYOSU					
YAPI / MAHAL İdealtepe Mah. · zemin kat dükkân · 103,78 m² iç alan			DİSİPLİN MİMARİ		
PAFTA ADI MİMARİ ALTLIK			Mevcut durum · ölçü ve aks sistemi		
PROJE MÜELLİFİ · ODA SİCİL NO — Oda sicil no: —					
ÇİZEN CC		KONTROL —		ONAY —	
TARİH 17 Eylül 2026		ÖLÇEK 1:50		BİRİM milimetre (mm)	
DURUM ÖN TASARIM		PAFTA NO A-01		REV H	
				SONRAKİ: A-02	

ÖLÇEK 1:50
0 1 2 3 4 5 m

ÖN TASARIM — UYGULAMA İÇİN DEĞİLDİR

LEJANT

- Mimari — mevcut duvar (korunuyor)
— Mimari — yeni alçıpan bölme
— Mimari — cephe doğraması
— Mimari — kapı ve açılım
— Mimari — spor ekipmanı (işverence temin)
— Mimari — sabit mobilya
— Mimari — mahal adı ve alan
— Mimari — mahal numarası ve kapı kodu balonu
- - - Mimari — kesit ve görüş hattı

GENEL NOTLAR

1. Mahal no, kapı kodu, duvar tipi ve
2. kesit hattı gösterilmiştir.
3. Tüm alçıpan bölmeler yapısal dösleme
4. altına (+3.20) kadar yükselir.

ÖLÇEK 1:50
0 1 2 3 4 5 m

ÖN TASARIM — UYGULAMA İÇİN DEĞİLDİR

100 mm

REV	TARİH	AÇIKLAMA	CZ	KT	ON
A	17.09.2026	İlk yayın — ön tasarım	CC	—	—
B	18.09.2026	Aks sistemi, zincir ölçü, ISO 5457/7200 pafta	CC	—	—
C	18.09.2026	A1 pafta, tekil DXF, ADP şeması CAD'de	CC	—	—
D	18.09.2026	ADP çok hatlı şema (faz ayrımı), B eğrisi, ana RCD	CC	—	—

İŞVEREN ÖZEL — MALTEPE / İDEALTEPE PROJE MOBİLYA MAĞAZASI → FONKSİYONEL ANTRENMAN STÜDYOSU		
YAPI / MAHAL İdealtepe Mah. · zemin kat dükkân · 103,78 m ² iç alan		DİSİPLİN MİMARİ
PAFTA ADI MİMARİ UYGULAMA PLANI		Bölme duvarlar · kapılar · mahal numaraları
PROJE MÜELLİFİ · ODA SİCİL NO — Oda sicil no: —		
ÇİZEN CC	KONTROL —	ONAY —
TARİH 17 Eylül 2026	ÖLÇEK 1:50	BİRİM milimetre (mm)
DURUM ÖN TASARIM	PAFTA NO A-02	REV H SONRAKİ: A-03

LEJANT

- Mimari — mevcut duvar (korunuyor)
— Mimari — yeni alçıpan bölme
— Mimari — cephe doğraması
— Mimari — kapı ve açılım
— Mimari — mahal numarası ve kapı kodu balonu
— Mimari — zemin kaplama tipi sınırı
— Mimari — zemin kaplama tipi ve kotu
— Mimari — kauçuk karo derz ızgarası

GENEL NOTLAR

1. Bitmiş zemin kotu tüm kuru hacimde
2. +/-0,00; dus ve WC -0,02.
3. Tesviye sapı kalınlıkları farklıdır
4. (Z1:3 Z2:30 Z3:42 Z5:38 mm).
5. Kauçuk karo derz 1000x1000 mm.


ÖLÇEK 1:50
0 1 2 3 4 5 m

ÖN TASARIM — UYGULAMA İÇİN DEĞİLDİR


REV	TARİH	AÇIKLAMA	CZ	KT	ON
A	17.09.2026	İlk yayın — ön tasarım	CC	—	—
B	18.09.2026	Aks sistemi, zincir ölçü, ISO 5457/7200 pafta	CC	—	—
C	18.09.2026	A1 pafta, tekil DXF, ADP şeması CAD'de	CC	—	—
D	18.09.2026	ADP çok hatlı şema (faz ayrımı), B eğrisi, ana RCD	CC	—	—

İŞVEREN ÖZEL — MALTEPE / İDEALTEPE			B		
PROJE MOBİLYA MAĞAZASI → FONKSİYONEL ANTRENMAN STÜDYOSU					
YAPI / MAHAL İdealtepe Mah. · zemin kat dükkân · 103,78 m² iç alan		DISIPLİN MİMARİ			
PAFTA ADI ZEMİN KAPLAMA PLANI		Kaplama tipleri · kot · derz yönü			
PROJE MÜELLİFİ · ODA SİCİL NO — Oda sicil no: —					
ÇİZEN CC		KONTROL —		ONAY —	
TARİH 17 Eylül 2026		ÖLÇEK 1:50		BİRİM milimetre (mm)	
DURUM ÖN TASARIM		PAFTA NO A-03		REV H	
				SONRAKİ: A-04	

ÖLÇÜ ALINMAZ — YAZILI ÖLÇÜLER GEÇERLİDİR

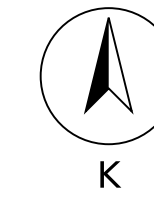

ANAHTAR PLAN

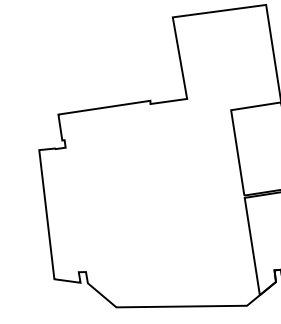

LEJANT

- Mimari — mevcut duvar (korunuyor)
- Mimari — yeni alçıpan bölme
- Mimari — cephe doğraması
- Mimari — kapı ve açılım
- Mimari — sabit mobilya
- Mimari — asma tavan tipi sınırı
- Mimari — asma tavan tipi ve kotu
- Mimari — revizyon kapağı 300x300
- Mekanik — taze hava kanalı
- Mekanik — egzoz kanalı
- Mekanik — ıslak hacim egzoz kanalı
- Mekanik — menfez ve valf
- Mekanik — menfez bransmanı
- Mekanik — fan ve panjur
- Mekanik — etiket ve not
- Elektrik — lineer LED armatür
- Elektrik — IP44 downlight
- Elektrik — acil aydınlatma / yönlendirme
- Elektrik — anahtar ve sensör
- Elektrik — aydınlatma linyesi (ortogonal)
- Elektrik — anahtar kumanda sortisi
- Elektrik — ana dağıtım panosu
- Elektrik — etiket ve not

GENEL NOTLAR

- T1 acık tavan +3.20 - T2 +2.75
- T4 +2.60 - T3 +2.40.
- Tesisat askisi alçıpan karkasına
- asılmaz; ayrı askılanır.
- Her ıslak hacimde 300x300 revizyon.


REV	TARİH	AÇIKLAMA	CZ	KT	ON
A	17.09.2026	İlk yayın — ön tasarım	CC	—	—
B	18.09.2026	Aks sistemi, zincir ölçü, ISO 5457/7200 pafta	CC	—	—
C	18.09.2026	A1 pafta, tekil DXF, ADP şeması CAD'de	CC	—	—
D	18.09.2026	ADP çok hatlı şema (faz ayrımı), B eğrisi, ana RCD	CC	—	—

İŞVEREN ÖZEL — MALTEPE / IDEALTEPE			PROJE MOBİLYA MAĞAZASI → FONKSİYONEL ANTRENMAN STÜDYOSU		
YAPI / MAHAL İdealtepe Mah. - zemin kat dükkân - 103,78 m² iç alan			DİSİPLİN MİMARİ		
PAFTA ADI TAVAN PLANI (RCP)			Asma tavan tipleri - kot - MEP koordinasyonu		
PROJE MÜELLİFİ - ODA SİCİL NO — Oda sicil no: —					
ÇİZEN CC		KONTROL —	ONAY —		A
TARİH 17 Eylül 2026		ÖLÇEK 1:50	BİRİM milimetre (mm)		
DURUM ÖN TASARIM		PAFTA NO A-04	REV H		SONRAKİ: A-05

ÖLÇEK 1:50
0 1 2 3 4 5 m

ÖN TASARIM — UYGULAMA İÇİN DEĞİLDİR

100 mm

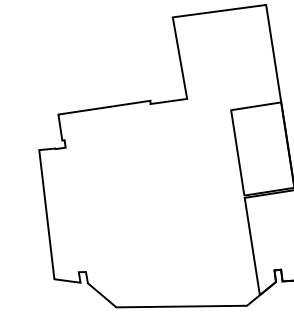


LEJANT

- Mimari — mevcut duvar (korunuyor)
- Mimari — yeni alçıpan bölme
- Mimari — cephe doğraması
- Mimari — kapı ve açılım
- Mimari — sabit mobilya
- Mimari — mahal adı ve alan
- Mimari — kaçış yolu ve çıkış
- Mimari — söndürücü, dolap, ihbar

GENEL NOTLAR

- İki bağımsız çıkış: C1 1,60 m, C2 1,00 m.
- En uzun kaçış yolu 13,4 m.
- Kaçış kapıları kaçış yönünde açılır.
- panik donanımlı, kilitsiz.

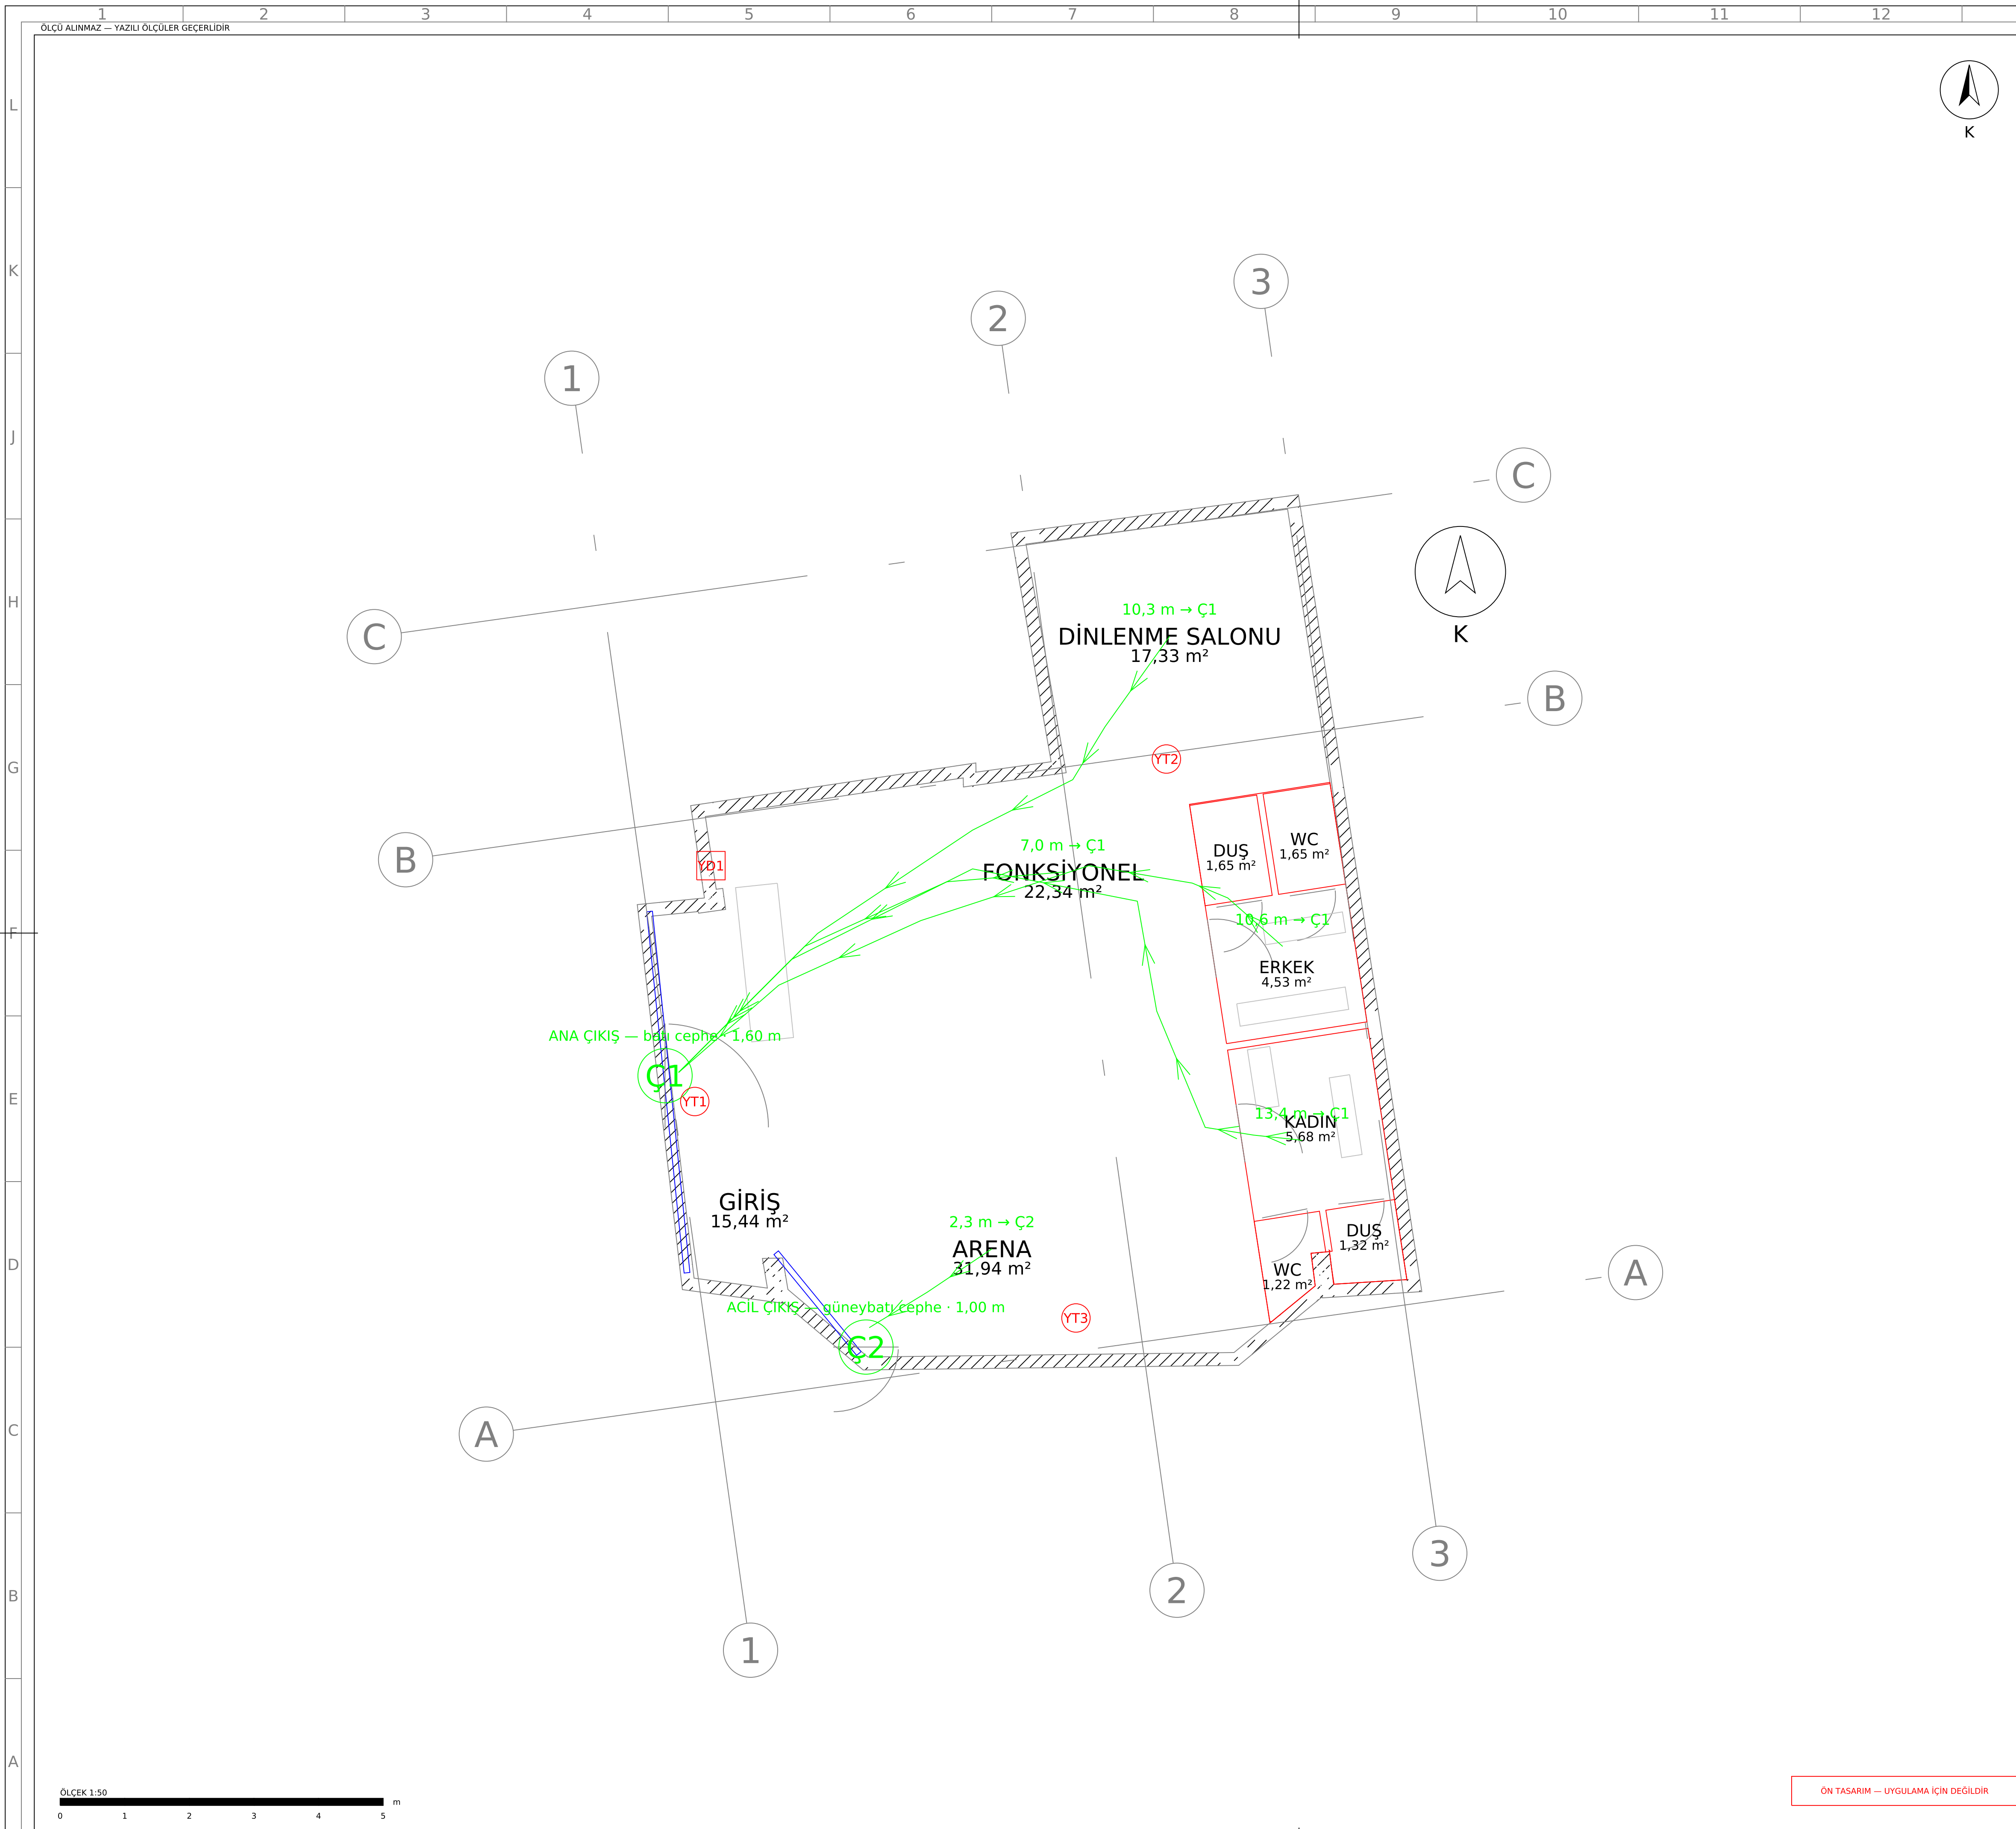

REV	TARİH	AÇIKLAMA	ÇZ	KT	ON
A	17.09.2026	İlk yayın — ön tasarım	CC	—	—
B	18.09.2026	Aks sistemi, zincir ölçü, ISO 5457/7200 pafta	CC	—	—
C	18.09.2026	A1 pafta, tekil DXF, ADP şeması CAD'de	CC	—	—
D	18.09.2026	ADP çok hatlı şema (faz ayrımı), B eğrisi, ana RCD	CC	—	—

İŞVEREN ÖZEL — MALTEPE / İDEALTEPE			B		
PROJE MOBİLYA MAĞAZASI → FONKSİYONEL ANTRENMAN STÜDYOSU					
YAPI / MAHAL İdealtepe Mah. · zemin kat dükkân · 103,78 m² iç alan		DİSİPLİN MİMARİ			
PAFTA ADI YANGIN VE TAHLİYE PLANI		Kaçış yolları · çıkışlar · söndürücü			
PROJE MÜELLİFİ · ODA SİCİL NO — Oda sicil no: —					
ÇİZEN CC		KONTROL —		ONAY —	
TARİH 17 Eylül 2026		ÖLÇEK 1:50		BİRİM milimetre (mm)	
DURUM ÖN TASARIM		PAFTA NO A-05		REV H	
				SONRAKİ: M-01	

LEJANT

- Mimari — mevcut duvar (korunuyor)
— Mimari — yeni alçıpan bölme
— Mimari — cephe doğraması
— Mimari — kapı ve açılım
— Mimari — spor ekipmanı (işverence temini)
— Mimari — sabit mobilya
— Mimari — mahal adı ve alan
— Mekanik — taze hava kanalı
— Mekanik — egzoz kanalı
— Mekanik — ıslak hacim egzoz kanalı
— Mekanik — menfez ve valf
— Mekanik — menfez bransmanı
— Mekanik — fan ve panjur
— Mekanik — etiket ve not

GENEL NOTLAR


1. Kanallar galvaniz sac, TS EN 1507 sınıf B.
2. Besleme ve egzoz hattı 19 mm izoleli.
3. Her bransman bası debi ayar damperli.
4. Devreye almada balanslama ve ölçüm raporu.

ÖLÇEK 1:50
0 1 2 3 4 5 m

ÖN TASARIM — UYGULAMA İÇİN DEĞİLDİR

100 mm

A1

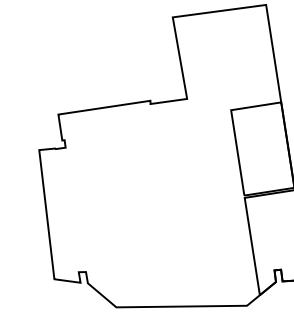


LEJANT

- Mimari — mevcut duvar (korunuyor)
- Mimari — yeni alçıpan bölme
- Mimari — cephe doğraması
- Mimari — kapı ve açılım
- Mimari — spor ekipmanı (işverence temin)
- Mimari — sabit mobilya
- Mimari — mahal adı ve alan
- Mekanik — klima iç ünite
- Mekanik — klima dış ünite platformu
- Mekanik — soğutucu akışkan bakır hattı
- Mekanik — klima drenaj hattı

GENEL NOTLAR

- İç ünite montaj kotu 2,40 m (altı kot).
- Bakır hat izoleli, dış ünite konsolu
- titresim takozlu.
- Drenaj %1 eğimli.

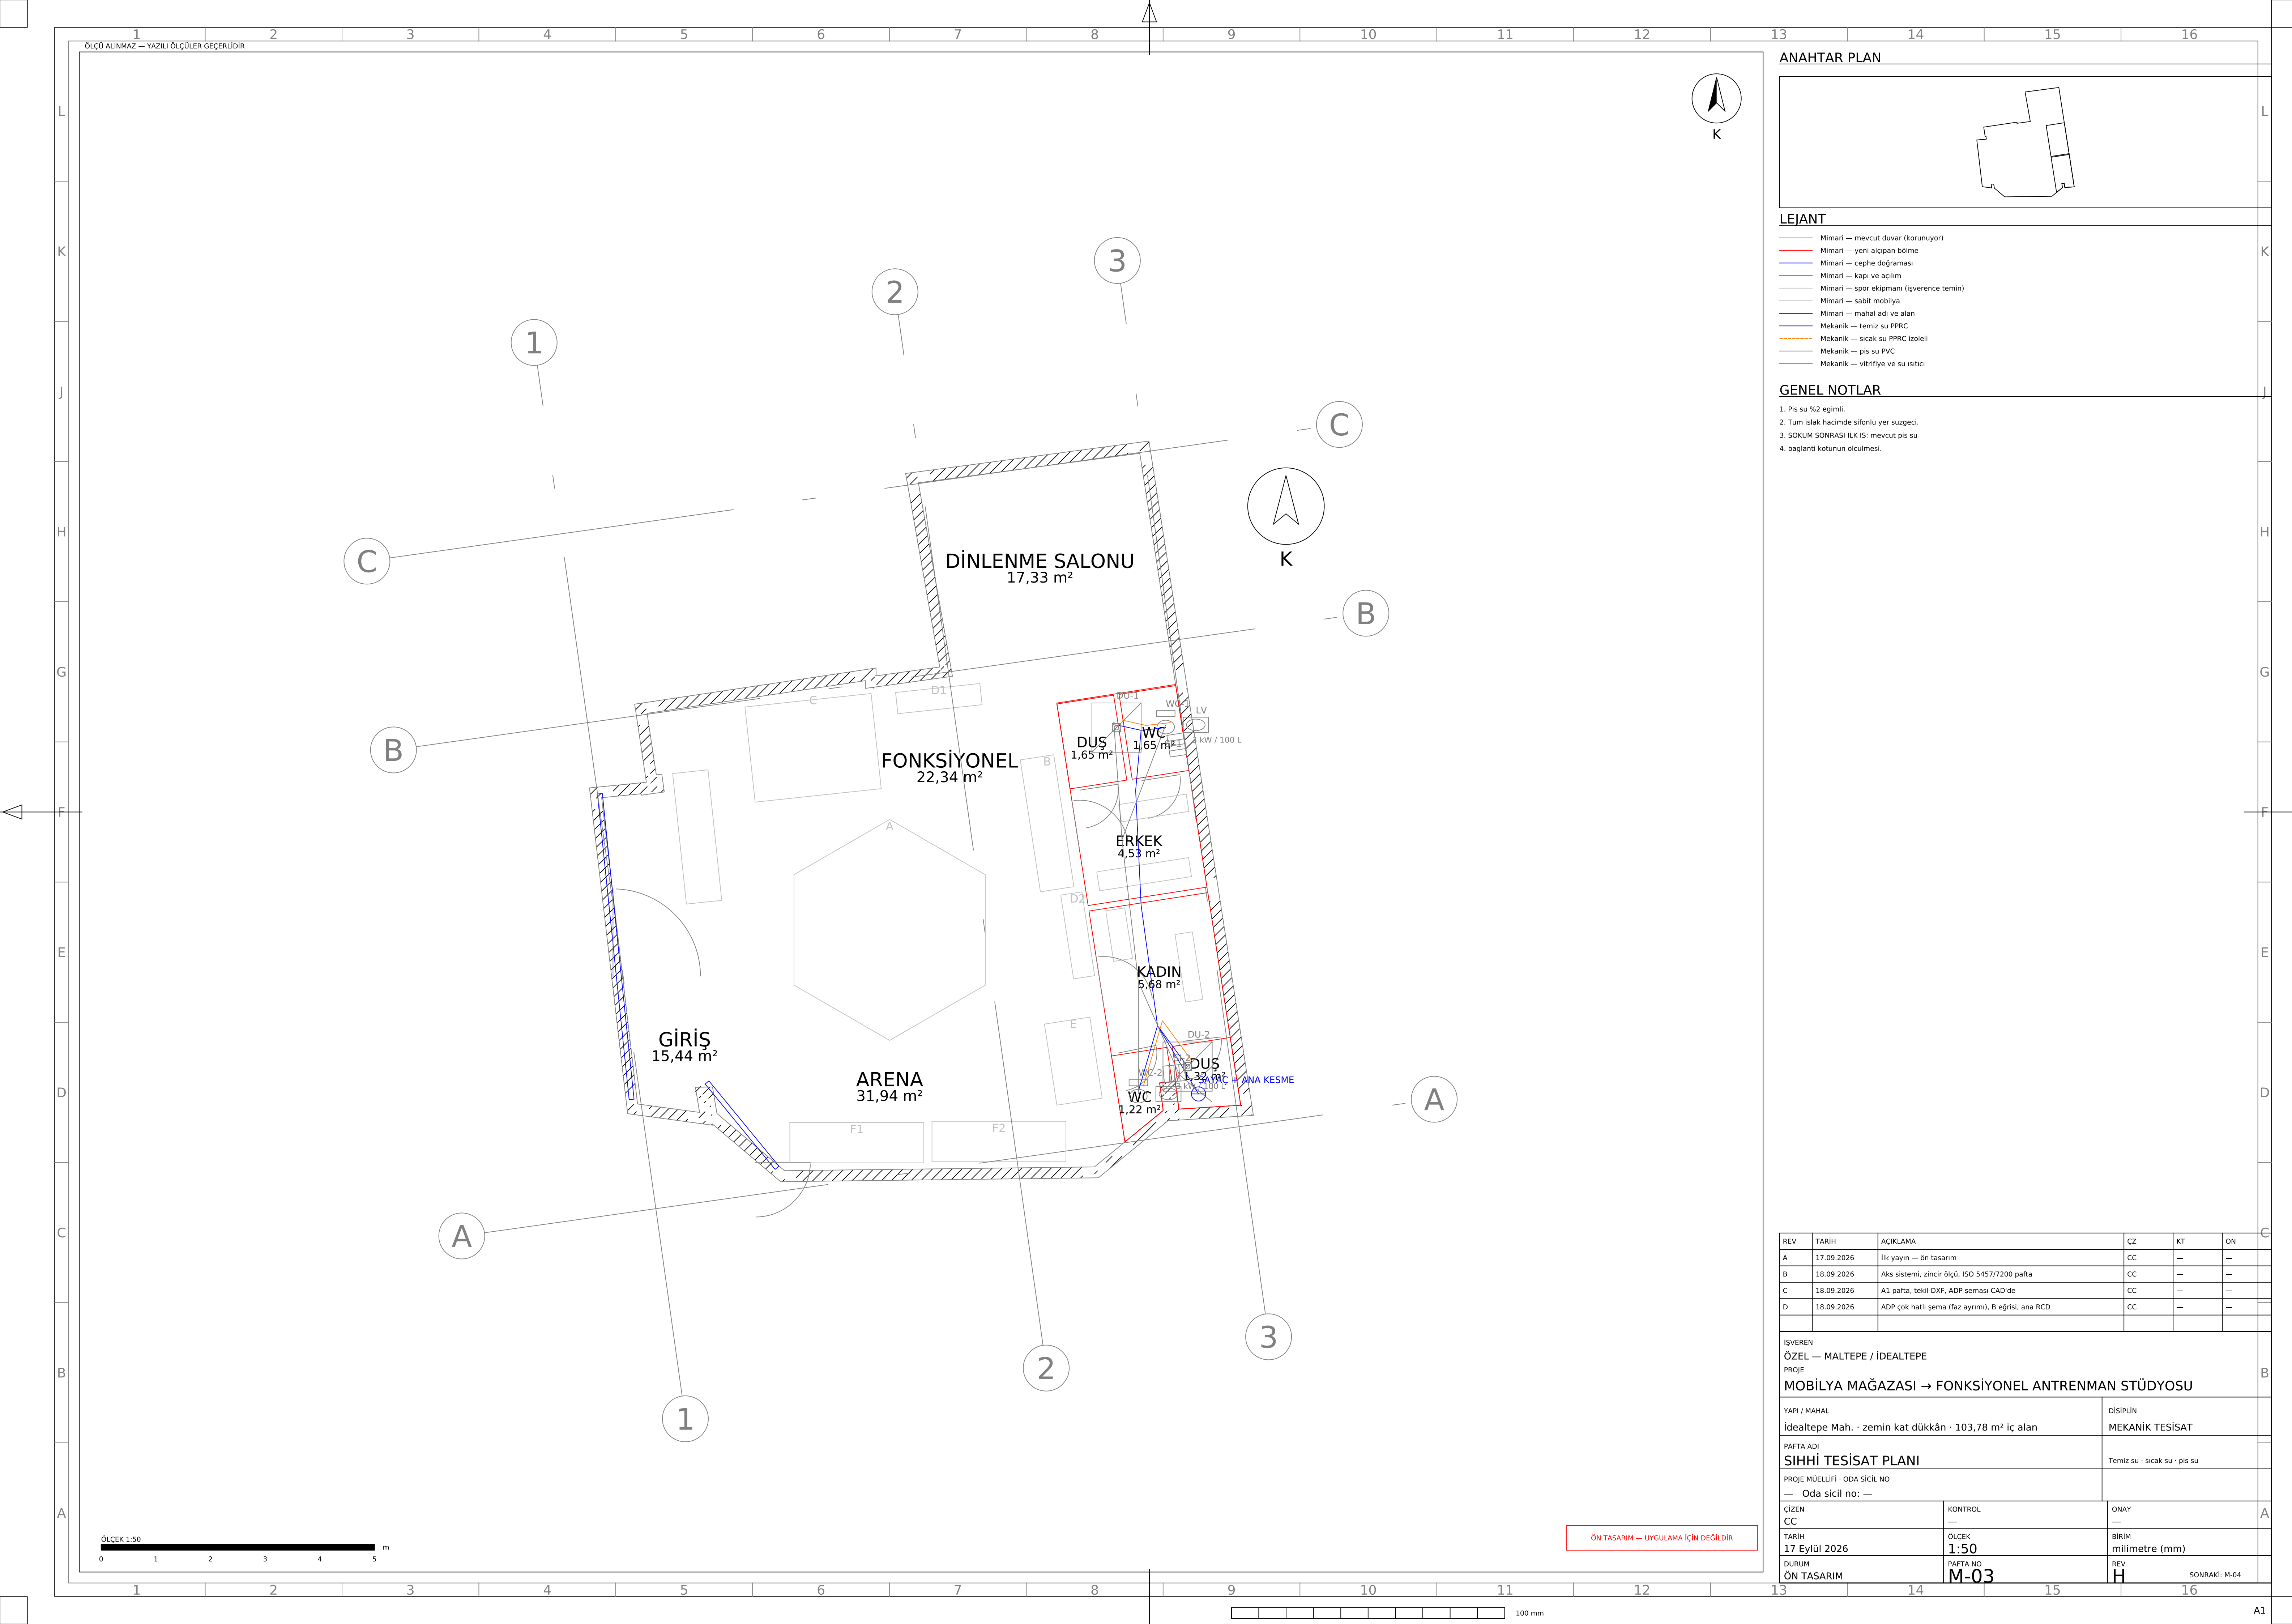

LEJANT

- Mimari — mevcut duvar (korunuyor)
- Mimari — yeni alçıpan bölme
- Mimari — cephe doğraması
- Mimari — kapı ve açılım
- Mimari — spor ekipmanı (işverence temini)
- Mimari — sabit mobilya
- Mimari — mahal adı ve alan
- Mekanik — taze hava kanalı
- Mekanik — egzoz kanalı
- Mekanik — ıslak hacim egzoz kanalı
- Mekanik — menfez ve valf
- Mekanik — menfez bransmanı
- Mekanik — fan ve panjur
- Mekanik — klima iç ünite
- Mekanik — klima dış ünite platformu
- Mekanik — soğutucu akışkan bakır hattı
- Mekanik — klima drenaj hattı
- Mekanik — temiz su PPRC
- Mekanik — sıcak su PPRC izoleli
- Mekanik — pis su PVC
- Mekanik — vitrifiye ve su ısıtıcı
- Mekanik — etiket ve not

GENEL NOTLAR


- Mekanik disiplin genel yerleşimi.
- Ayrıntı için M-01, M-02, M-03 paftaları.

ÖLÇEK 1:50
0 1 2 3 4 5 m

ÖN TASARIM — UYGULAMA İÇİN DEĞİLDİR

REV	TARİH	AÇIKLAMA	CZ	KT	ON
A	17.09.2026	İlk yayın — ön tasarım	CC	—	—
B	18.09.2026	Aks sistemi, zincir ölçü, ISO 5457/7200 pafta	CC	—	—
C	18.09.2026	A1 pafta, tekil DXF, ADP şeması CAD'de	CC	—	—
D	18.09.2026	ADP çok hatlı şema (faz ayrımı), B eğrisi, ana RCD	CC	—	—

İŞVEREN ÖZEL — MALTEPE / İDEALTEPE		B	
PROJE MOBİLYA MAĞAZASI → FONKSİYONEL ANTRENMAN STÜDYOSU			
YAPI / MAHAL İdealtepe Mah. · zemin kat dükkân · 103,78 m ² iç alan		DISIPLİN MEKANİK TESİSAT	
PAFTA ADI MEKANİK GENEL YERLEŞİM		Mekanik disiplin genel yerleşimi	
PROJE MÜELLİFİ - ODA SİCİL NO — Oda sicil no: —			
ÇİZEN CC	KONTROL —	ONAY —	A
TARİH 17 Eylül 2026	ÖLÇEK 1:50	BİRİM milimetre (mm)	
DURUM ÖN TASARIM	PAFTA NO M-04	REV H	SONRAKİ: E-01

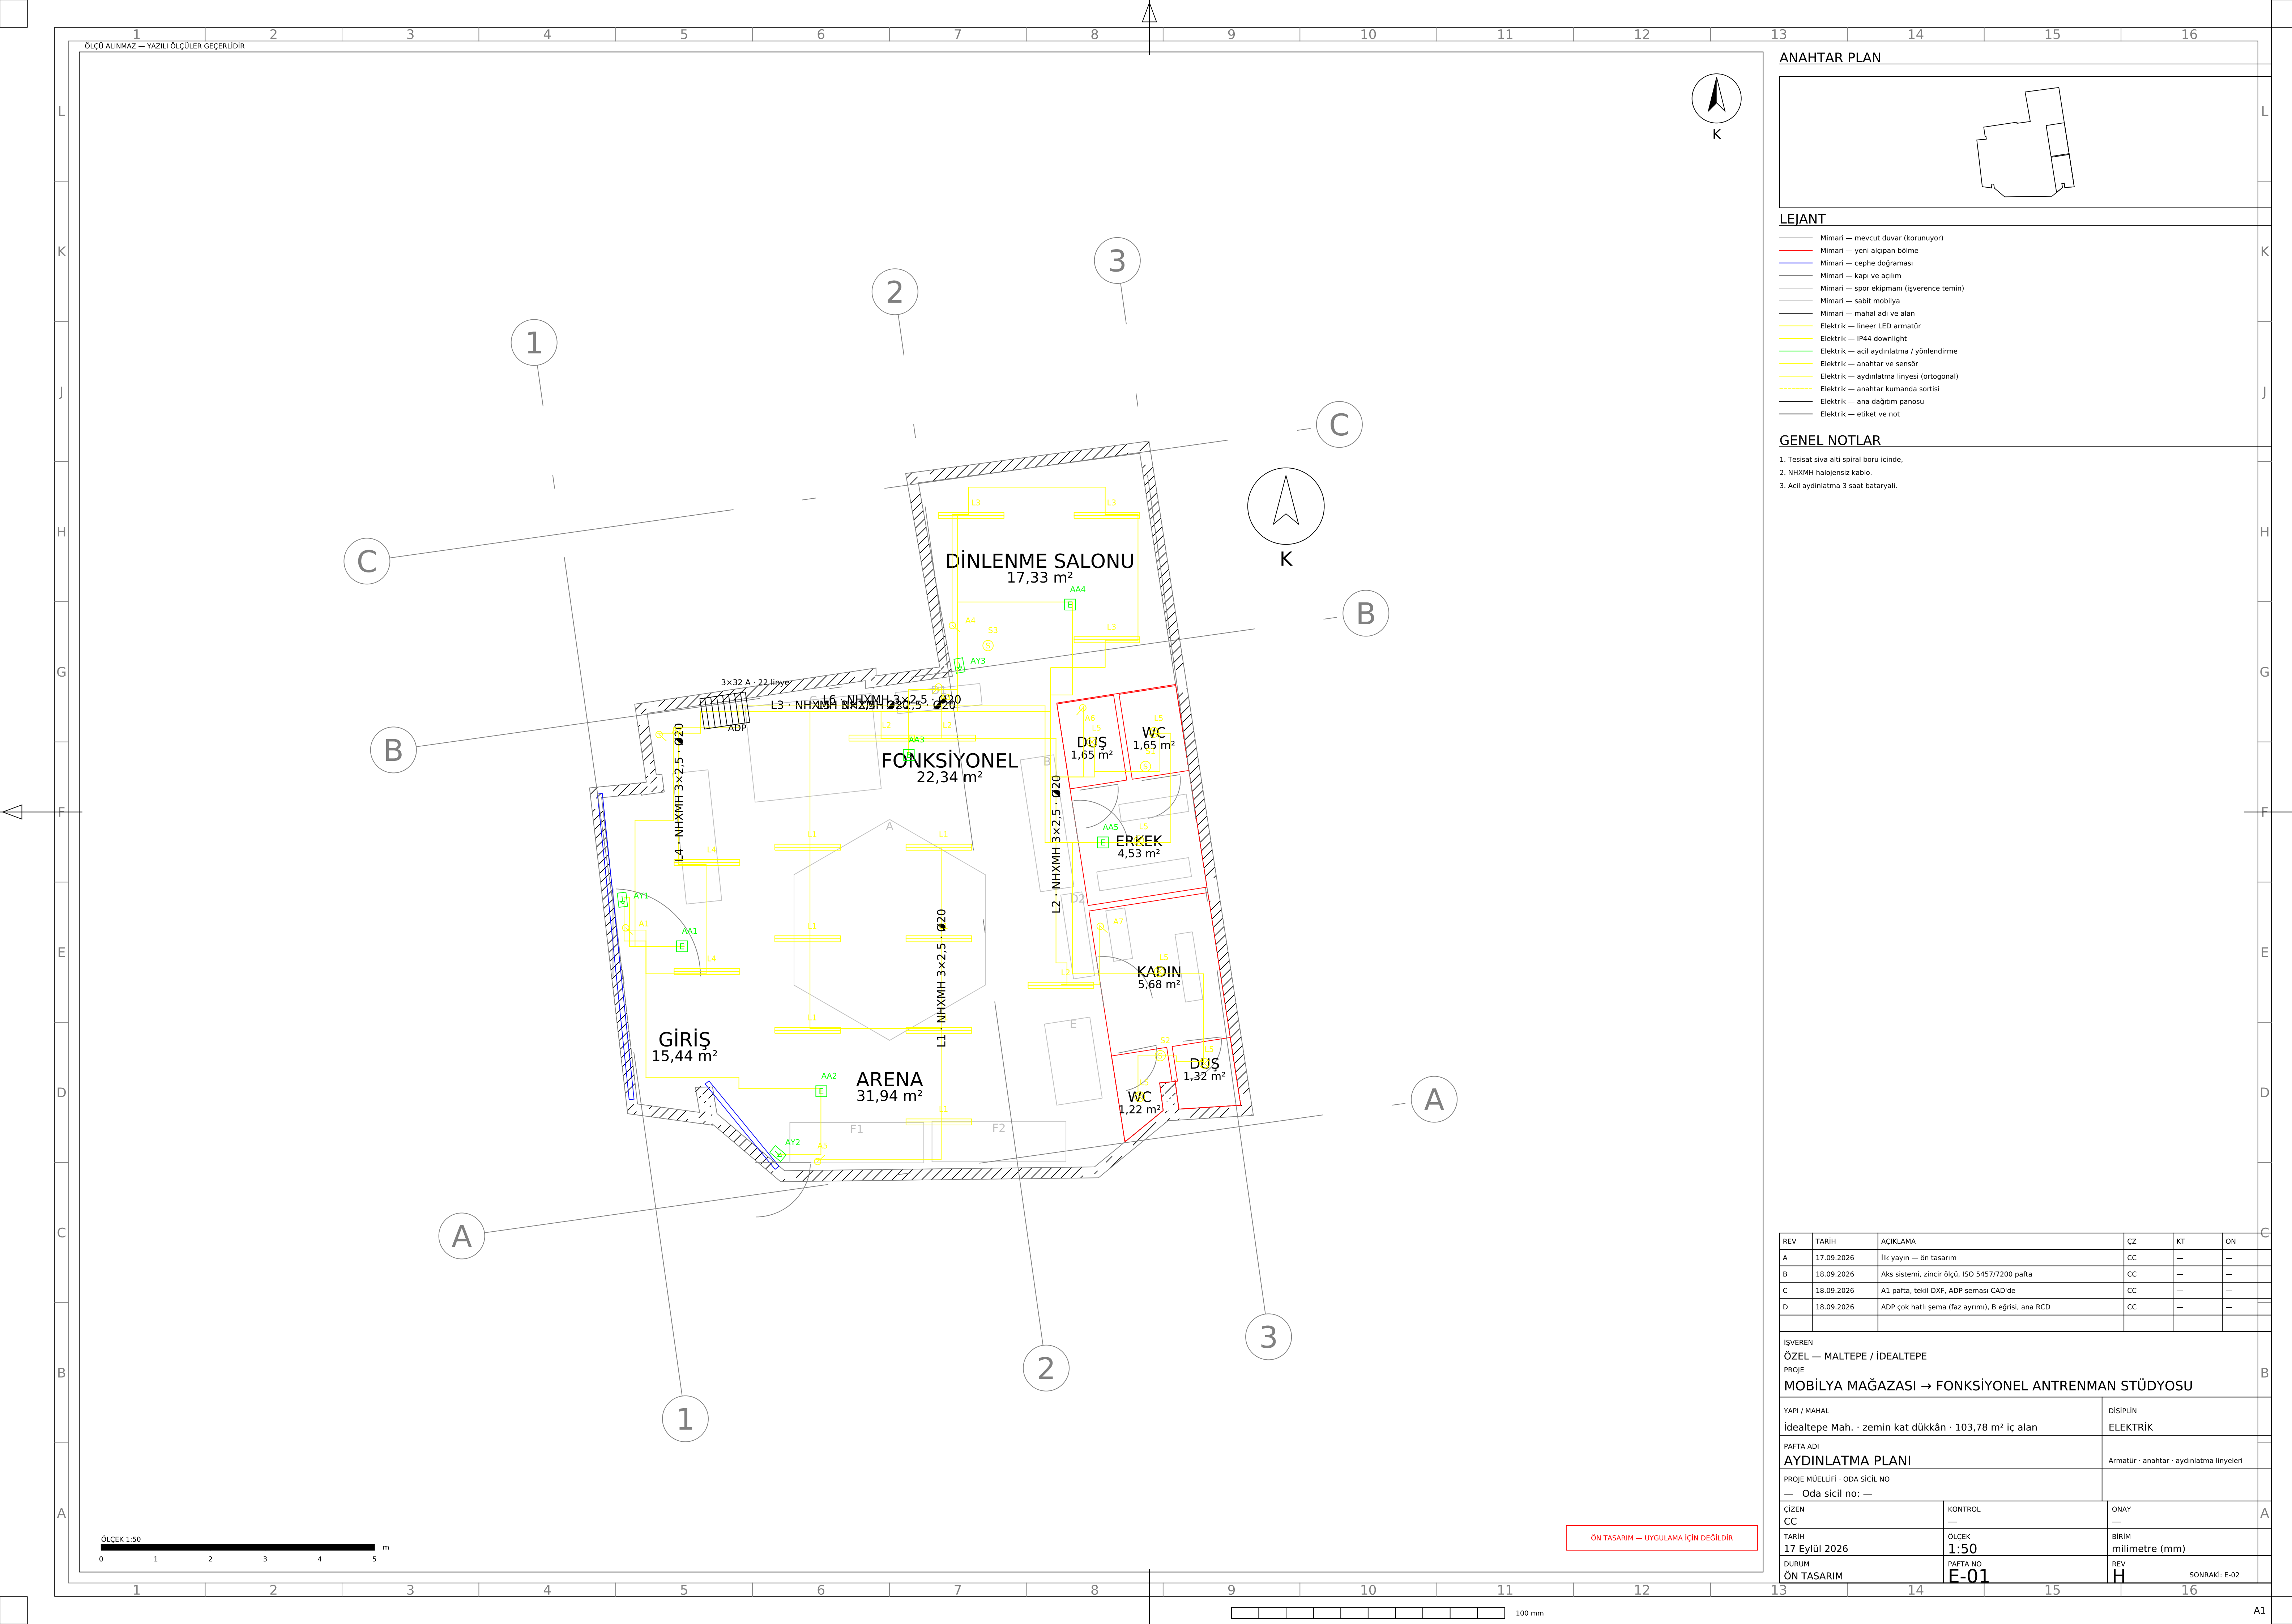

LEJANT

- Mimari — mevcut duvar (korunuyor)
- Mimari — yeni alçıpan bölme
- Mimari — cephe doğraması
- Mimari — kapı ve açılım
- Mimari — spor ekipmanı (işverence temin)
- Mimari — sabit mobilya
- Mimari — mahal adı ve alan
- Elektrik — priz
- Elektrik — klima/sıtıcı/fan beslemesi
- Elektrik — priz ve kuvvet linyesi
- Elektrik — ana dağıtım panosu
- Elektrik — etiket ve not

GENEL NOTLAR

- Islak hacim linyeleri ayrı 30 mA
- kacak akım rolesinden beslenir.
- Kardiyo ekipmanı ayrı linyede (P4).

ÖLÇEK 1:50
0 1 2 3 4 5 m

ÖN TASARIM — UYGULAMA İÇİN DEĞİLDİR

REV	TARİH	AÇIKLAMA	CZ	KT	ON
A	17.09.2026	İlk yayın — ön tasarım	CC	—	—
B	18.09.2026	Aks sistemi, zincir ölçü, ISO 5457/7200 pafta	CC	—	—
C	18.09.2026	A1 pafta, tekil DXF, ADP şeması CAD'de	CC	—	—
D	18.09.2026	ADP çok hatlı şema (faz ayrımı), B eğrisi, ana RCD	CC	—	—

İŞVEREN ÖZEL — MALTEPE / İDEALTEPE PROJE MOBİLYA MAĞAZASI → FONKSİYONEL ANTRENMAN STÜDYOSU			B
YAPI / MAHAL İdealtepe Mah. · zemin kat dükkân · 103,78 m ² iç alan		DISIPLİN ELEKTRİK	
PAFTA ADI PRİZ VE KUVVET PLANI		Priz · kuvvet linyeleri · cihaz beslemeleri	
PROJE MÜELLİFİ · ODA SİCİL NO — Oda sicil no; —			
ÇİZEN CC	KONTROL —	ONAY —	A
TARİH 17 Eylül 2026	ÖLÇEK 1:50	BİRİM milimetre (mm)	
DURUM ÖN TASARIM	PAFTA NO E-02	REV H	
		SONRAKİ: E-03	

LEJANT

- Mimari — mevcut duvar (korunuyor)
- Mimari — yeni alçıpan bölme
- Mimari — cephe doğraması
- Mimari — kapı ve açılım
- Mimari — spor ekipmanı (işverence temin)
- Mimari — sabit mobilya
- Mimari — mahal adı ve alan
- Elektrik — IP kamera
- Elektrik — tavan hoparlörü
- Elektrik — veri prizi ve rack
- Elektrik — dedektör, buton, siren
- Elektrik — yangın algılama çevrimi
- Elektrik — zayıf akım kablo kanalı
- Elektrik — ana dağıtım panosu
- Elektrik — etiket ve not

GENEL NOTLAR

- SOYUNMA VE WC İÇİNE KAMERA KONULMAZ.
- Yangın algılama panosu kesintisiz beslenir.
- Topraklama direnci ≤ 10 ohm.

ÖLÇEK 1:50
0 1 2 3 4 5 m

ÖN TASARIM — UYGULAMA İÇİN DEĞİLDİR

LEJANT

- Mimari — mevcut duvar (korunuyor)
- Mimari — yeni alçıpan bölme
- Mimari — cephe doğraması
- Mimari — kapı ve açılım
- Mimari — spor ekipmanı (işverence temini)
- Mimari — sabit mobilya
- Mimari — mahal adı ve alan
- Elektrik — lineer LED armatür
- Elektrik — IP44 downlight
- Elektrik — acil aydınlatma / yönlendirme
- Elektrik — anahtar ve sensör
- Elektrik — priz
- Elektrik — klima/sıtıcı/fan beslemesi
- Elektrik — IP kamera
- Elektrik — tavan hoparlörü
- Elektrik — veri prizi ve rack
- Elektrik — dedektör, buton, siren
- Elektrik — yangın algılama çevrimi
- Elektrik — aydınlatma lineyesi (ortogonal)
- Elektrik — anahtar kumanda sortisi
- Elektrik — priz ve kuvvet lineyesi
- Elektrik — zayıf akım kablo kanalı
- Elektrik — ana dağıtım panosu
- Elektrik — etiket ve not

GENEL NOTLAR

- Elektrik disiplin genel yerleşimi.
- Ayrintı için E-01, E-02, E-03 paftaları.

ÖLÇEK 1:50
0 1 2 3 4 5 m

ÖN TASARIM — UYGULAMA İÇİN DEĞİLDİR

REV	TARİH	AÇIKLAMA	CZ	KT	ON
A	17.09.2026	İlk yayın — ön tasarım	CC	—	—
B	18.09.2026	Aks sistemi, zincir ölçü, ISO 5457/7200 pafta	CC	—	—
C	18.09.2026	A1 pafta, tekil DXF, ADP şeması CAD'de	CC	—	—
D	18.09.2026	ADP çok hatlı şema (faz ayrımı), B eğrisi, ana RCD	CC	—	—

İŞVEREN	ÖZEL — MALTEPE / IDEALTEPE
PROJE	MOBİLYA MAĞAZASI → FONKSİYONEL ANTRENMAN STÜDYOSU
YAPI / MAHAL	İdealtepe Mah. · zemin kat dükkân · 103,78 m ² iç alan
PAFTA ADI	ELEKTRİK GENEL YERLEŞİM
PROJE MÜELLİFİ · ODA SİCİL NO	— Oda sicil no: —
ÇİZEN	CC
TARİH	17 Eylül 2026
DURUM	ÖN TASARIM
KONTROL	—
ÖLÇEK	1:50
PAFTA NO	E-04
ONAY	—
BİRİM	milimetre (mm)
REV	H
SONRAKİ:	E-05

